















INSIDE: MDF HMR E1 V313 DKP # PP 022 WM | American Walnut  
 OUTSIDE: MDF HMR E1 V313 DKP # 836 NCT | Anti-Fingerprint  
 FRONTAGE: MDF HMR E1 V313 DKP # 836 NCT | Anti-Fingerprint  
 HANDLE: Aluminum DKP #5230 | Ivory  
 HANDLE: Aluminum DKP #5230 | Dark Choco

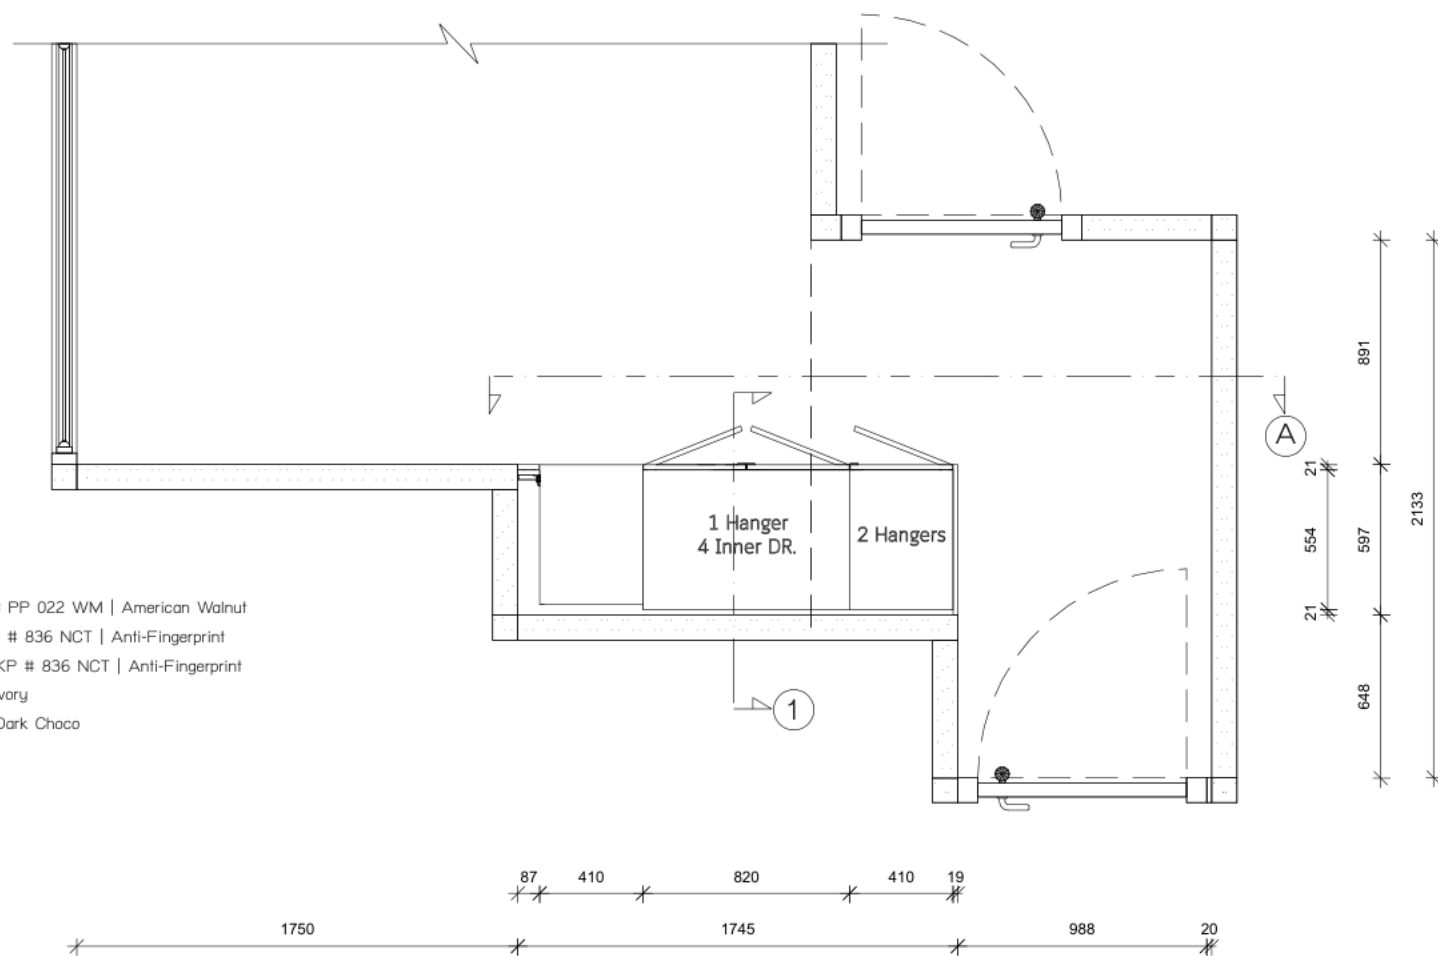


**Dkbb**

157 Praditmanutham Road  
 Bangkapi Bangkok 10240  
 TEL:0-2515-1162 FAX:0-2515-1161  
 WWW.decorchoice.co.th

|                 |                             |                  |
|-----------------|-----------------------------|------------------|
| Client : Ari789 | Design : WIC1-4C            | View : Plan      |
| Address :       | Series : Elegance           | Scale : 1:30     |
| Province :      | Drawn by : บริษัท สุนทรจามร | Date : 19/9/2569 |
| Phone :         | Email :                     | Page : 01        |

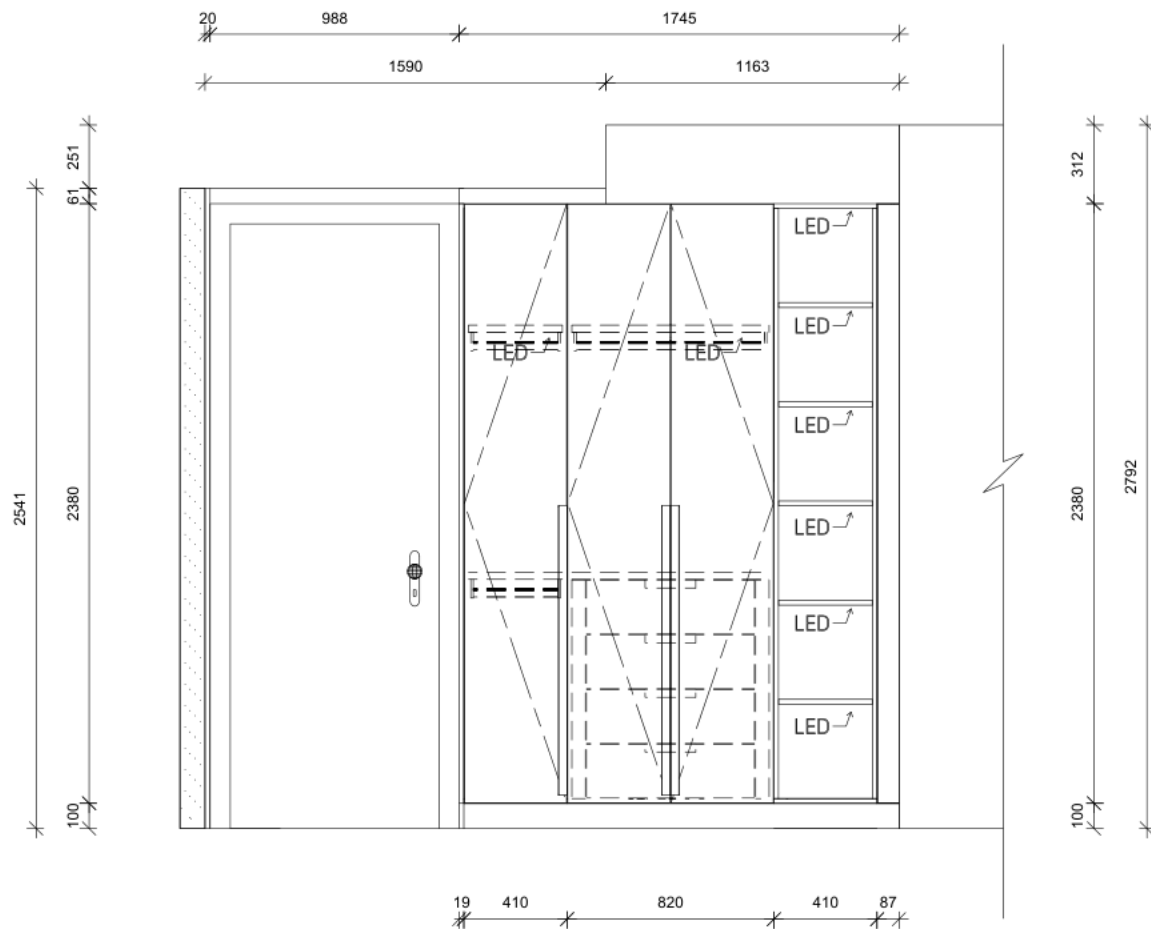

ELEVATION A

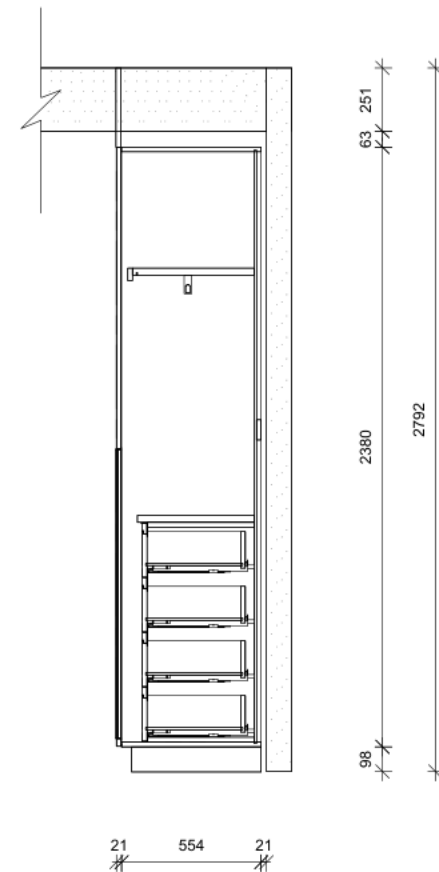

SECTION 1

**Dkbb**

157 Praditmanutham Road  
Bangkapi Bangkok 10240  
TEL:0-2515-1162 FAX:0-2515-1161  
WWW.decorchoice.co.th

|                 |                             |                                |
|-----------------|-----------------------------|--------------------------------|
| Client : Ari789 | Design : WIC1-4C            | View : Elevation A , Section 1 |
| Address :       | Series : Elegance           | Scale : 1:30                   |
| Province :      | Drawn by : บริษัท สุนทรจามร | Date : 19/9/2569               |
| Phone :         | Email :                     | Page : 02                      |



ใบสรุปเฟอร์นิเจอร์ บริษัท อารี789 ดีเวลลอปเม้นท์ จำกัด  
เลขที่ 10/1 ซอยพหลโยธิน 5 ถนนพหลโยธิน แขวงพญาไท เขตพญาไท  
กรุงเทพมหานคร 10400 โทร : 044-110218  
เลขประจำตัวผู้เสียภาษีอากร 0105565012642 (สำนักงานใหญ่)

2 ตุลาคม 2569

Q.26/1005

4C Floor 4 : Walk-in closet (Bedroom 1) รุ่น ELEGANCE

|   |                                                       |            |
|---|-------------------------------------------------------|------------|
| 1 | ตู้เสื้อผ้าบานเปิดตัว I ขนาด 0.596 X 1.745 X 2.792 ม. | 118,587.00 |
|   | รวม                                                   | 118,587.00 |
|   | ส่วนลด 15%                                            | -17,788.00 |
|   | ยอดรวม หลังหักส่วนลด                                  | 100,799.00 |
| 2 | ไฟ LED ในตู้เสื้อผ้าบานเปิดตัว I                      | 5,490.00   |
|   | รวมเงิน Ex. Vat                                       | 106,289.00 |
|   | VAT 7%                                                | 7,440.23   |
|   | ยอดสุทธิ                                              | 113,729.23 |

- หมายเหตุ - ก่อนเซ็นสั่งซื้อสินค้า กรุณาตรวจสอบแบบและรายละเอียดต่างๆ ให้ครบถ้วน  
เนื่องจากการสั่งผลิตเฉพาะงาน
- ไฟแสงสว่าง, สีของไฟ LED, ตำแหน่งปลั๊กใช้งาน, กุญแจล็อคต่างๆ ไม่สามารถเพิ่มภายหลังได้
  - กรุณาตรวจสอบก่อนว่ามีครบตามต้องการหรือไม่
  - หลังจากสั่งซื้อสินค้าแล้ว ทางบริษัทฯ ขอสงวนสิทธิ์ในการแก้ไขใดๆทั้งสิ้น

บริษัท เดคคอร์ส ชอยส์ จำกัด

157 ซ.โยธินพัฒนา ถ.ประดิษฐ์มนูธรรม แขวงคลองจั่น เขตบางกะปิ กรุงเทพฯ 10240

Tel : 0 2515 1162 Fax : 0 2515 1161 Call Center : 08-1954-5550

E-mail : decorchoice@gmail.com www.decorchoice.co.th














INSIDE: MDF HMR E1 V313 DKP # PP 022 WM | American Walnut  
OUTSIDE: MDF HMR E1 V313 DKP # 836 NCT | Anti-Fingerprint  
FRONTAGE: MDF HMR E1 V313 DKP # 836 NCT | Anti-Fingerprint  
HANDLE: Aluminum DKP #5230 | Ivory  
HANDLE: Aluminum DKP #5230 | Dark Choco  
TOP: Quartz Vadara G1 #V743 | Ostara Dawn  
FRONTAGE: Aluminum DKP #5158 (มีมือจับในตัว) | Dark Choco ,  
กรุกระจกใส TYK | Euro Bronze 5 mm. (Tempered)  
MIRROR: Aluminum DKP #5158 (มีมือจับในตัว) | Ivory ,  
กรุกระจกเงา TYK 5 mm.

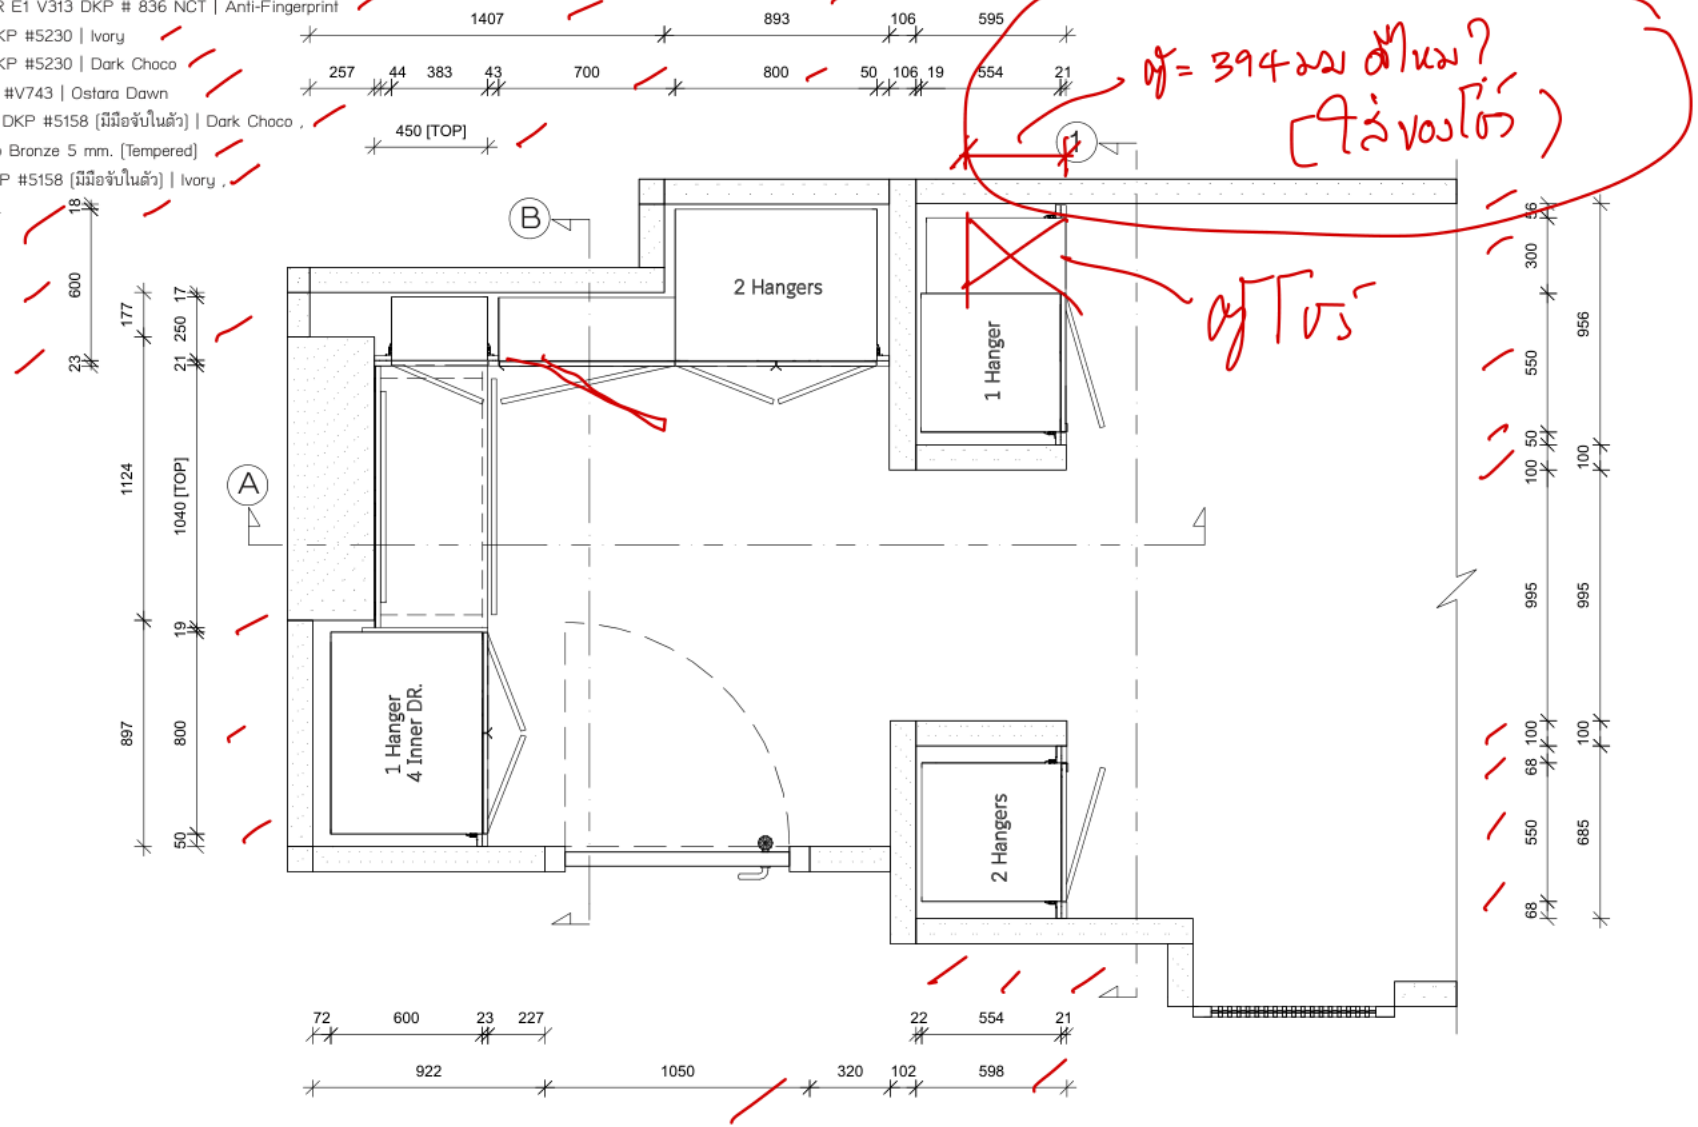

|   |                 |                             |                  |
|---|-----------------|-----------------------------|------------------|
|  <div>157 Praditmanutham Road<br/>Bangkapi Bangkok 10240<br/>TEL:0-2515-1162 FAX:0-2515-1161<br/>WWW.decorchoice.co.th</div> | Client : Ari789 | Design : WICMB-4C           | View : Plan      |
|   | Address :       | Series : Elegance           | Scale : 1:30     |
|   | Province :      | Drawn by : บริษัท สุนทรจามร | Date : 22/9/2569 |
|   | Phone :         | Email :                     | Page : 01        |
|   |                 |                             |                  |

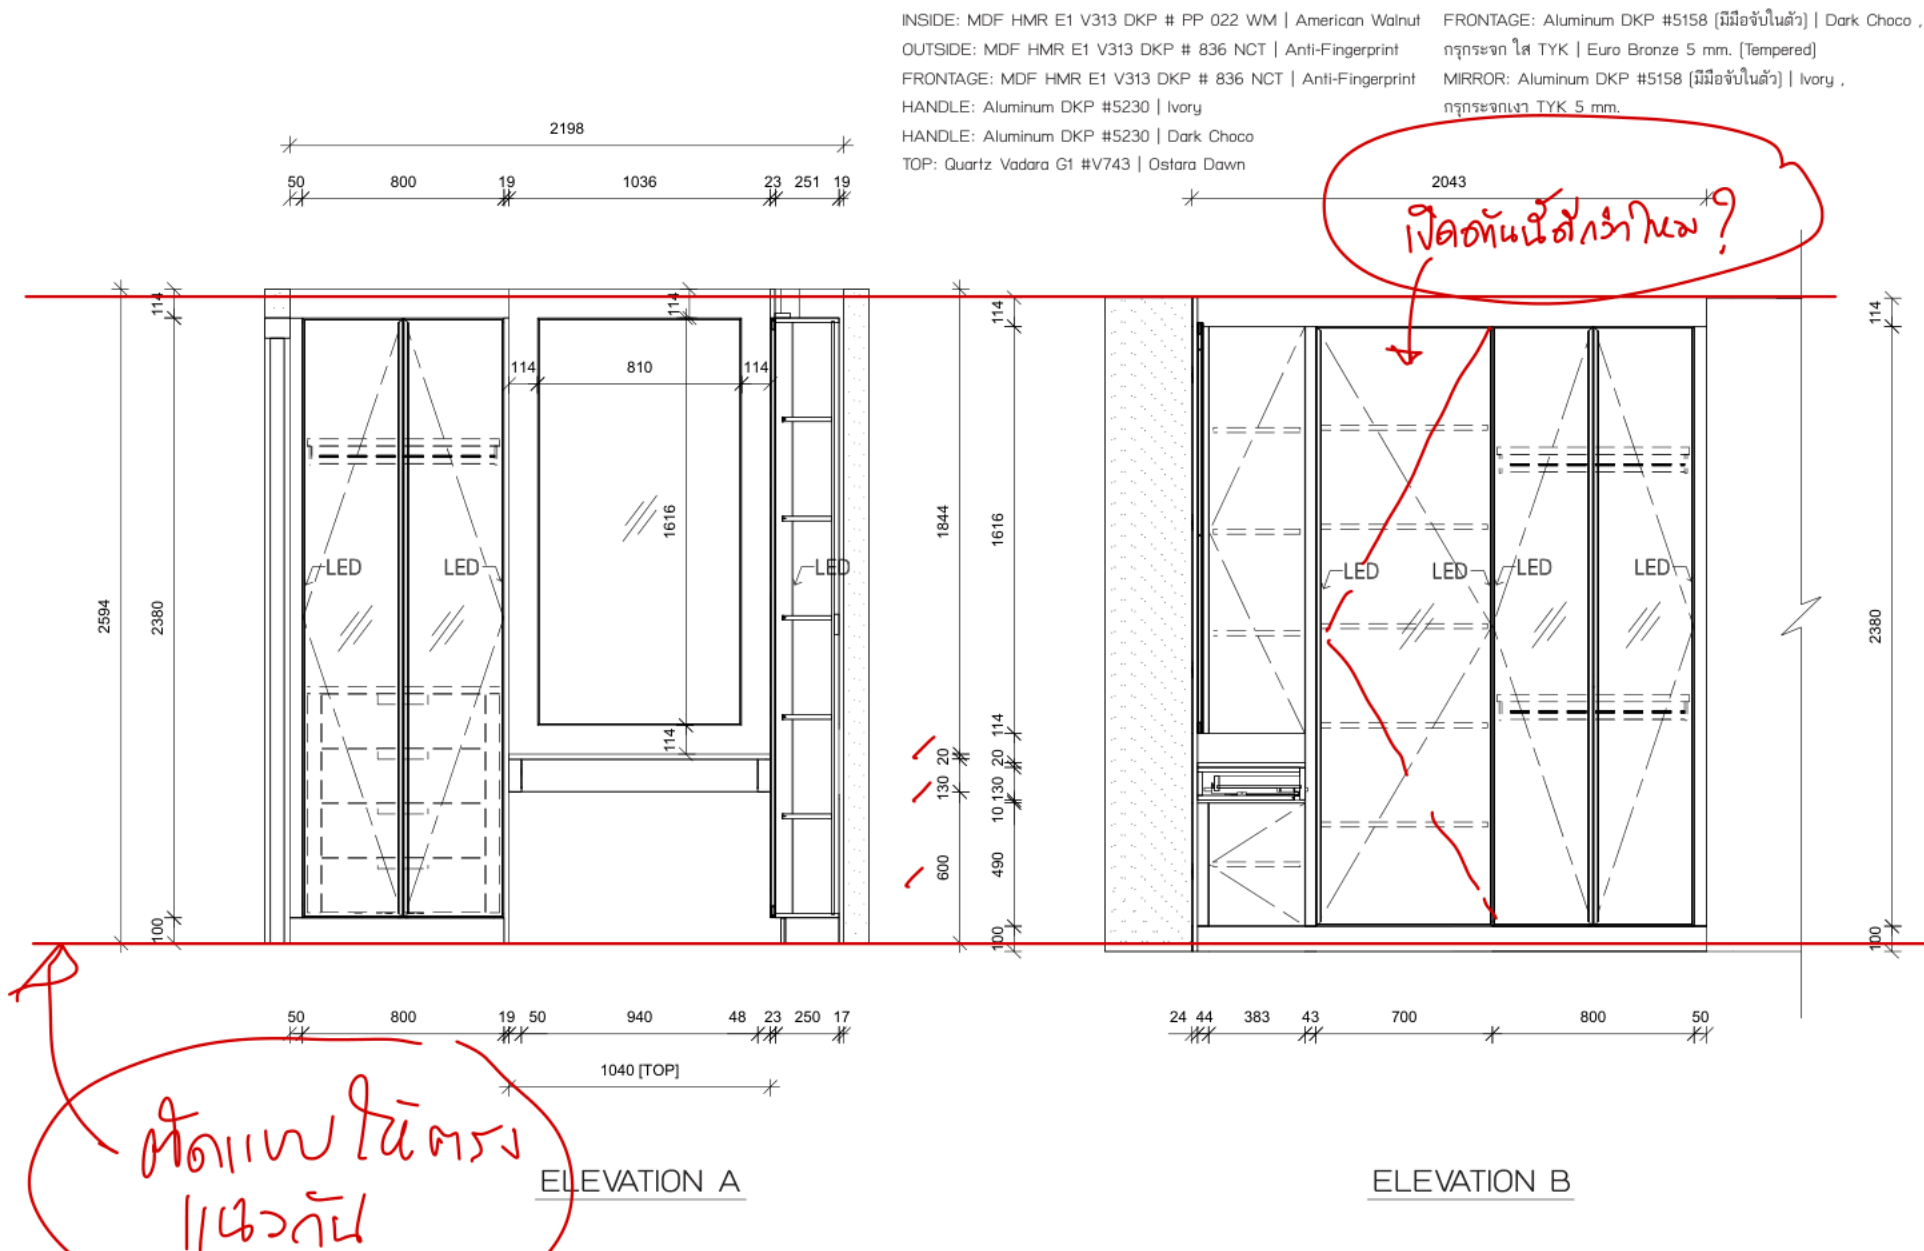

INSIDE: MDF HMR E1 V313 DKP # PP 022 WM | American Walnut  
OUTSIDE: MDF HMR E1 V313 DKP # 836 NCT | Anti-Fingerprint  
FRONTAGE: MDF HMR E1 V313 DKP # 836 NCT | Anti-Fingerprint  
HANDLE: Aluminum DKP #5230 | Ivory  
HANDLE: Aluminum DKP #5230 | Dark Choco  
TOP: Quartz Vadara G1 #V743 | Ostara Dawn  
FRONTAGE: Aluminum DKP #5158 (มีมือจับในตัว) | Dark Choco ,  
กรุกระจก ใส TYK | Euro Bronze 5 mm. [Tempered]  
MIRROR: Aluminum DKP #5158 (มีมือจับในตัว) | Ivory ,  
กรุกระจกเงา TYK 5 mm.

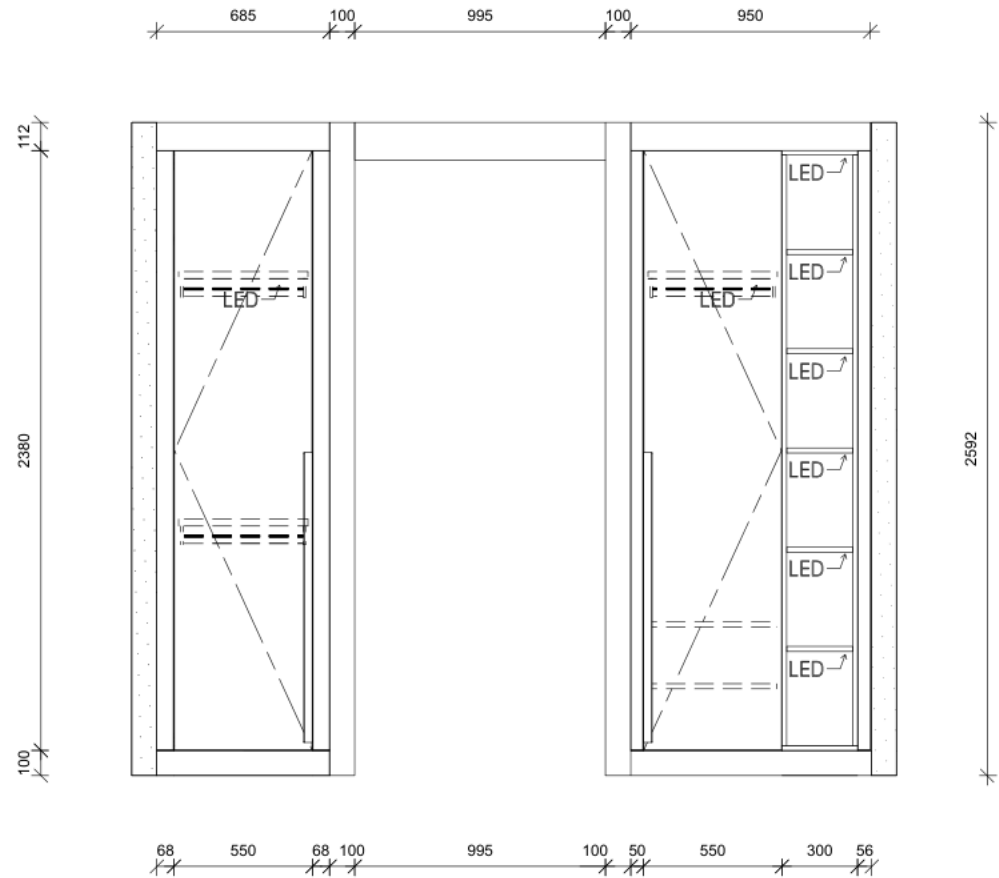

ELEVATION C

|   |                 |                             |                    |
|---|-----------------|-----------------------------|--------------------|
| <div><div>Dkbb</div><div>157 Praditmanutham Road<br/>Bangkapi Bangkok 10240<br/>TEL:0-2515-1162 FAX:0-2515-1161<br/>WWW.decorchoice.co.th</div></div> | Client : Ari789 | Design : WICMB-4C           | View : Elevation C |
|   | Address :       | Series : Elegance           | Scale : 1:30       |
|   | Province :      | Drawn by : บริษัท สุนทรจามร | Date : 22/9/2569   |
|   | Phone :         | Email :                     | Page : 03          |