














INSIDE: MDF HMR E1 V313 DKP # PP 022 WM | American Walnut
OUTSIDE: MDF HMR E1 V313 DKP # 836 NCT | Anti-Fingerprint
FRONTAGE: MDF HMR E1 V313 DKP # 836 NCT | Anti-Fingerprint
HANDLE: Aluminum DKP #5230 | Ivory
HANDLE: Aluminum DKP #5230 | Dark Choco
TOP: Quartz Vadara G1 #V743 | Ostara Dawn
FRONTAGE: Aluminum DKP #5158 (มีมือจับในตัว) | Dark Choco ,
กรุกระจกใส TYK | Euro Bronze 5 mm. (Tempered)
MIRROR: Aluminum DKP #5158 (มีมือจับในตัว) | Ivory ,
กรุกระจกเงา TYK 5 mm.

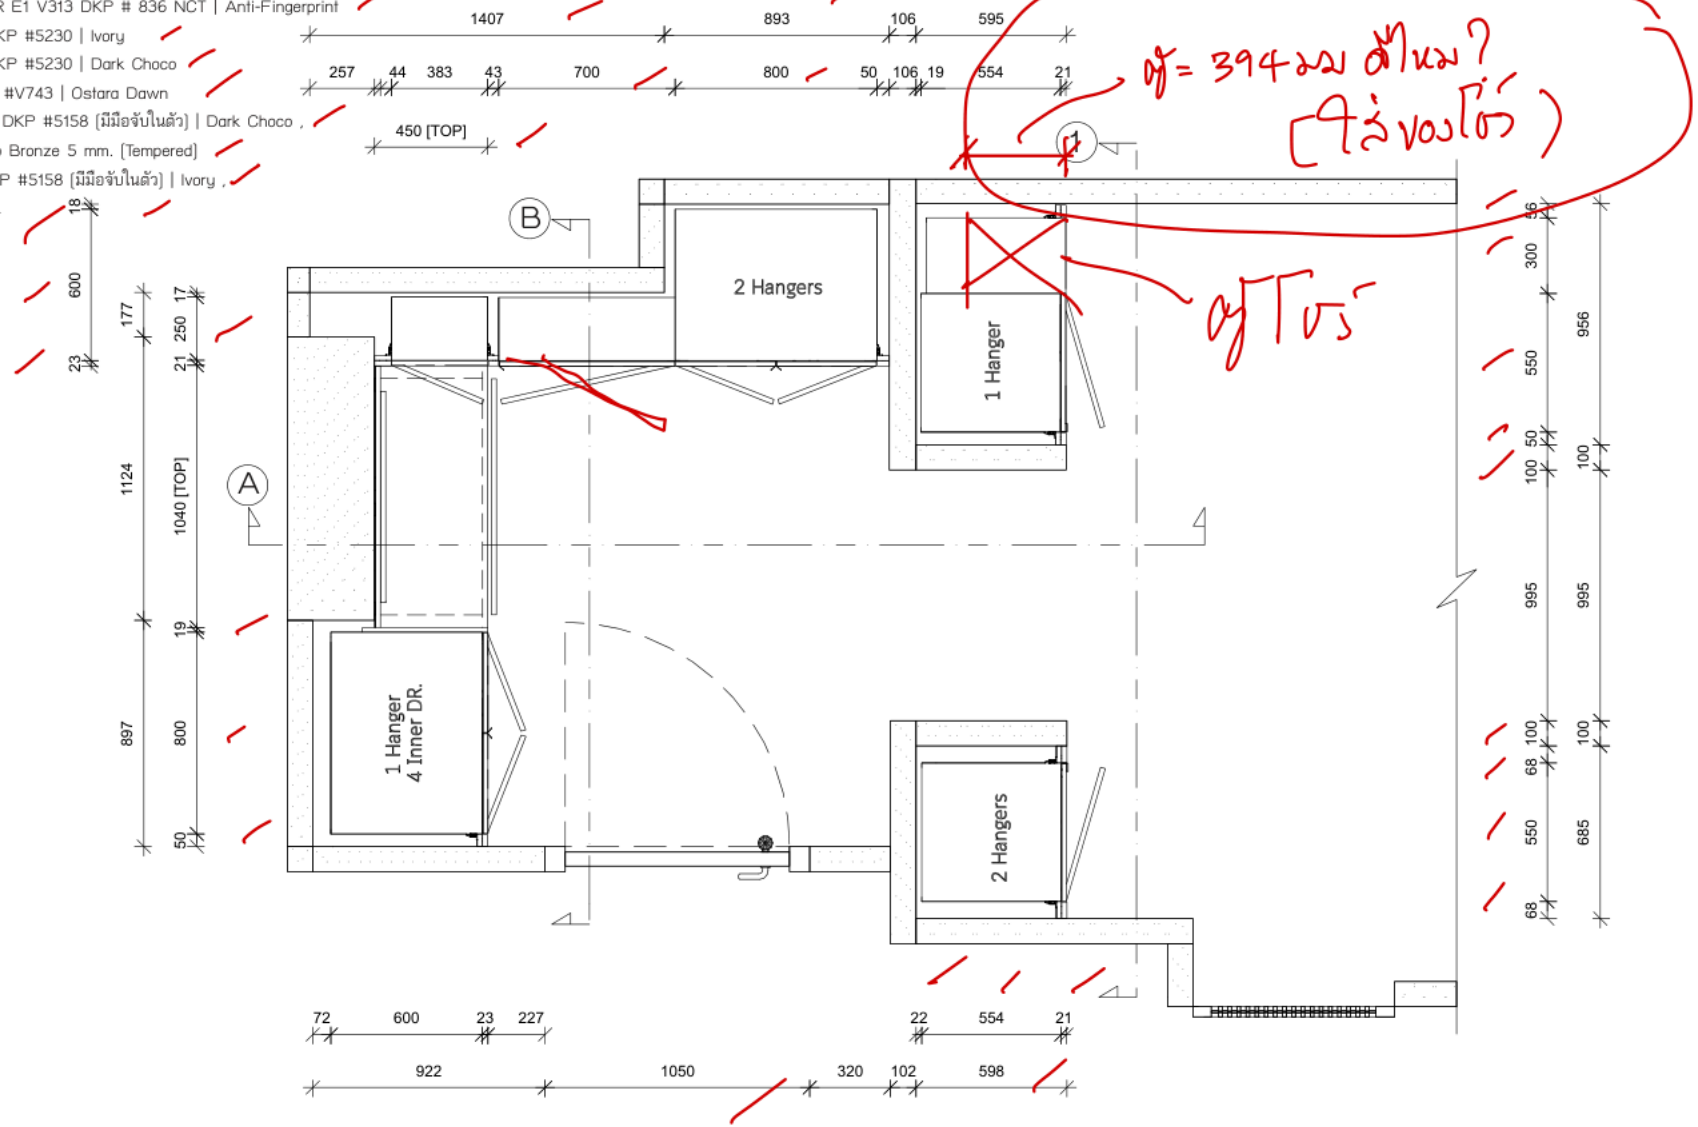

Dkbb 157 Praditmanutham Road Bangkapi Bangkok 10240 TEL:0-2515-1162 FAX:0-2515-1161 WWW.decorchoice.co.th	Client : Ari789	Design : WICMB-4C	View : Plan
	Address :	Series : Elegance	Scale : 1:30
	Province :	Drawn by : บริษัท สุนทรจามร	Date : 22/9/2569
	Phone :	Email :	Page : 01

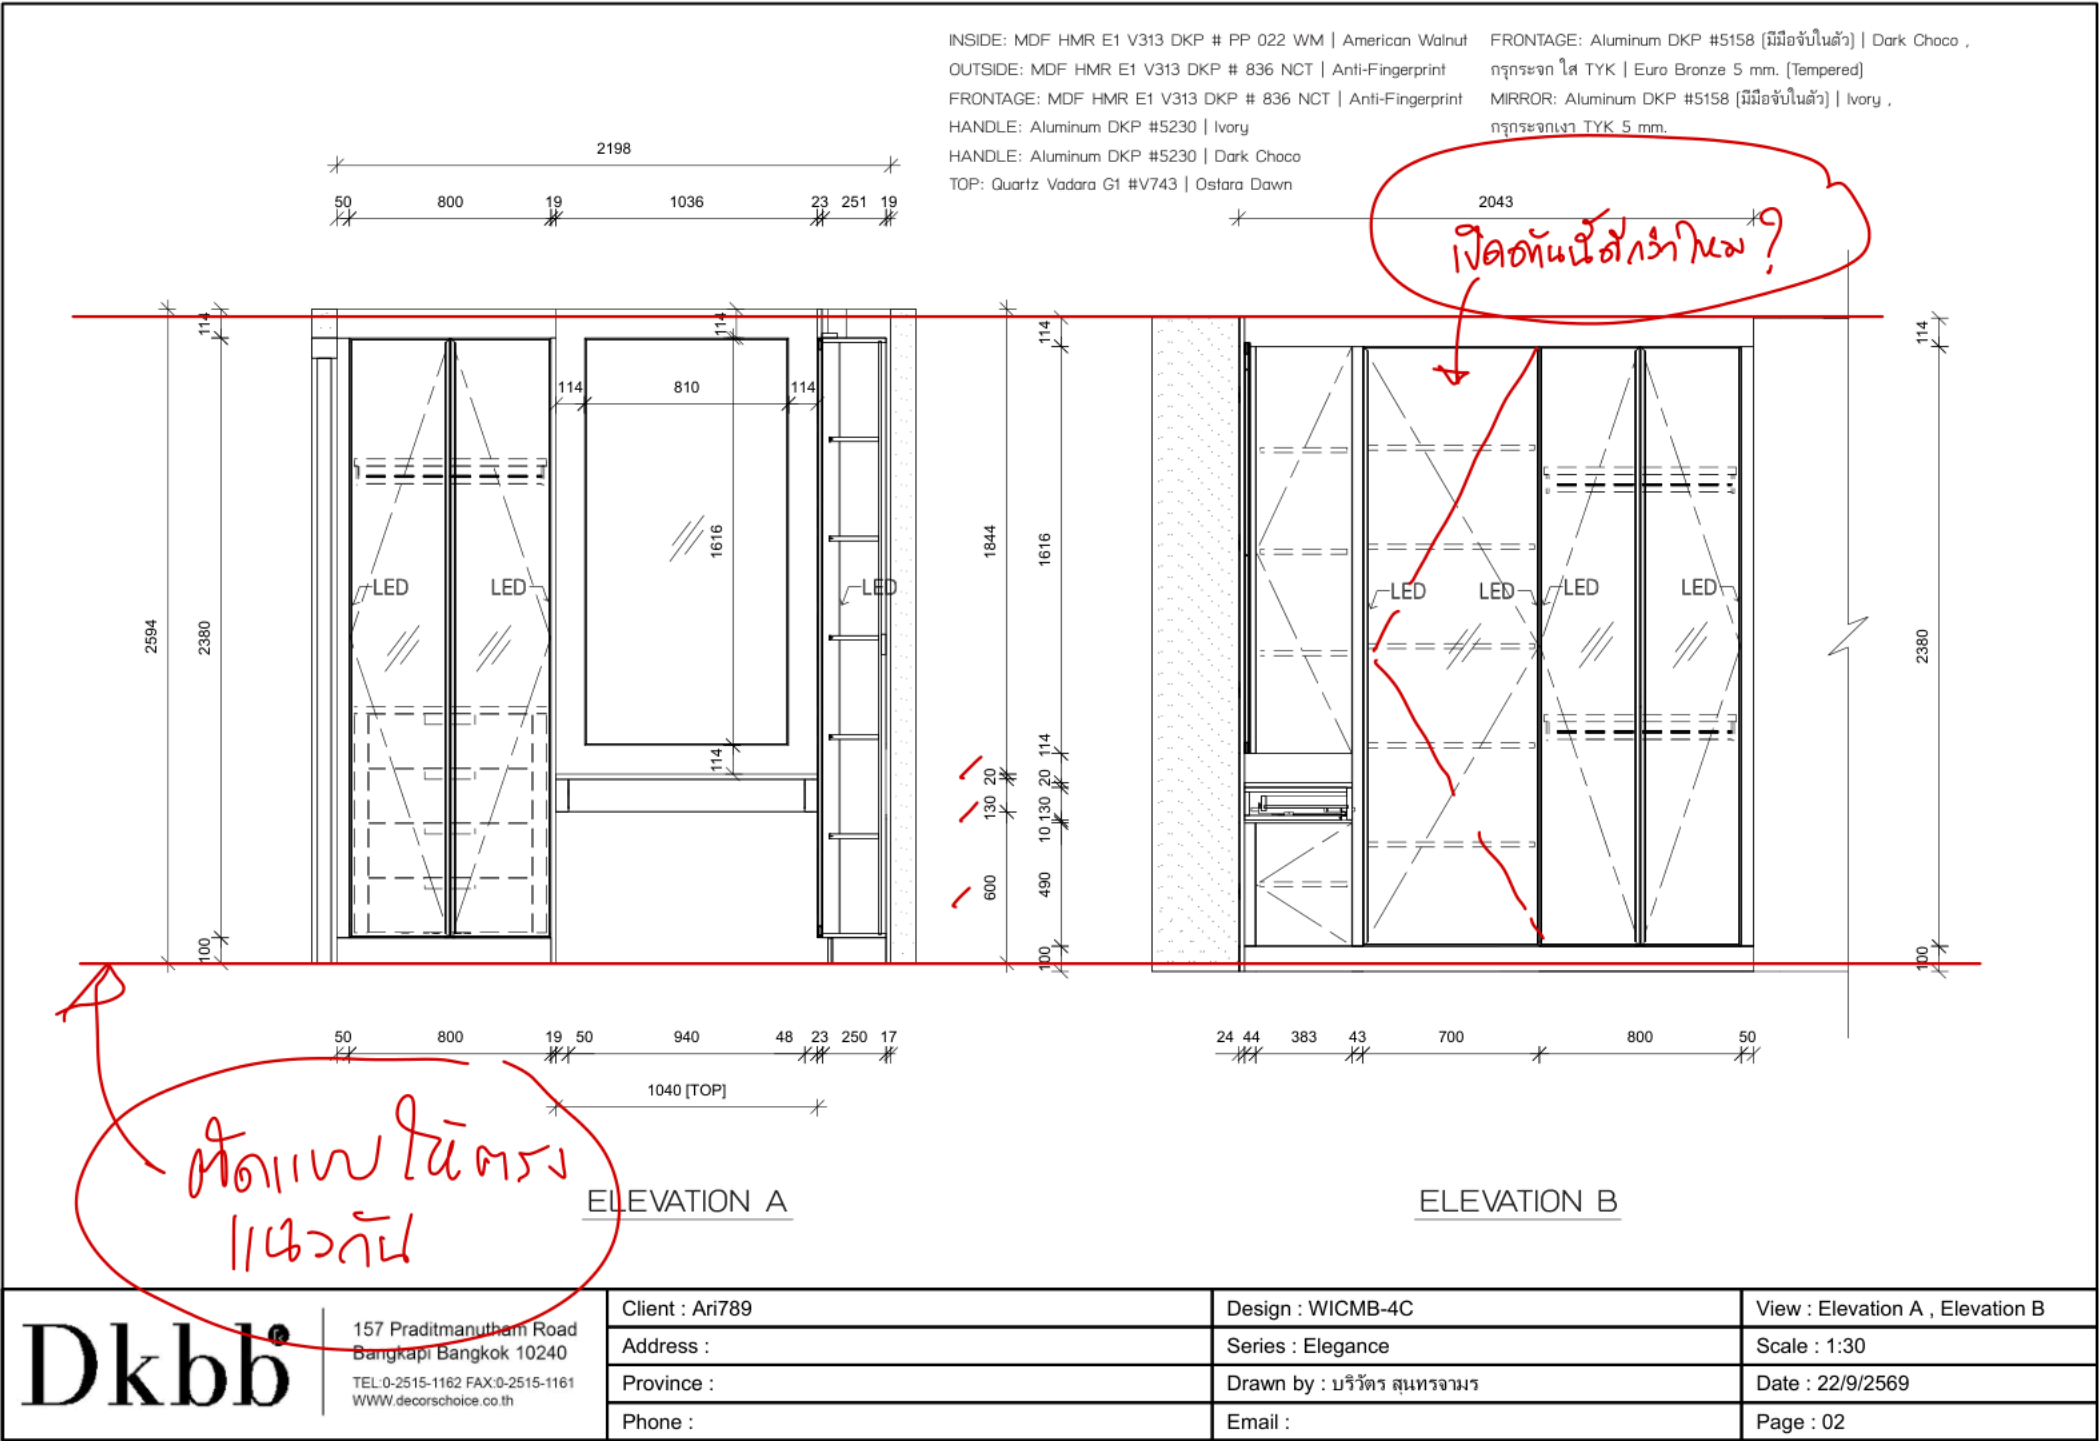

INSIDE: MDF HMR E1 V313 DKP # PP 022 WM | American Walnut
OUTSIDE: MDF HMR E1 V313 DKP # 836 NCT | Anti-Fingerprint
FRONTAGE: MDF HMR E1 V313 DKP # 836 NCT | Anti-Fingerprint
HANDLE: Aluminum DKP #5230 | Ivory
HANDLE: Aluminum DKP #5230 | Dark Choco
TOP: Quartz Vadara G1 #V743 | Ostara Dawn
FRONTAGE: Aluminum DKP #5158 (มีมือจับในตัว) | Dark Choco ,
กรุกระจกใส TYK | Euro Bronze 5 mm. [Tempered]
MIRROR: Aluminum DKP #5158 (มีมือจับในตัว) | Ivory ,
กรุกระจกเงา TYK 5 mm.

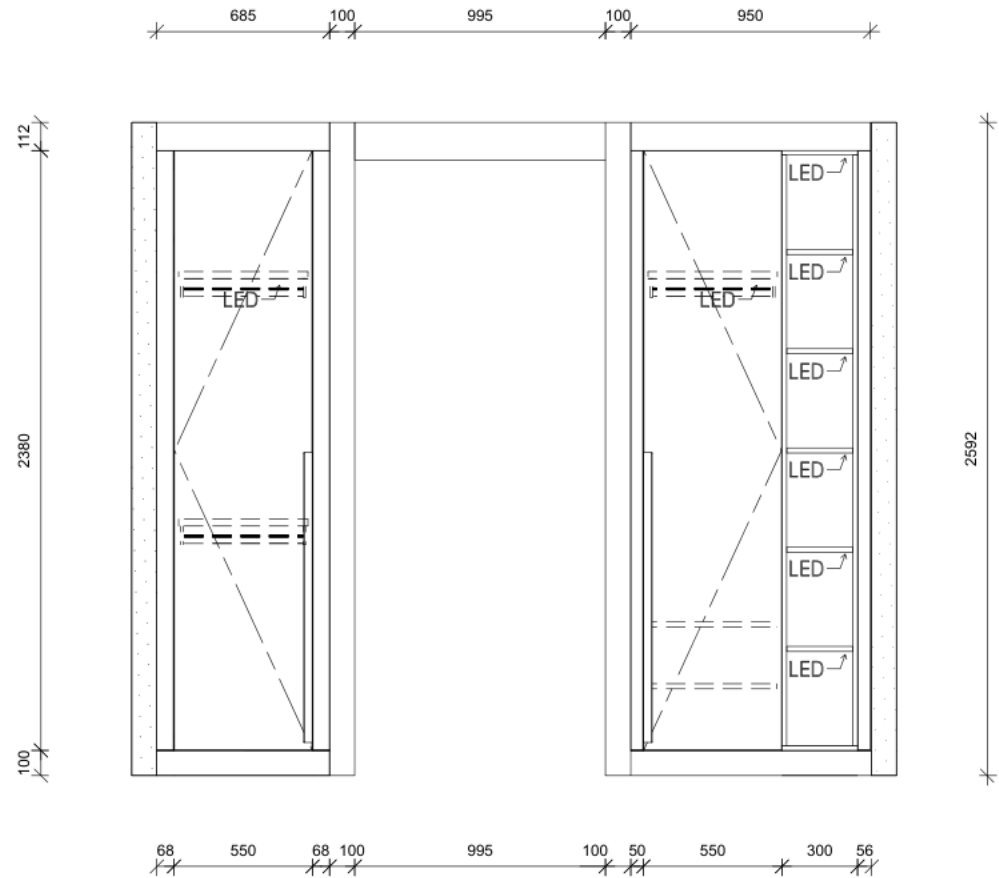

ELEVATION C

Dkbb 157 Praditmanutham Road Bangkapi Bangkok 10240 TEL:0-2515-1162 FAX:0-2515-1161 WWW.decorchoice.co.th	Client : Ari789	Design : WICMB-4C	View : Elevation C
	Address :	Series : Elegance	Scale : 1:30
	Province :	Drawn by : บริษัท สุนทรจามร	Date : 22/9/2569
	Phone :	Email :	Page : 03