


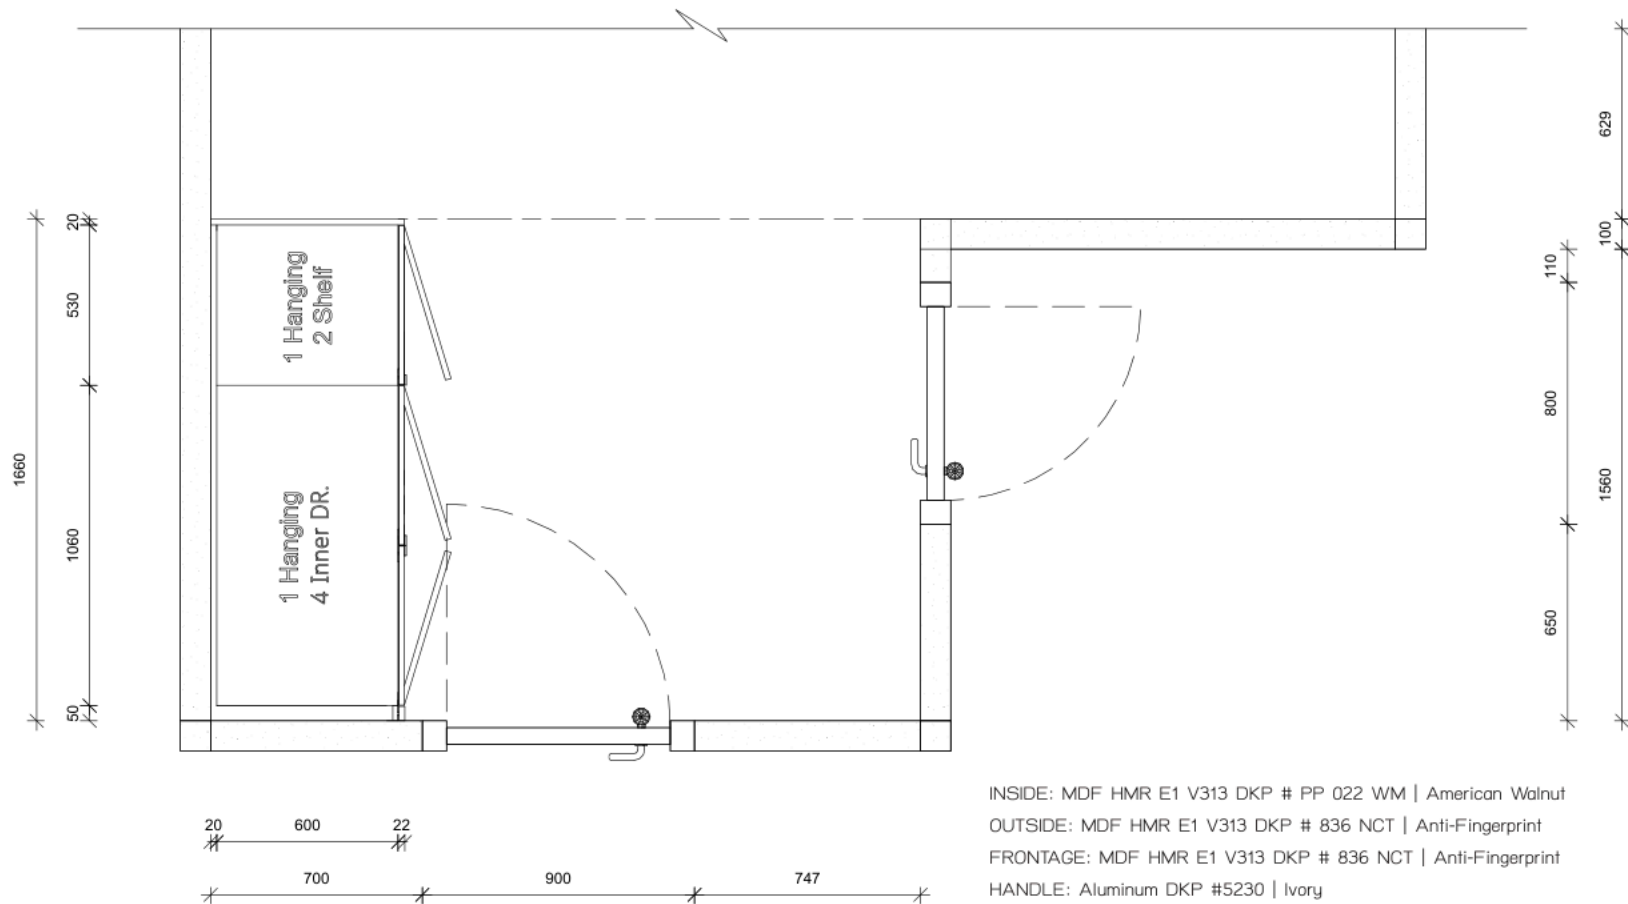

Dkbb

157 Praditmanutham Road
Bangkapi Bangkok 10240
TEL: 0-2515-1162 FAX: 0-2515-1161
WWW.decorchoice.co.th

Client : ARI789

Address :

Province :-

Phone :

Design : Bedroom 2 - Walk in 4A

Series : Elegance

Drawn by : Sunisa


Email :

View : Plan

Scale : 1:25

Date : 11/6/2569

Page : 01

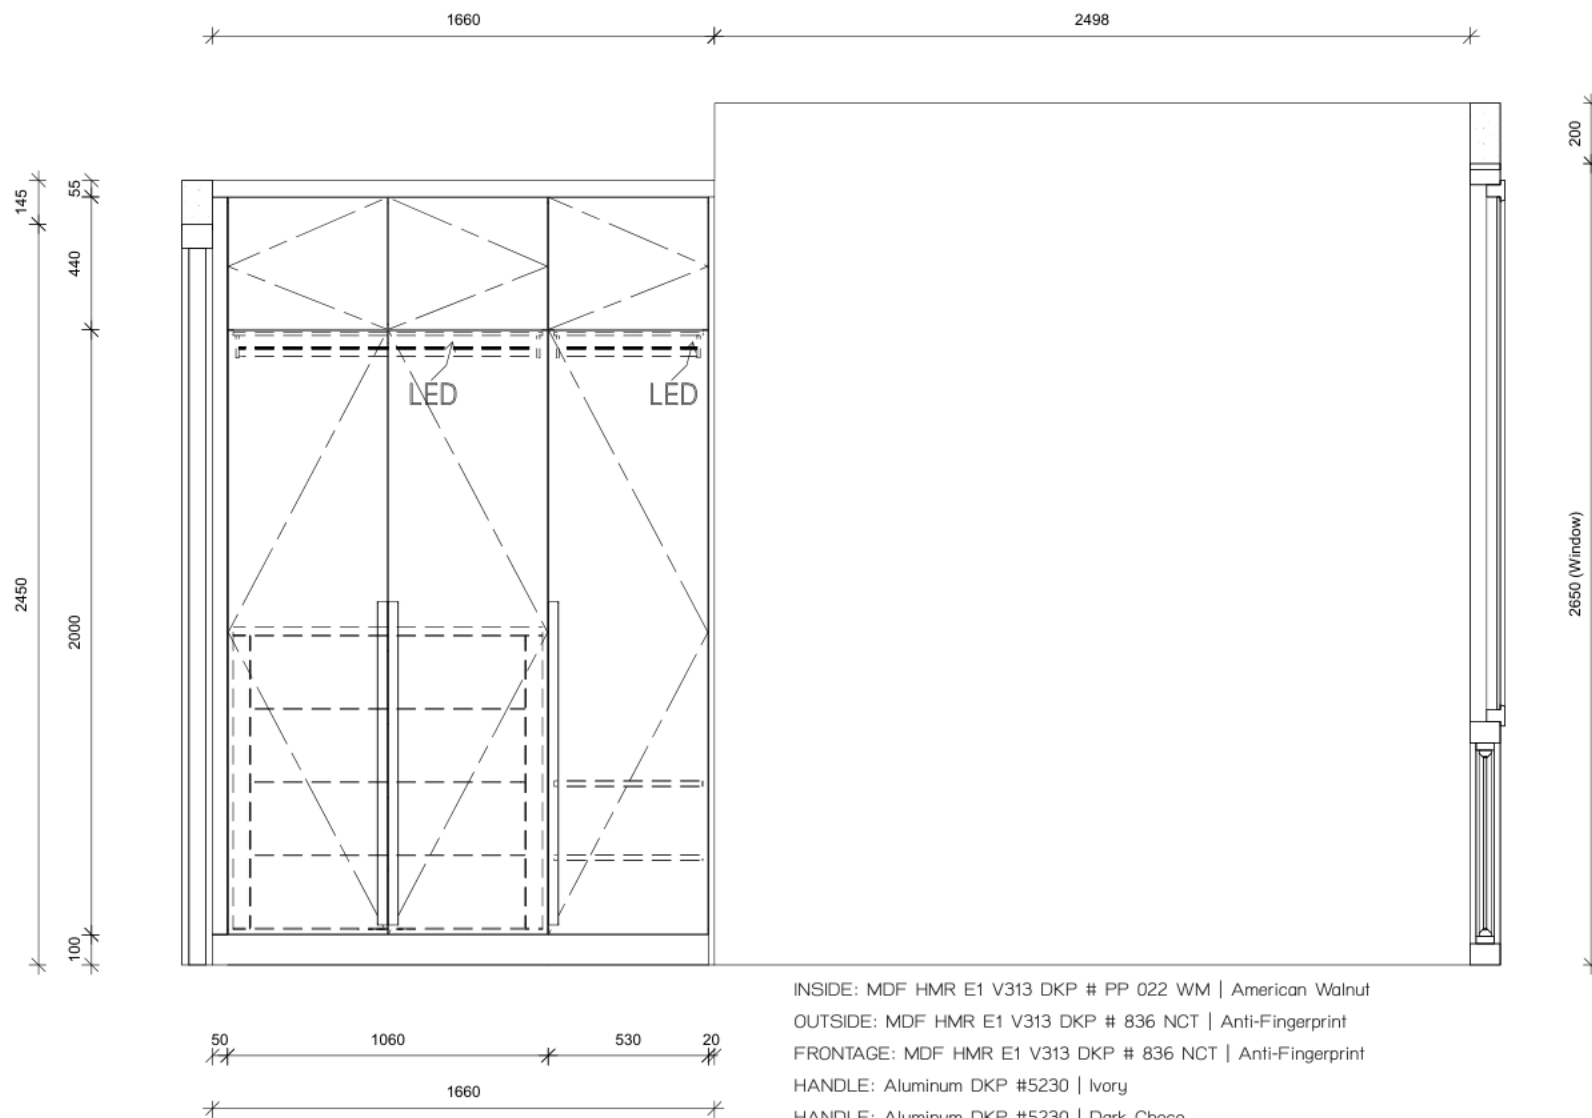

Dkbb

157 Praditmanutham Road
Bangkapi Bangkok 10240
TEL: 0-2515-1162 FAX: 0-2515-1161
WWW.decorchoice.co.th

Client : ARI789

Address :

Province :-

Phone :

Design : Bedroom 2 - Walk in 4A

Series : Elegance

Drawn by : Sunisa


Email :

View : Elevation A

Scale : 1:25

Date : 11/6/2569

Page : 02

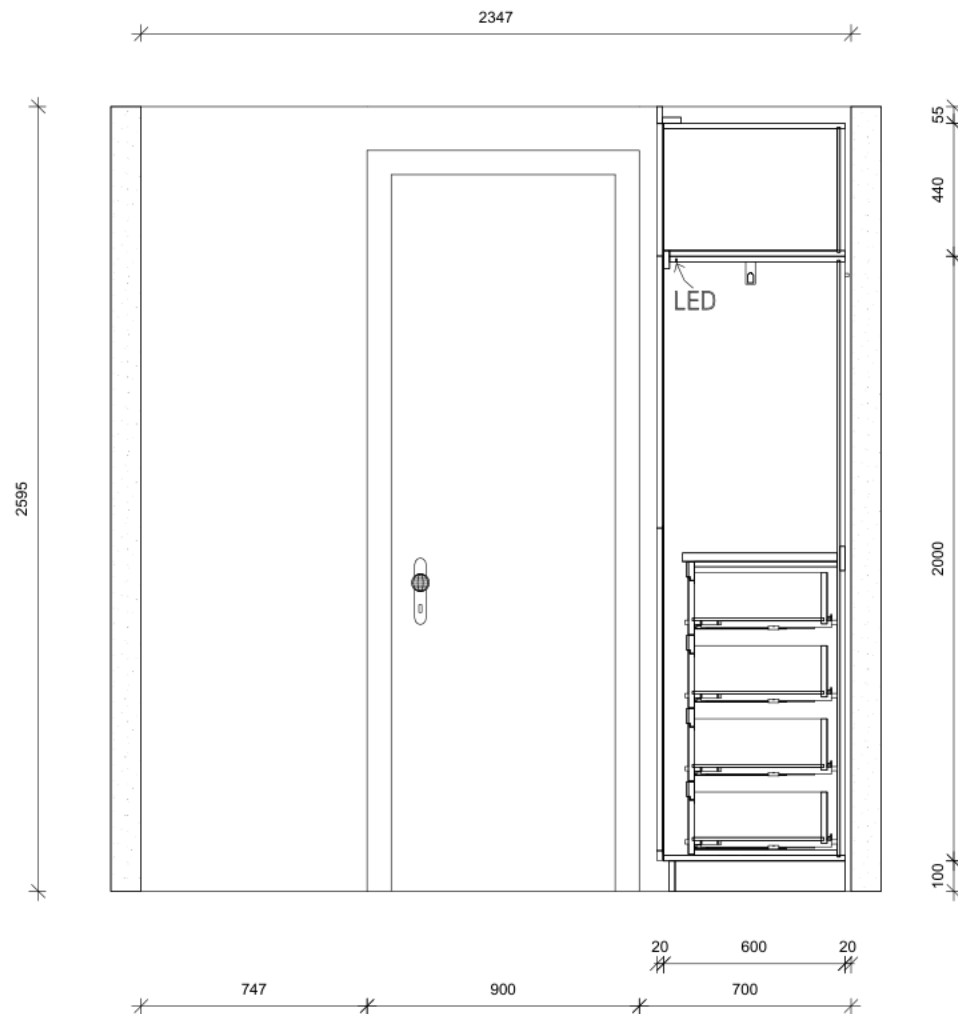


INSIDE: MDF HMR E1 V313 DKP # PP 022 WM | American Walnut
 OUTSIDE: MDF HMR E1 V313 DKP # 836 NCT | Anti-Fingerprint
 FRONTAGE: MDF HMR E1 V313 DKP # 836 NCT | Anti-Fingerprint
 HANDLE: Aluminum DKP #5230 | Ivory
 HANDLE: Aluminum DKP #5230 | Dark Choco

Dkbb

157 Praditmanutham Road
 Bangkapi Bangkok 10240
 TEL:0-2515-1162 FAX:0-2515-1161
 WWW.decorchoice.co.th

Client : ARI789	Design : Bedroom 2 - Walk in 4A	View : Section 1
Address :	Series : Elegance	Scale : 1:30
Province :-	Drawn by : Sunisa	Date : 11/6/2569
Phone :	Email :	Page : 03

INSIDE: MDF HMR E1 V313 DKP # PP 022 WM | American Walnut
 OUTSIDE: MDF HMR E1 V313 DKP # 836 NCT | Anti-Fingerprint
 FRONTAGE: MDF HMR E1 V313 DKP # 836 NCT | Anti-Fingerprint
 HANDLE: Aluminum DKP #5230 | Ivory
 HANDLE: Aluminum DKP #5230 | Dark Choco
 TOP: Quartz Vadara G1 #V743 | Ostara Dawn
 FRONTAGE: Aluminum DKP #5158 (มีมือจับในตัว) | Dark Choco ,
 กระจกใส TYK | Euro Bronze 5 mm. (Tempered)

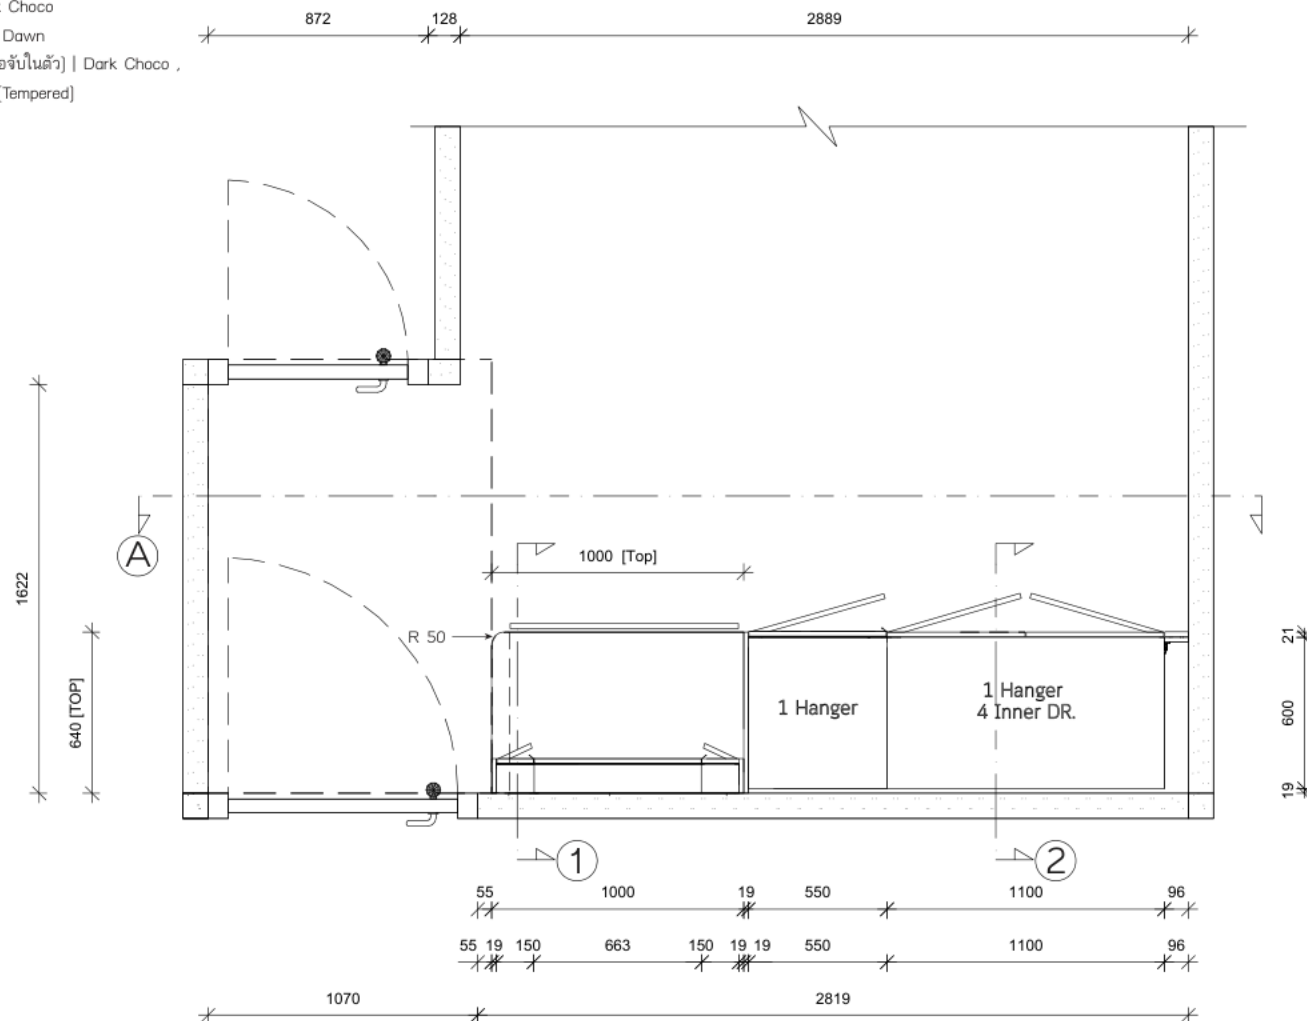

Dkbb

157 Praditmanutham Road
 Bangkapi Bangkok 10240
 TEL:0-2515-1162 FAX:0-2515-1161
 WWW.decorchoice.co.th

Client : Ari789

Address :

Province :

Phone :

Design : WIC1-4A

Series : Elegance

Drawn by : บริษัท สุนทรจามร

Email :


View : Plan

Scale : 1:30

Date : 18/9/2569

Page : 01

INSIDE: MDF HMR E1 V313 DKP # PP 022 WM | American Walnut
OUTSIDE: MDF HMR E1 V313 DKP # 836 NCT | Anti-Fingerprint
FRONTAGE: MDF HMR E1 V313 DKP # 836 NCT | Anti-Fingerprint
HANDLE: Aluminum DKP #5230 | Ivory
HANDLE: Aluminum DKP #5230 | Dark Choco
TOP: Quartz Vadara G1 #V743 | Ostara Dawn
FRONTAGE: Aluminum DKP #5158 (มีมือจับในตัว) | Dark Choco ,
กระจกใส TYK | Euro Bronze 5 mm. [Tempered]


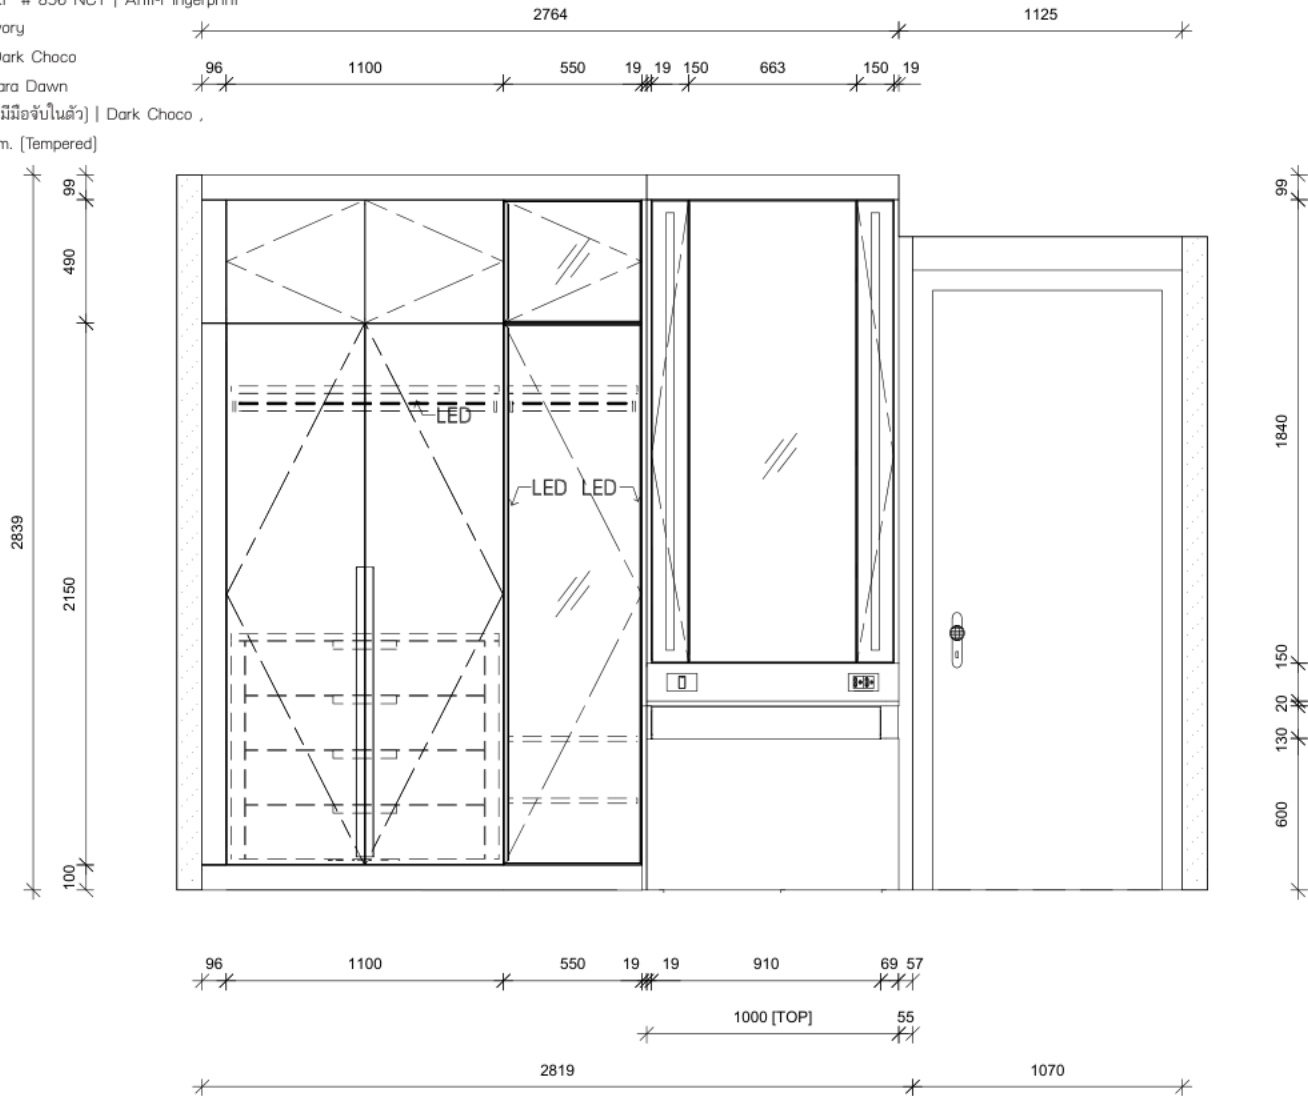


Dkbb



157 Praditmanutham Road
Bangkapi Bangkok 10240
TEL:0-2515-1162 FAX:0-2515-1161
WWW.decorchoice.co.th

Client : Ari789	Design : WIC1-4A	View : Elevation A
Address :	Series : Elegance	Scale : 1:30
Province :	Drawn by : บริษัท สุนทรจามร	Date : 18/9/2569
Phone :	Email :	Page : 02

INSIDE: MDF HMR E1 V313 DKP # PP 022 WM | American Walnut
OUTSIDE: MDF HMR E1 V313 DKP # 836 NCT | Anti-Fingerprint
FRONTAGE: MDF HMR E1 V313 DKP # 836 NCT | Anti-Fingerprint
HANDLE: Aluminum DKP #5230 | Ivory
HANDLE: Aluminum DKP #5230 | Dark Choco
TOP: Quartz Vadara G1 #V743 | Ostara Dawn
FRONTAGE: Aluminum DKP #5158 [มีมือจับในตัว] | Dark Choco ,
กระจกใส TYK | Euro Bronze 5 mm. (Tempered)

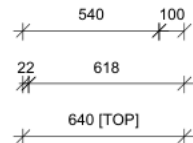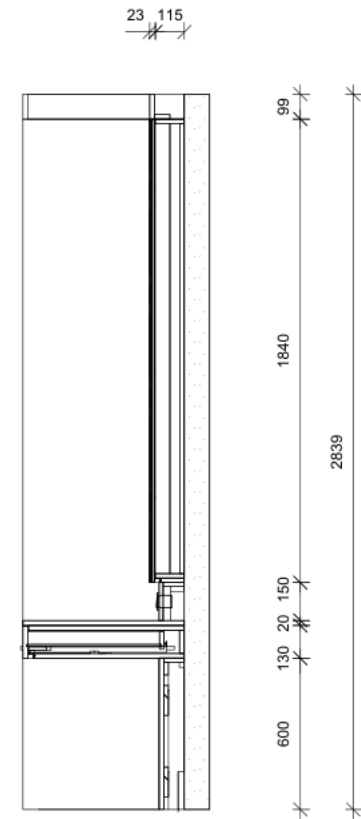

SECTION 1

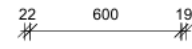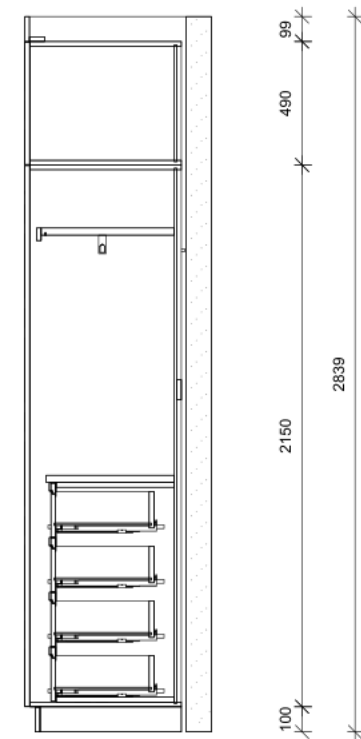


SECTION 2



157 Praditmanutham Road
Bangkapi Bangkok 10240
TEL:0-2515-1162 FAX:0-2515-1161
WWW.decorchoice.co.th

Client : Ari789	Design : WIC1-4A	View : Section 1
Address :	Series : Elegance	Scale : 1:30
Province :	Drawn by : บริษัท สุนทรจามร	Date : 18/9/2569
Phone :	Email :	Page : 03

INSIDE: MDF HMR E1 V313 DKP # PP 022 WM | American Walnut
 OUTSIDE: MDF HMR E1 V313 DKP # 836 NCT | Anti-Fingerprint
 FRONTAGE: MDF HMR E1 V313 DKP # 836 NCT | Anti-Fingerprint
 HANDLE: Aluminum DKP #5230 | Ivory
 HANDLE: Aluminum DKP #5230 | Dark Choco
 TOP: Quartz Vadara G1 #V743 | Ostara Dawn
 FRONTAGE: Aluminum DKP #5158 (มีมือจับในตัว) | Dark Choco ,
 กระจกใส TYK | Euro Bronze 5 mm. (Tempered)

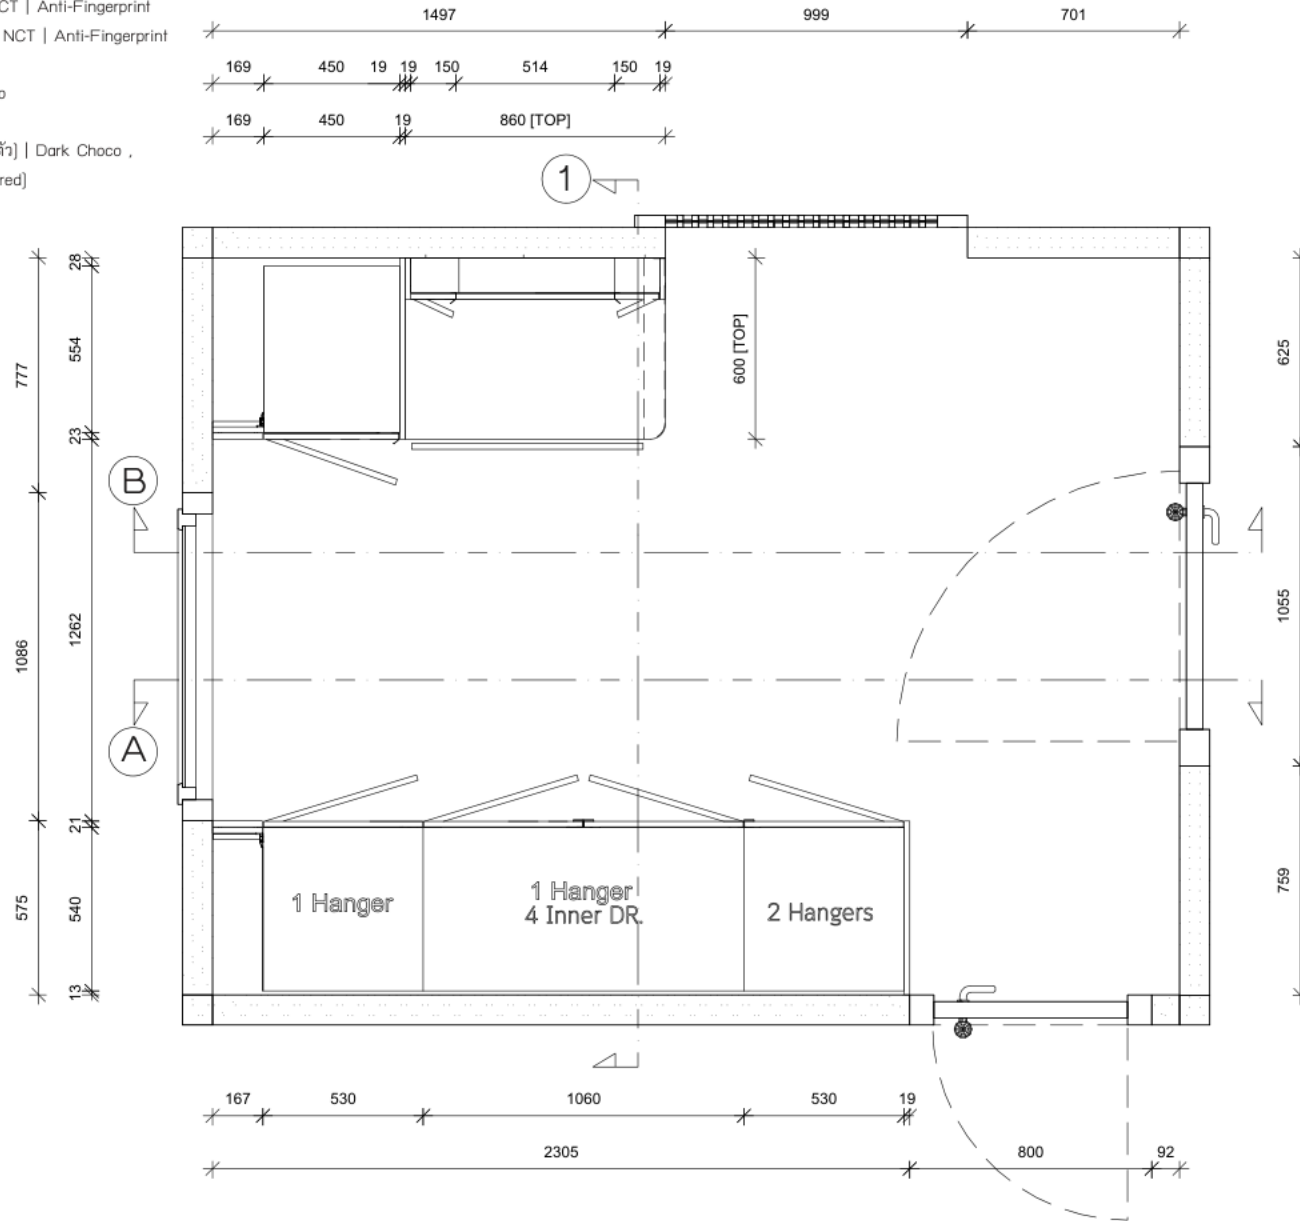


Dkbb

157 Praditmanutham Road
 Bangkapi Bangkok 10240
 TEL:0-2515-1162 FAX:0-2515-1161
 WWW.decorchoice.co.th


Client : Ari789	Design : WICMB-4A	View : Plan
Address :	Series : Elegance	Scale : 1:25
Province :	Drawn by : บริษัท สุนทรจามร	Date : 18/9/2569
Phone :	Email :	Page : 01

INSIDE: MDF HMR E1 V313 DKP # PP 022 WM | American Walnut
OUTSIDE: MDF HMR E1 V313 DKP # 836 NCT | Anti-Fingerprint
FRONTAGE: MDF HMR E1 V313 DKP # 836 NCT | Anti-Fingerprint
HANDLE: Aluminum DKP #5230 | Ivory
HANDLE: Aluminum DKP #5230 | Dark Choco
TOP: Quartz Vadara G1 #V743 | Ostara Dawn
FRONTAGE: Aluminum DKP #5158 (มีมือจับในตัว) | Dark Choco ,
กรุกระจก ใส TYK | Euro Bronze 5 mm. (Tempered)

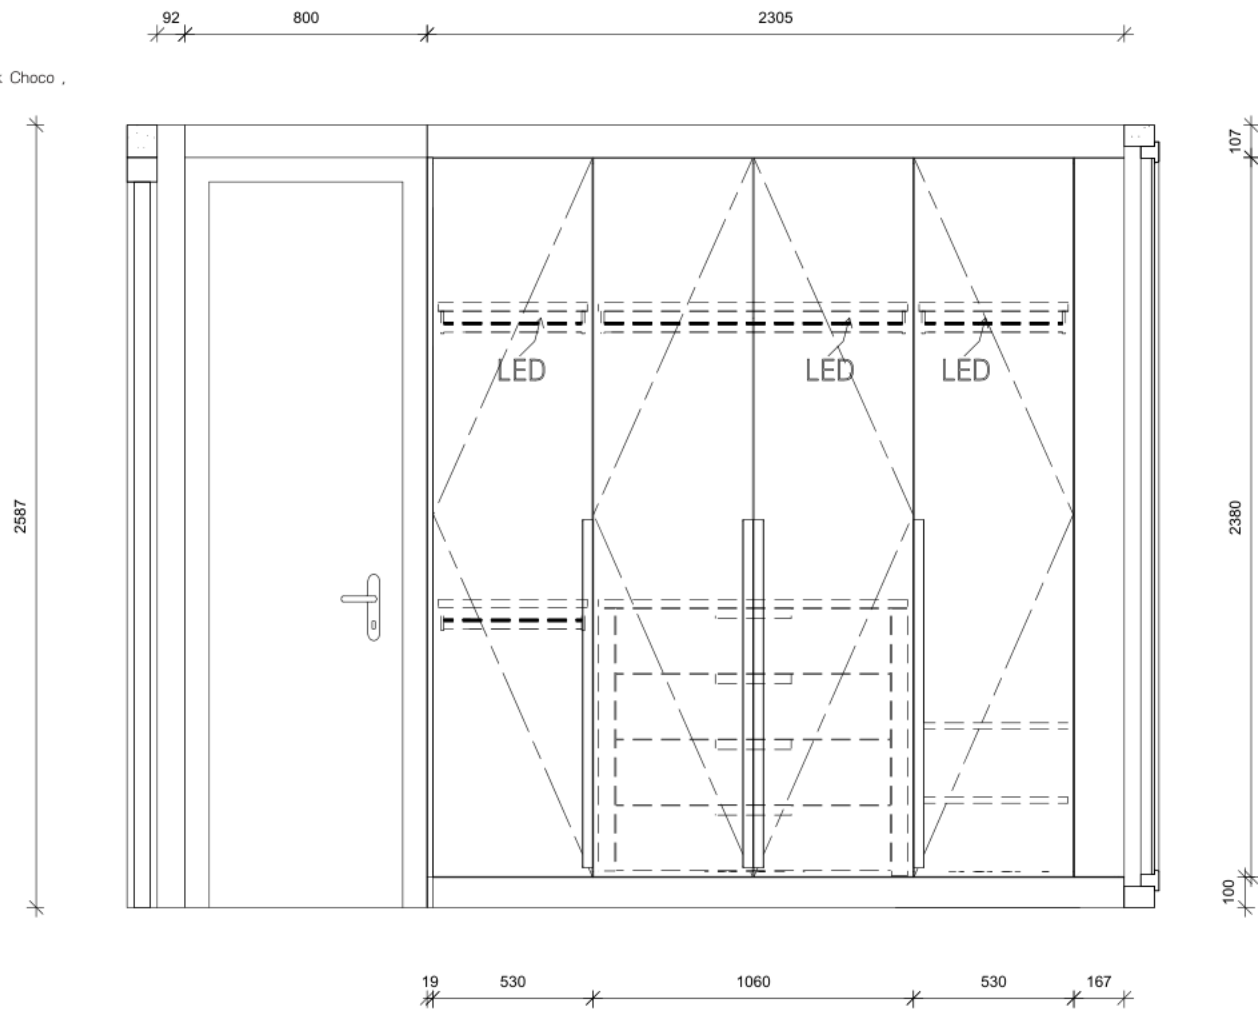

Dkbb 157 Praditmanutham Road Bangkapi Bangkok 10240 TEL:0-2515-1162 FAX:0-2515-1161 WWW.decorchoice.co.th	Client : Ari789	Design : WICMB-4A	View : Elevation A
	Address :	Series : Elegance	Scale : 1:25
	Province :	Drawn by : บริษัท สุนทรจามร	Date : 18/9/2569
	Phone :	Email :	Page : 02

INSIDE: MDF HMR E1 V313 DKP # PP 022 WM | American Walnut
OUTSIDE: MDF HMR E1 V313 DKP # 836 NCT | Anti-Fingerprint
FRONTAGE: MDF HMR E1 V313 DKP # 836 NCT | Anti-Fingerprint
HANDLE: Aluminum DKP #5230 | Ivory
HANDLE: Aluminum DKP #5230 | Dark Choco
TOP: Quartz Vadara G1 #V743 | Ostara Dawn
FRONTAGE: Aluminum DKP #5158 (มีมือจับในตัว) | Dark Choco ,
กรุกระจกใส TYK | Euro Bronze 5 mm. (Tempered)

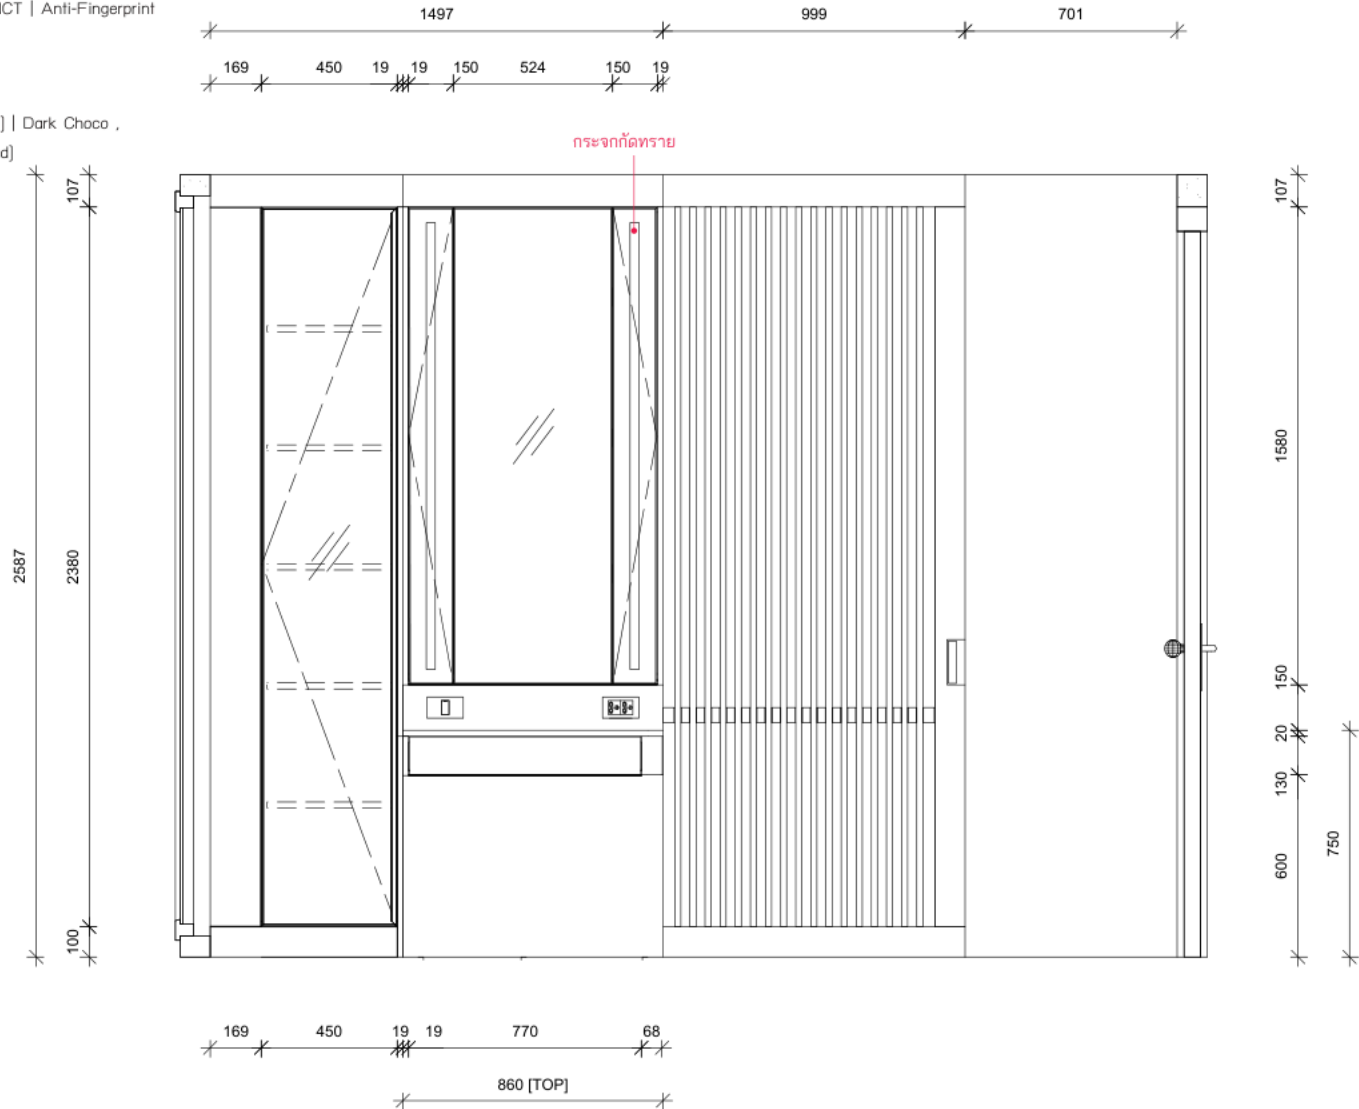


Dkbb

157 Praditmanutham Road
Bangkapi Bangkok 10240
TEL:0-2515-1162 FAX:0-2515-1161
WWW.decorchoice.co.th

Client : Ari789	Design : WICMB-4A	View : Elevation B
Address :	Series : Elegance	Scale : 1:25
Province :	Drawn by : บริษัท สุนทรจามร	Date : 18/9/2569
Phone :	Email :	Page : 03

INSIDE: MDF HMR E1 V313 DKP # PP 022 WM | American Walnut
OUTSIDE: MDF HMR E1 V313 DKP # 836 NCT | Anti-Fingerprint
FRONTAGE: MDF HMR E1 V313 DKP # 836 NCT | Anti-Fingerprint
HANDLE: Aluminum DKP #5230 | Ivory
HANDLE: Aluminum DKP #5230 | Dark Choco
TOP: Quartz Vadara G1 #V743 | Ostara Dawn
FRONTAGE: Aluminum DKP #5158 (มีมือจับในตัว) | Dark Choco ,
กรุกระจกใส TYK | Euro Bronze 5 mm. (Tempered)

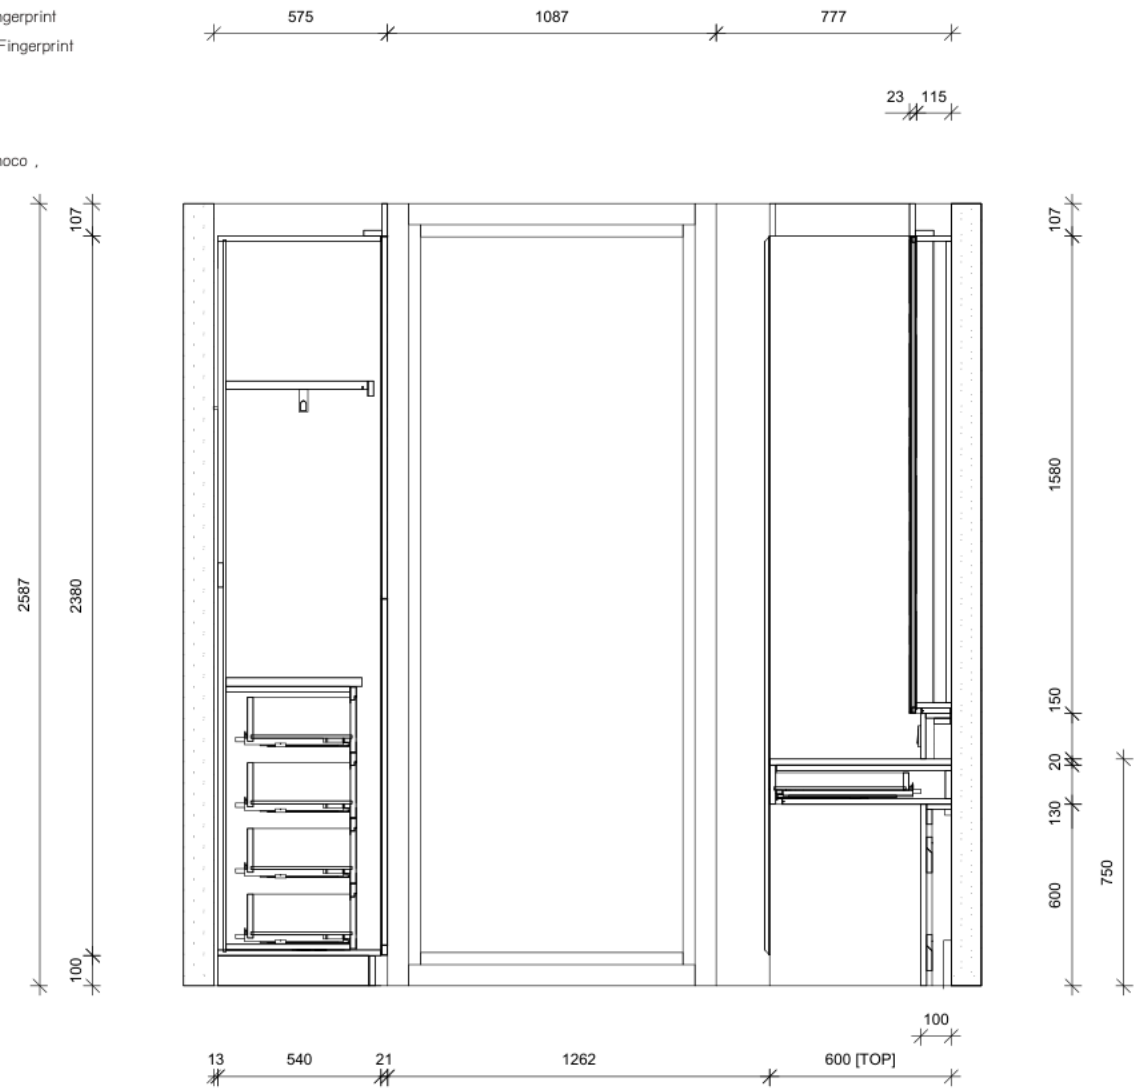

Dkbb

157 Praditmanutham Road
Bangkapi Bangkok 10240
TEL:0-2515-1162 FAX:0-2515-1161
WWW.decorchoice.co.th

Client : Ari789	Design : WICMB-4A	View : Section 1
Address :	Series : Elegance	Scale : 1:25
Province :	Drawn by : บริษัท สุนทรจามร	Date : 18/9/2569
Phone :	Email :	Page : 04