


INSIDE: MDF HMR E1 V313 DKP # PP 022 WM | American Walnut
 OUTSIDE: MDF HMR E1 V313 DKP # 836 NCT | Anti-Fingerprint
 FRONTAGE: MDF HMR E1 V313 DKP # 836 NCT | Anti-Fingerprint
 HANDLE: Aluminum DKP #5230 | Ivory
 HANDLE: Aluminum DKP #5230 | Dark Choco
 TOP: Quartz Vadara G1 #V743 | Ostara Dawn
 FRONTAGE: Aluminum DKP #5158 (มีมือจับในตัว) | Dark Choco ,
 กระจกใส TYK | Euro Bronze 5 mm. (Tempered)

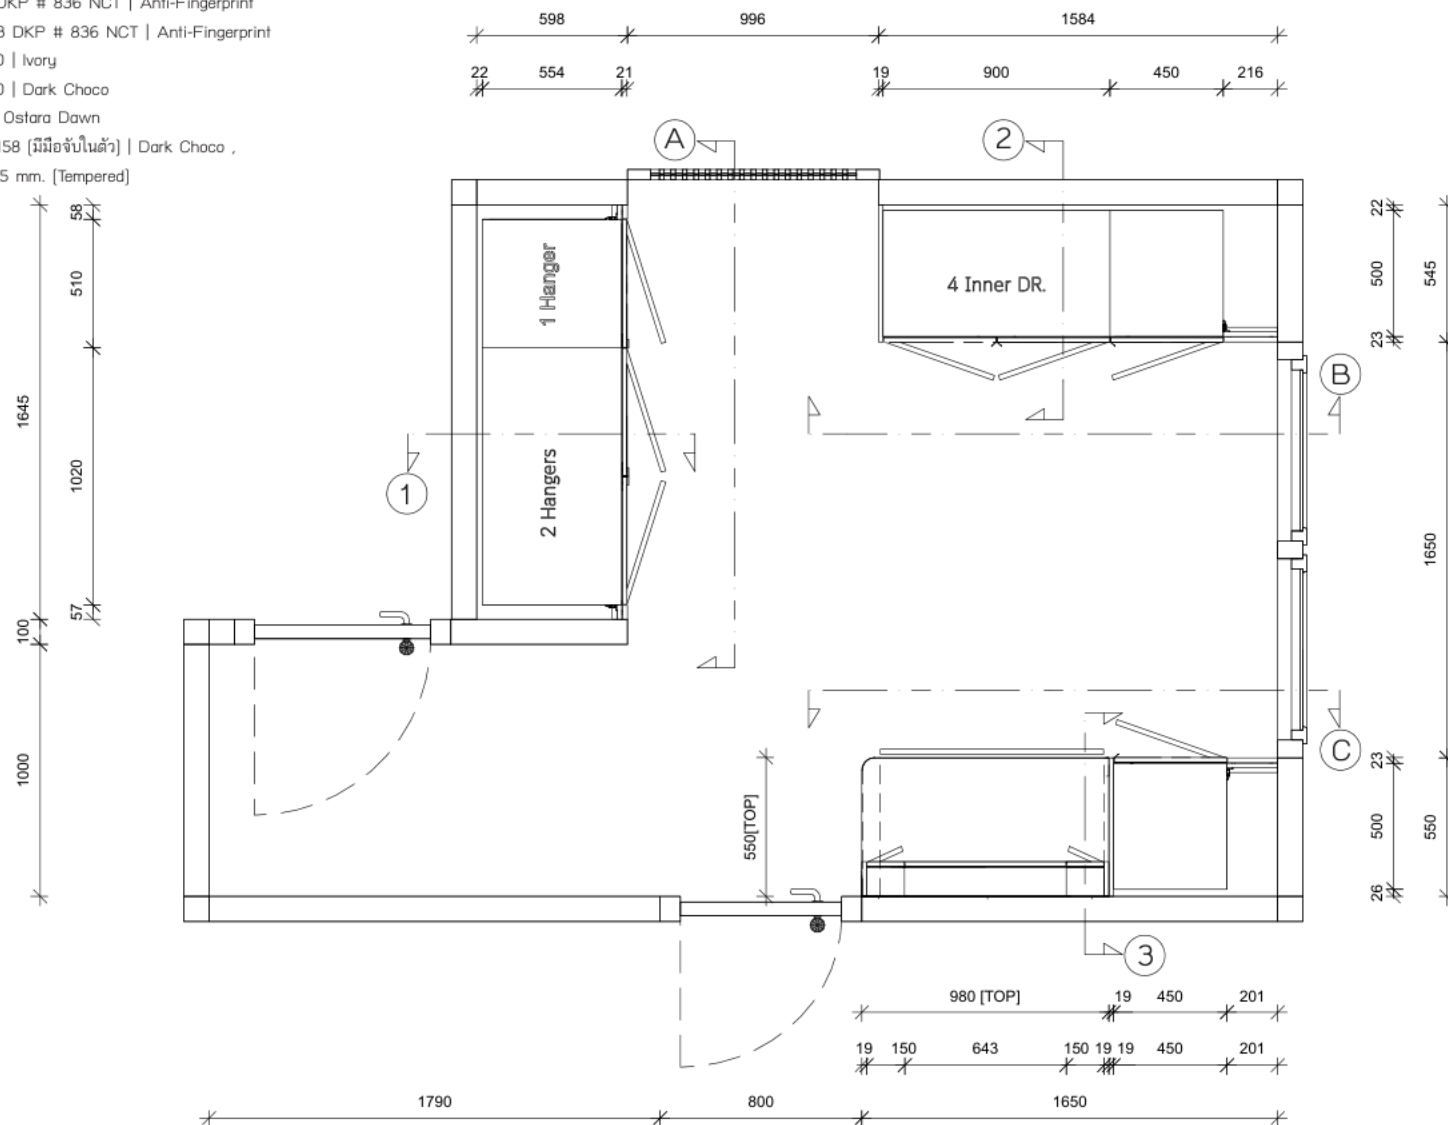

Dkbb

157 Praditmanutham Road
 Bangkapi Bangkok 10240
 TEL: 0-2515-1162 FAX: 0-2515-1161
 WWW.decorchoice.co.th

Client : Ari789

Address :

Province :-

Phone :

Design : Master Walk-In Closet - 4B

Series : Elegance

Drawn by : บริษัท สุนทรจามร

Email :


View : Plan

Scale : 1:30


Date : 10/9/2569

Page : 01

INSIDE: MDF HMR E1 V313 DKP # PP 022 WM | American Walnut
 OUTSIDE: MDF HMR E1 V313 DKP # 836 NCT | Anti-Fingerprint
 FRONTAGE: MDF HMR E1 V313 DKP # 836 NCT | Anti-Fingerprint
 HANDLE: Aluminum DKP #5230 | Ivory
 HANDLE: Aluminum DKP #5230 | Dark Choco
 TOP: Quartz Vadara G1 #V743 | Ostara Dawn
 FRONTAGE: Aluminum DKP #5158 (มีมือจับในตัว) | Dark Choco ,
 กระจกใส TYK | Euro Bronze 5 mm. (Tempered)

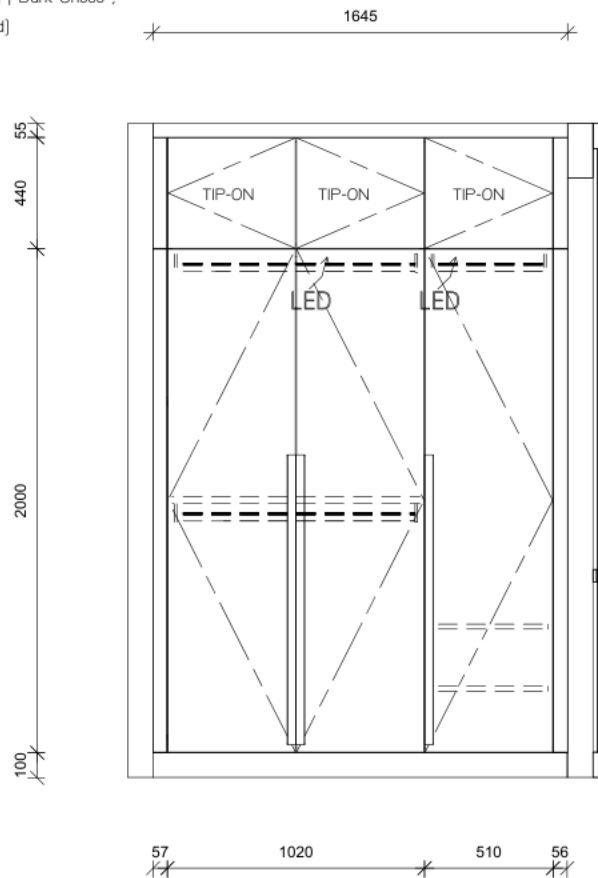

ELEVATION A

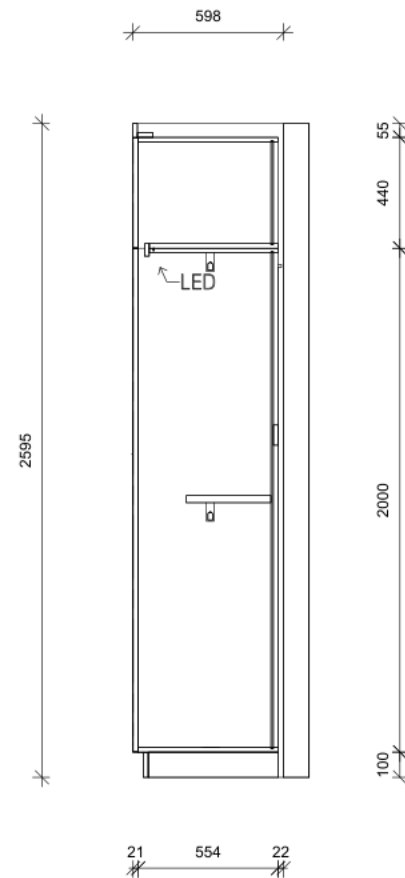


SECTION 1

Dkbb


157 Praditmanutham Road
 Bangkapi Bangkok 10240
 TEL:0-2515-1162 FAX:0-2515-1161
 WWW.decorchoice.co.th

Client : Ari789	Design : Master Walk-In Closet - 4B	View : Elevation A , Section 1
Address :	Series : Elegance	Scale : 1:30
Province :-	Drawn by : บริษัท สุนทรจามร	Date : 10/9/2569
Phone :	Email :	Page : 02

INSIDE: MDF HMR E1 V313 DKP # PP 022 WM | American Walnut
 OUTSIDE: MDF HMR E1 V313 DKP # 836 NCT | Anti-Fingerprint
 FRONTAGE: MDF HMR E1 V313 DKP # 836 NCT | Anti-Fingerprint
 HANDLE: Aluminum DKP #5230 | Ivory
 HANDLE: Aluminum DKP #5230 | Dark Choco
 TOP: Quartz Vadara G1 #V743 | Ostara Dawn
 FRONTAGE: Aluminum DKP #5158 (มีมือจับในตัว) | Dark Choco ,
 กระจกเงา ใส TYK | Euro Bronze 5 mm. (Tempered)

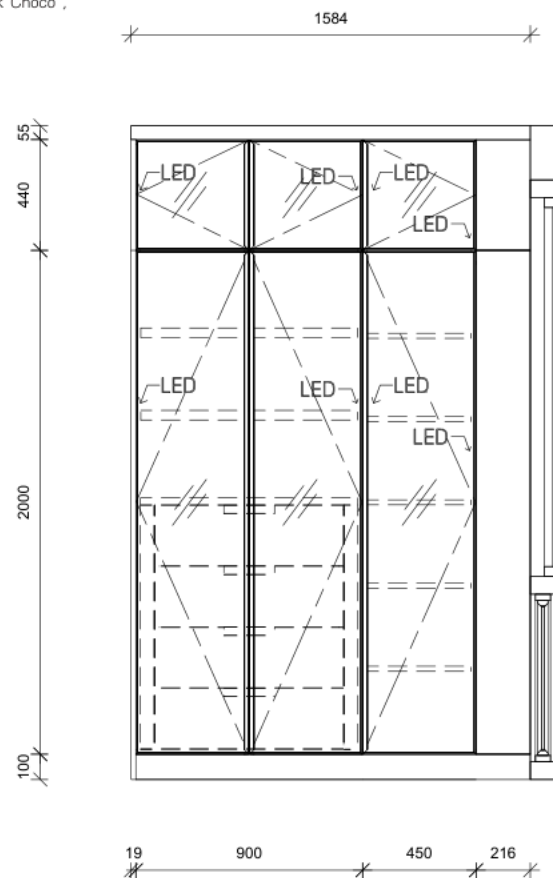

ELEVATION B

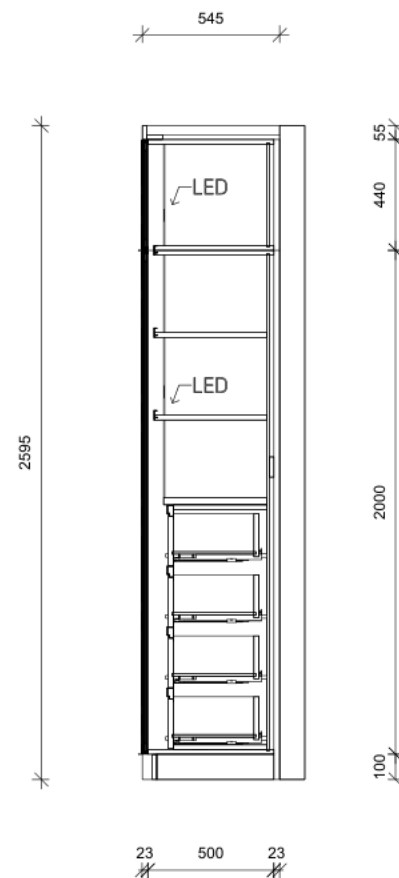


SECTION 2

Dkbb


157 Praditmanutham Road
 Bangkapi Bangkok 10240
 TEL:0-2515-1162 FAX:0-2515-1161
 WWW.decorchoice.co.th

Client : Ari789	Design : Master Walk-In Closet - 4B	View : Elevation B , Section 2
Address :	Series : Elegance	Scale : 1:30
Province :-	Drawn by : บริษัท สุนทรจามร	Date : 10/9/2569
Phone :	Email :	Page : 03

INSIDE: MDF HMR E1 V313 DKP # PP 022 WM | American Walnut
 OUTSIDE: MDF HMR E1 V313 DKP # 836 NCT | Anti-Fingerprint
 FRONTAGE: MDF HMR E1 V313 DKP # 836 NCT | Anti-Fingerprint
 HANDLE: Aluminum DKP #5230 | Ivory
 HANDLE: Aluminum DKP #5230 | Dark Choco
 TOP: Quartz Vadara G1 #V743 | Ostara Dawn
 FRONTAGE: Aluminum DKP #5158 (มีมือจับในตัว) | Dark Choco ,
 กระจกเงา ใส TYK | Euro Bronze 5 mm. (Tempered)

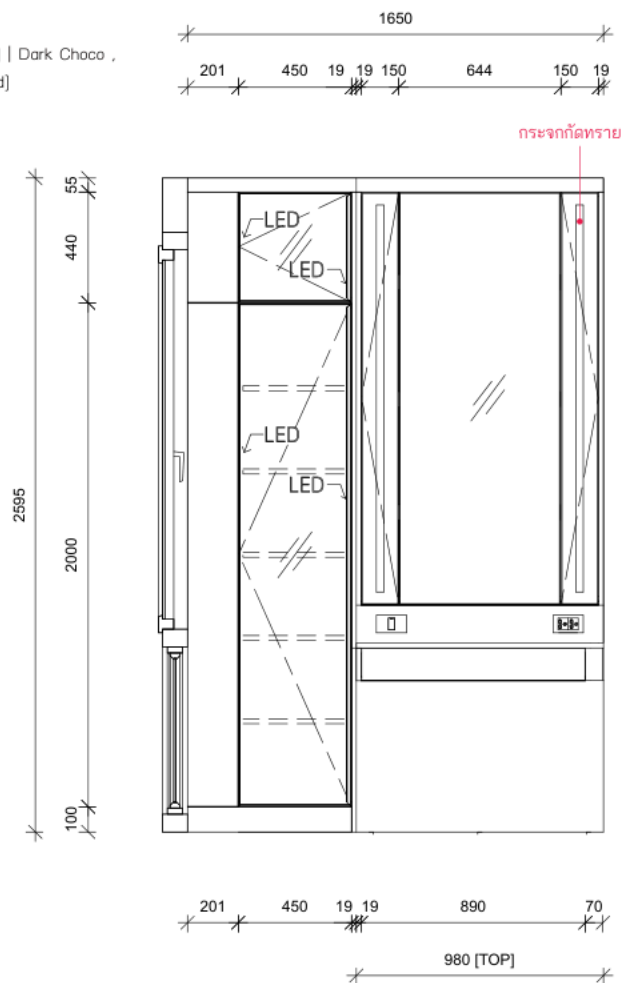

ELEVATION C

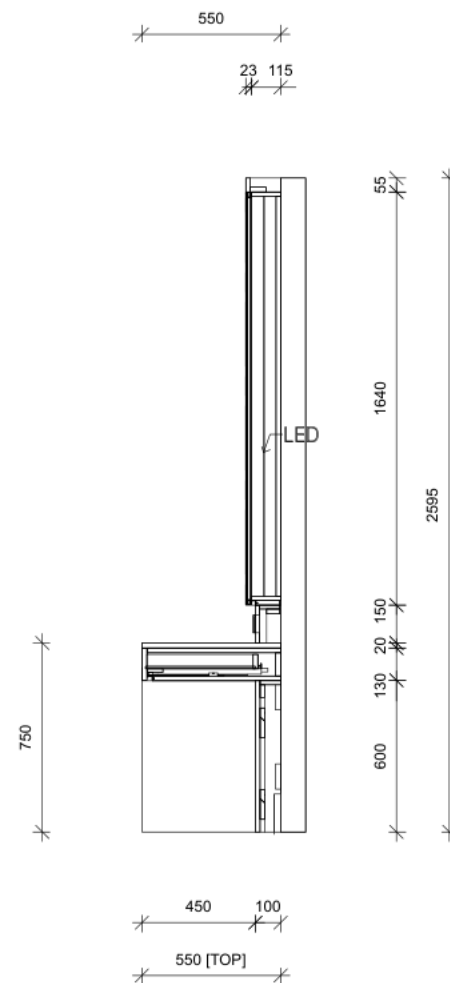

SECTION 3

Dkbb

157 Praditmanutham Road
 Bangkapi Bangkok 10240
 TEL:0-2515-1162 FAX:0-2515-1161
 WWW.decorchoice.co.th

Client : Ari789

Address :

Province :-

Phone :

Design : Master Walk-In Closet - 4B

Series : Elegance

Drawn by : บริษัท สุนทรจามร


Email :

View : Elevation C , Section 3

Scale : 1:30

Date : 10/9/2569

Page : 04

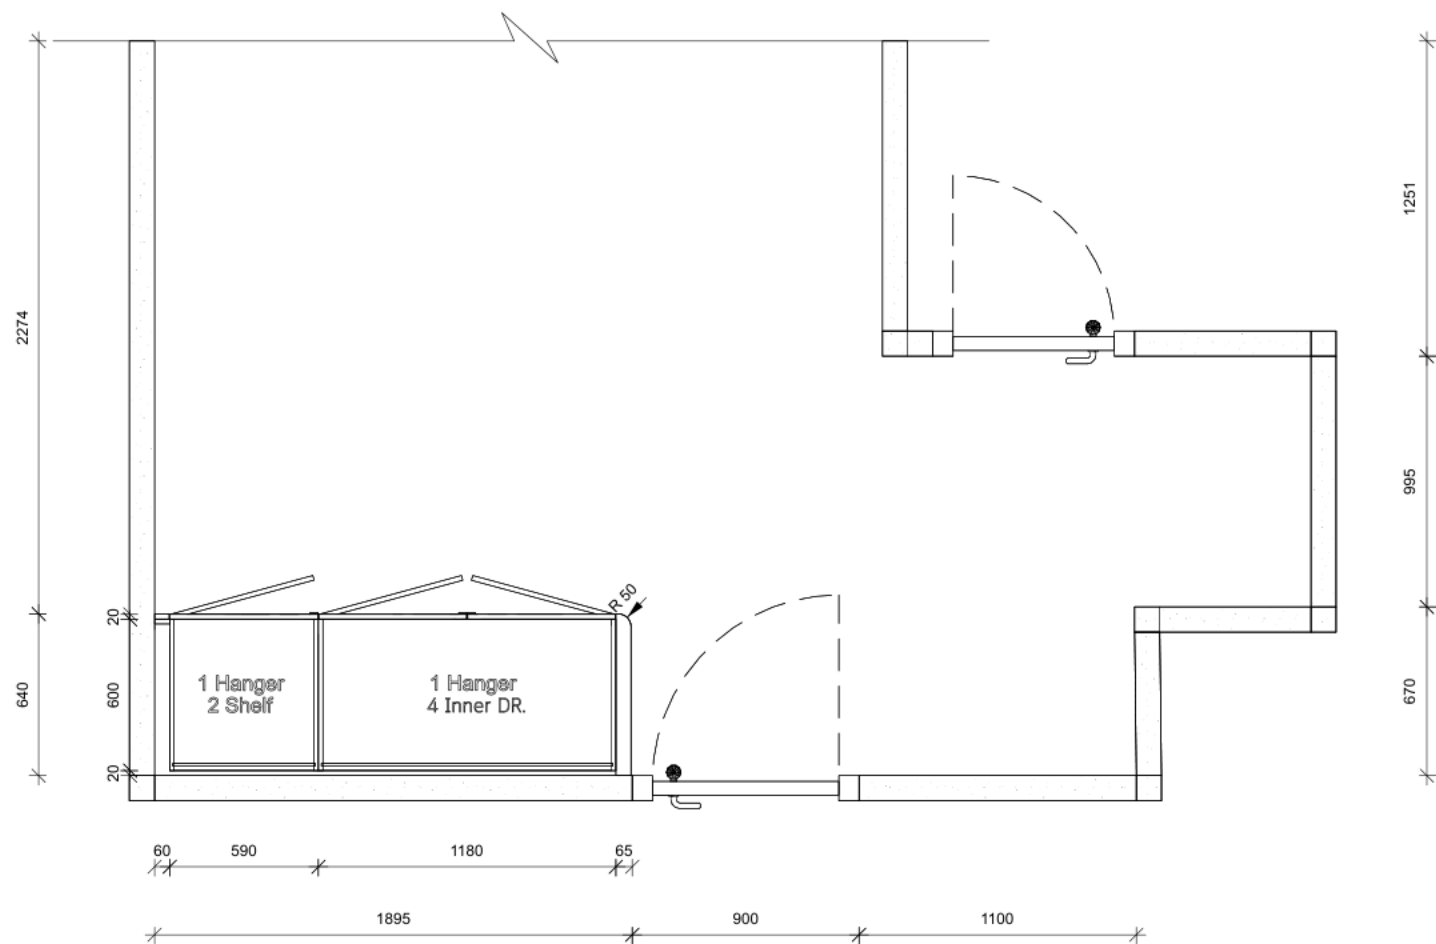


Dkbb

157 Praditmanutham Road
Bangkapi Bangkok 10240
TEL: 0-2515-1162 FAX: 0-2515-1161
WWW.decorchoice.co.th

Client : ARI789	Design : Bedroom 2 - Walk in 4B	View : Plan
Address :	Series : Elegance	Scale : 1:30
Province :-	Drawn by : Sunisa	Date : 20/6/2569
Phone :	Email :	Page : 01

INSIDE: MDF HMR E1 V313 DKP # PP 022 WM | American Walnut
 OUTSIDE: MDF HMR E1 V313 DKP # 836 NCT | Anti-Fingerprint
 FRONTAGE: MDF HMR E1 V313 DKP # 836 NCT | Anti-Fingerprint
 HANDLE: Aluminum DKP #5230 | Ivory
 HANDLE: Aluminum DKP #5230 | Dark Choco

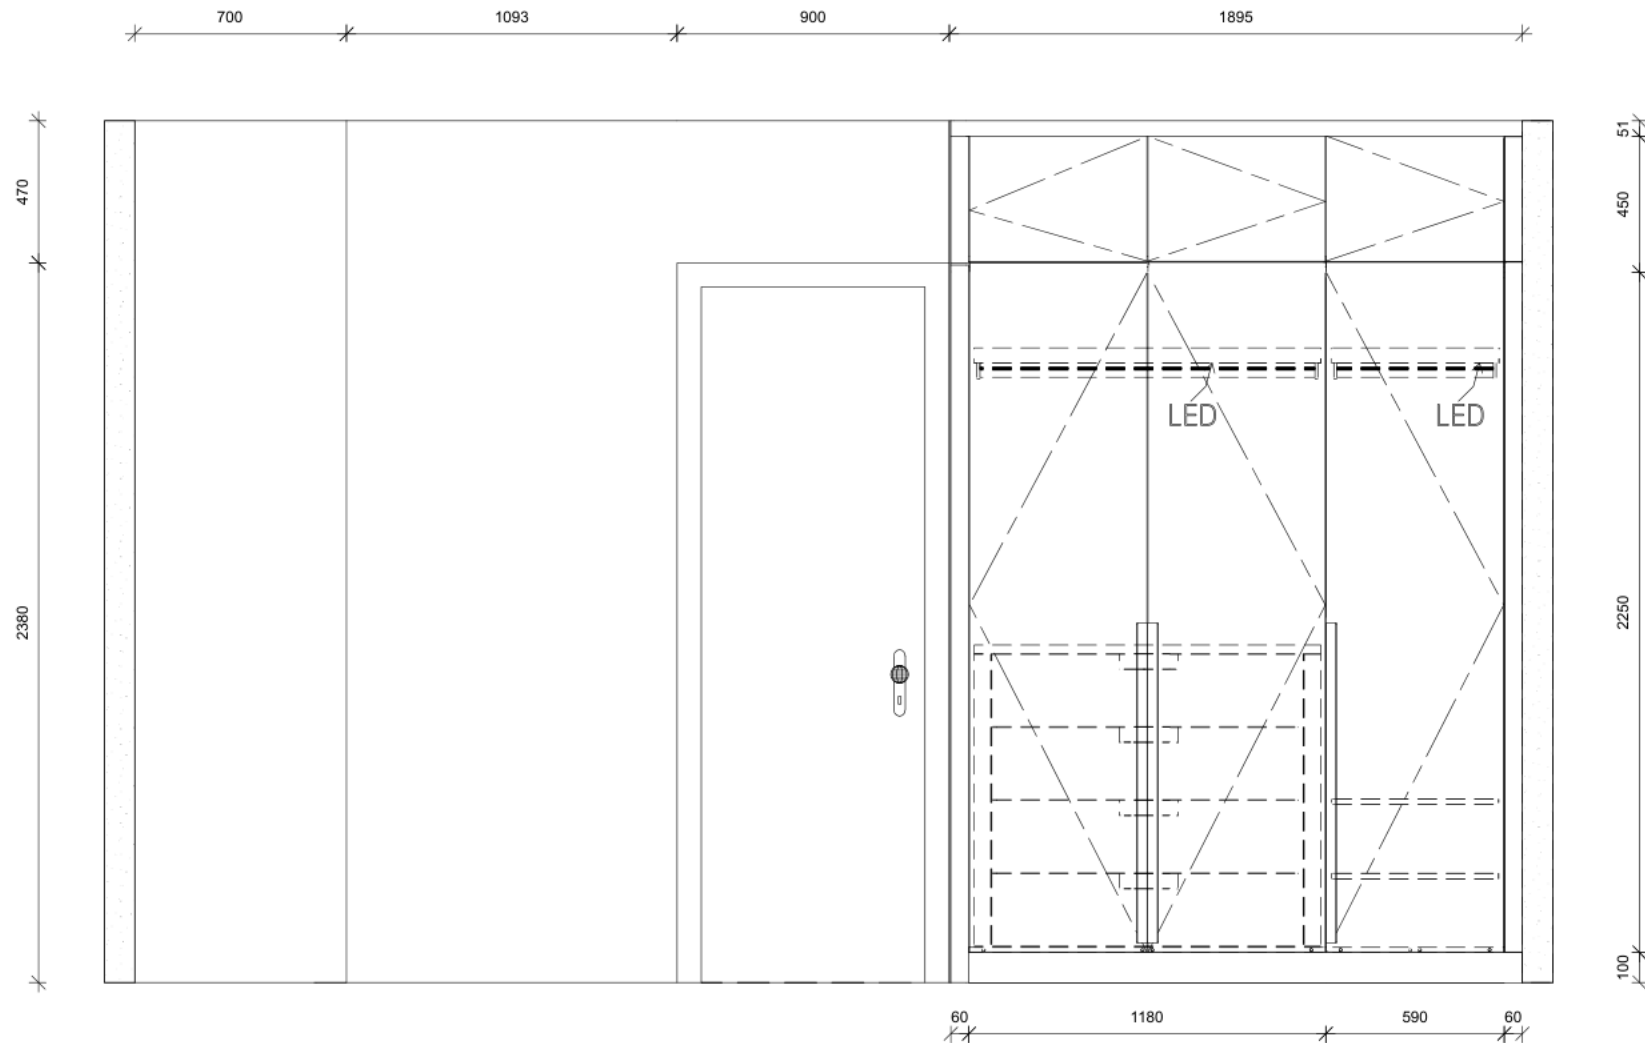

Dkbb

157 Praditmanutham Road
 Bangkapi Bangkok 10240
 TEL:0-2515-1162 FAX:0-2515-1161
 WWW.decorchoice.co.th

Client : ARI789	Design : Bedroom 2 - Walk in 4B	View : Elevation A
Address :	Series : Elegance	Scale : 1:25
Province :-	Drawn by : Sunisa	Date : 20/6/2569
Phone :	Email :	Page : 02


INSIDE: MDF HMR E1 V313 DKP # PP 022 WM | American Walnut
 OUTSIDE: MDF HMR E1 V313 DKP # 836 NCT | Anti-Fingerprint
 FRONTAGE: MDF HMR E1 V313 DKP # 836 NCT | Anti-Fingerprint
 HANDLE: Aluminum DKP #5230 | Ivory
 HANDLE: Aluminum DKP #5230 | Dark Choco



Dkbb

157 Praditmanutham Road
 Bangkapi Bangkok 10240
 TEL:0-2515-1162 FAX:0-2515-1161
 WWW.decorchoice.co.th

Client : ARI789	Design : Bedroom 2 - Walk in 4B	View : Section 1
Address :	Series : Elegance	Scale : 1:25
Province :-	Drawn by : Sunisa	Date : 20/6/2569
Phone :	Email :	Page : 03

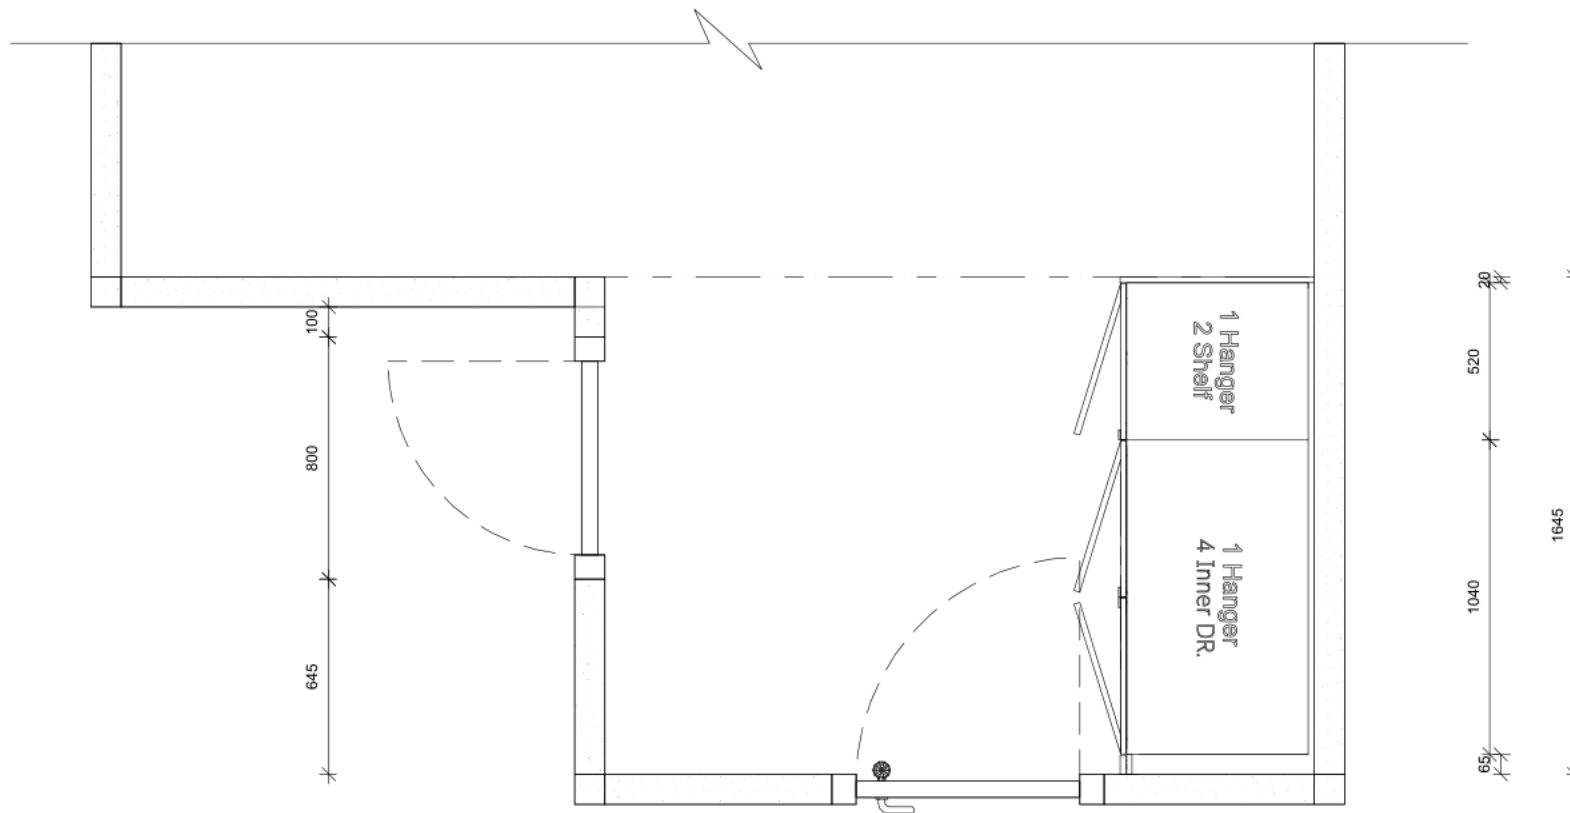

INSIDE: MDF HMR E1 V313 DKP # PP 022 WM | American Walnut

OUTSIDE: MDF HMR E1 V313 DKP # 836 NCT | Anti-Fingerprint

FRONTAGE: MDF HMR E1 V313 DKP # 836 NCT | Anti-Fingerprint


HANDLE: Aluminum DKP #5230 | Ivory

HANDLE: Aluminum DKP #5230 | Dark Choco

TOP: Vadara #G1 V743 | Ostara Dawn

FRONTAGE: Aluminum MEBEL (มีมือจับในตัว) | Dark Choco , กระจกใส TYK

| Euro Bronze 5 mm.

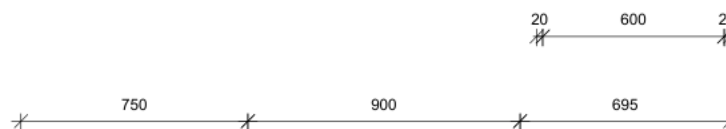

Dkbb

157 Praditmanutham Road
Bangkapi Bangkok 10240
TEL:0-2515-1162 FAX:0-2515-1161
WWW.decorchoice.co.th

Client : ARI789

Address :

Province :-

Phone :

Design : Bedroom 1 - Walk in 4B

Series : Elegance

Drawn by : Sunisa


Email :

View : Plan

Scale :1:25

Date : 11/6/2569

Page : 01

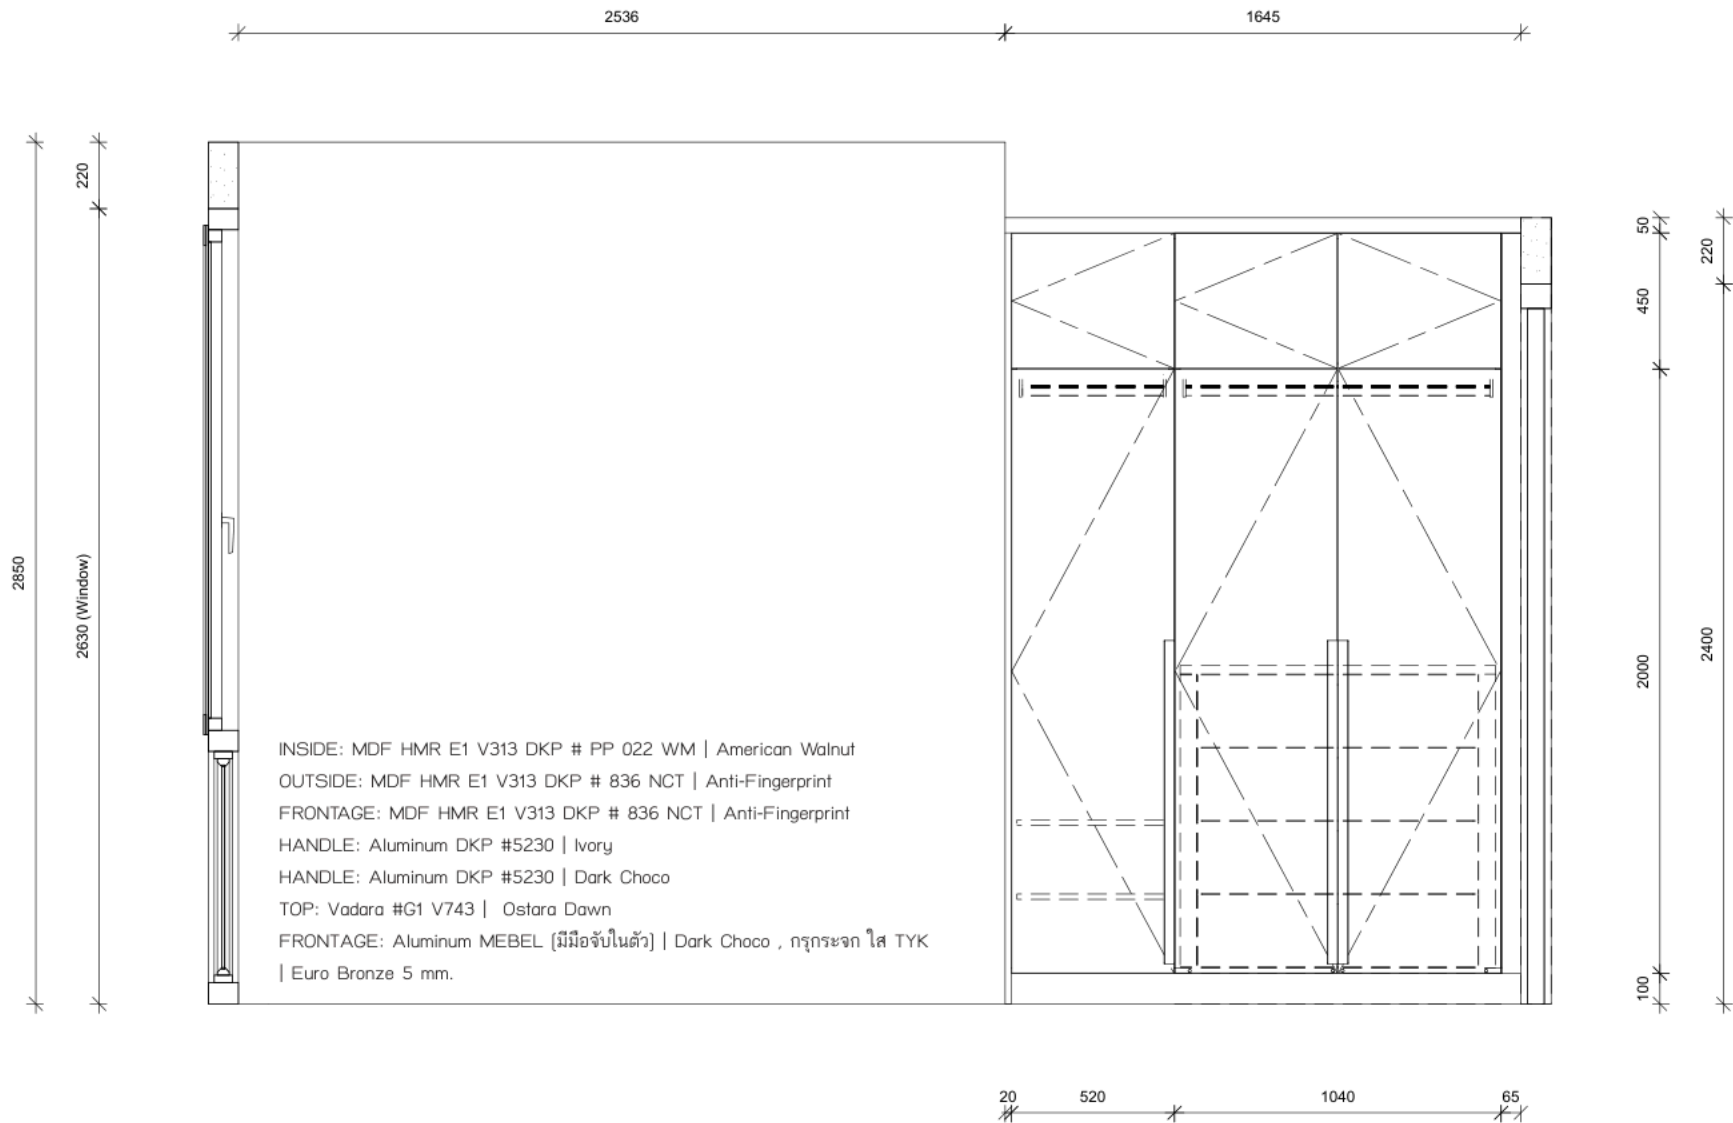

Dkbb

157 Praditmanutham Road
 Bangkapi Bangkok 10240
 TEL:0-2515-1162 FAX:0-2515-1161
 WWW.decorchoice.co.th

Client : ARI789

Address :

Province :-

Phone :

Design : Bedroom 1 - Walk in 4B

Series : Elegance

Drawn by : Sunisa

Email :


View : Elevation A

Scale : 1:30

Date : 11/6/2569

Page : 02

INSIDE: MDF HMR E1 V313 DKP # PP 022 WM | American Walnut
 OUTSIDE: MDF HMR E1 V313 DKP # 836 NCT | Anti-Fingerprint
 FRONTAGE: MDF HMR E1 V313 DKP # 836 NCT | Anti-Fingerprint
 HANDLE: Aluminum DKP #5230 | Ivory
 HANDLE: Aluminum DKP #5230 | Dark Choco
 TOP: Vadara #G1 V743 | Ostara Dawn
 FRONTAGE: Aluminum MEBEL [มีมือจับในตัว] | Dark Choco
 ,กรุกระจกใส TYK | Euro Bronze 5 mm.

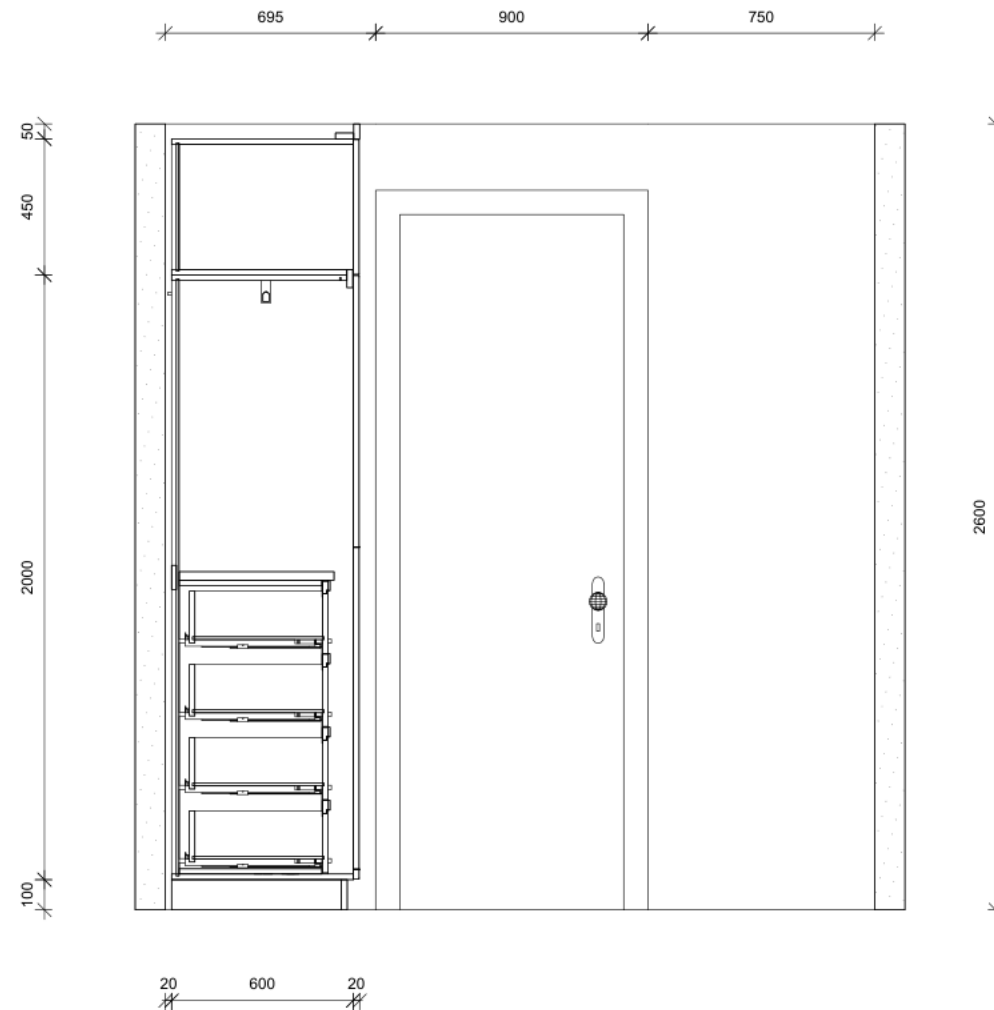

Dkbb

157 Praditmanutham Road
 Bangkapi Bangkok 10240
 TEL:0-2515-1162 FAX:0-2515-1161
 WWW.decorchoice.co.th

Client : ARI789	Design : Bedroom 1 - Walk in 4B	View : Section 1
Address :	Series : Elegance	Scale : 1:25
Province :-	Drawn by : Sunisa	Date : 11/6/2569
Phone :	Email :	Page : 03