

INSIDE: MDF HMR E1 V313 DKP # PP 022 WM | American Walnut

OUTSIDE: MDF HMR E1 V313 DKP # 836 NCT | Anti-Fingerprint


FRONTAGE: MDF HMR E1 V313 DKP # 836 NCT | Anti-Fingerprint

FRONTAGE: Aluminum DKP #5158 [มีมือจับในตัว]

| Dark Choco , กรูกระจุก สี TYK | Euro Bronze 5 mm.

HANDLE: Aluminum DKP #5230 | Ivory

HANDLE [DW]: Aluminum DKP #5230 | Dark Choco

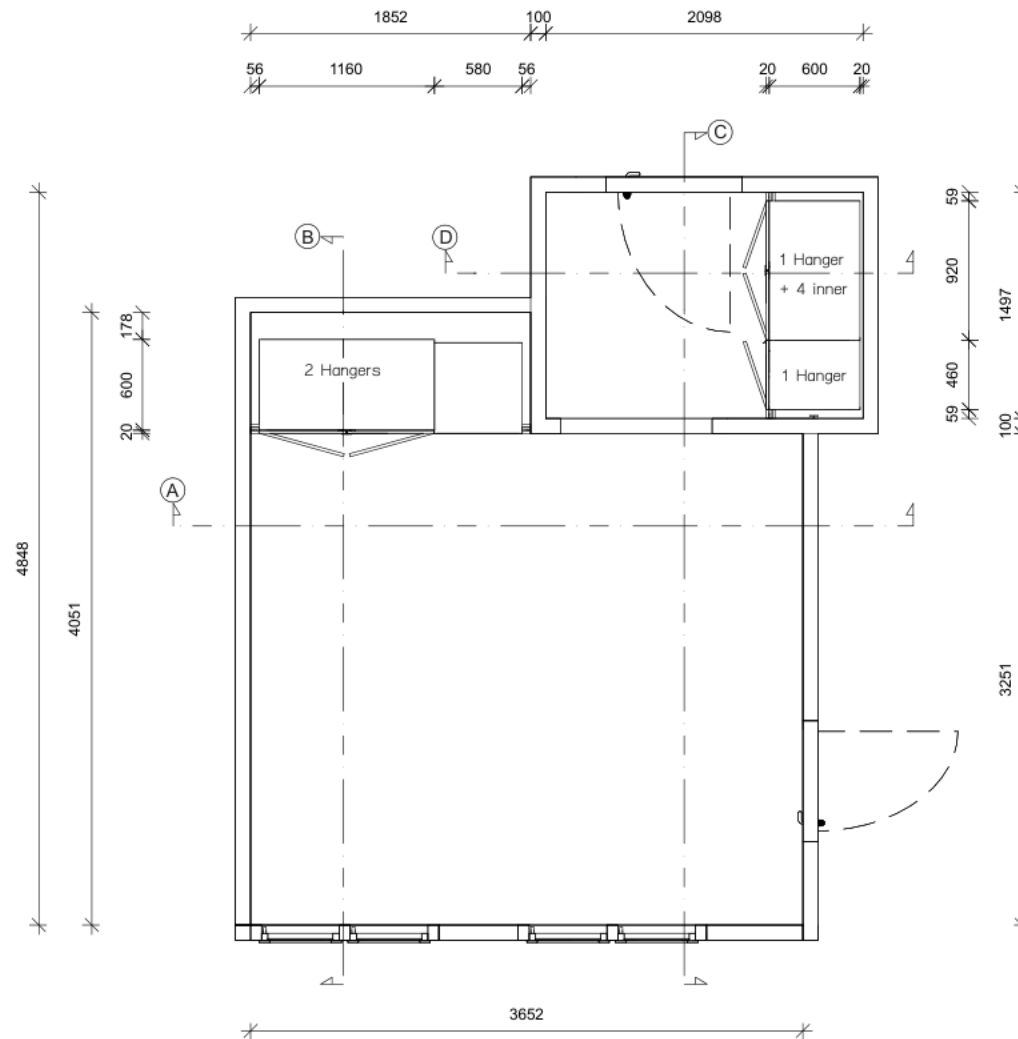

amh
2-9-69

Dkbb

157 Praditmanutham Road
Bangkapi Bangkok 10240
TEL:0-2515-1162 FAX:0-2515-1161
WWW.decorchoice.co.th

Client : Ari789

Address :

Province :

Phone :

Design : 5A WALK-IN CLOSET BEDROOM 1

Series : Elegance

Drawn by :Nirarat

Email :


View : Plan

Scale : 1:50

Date : 31/8/2569

Page : 01

INSIDE: MDF HMR E1 V313 DKP # PP 022 WM | American Walnut
OUTSIDE: MDF HMR E1 V313 DKP # 836 NCT | Anti-Fingerprint
FRONTAGE: MDF HMR E1 V313 DKP # 836 NCT | Anti-Fingerprint
FRONTAGE: Aluminum DKP #5158 [มีมือจับในตัว]
| Dark Choco , กรูกระจุก ใส TYK | Euro Bronze 5 mm.
HANDLE: Aluminum DKP #5230 | Ivory
HANDLE [DW]: Aluminum DKP #5230 | Dark Choco

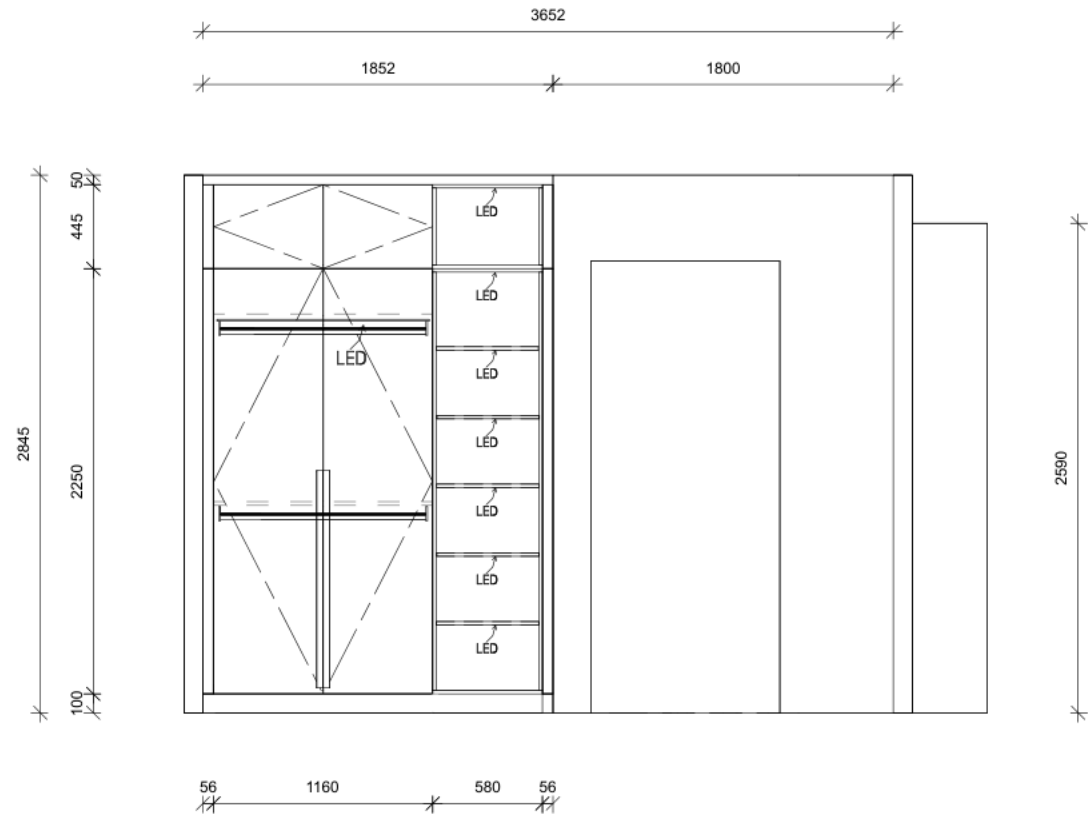

amh
2-9-69

Dkbb

157 Praditmanutham Road
Bangkapi Bangkok 10240
TEL:0-2515-1162 FAX:0-2515-1161
WWW.decorchoice.co.th

Client : Ari789	Design : 5A WALK-IN CLOSET BEDROOM 1	View : Elevation A
Address :	Series : Elegance	Scale : 1:40
Province :	Drawn by :Nirarat	Date : 31/8/2569
Phone :	Email :	Page : 02

INSIDE: MDF HMR E1 V313 DKP # PP 022 WM | American Walnut
OUTSIDE: MDF HMR E1 V313 DKP # 836 NCT | Anti-Fingerprint
FRONTAGE: MDF HMR E1 V313 DKP # 836 NCT | Anti-Fingerprint
FRONTAGE: Aluminum DKP #5158 [มีมือจับในตัว]
| Dark Choco , กรอบกระจก ใส TYK | Euro Bronze 5 mm.
HANDLE: Aluminum DKP #5230 | Ivory
HANDLE [DW]: Aluminum DKP #5230 | Dark Choco




amoh
2-9-69

Dkbb

157 Praditmanutham Road
Bangkapi Bangkok 10240
TEL:0-2515-1162 FAX:0-2515-1161
WWW.decorchoice.co.th

Client : Ari789	Design : 5A WALK-IN CLOSET BEDROOM 1	View : Section B
Address :	Series : Elegance	Scale : 1:40
Province :	Drawn by :Nirarat	Date : 31/8/2569
Phone :	Email :	Page : 03

INSIDE: MDF HMR E1 V313 DKP # PP 022 WM | American Walnut
OUTSIDE: MDF HMR E1 V313 DKP # 836 NCT | Anti-Fingerprint
FRONTAGE: MDF HMR E1 V313 DKP # 836 NCT | Anti-Fingerprint
FRONTAGE: Aluminum DKP #5158 (มีมือจับในตัว)
| Dark Choco , กระจกจาก ไทย TYK | Euro Bronze 5 mm.
HANDLE: Aluminum DKP #5230 | Ivory
HANDLE [DW]: Aluminum DKP #5230 | Dark Choco

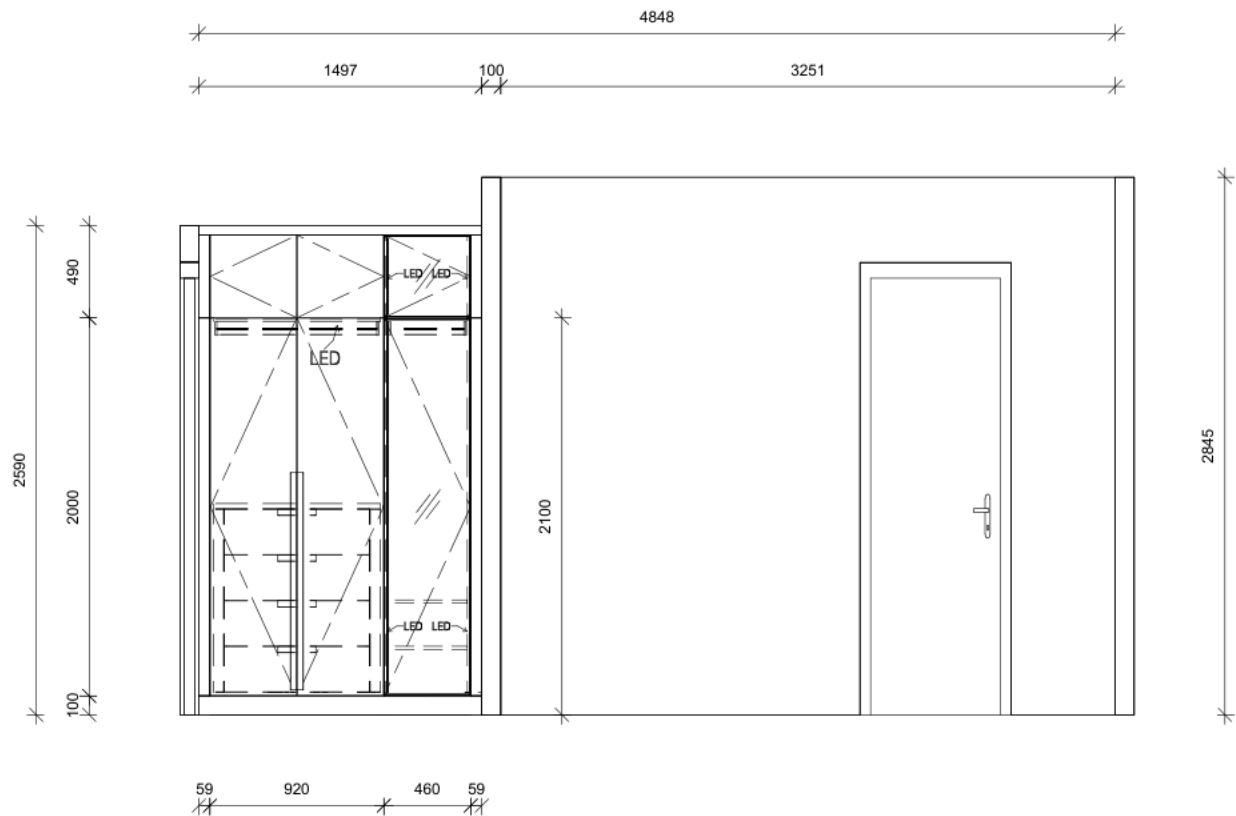

mmk
2-9-69

Dkbb

157 Praditmanutham Road
Bangkapi Bangkok 10240
TEL:0-2515-1162 FAX:0-2515-1161
WWW.decorchoice.co.th

Client : Ari789	Design : 5A WALK-IN CLOSET BEDROOM 1	View : Elevation C
Address :	Series : Elegance	Scale : 1:40
Province :	Drawn by :Nirarat	Date : 31/8/2569
Phone :	Email :	Page : 04

INSIDE: MDF HMR E1 V313 DKP # PP 022 WM | American Walnut

OUTSIDE: MDF HMR E1 V313 DKP # 836 NCT | Anti-Fingerprint


FRONTAGE: MDF HMR E1 V313 DKP # 836 NCT | Anti-Fingerprint

FRONTAGE: Aluminum DKP #5158 (มีมือจับในตัว)

| Dark Choco , กระจกใส TYK | Euro Bronze 5 mm.

HANDLE: Aluminum DKP #5230 | Ivory

HANDLE [DW]: Aluminum DKP #5230 | Dark Choco

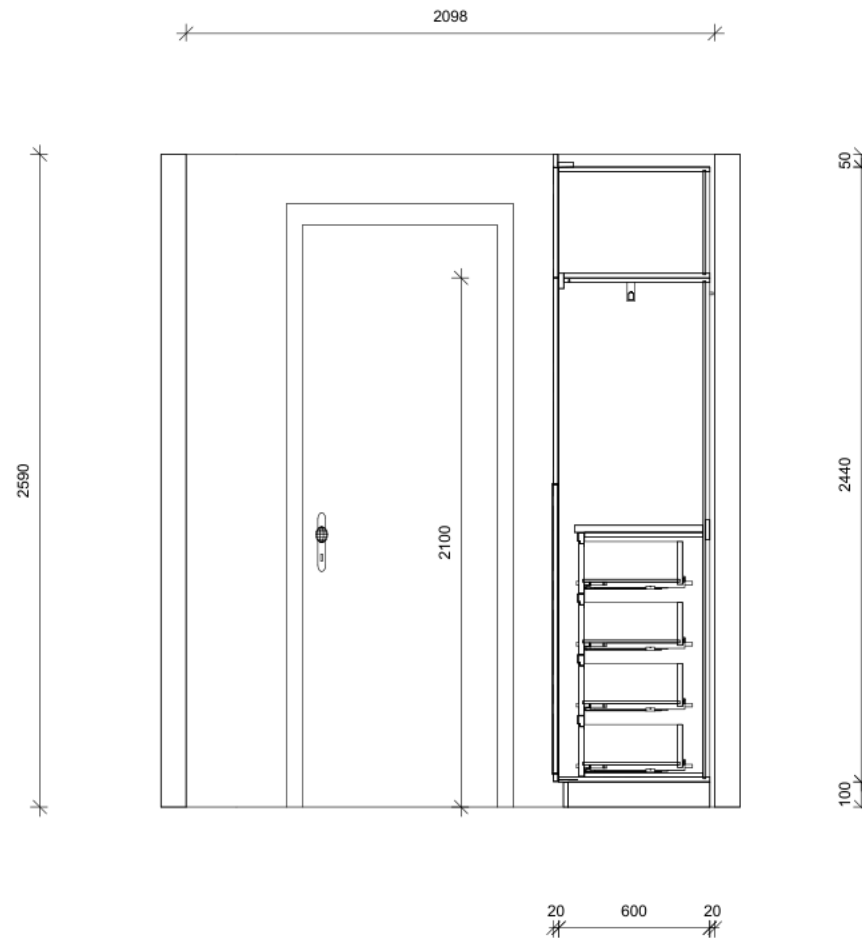

Handwritten signature
2-9-69

Dkbb

157 Praditmanutham Road
Bangkapi Bangkok 10240
TEL:0-2515-1162 FAX:0-2515-1161
WWW.decorchoice.co.th

Client : Ari789	Design : 5A WALK-IN CLOSET BEDROOM 1	View : Section D
Address :	Series : Elegance	Scale : 1:30
Province :	Drawn by :Nirarat	Date : 31/8/2569
Phone :	Email :	Page : 05