


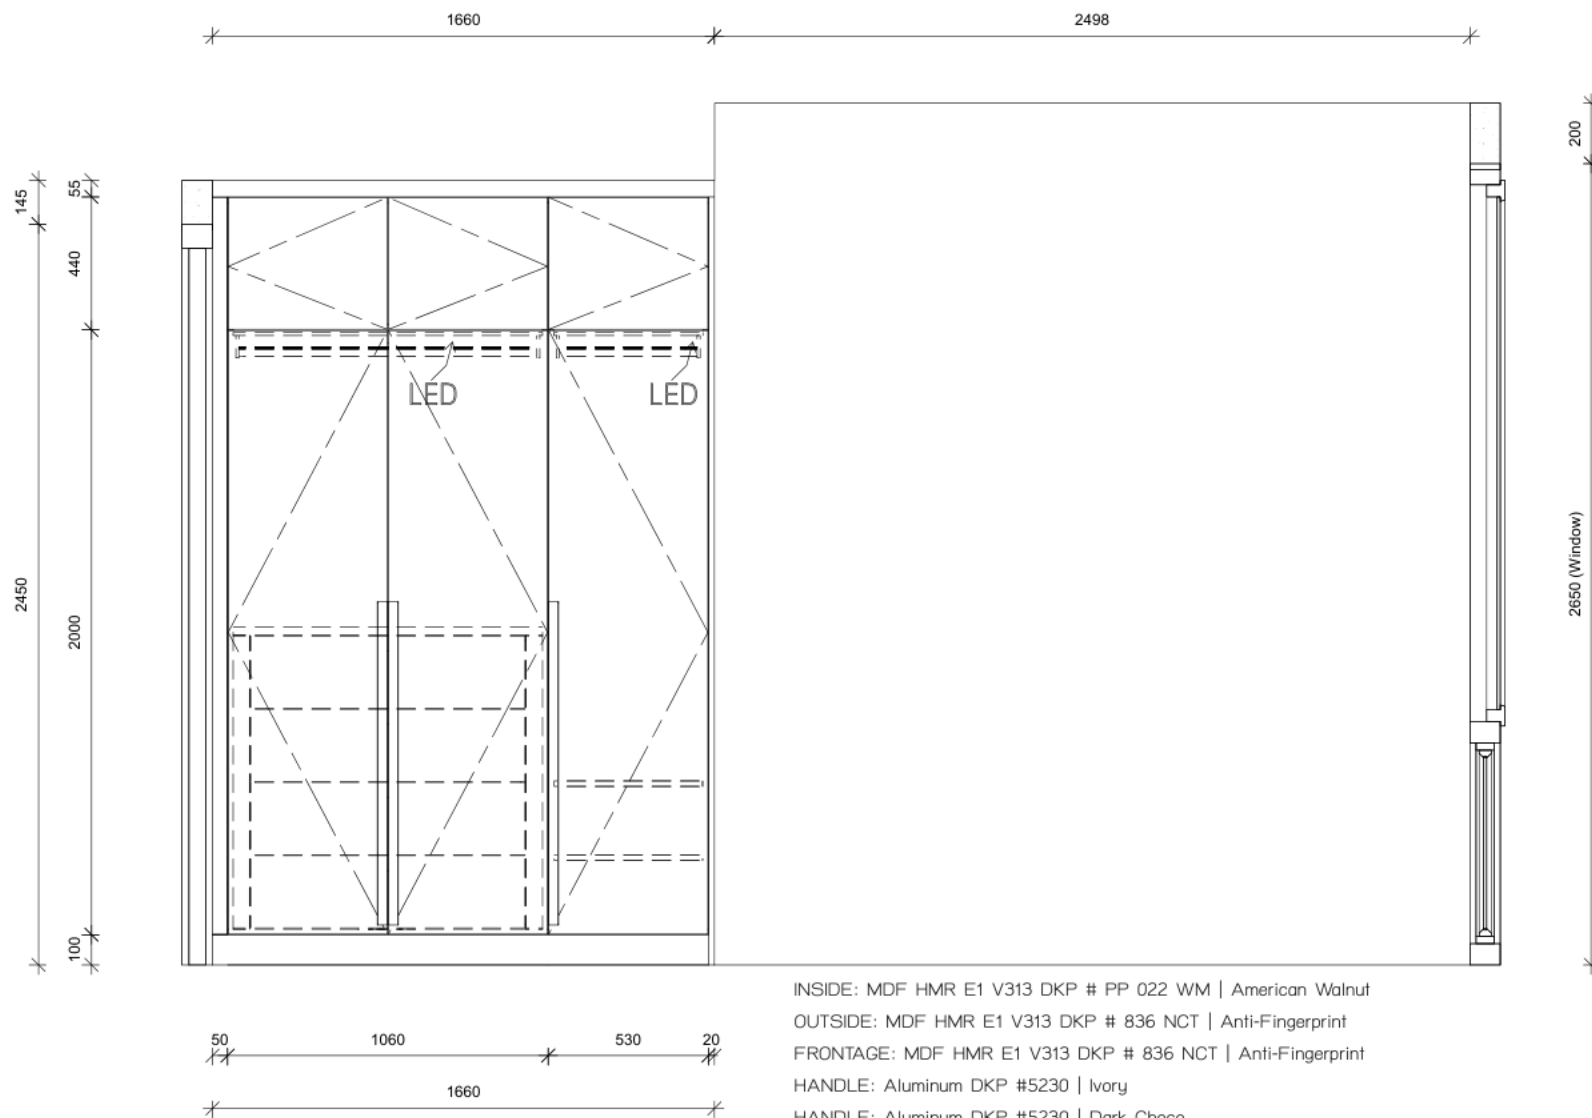




Dkbb

157 Praditmanutham Road
Bangkapi Bangkok 10240
TEL: 0-2515-1162 FAX: 0-2515-1161
WWW.decorchoice.co.th

Client : ARI789	Design : Bedroom 2 - Walk in 4A	View : Elevation A
Address :	Series : Elegance	Scale : 1:25
Province :-	Drawn by : Sunisa	Date : 11/6/2569
Phone :	Email :	Page : 02

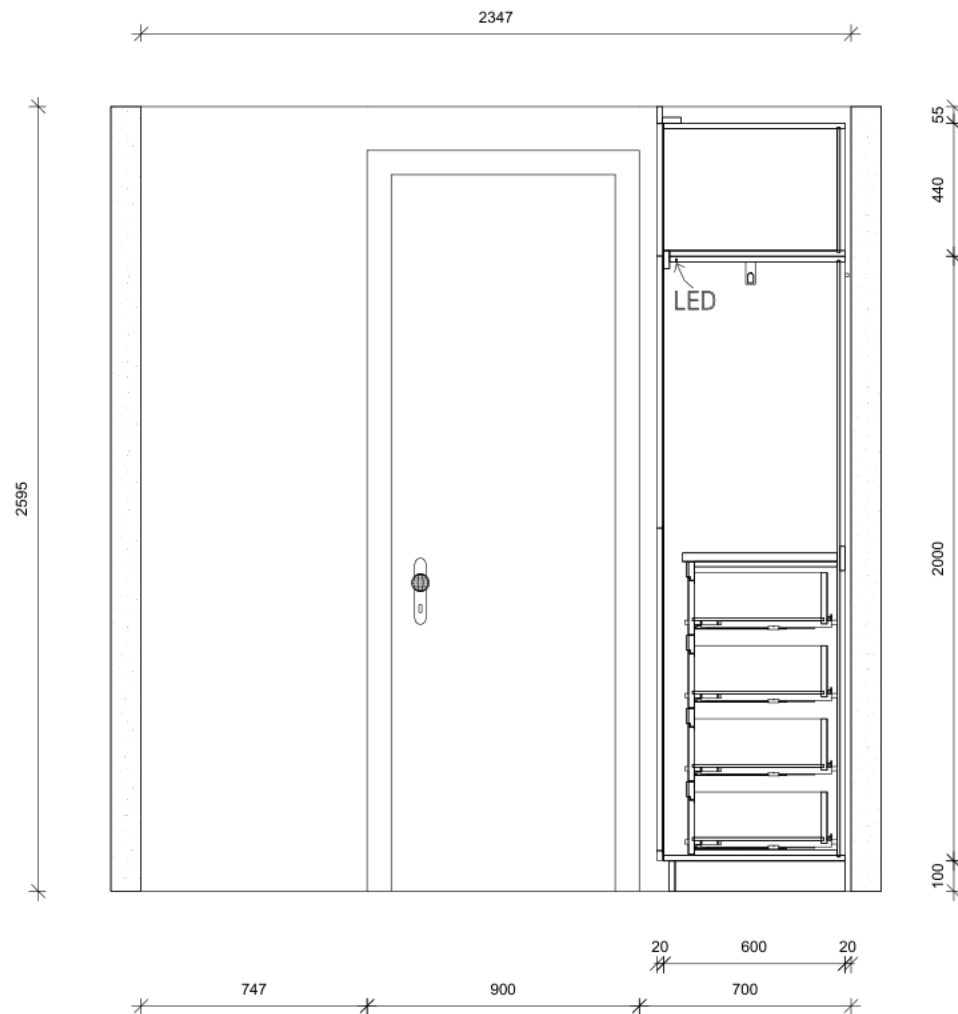

INSIDE: MDF HMR E1 V313 DKP # PP 022 WM | American Walnut
 OUTSIDE: MDF HMR E1 V313 DKP # 836 NCT | Anti-Fingerprint
 FRONTAGE: MDF HMR E1 V313 DKP # 836 NCT | Anti-Fingerprint
 HANDLE: Aluminum DKP #5230 | Ivory
 HANDLE: Aluminum DKP #5230 | Dark Choco

Dkbb

157 Praditmanutham Road
 Bangkapi Bangkok 10240
 TEL:0-2515-1162 FAX:0-2515-1161
 WWW.decorchoice.co.th

Client : ARI789	Design : Bedroom 2 - Walk in 4A	View : Section 1
Address :	Series : Elegance	Scale : 1:30
Province :-	Drawn by : Sunisa	Date : 11/6/2569
Phone :	Email :	Page : 03