










INSIDE: MDF HMR E1 V313 DKP # PP 022 WM | American Walnut
 OUTSIDE: MDF HMR E1 V313 DKP # 836 NCT | Anti-Fingerprint
 FRONTAGE: MDF HMR E1 V313 DKP # 836 NCT | Anti-Fingerprint
 HANDLE: Aluminum DKP #5230 | Ivory
 HANDLE: Aluminum DKP #5230 | Dark Choco
 TOP: Quartz Vadara G1 #V743 | Ostara Dawn
 FRONTAGE: Aluminum DKP #5158 (มีมือจับในตัว) | Dark Choco ,
 กระจกใส TYK | Euro Bronze 5 mm. (Tempered)

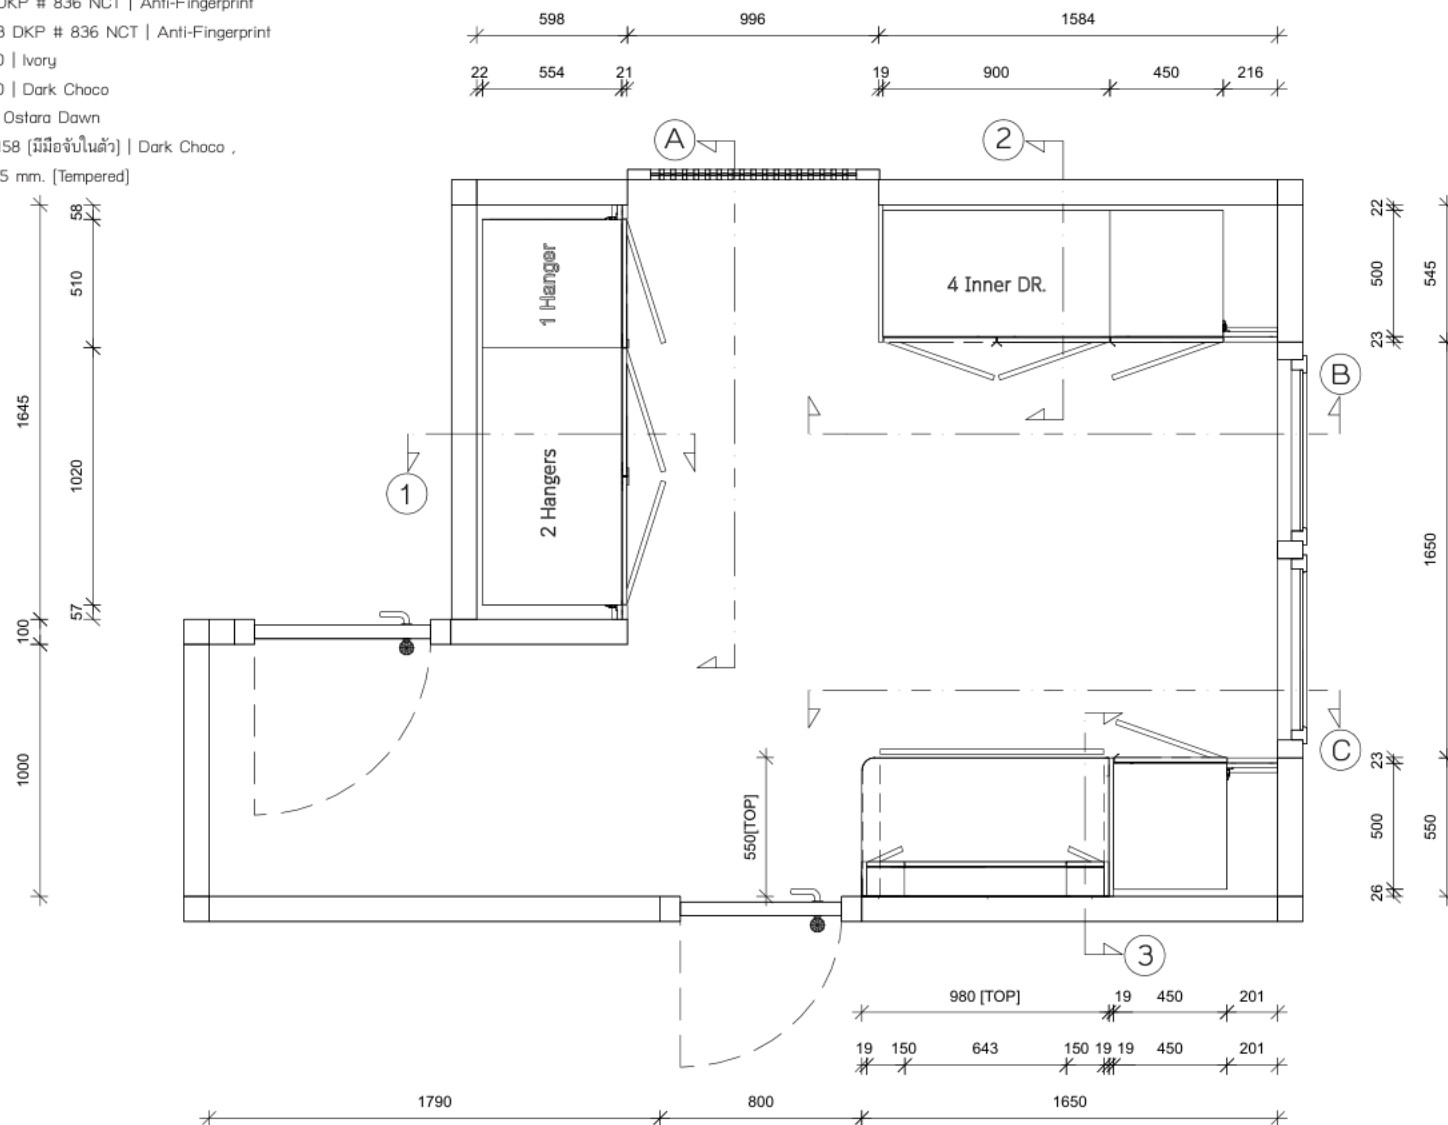

Dkbb

157 Praditmanutham Road
 Bangkapi Bangkok 10240
 TEL: 0-2515-1162 FAX: 0-2515-1161
 WWW.decorchoice.co.th

Client : Ari789

Address :

Province :-

Phone :

Design : Master Walk-In Closet - 4B

Series : Elegance

Drawn by : บริษัท สุนทรจามร

Email :


View : Plan

Scale : 1:30


Date : 10/9/2569

Page : 01

INSIDE: MDF HMR E1 V313 DKP # PP 022 WM | American Walnut
OUTSIDE: MDF HMR E1 V313 DKP # 836 NCT | Anti-Fingerprint
FRONTAGE: MDF HMR E1 V313 DKP # 836 NCT | Anti-Fingerprint
HANDLE: Aluminum DKP #5230 | Ivory
HANDLE: Aluminum DKP #5230 | Dark Choco
TOP: Quartz Vadara G1 #V743 | Ostara Dawn
FRONTAGE: Aluminum DKP #5158 (มีมือจับในตัว) | Dark Choco ,
กรุกระจกใส TYK | Euro Bronze 5 mm. (Tempered)

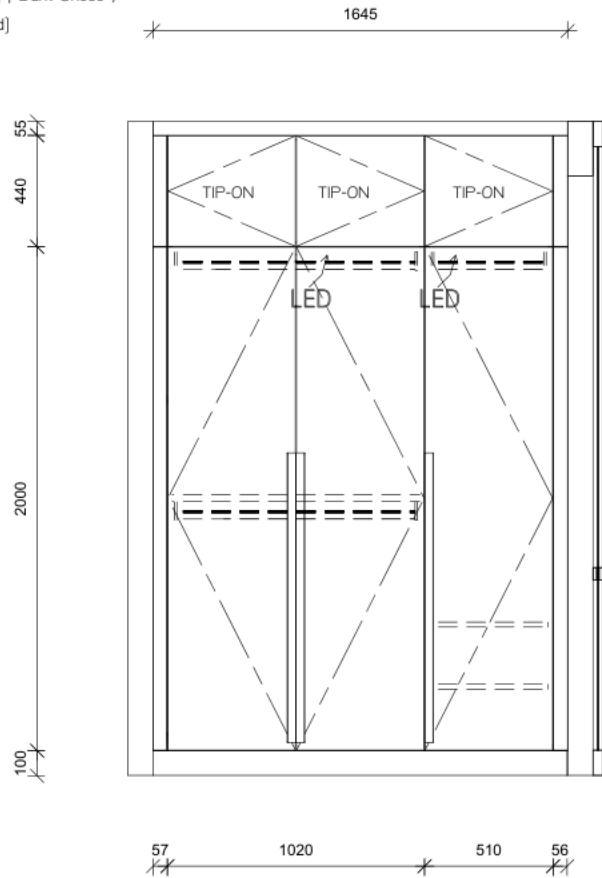

ELEVATION A

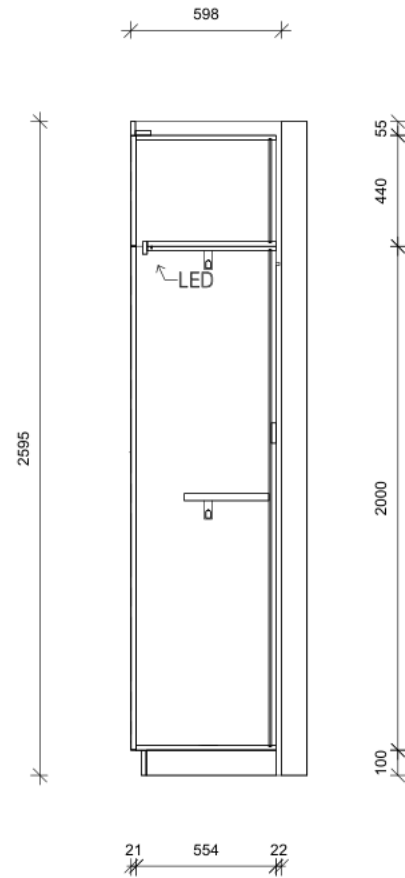

SECTION 1

Dkbb

157 Praditmanutham Road
Bangkapi Bangkok 10240
TEL:0-2515-1162 FAX:0-2515-1161
WWW.decorchoice.co.th

Client : Ari789

Address :

Province :-

Phone :

Design : Master Walk-In Closet - 4B

Series : Elegance

Drawn by : บริษัท สุนทรจามร

Email :


View : Elevation A , Section 1

Scale : 1:30


Date : 10/9/2569

Page : 02

INSIDE: MDF HMR E1 V313 DKP # PP 022 WM | American Walnut
 OUTSIDE: MDF HMR E1 V313 DKP # 836 NCT | Anti-Fingerprint
 FRONTAGE: MDF HMR E1 V313 DKP # 836 NCT | Anti-Fingerprint
 HANDLE: Aluminum DKP #5230 | Ivory
 HANDLE: Aluminum DKP #5230 | Dark Choco
 TOP: Quartz Vadara G1 #V743 | Ostara Dawn
 FRONTAGE: Aluminum DKP #5158 (มีมือจับในตัว) | Dark Choco ,
 กระจกใส TYK | Euro Bronze 5 mm. (Tempered)

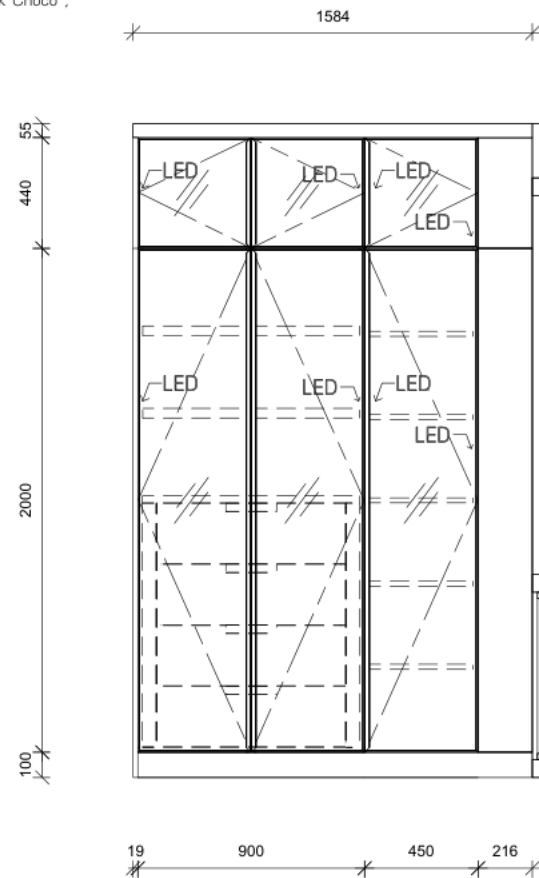

ELEVATION B

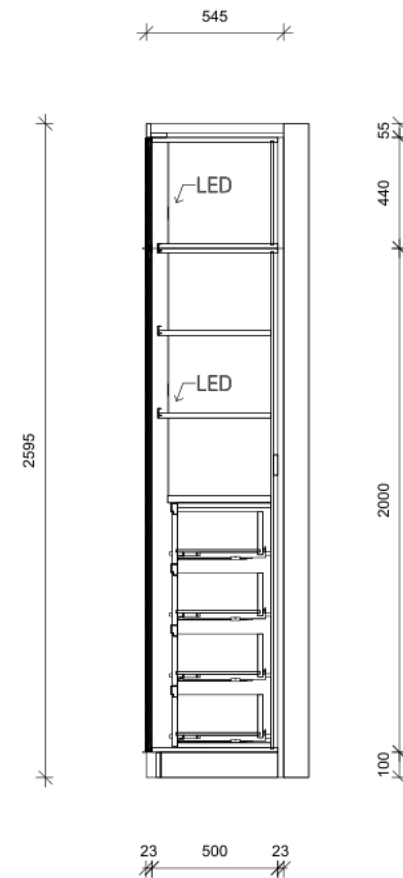


SECTION 2

Dkbb


157 Praditmanutham Road
 Bangkapi Bangkok 10240
 TEL:0-2515-1162 FAX:0-2515-1161
 WWW.decorchoice.co.th

Client : Ari789	Design : Master Walk-In Closet - 4B	View : Elevation B , Section 2
Address :	Series : Elegance	Scale : 1:30
Province :-	Drawn by : บริษัท สุนทรจามร	Date : 10/9/2569
Phone :	Email :	Page : 03

INSIDE: MDF HMR E1 V313 DKP # PP 022 WM | American Walnut
 OUTSIDE: MDF HMR E1 V313 DKP # 836 NCT | Anti-Fingerprint
 FRONTAGE: MDF HMR E1 V313 DKP # 836 NCT | Anti-Fingerprint
 HANDLE: Aluminum DKP #5230 | Ivory
 HANDLE: Aluminum DKP #5230 | Dark Choco
 TOP: Quartz Vadara G1 #V743 | Ostara Dawn
 FRONTAGE: Aluminum DKP #5158 (มีมือจับในตัว) | Dark Choco ,
 กระจกเงา ใส TYK | Euro Bronze 5 mm. (Tempered)

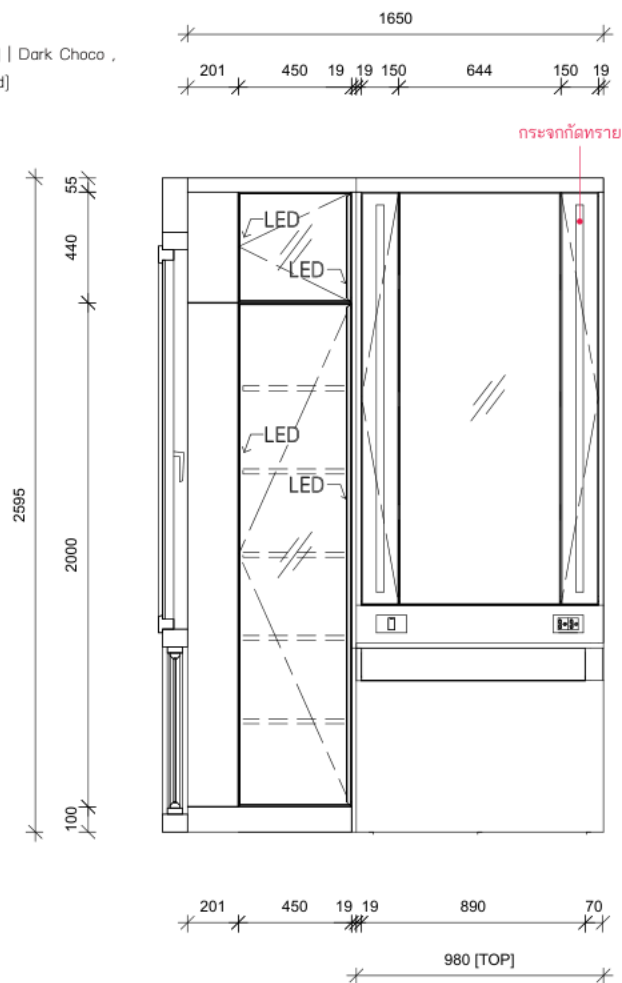

ELEVATION C

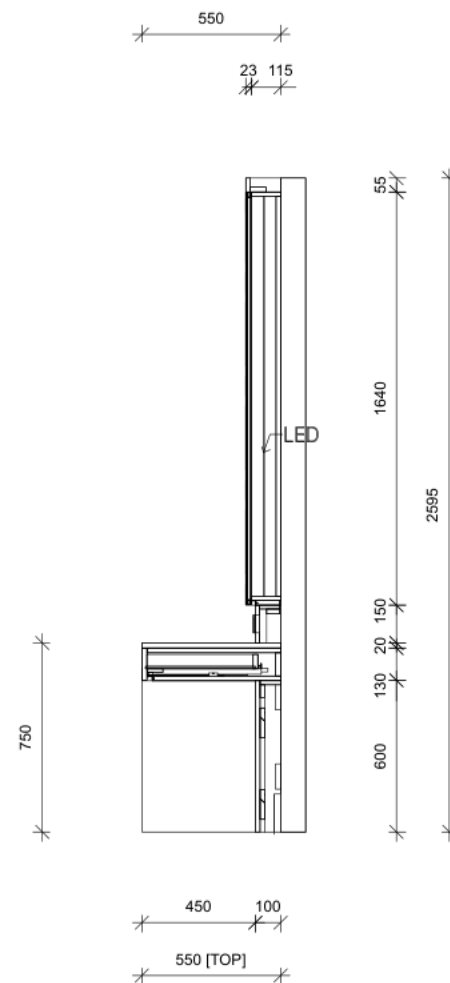

SECTION 3

Dkbb

157 Praditmanutham Road
 Bangkapi Bangkok 10240
 TEL:0-2515-1162 FAX:0-2515-1161
 WWW.decorchoice.co.th

Client : Ari789

Address :

Province :-

Phone :

Design : Master Walk-In Closet - 4B

Series : Elegance

Drawn by : บริษัท สุนทรจามร

Email :

View : Elevation C , Section 3

Scale : 1:30

Date : 10/9/2569

Page : 04



โบสรูปเฟอร์นิเจอร์ บริษัท อารี789 ดีเวลลอปเม้นท์ จำกัด
เลขที่ 10/1 ซอยพหลโยธิน 5 ถนนพหลโยธิน แขวงพญาไท เขตพญาไท
กรุงเทพมหานคร 10400 โทร : 044-110218
เลขประจำตัวผู้เสียภาษีอากร 0105565012642 (สำนักงานใหญ่)

Q.26/0917

14 กันยายน 2569

4B Floor 4 : Walk-in closet (Master Bedroom) รุ่น ELEGANCE

1	ตู้เก็บของพร้อมโต๊ะแต่งตัว ขนาด 0.55 X 1.65 X 2.595 ม.	69,196.00
2	ตู้เสื้อผ้าบานเปิดตัว I ขนาด 0.598 X 1.645 X 2.595 ม.	86,921.00
3	ตู้เก็บของ ขนาด 0.545 X 1.584 X 2.595 ม.	102,327.00
รวม		258,444.00
ส่วนลด 15%		-38,767.00
ยอดรวม หลังหักส่วนลด		219,677.00
4	ไฟ LED ในตู้เก็บของพร้อมโต๊ะแต่งตัว	10,360.00
5	ไฟ LED ในตู้เสื้อผ้าบานเปิดตัว I	3,480.00
6	ไฟ LED ในตู้เก็บของ	9,910.00
รวมเงิน Ex. Vat		243,427.00
VAT 7%		17,039.89
ยอดสุทธิ		260,466.89

หมายเหตุ - ก่อนเซ็นสั่งซื้อสินค้า กรุณาตรวจสอบแบบและรายละเอียดต่างๆ ให้ครบถ้วน
เนื่องจากเป็นการสั่งผลิตเฉพาะงาน
- ไฟแสงสว่าง, สีของไฟ LED, ตำแหน่งปลั๊กใช้งาน, กุญแจล็อคต่างๆ ไม่สามารถเพิ่มภายหลังได้
กรุณาตรวจสอบก่อนว่ามีครบตามต้องการหรือไม่
- หลังจากสั่งซื้อสินค้าแล้ว ทางบริษัทฯ ขอสงวนสิทธิ์ในการแก้ไขใดๆทั้งสิ้น

บริษัท เดคคอร์ส ชอยส์ จำกัด

157 ซ.โยธินพัฒนา ถ.ประดิษฐ์มนูธรรม แขวงคลองจั่น เขตบางกะปิ กรุงเทพฯ 10240

Tel : 0 2515 1162 Fax : 0 2515 1161 Call Center : 08-1954-5550

E-mail : decorchoice@gmail.com www.decorchoice.co.th