












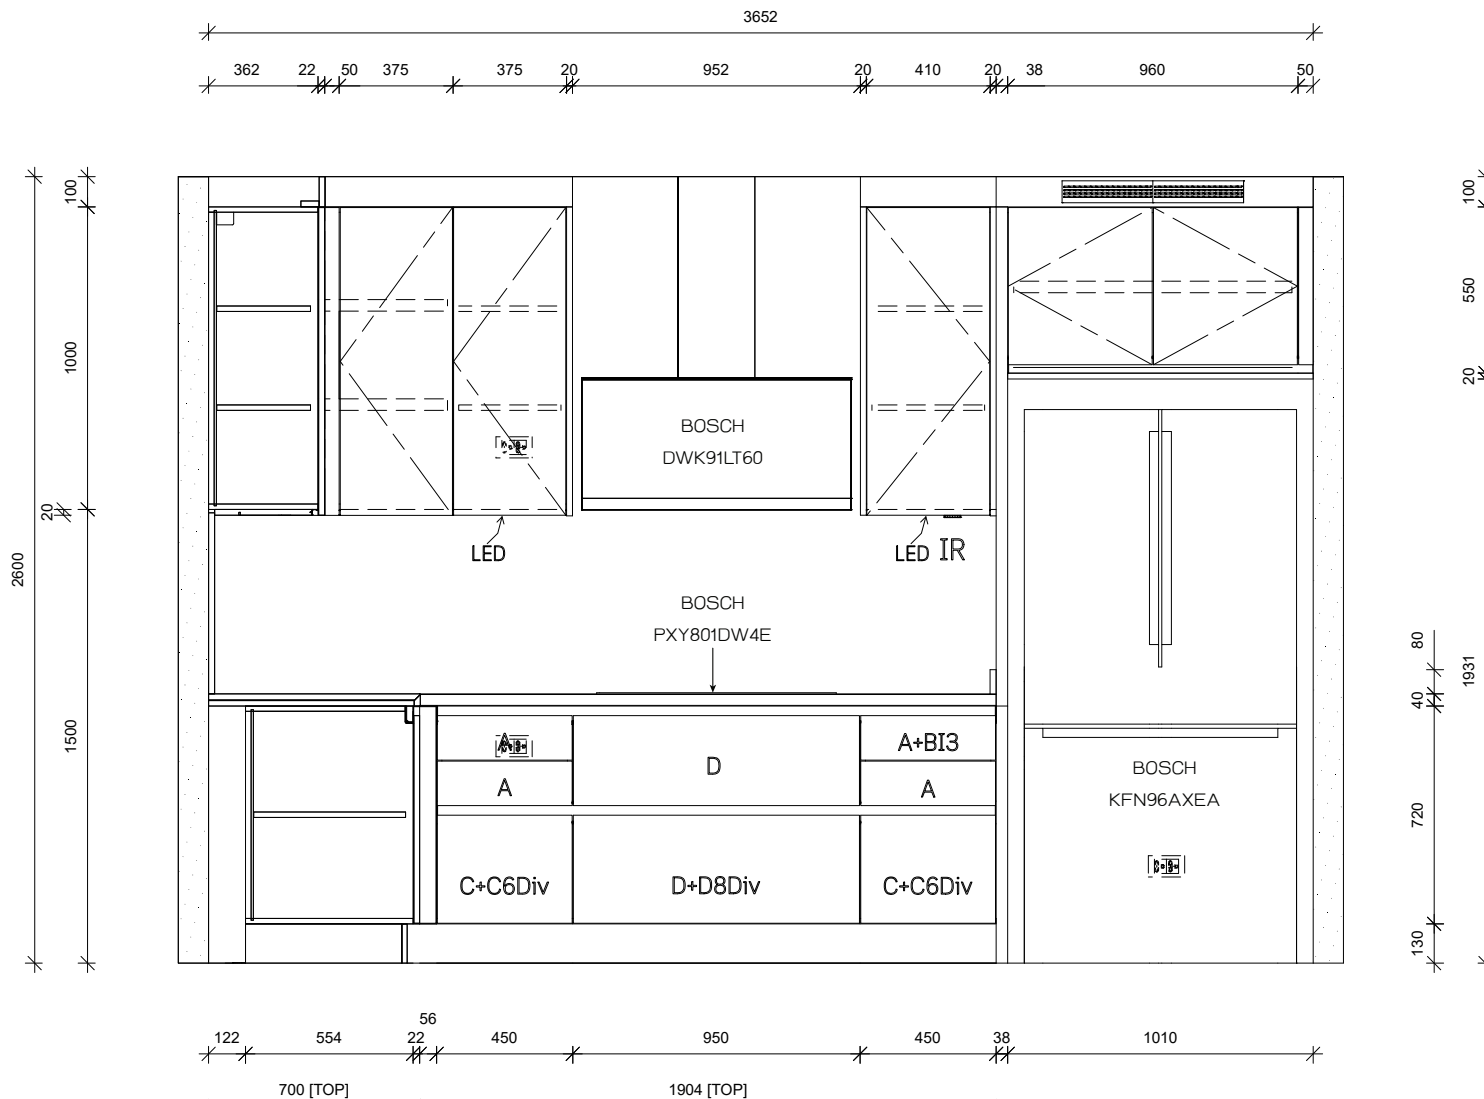

INSIDE : DK Board Laminate DKBB #IAB 8101 | PLEASANT TEAK

OUTSIDE : DK Board Laminate FORMICA FENIX NTM #0748 | BEIGE ARIZONA

FRONTAGE : VI PLUS Laminate FORMICA FENIX NTM #0748 | BEIGE ARIZONA

ด้านหลังปิด Laminate PANAPLAST # S-B 28779PM | LATTE

TOP/BACK SPLASH : QUARTZ VADARA #V743 | OSTARA DAWN 20 mm.

HANDLE : ALUMINIUM PROFILE-C | ALUMINIUM

HANDLE : ALUMINIUM PROFILE-J | ALUMINIUM

HANDLE : HAFELE # 125.95.910

HANDLE : HAFELE #126.95.920

เสริมแข็ง : Ivory

Dkbb

157 Praditmanutham Road
Bangkapi Bangkok 10240
TEL:0-2515-1162 FAX:0-2515-1161
WWW.decorchoice.co.th

Client : ARI 789

Address :

Province :-

Phone :

Design : Kitchen 3A

Series : Elegance Plus

Drawn by : บริษัท สุนทรจามร

Email :


View : Elevation A

Scale : 1:25

Date : 28/2/2569

Page : 02

Handwritten signature and date
9-3-69

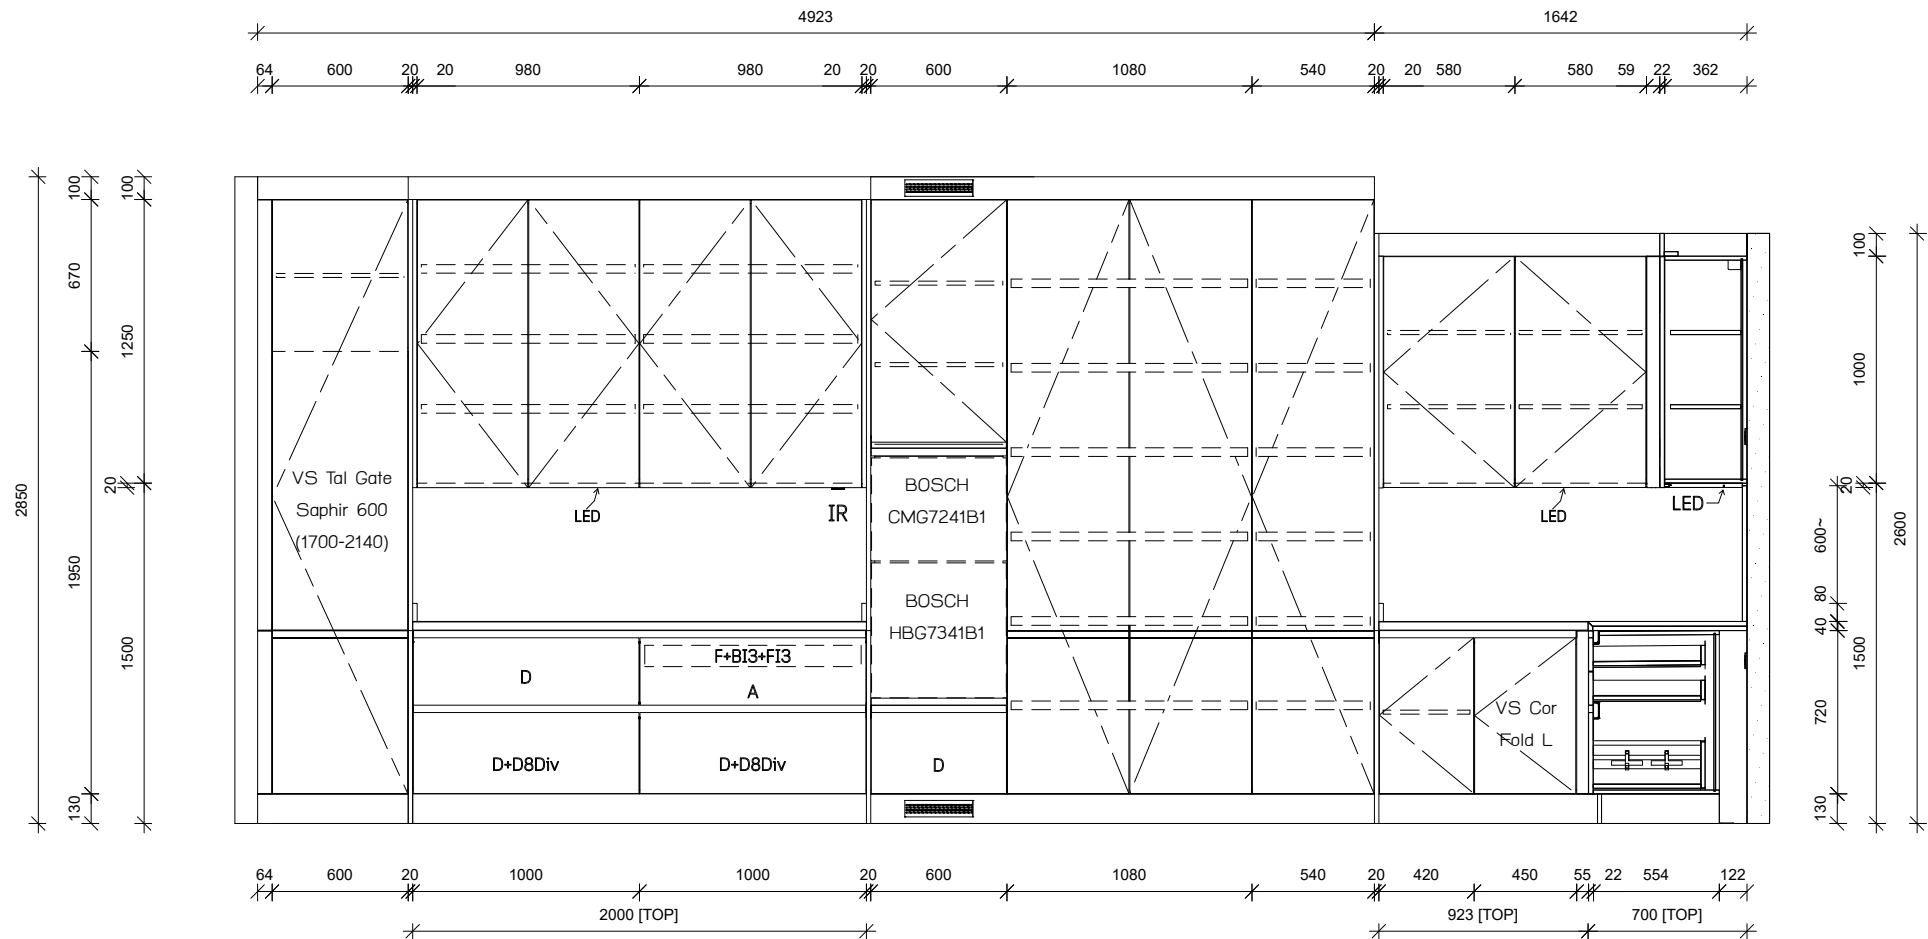

INSIDE : DK Board Laminate DKBB #IAB 8101 | PLEASANT TEAK

OUTSIDE : DK Board Laminate FORMICA FENIX NTM #0748 | BEIGE ARIZONA

FRONTAGE : VI PLUS Laminate FORMICA FENIX NTM #0748 | BEIGE ARIZONA

ด้านหลังปิด Laminate PANAPLAST # S-B 28779PM | LATTE

TOP/BACK SPLASH : QUARTZ VADARA #V743 | OSTARA DAWN 20 mm.

HANDLE : ALUMINIUM PROFILE-C | ALUMINIUM

HANDLE : ALUMINIUM PROFILE-J | ALUMINIUM

HANDLE : HAFELE # 125.95.910

HANDLE : HAFELE #126.95.920

เสริมแข็ง : Ivory

Dkbb

157 Praditmanutham Road
Bangkapi Bangkok 10240
TEL:0-2515-1162 FAX:0-2515-1161
WWW.decorchoice.co.th

Client : ARI 789

Address :

Province :-

Phone :

Design : Kitchen 3A

Series : Elegance Plus

Drawn by : บริษัท สุนทรจามร

Email :


View : Elevation B

Scale : 1:33.33


Date : 28/2/2569

Page : 03

amh
9-3-69

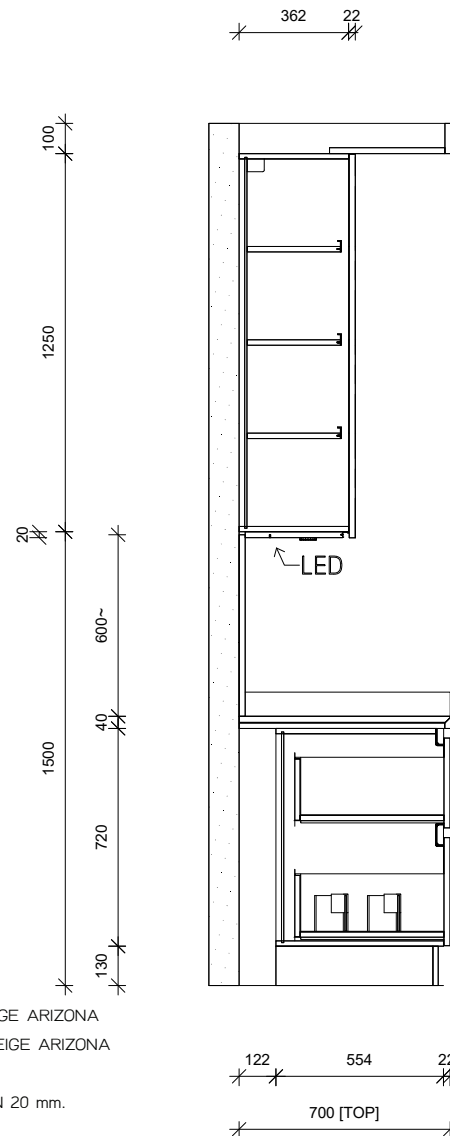

SECTION 1

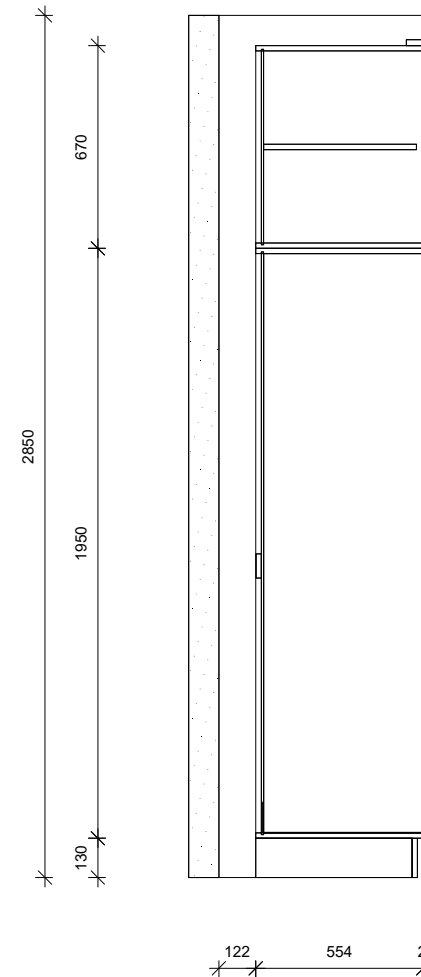

SECTION 2

INSIDE : DK Board Laminate DKBB #IAB 8101 | PLEASANT TEAK
 OUTSIDE : DK Board Laminate FORMICA FENIX NTM #0748 | BEIGE ARIZONA
 FRONTAGE : VI PLUS Laminate FORMICA FENIX NTM #0748 | BEIGE ARIZONA
 ด้านหลังปิด Laminate PANAPLAST # S-B 28779PM | LATTE
 TOP/BACK SPLASH : QUARTZ VADARA #V743 | OSTARA DAWN 20 mm.
 HANDLE : ALUMINIUM PROFILE-C | ALUMINIUM
 HANDLE : ALUMINIUM PROFILE-J | ALUMINIUM
 HANDLE : HAFELE # 125.95.910
 HANDLE : HAFELE #126.95.920
 เสีร์มแข็ง : Ivory

Handwritten signature and date:
 ๑-3-69

Dkbb

157 Praditmanutham Road
 Bangkapi Bangkok 10240
 TEL:0-2515-1162 FAX:0-2515-1161
 WWW.decorchoice.co.th

Client : ARI 789

Address :

Province :-

Phone :

Design : Kitchen 3A

Series : Elegance Plus

Drawn by : บริษัท สุนทรจามร

Email :

View : Section 1,2

Scale : 1:25

Date : 28/2/2569

Page : 04

INSIDE : DK Board Laminate DKBB #IAB 8101 | PLEASANT TEAK

OUTSIDE : DK Board Laminate FORMICA FENIX NTM #0748 | BEIGE ARIZONA

FRONTAGE : VI PLUS Laminate FORMICA FENIX NTM #0748 | BEIGE ARIZONA

ด้านหลังปิด Laminate PANAPLAST # S-B 28779PM | LATTE

TOP/BACK SPLASH : QUARTZ VADARA #V743 | OSTARA DAWN 20 mm.


HANDLE : ALUMINIUM PROFILE-C | ALUMINIUM

HANDLE : ALUMINIUM PROFILE-J | ALUMINIUM

HANDLE : HAFELE # 125.95.910


HANDLE : HAFELE #126.95.920

เสริมแข็ง : Ivory

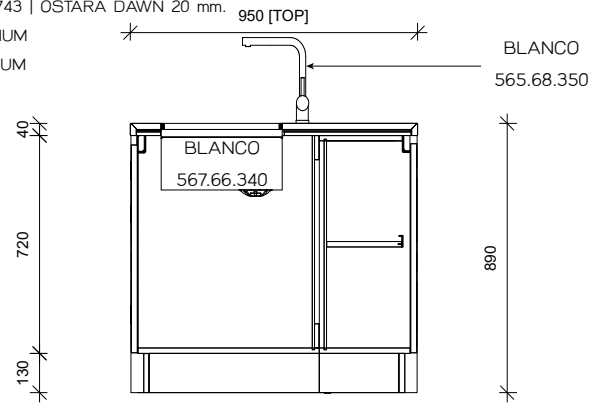


22 600 300 22

SECTION 4

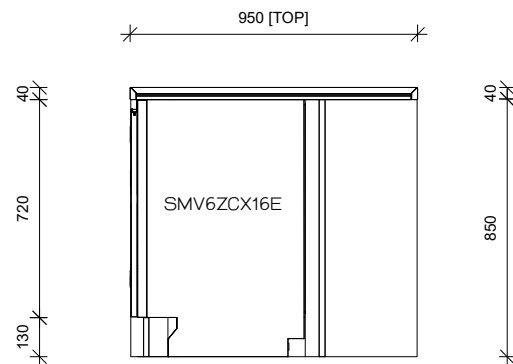


20 602 20 304

SECTION 5

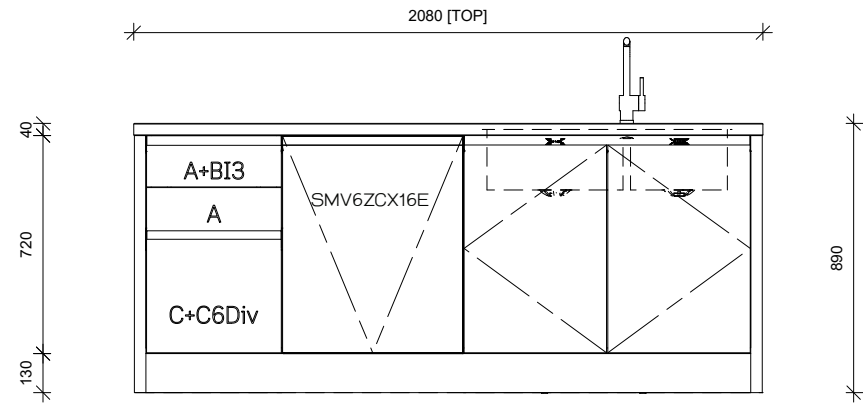

40 450 600 950 40

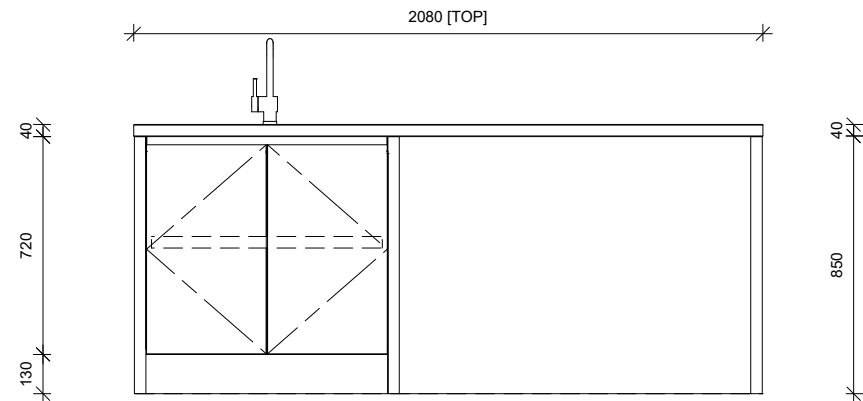

38 800 38 1162 38

9-3-69

Dkbb

157 Praditmanutham Road
Bangkapi Bangkok 10240
TEL:0-2515-1162 FAX:0-2515-1161
WWW.decorchoice.co.th

Client : ARI 789

Address :

Province :-

Phone :

Design : Kitchen 3A

Series : Elegance Plus

Drawn by : บริษัท สุนทรจามร

Email :

View : Island

Scale : 1:25

Date : 28/2/2569

Page : 05



ใบสรุปเฟอร์นิเจอร์ บริษัท อาร์789 ดีเวลลอปเม้นท์ จำกัด
เลขที่ 10/1 ซอยพหลโยธิน 5 ถนนพหลโยธิน แขวงพญาไท เขตพญาไท
กรุงเทพมหานคร 10400 โทร : 044-110218
เลขประจำตัวผู้เสียภาษีอากร 0105565012642 (สำนักงานใหญ่)

9 มีนาคม 2569

3A Floor 3-KITCHEN รุ่น ELEGANCE PLUS (กันปลวกกันน้ำรับประกัน 10 ปี)

1 KITCHEN ตัว L		1,048,731.00
1.1 KITCHEN ตัว L ขนาด 0.70 X 10.217 X 2.85 ม.	744,346.00	
1.2 TOP และผนังกันเปื้อน หิน QUARTZ VADARA # V743 (OSTARA DAWN)	92,750.00	
1.3 อุปกรณ์ภายในตู้	211,635.00	
2 ISLAND		205,607.00
2.1 ISLAND ขนาด 1.00 X 2.08 X 0.89 ม.	150,227.00	
2.2 TOP หิน QUARTZ VADARA # V743 (OSTARA DAWN)	22,880.00	
2.3 อุปกรณ์ภายในตู้	32,500.00	
	รวม	1,254,338.00
	ส่วนลด 15%	-188,151.00
	ยอดรวม หลังหักส่วนลด	1,066,187.00
3 ไฟ LED		7,240.00
4 ค่าติดตั้งอุปกรณ์ครัว (ในกรณีลูกค้าซื้ออุปกรณ์ครัวเอง)		5,800.00
	รวมเงิน Ex. Vat	1,079,227.00
	VAT 7%	75,545.89
	ยอดสุทธิ	1,154,772.89

หมายเหตุ - ก่อนเซ็นสั่งซื้อสินค้า กรุณาตรวจสอบแบบและรายละเอียดต่างๆ ให้ครบถ้วน
เนื่องจากการสั่งผลิตเฉพาะงาน
- ไฟแสงสว่าง, สีของไฟ LED, ตำแหน่งปลั๊กใช้งาน, ภูเขาเหล็กต่างๆ ไม่สามารถเพิ่มภายหลังได้
กรุณาตรวจสอบก่อนว่ามีครบตามต้องการหรือไม่
- หลังจากสั่งซื้อสินค้าแล้ว ทางบริษัทฯ ขอสงวนสิทธิ์ในการแก้ไขใดๆทั้งสิ้น

บริษัท เดคคอร์ส ชอยส์ จำกัด

157 ซ.โยธินพัฒนา อ.ประดิษฐ์มนูธรรม แขวงคลองจั่น เขตบางกะปิ กรุงเทพฯ 10240

Tel : 0 2515 1162 Fax : 0 2515 1161 Call Center : 08-1954-5550

E-mail : decorchoice@gmail.com www.decorchoice.co.th