


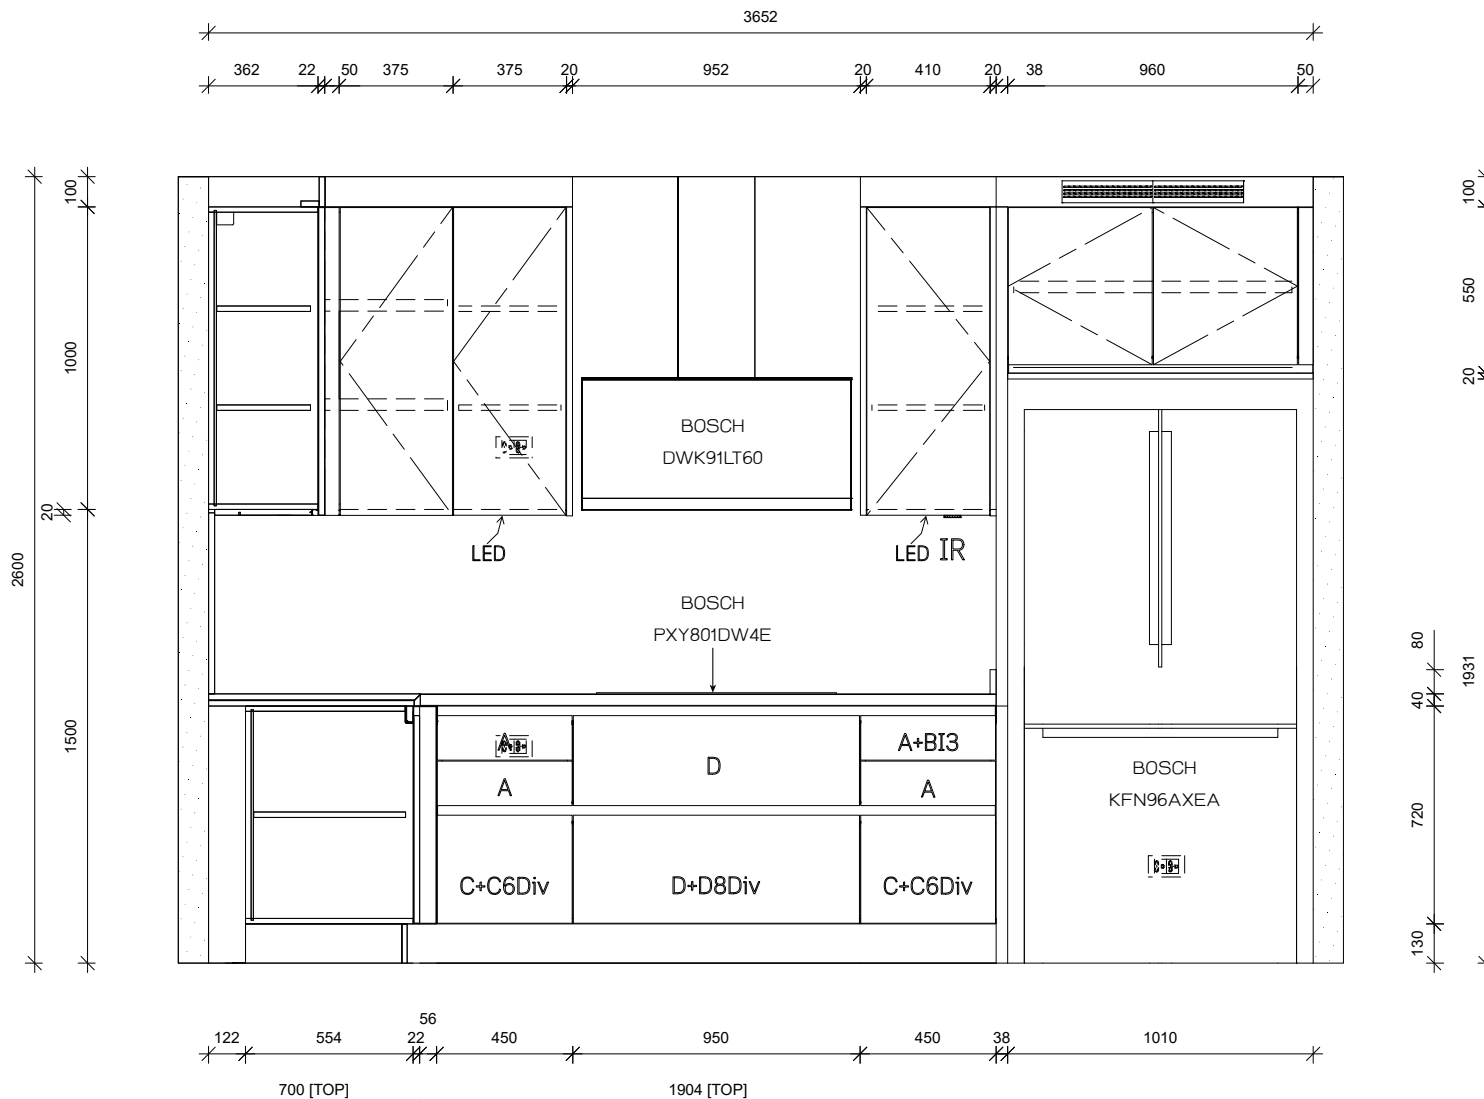

INSIDE : DK Board Laminate DKBB #IAB 8101 | PLEASANT TEAK

OUTSIDE : DK Board Laminate FORMICA FENIX NTM #0748 | BEIGE ARIZONA

FRONTAGE : VI PLUS Laminate FORMICA FENIX NTM #0748 | BEIGE ARIZONA

ด้านหลังปิด Laminate PANAPLAST # S-B 28779PM | LATTE

TOP/BACK SPLASH : QUARTZ VADARA #V743 | OSTARA DAWN 20 mm.

HANDLE : ALUMINIUM PROFILE-C | ALUMINIUM

HANDLE : ALUMINIUM PROFILE-J | ALUMINIUM

HANDLE : HAFELE # 125.95.910

HANDLE : HAFELE #126.95.920

เสริมแข็ง : Ivory

Dkbb

157 Praditmanutham Road
Bangkapi Bangkok 10240
TEL:0-2515-1162 FAX:0-2515-1161
WWW.decorschoice.co.th

Client : ARI 789

Address :

Province :-

Phone :

Design : Kitchen 3A

Series : Elegance Plus

Drawn by : บริษัท สุนทรจามร

Email :


View : Elevation A

Scale : 1:25

Date : 28/2/2569

Page : 02

Handwritten signature and date
9-3-69

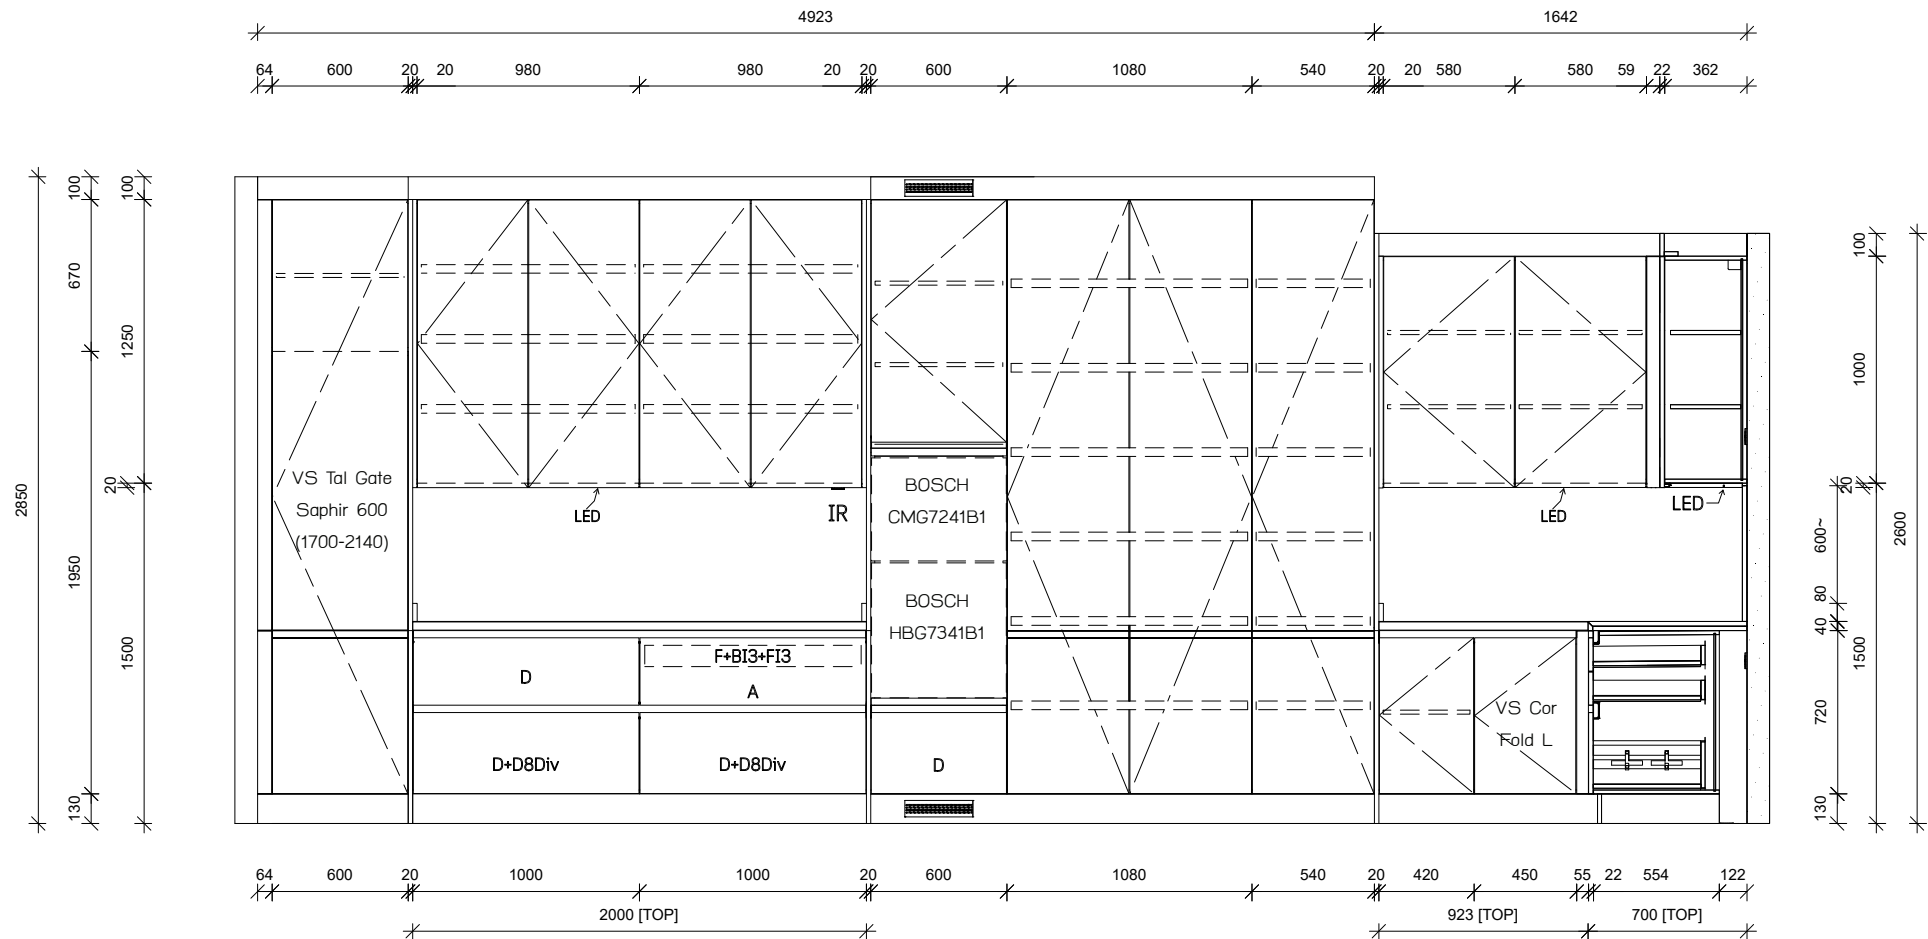

Handwritten signature and date:
9-3-69

Dkbb

157 Praditmanutham Road
Bangkapi Bangkok 10240
TEL:0-2515-1162 FAX:0-2515-1161
WWW.decorchoice.co.th

Client : ARI 789

Address :

Province :-

Phone :

Design : Kitchen 3A

Series : Elegance Plus

Drawn by : บริษัท สุนทรจามร


Email :

View : Elevation B


Scale : 1:33.33

Date : 28/2/2569

Page : 03

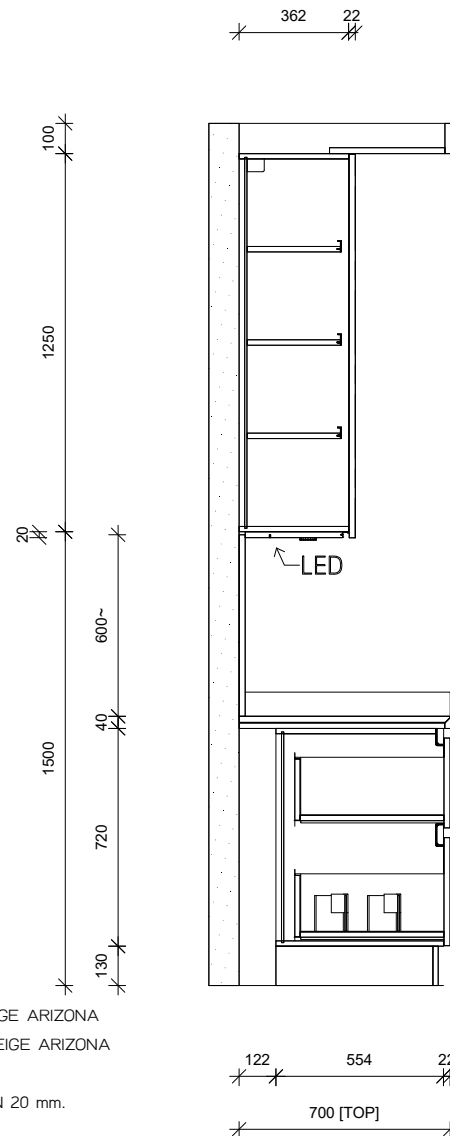

SECTION 1

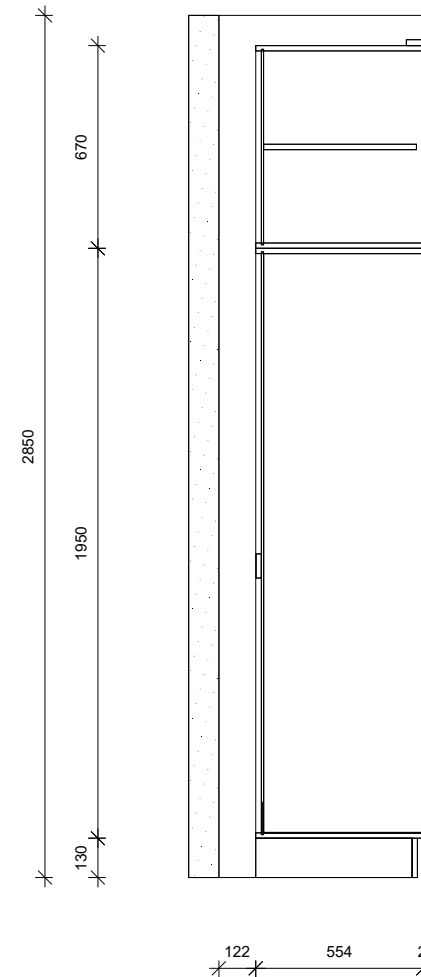

SECTION 2

INSIDE : DK Board Laminate DKBB #IAB 8101 | PLEASANT TEAK
 OUTSIDE : DK Board Laminate FORMICA FENIX NTM #0748 | BEIGE ARIZONA
 FRONTAGE : VI PLUS Laminate FORMICA FENIX NTM #0748 | BEIGE ARIZONA
 ด้านหลังปิด Laminate PANAPLAST # S-B 28779PM | LATTE
 TOP/BACK SPLASH : QUARTZ VADARA #V743 | OSTARA DAWN 20 mm.
 HANDLE : ALUMINIUM PROFILE-C | ALUMINIUM
 HANDLE : ALUMINIUM PROFILE-J | ALUMINIUM
 HANDLE : HAFELE # 125.95.910
 HANDLE : HAFELE #126.95.920
 เสีริมแข็ง : Ivory

Handwritten signature and date:
 ๑-3-69

Dkbb

157 Praditmanutham Road
 Bangkapi Bangkok 10240
 TEL:0-2515-1162 FAX:0-2515-1161
 WWW.decorchoice.co.th

Client : ARI 789	Design : Kitchen 3A	View : Section 1,2
Address :	Series : Elegance Plus	Scale : 1:25
Province :-	Drawn by : บริษัท สุนทรจามร	Date : 28/2/2569
Phone :	Email :	Page : 04

INSIDE : DK Board Laminate DKBB #IAB 8101 | PLEASANT TEAK

OUTSIDE : DK Board Laminate FORMICA FENIX NTM #0748 | BEIGE ARIZONA

FRONTAGE : VI PLUS Laminate FORMICA FENIX NTM #0748 | BEIGE ARIZONA

ด้านหลังปิด Laminate PANAPLAST # S-B 28779PM | LATTE

TOP/BACK SPLASH : QUARTZ VADARA #V743 | OSTARA DAWN 20 mm.


HANDLE : ALUMINIUM PROFILE-C | ALUMINIUM

HANDLE : ALUMINIUM PROFILE-J | ALUMINIUM

HANDLE : HAFELE # 125.95.910


HANDLE : HAFELE #126.95.920

เสริมแข็ง : Ivory

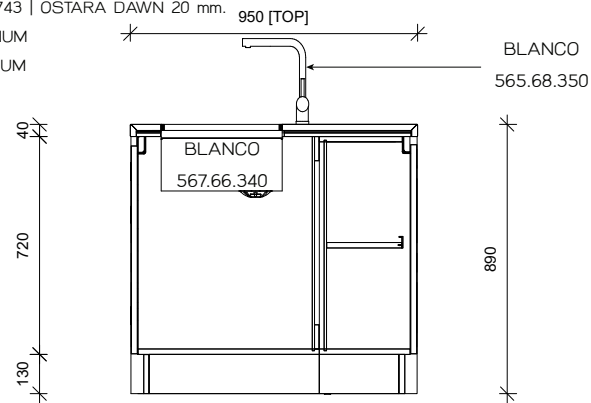


22 600 300 22

SECTION 4

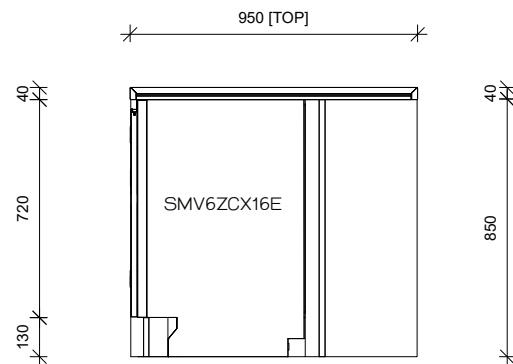


20 602 20 304

SECTION 5

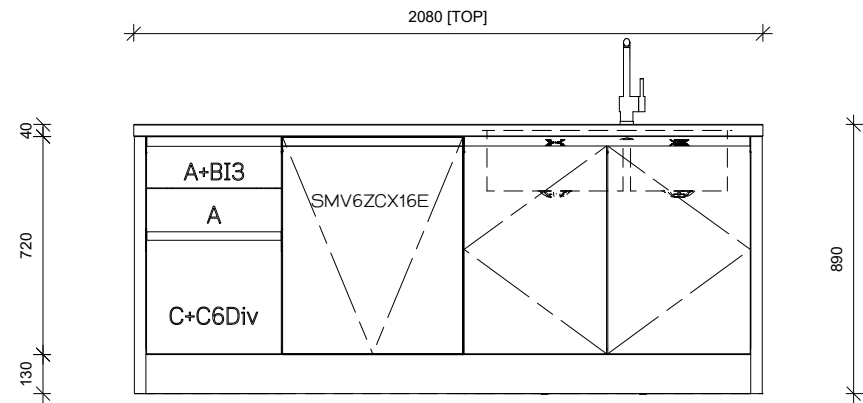

40 450 600 950 40

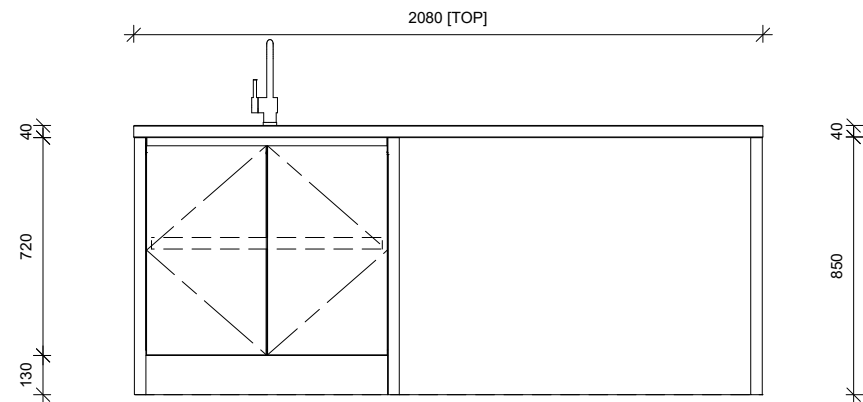

38 800 38 1162 38

9-3-69

Dkbb

157 Praditmanutham Road
Bangkapi Bangkok 10240
TEL:0-2515-1162 FAX:0-2515-1161
WWW.decorchoice.co.th

Client : ARI 789

Address :

Province :-

Phone :

Design : Kitchen 3A

Series : Elegance Plus

Drawn by : บริษัท สุนทรจามร

Email :

View : Island

Scale : 1:25

Date : 28/2/2569

Page : 05