


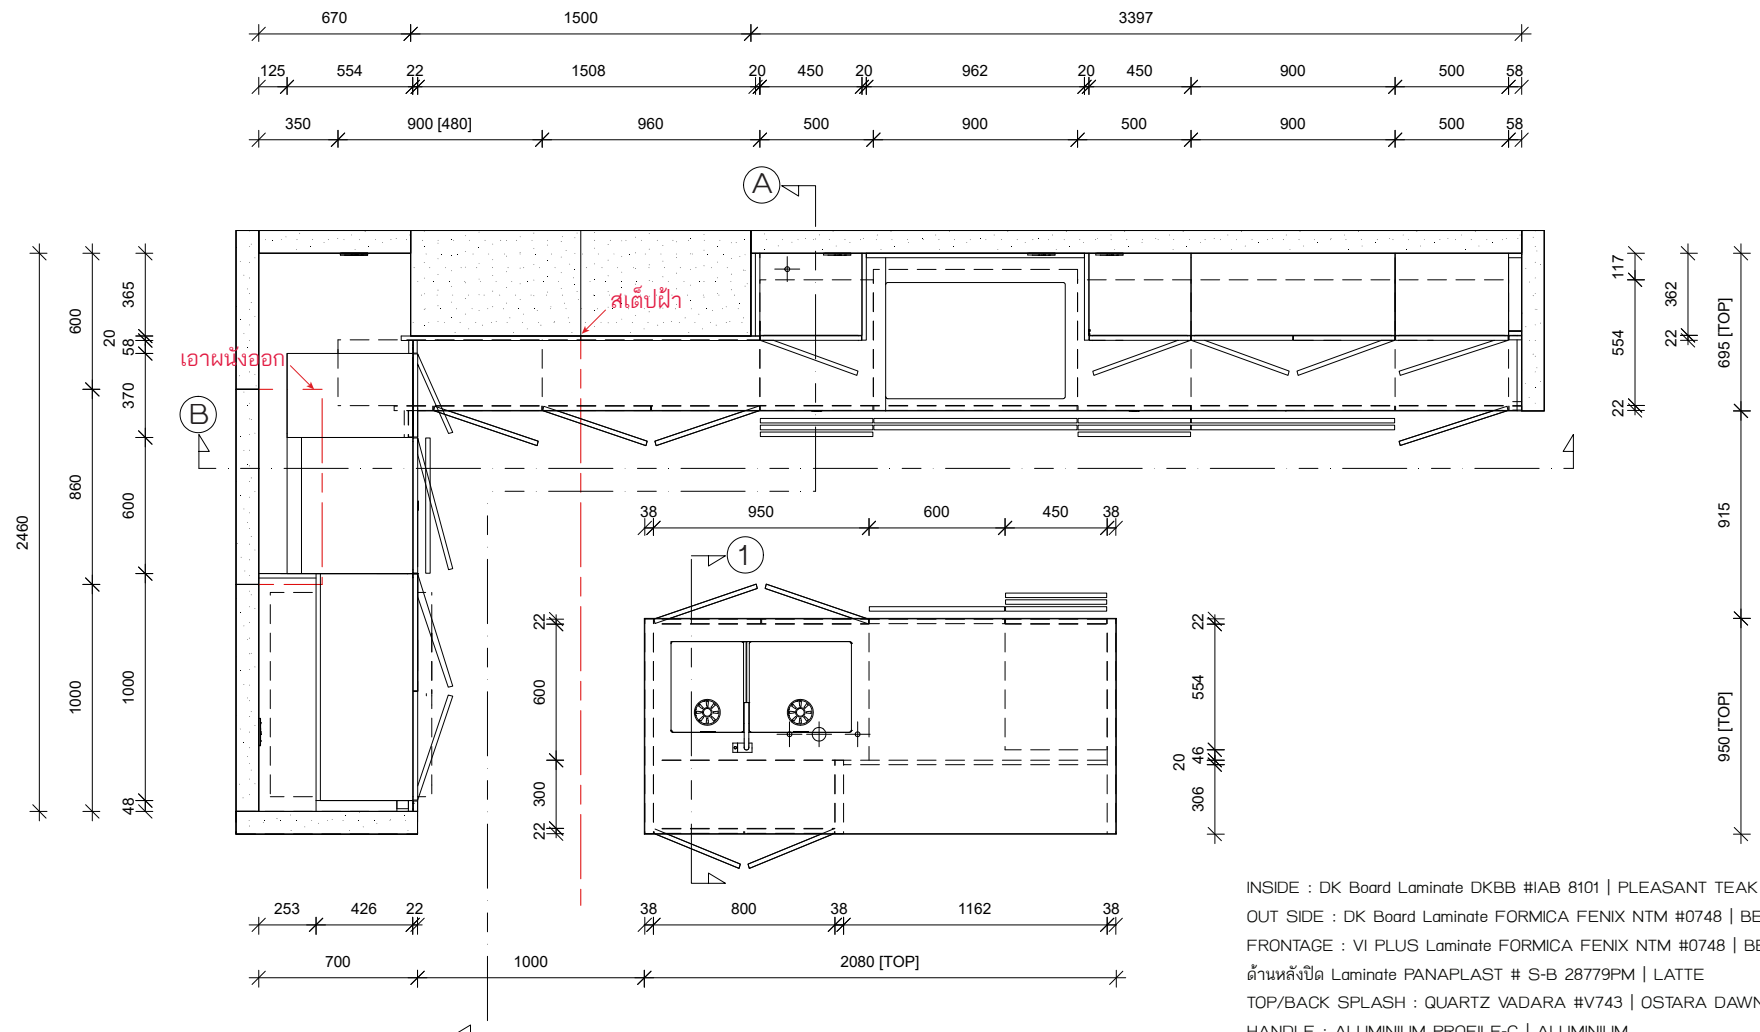









INSIDE : DK Board Laminate DKBB #IAB 8101 | PLEASANT TEAK
 OUT SIDE : DK Board Laminate FORMICA FENIX NTM #0748 | BEIGE ARIZONA
 FRONTAGE : VI PLUS Laminate FORMICA FENIX NTM #0748 | BEIGE ARIZONA
 ด้านหลังปิด Laminate PANAPLAST # S-B 28779PM | LATTE
 TOP/BACK SPLASH : QUARTZ VADARA #V743 | OSTARA DAWN 20 mm.
 HANDLE : ALUMINIUM PROFILE-C | ALUMINIUM
 HANDLE : ALUMINIUM PROFILE-J | ALUMINIUM
 HANDLE : HAFELE # 125.95.910
 เสีร์มแข็ง : Ivory

amdt
 19-2-69

Dkbb

157 Praditmanutham Road
 Bangkapi Bangkok 10240
 TEL:0-2515-1162 FAX:0-2515-1161
 WWW.decorschoice.co.th

Client : ARI 789

Address :

Province :-

Phone :

Design : Kitchen 3C

Series : Elegance Plus

Drawn by : บริษัท สุนทรจามร

Email :

View : Plan

Scale : 1:33

Date : 18/2/2569

Page : 01

INSIDE : DK Board Laminate DKBB #IAB 8101 | PLEASANT TEAK

OUT SIDE : DK Board Laminate FORMICA FENIX NTM #0748 | BEIGE ARIZONA

FRONTAGE : VI PLUS Laminate FORMICA FENIX NTM #0748 | BEIGE ARIZONA

ด้านหลังปิด Laminate PANAPLAST # S-B 28779PM | LATTE


TOP/BACK SPLASH : QUARTZ VADARA #V743 | OSTARA DAWN 20 mm.

HANDLE : ALUMINIUM PROFILE-C | ALUMINIUM

HANDLE : ALUMINIUM PROFILE-J | ALUMINIUM

HANDLE : HAFELE # 125.95.910

เสริมแข็ง : Ivory

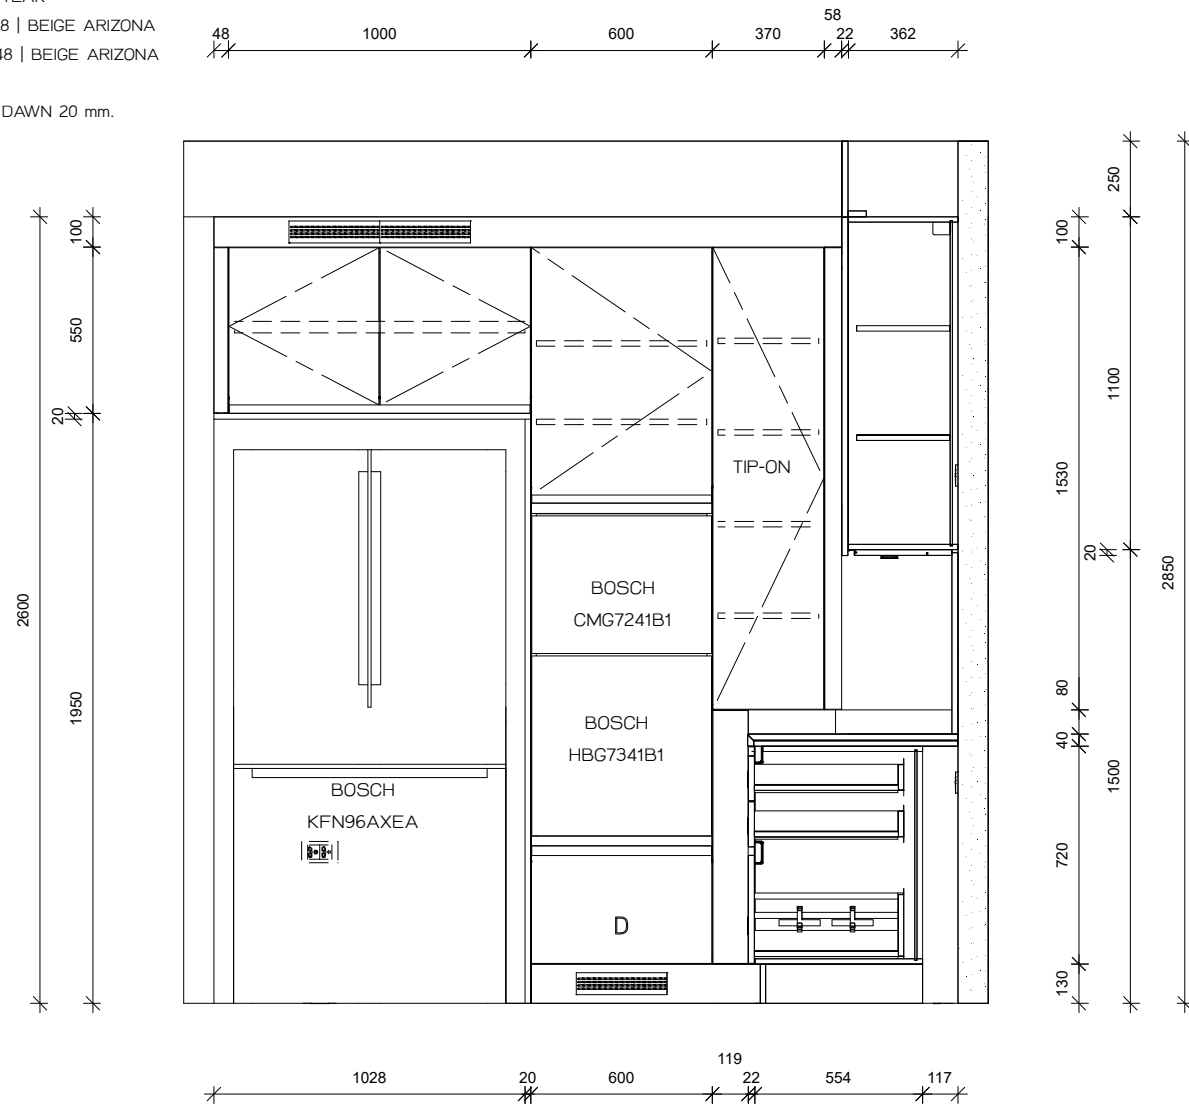

amv
19-2-69

Dkbb

157 Praditmanutham Road
Bangkapi Bangkok 10240
TEL:0-2515-1162 FAX:0-2515-1161
WWW.decorchoice.co.th

Client : ARI 789

Address :

Province :-

Phone :

Design : Kitchen 3C

Series : Elegance Plus

Drawn by : บริษัท สุนทรจามร


Email :

View : Elevation A

Scale : 1:25

Date : 18/2/2569

Page : 02

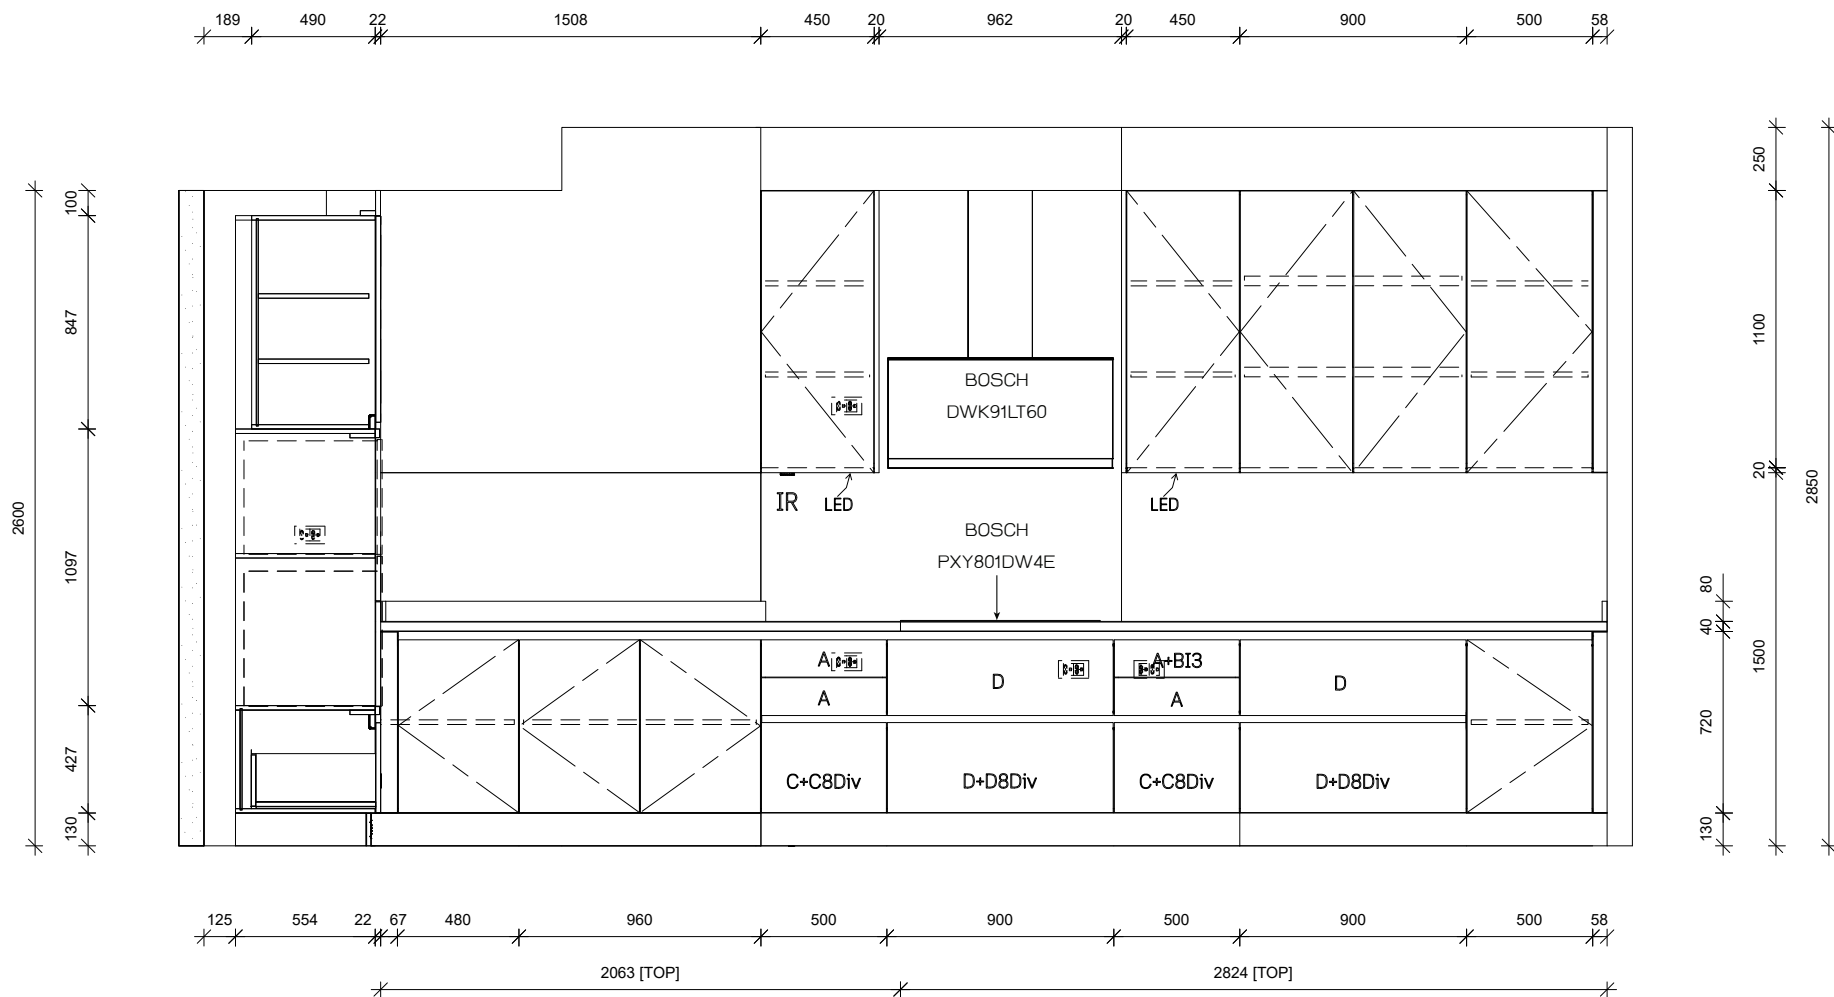

INSIDE : DK Board Laminate DKBB #IAB 8101 | PLEASANT TEAK
 OUT SIDE : DK Board Laminate FORMICA FENIX NTM #0748 | BEIGE ARIZONA
 FRONTAGE : VI PLUS Laminate FORMICA FENIX NTM #0748 | BEIGE ARIZONA
 ด้านหลังปิด Laminate PANAPLAST # S-B 28779PM | LATTE

TOP/BACK SPLASH : QUARTZ VADARA #V743 | OSTARA DAWN 20 mm. เสริมแข็ง : Ivory
 HANDLE : ALUMINIUM PROFILE-C | ALUMINIUM
 HANDLE : ALUMINIUM PROFILE-J | ALUMINIUM
 HANDLE : HAFELE # 125.95.910

pmah
 19-2-69

Dkbb

157 Praditmanutham Road
 Bangkapi Bangkok 10240
 TEL:0-2515-1162 FAX:0-2515-1161
 WWW.decorchoice.co.th

Client : ARI 789

Address :

Province :-

Phone :

Design : Kitchen 3C

Series : Elegance Plus

Drawn by : บริษัท สุนทรจามร



Email :

View : Elevation B


Scale : 1:30

Date : 18/2/2569

Page : 03

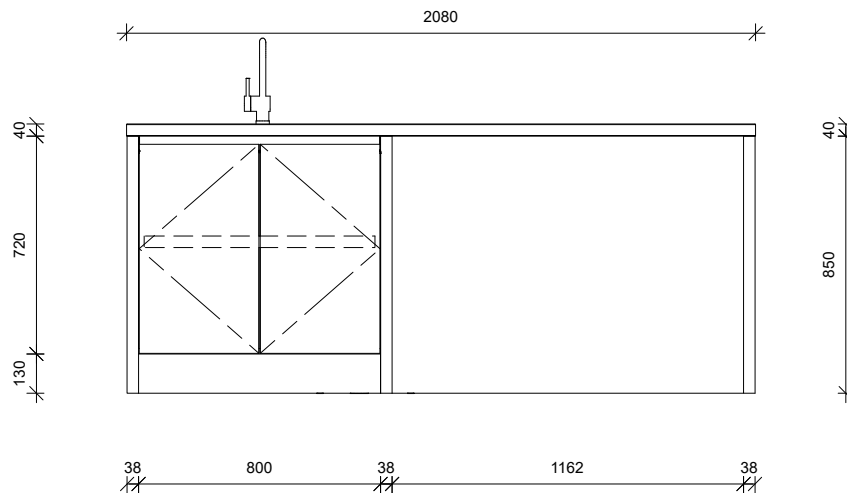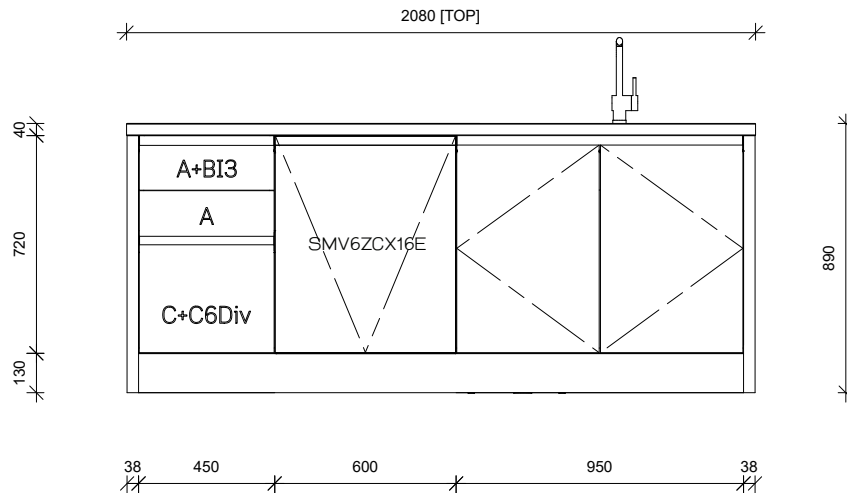

INSIDE : DK Board Laminate DKBB #IAB 8101 | PLEASANT TEAK
 OUT SIDE : DK Board Laminate FORMICA FENIX NTM #0748 | BEIGE ARIZONA
 FRONTAGE : VI PLUS Laminate FORMICA FENIX NTM #0748 | BEIGE ARIZONA
 ด้านหลังปิด Laminate PANAPLAST # S-B 28779PM | LATTE
 TOP/BACK SPLASH : QUARTZ VADARA #V743 | OSTARA DAWN 20 mm.
 HANDLE : ALUMINIUM PROFILE-C | ALUMINIUM
 HANDLE : ALUMINIUM PROFILE-J | ALUMINIUM
 HANDLE : HAFELE # 125.95.910
 เสีริมแข็ง : Ivory

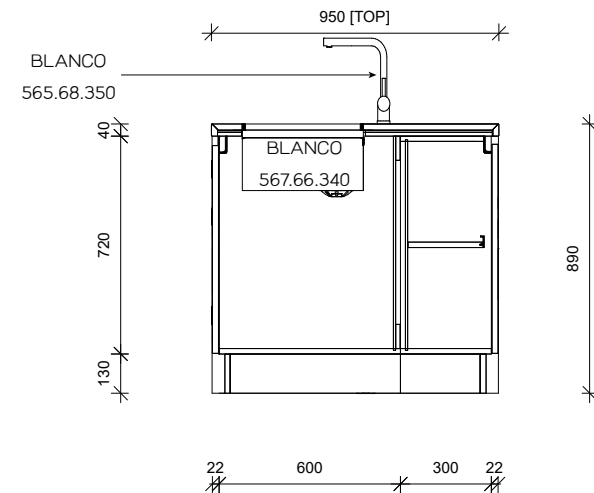

omdt
 19-2-69

Dkbb

157 Praditmanutham Road
 Bangkapi Bangkok 10240
 TEL:0-2515-1162 FAX:0-2515-1161
 WWW.decorchoice.co.th

Client : ARI 789	Design : Kitchen 3C	View : Island
Address :	Series : Elegance Plus	Scale : 1:25
Province :-	Drawn by : บริษัท สุนทรจามร	Date : 18/2/2569
Phone :	Email :	Page : 04



ใบสรุปเฟอร์นิเจอร์ บริษัท อาร์789 ดีเวลลอปเม้นท์ จำกัด
เลขที่ 10/1 ซอยพหลโยธิน 5 ถนนพหลโยธิน แขวงพญาไท เขตพญาไท
กรุงเทพมหานคร 10400 โทร : 044-110218
เลขประจำตัวผู้เสียภาษีอากร 0105565012642 (สำนักงานใหญ่)

19 กุมภาพันธ์ 2569

3C Floor 3-KITCHEN รุ่น ELEGANCE PLUS (กันปลวกกันน้ำรับประกัน 10 ปี)

1	KITCHEN ตัว L	631,540.00
1.1	KITCHEN ตัว L ขนาด 0.70 X 7.664 X 2.85 ม.	441,207.00
1.2	TOP และผนังกันเปื้อน หิน QUARTZ VADARA # V743 (OSTARA DAWN)	70,013.00
1.3	อุปกรณ์ภายในตู้	120,320.00
2	ISLAND	205,607.00
2.1	ISLAND ขนาด 1.00 X 2.08 X 0.89 ม.	150,227.00
2.2	TOP หิน QUARTZ VADARA # V743 (OSTARA DAWN)	22,880.00
2.3	อุปกรณ์ภายในตู้	32,500.00
รวม		837,147.00
ส่วนลด 15%		-125,572.00
ยอดรวม หลังหักส่วนลด		711,575.00
3	ไฟ LED ใต้ตู้ลอย	3,410.00
4	ค่าติดตั้งอุปกรณ์ครัว (ในกรณีลูกค้าซื้ออุปกรณ์ครัวเอง)	5,800.00
รวมเงิน Ex. Vat		720,785.00
VAT 7%		50,454.95
ยอดสุทธิ		771,239.95

หมายเหตุ - ก่อนเซ็นสั่งซื้อสินค้า กรุณาตรวจสอบแบบและรายละเอียดต่างๆ ให้ครบถ้วน
เนื่องจากการสั่งผลิตเฉพาะงาน
- ไฟแสงสว่าง, สีของไฟ LED, ตำแหน่งปลั๊กใช้งาน, ภูเขาเหล็กต่างๆ ไม่สามารถเพิ่มภายหลังได้
กรุณาตรวจสอบก่อนว่ามีครบตามต้องการหรือไม่
- หลังจากสั่งซื้อสินค้าแล้ว ทางบริษัทฯ ขอสงวนสิทธิ์ในการแก้ไขใดๆทั้งสิ้น

บริษัท เดคคอร์ส ชอยส์ จำกัด

157 ซ.โยธินพัฒนา อ.ประดิษฐ์มนูธรรม แขวงคลองจั่น เขตบางกะปิ กรุงเทพฯ 10240

Tel : 0 2515 1162 Fax : 0 2515 1161 Call Center : 08-1954-5550

E-mail : decorchoice@gmail.com www.decorchoice.co.th