


INSIDE: MDF HMR E1 V313 DKP # PP 022 WM | American Walnut
 OUTSIDE: MDF HMR E1 V313 DKP # 836 NCT | Anti-Fingerprint
 FRONTAGE: MDF HMR E1 V313 DKP # 836 NCT | Anti-Fingerprint
 HANDLE: Aluminum DKP #5230 | Ivory
 HANDLE: Aluminum DKP #5230 | Dark Choco
 TOP: Quartz Vadara G1 #V743 | Ostara Dawn
 FRONTAGE: Aluminum DKP #5158 (มีมือจับในตัว) | Dark Choco ,
 กระจกใส TYK | Euro Bronze 5 mm. (Tempered)

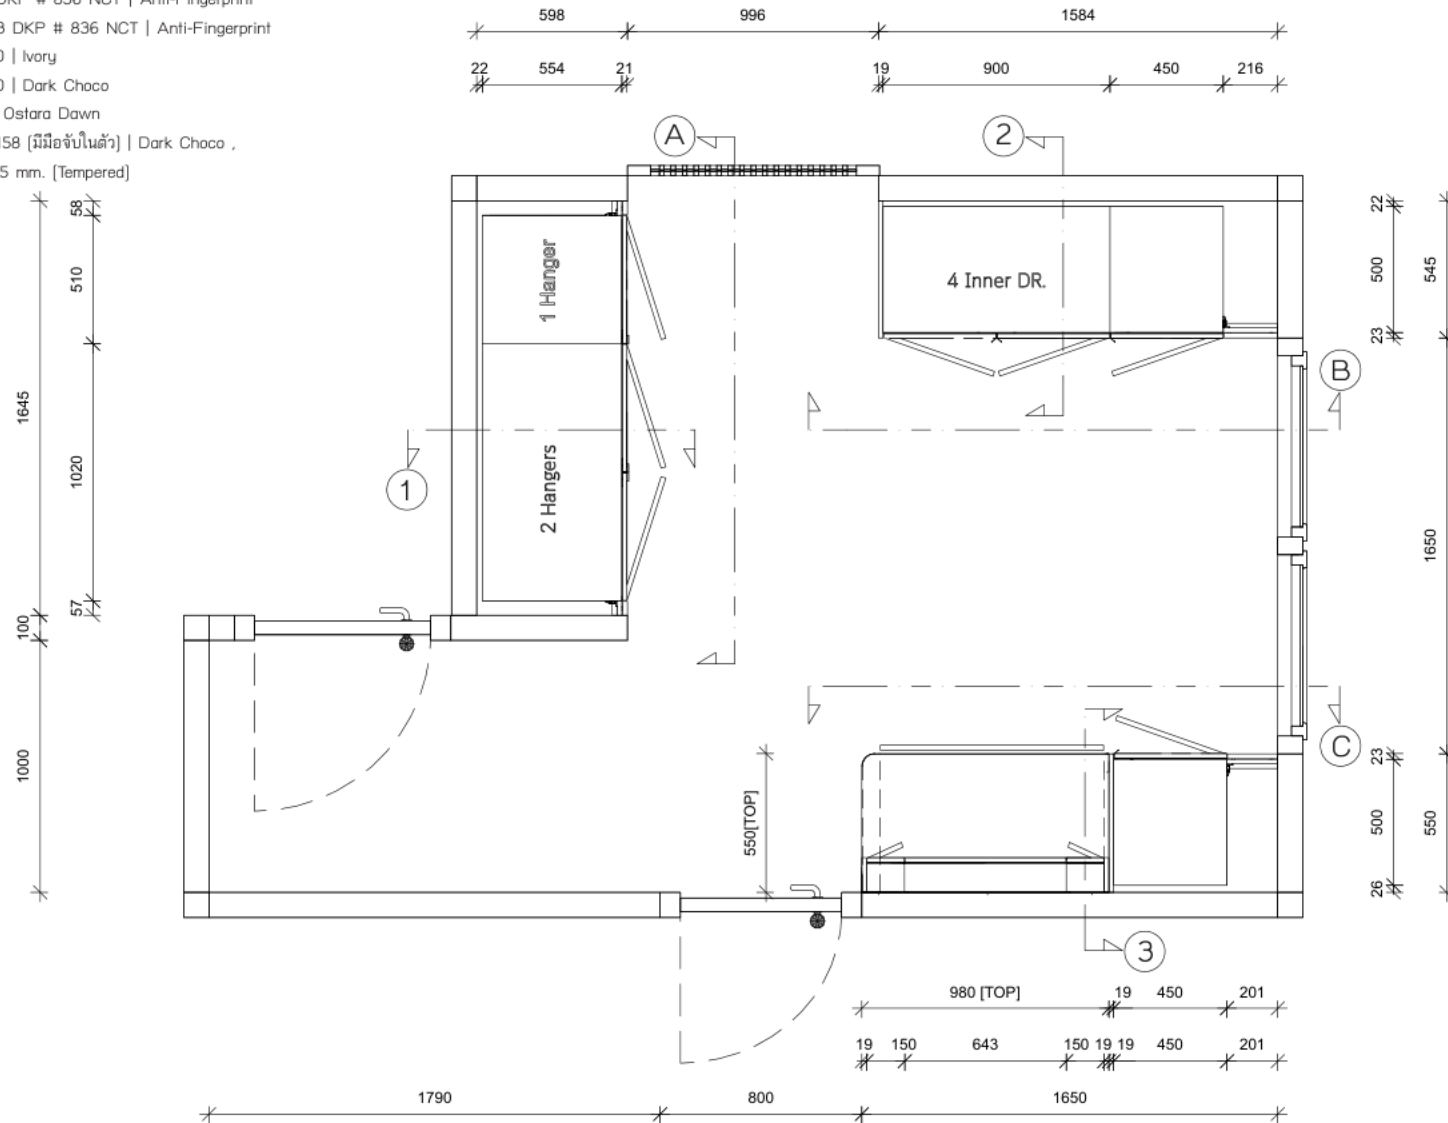

Handwritten signature and date:
 19-9-69

Dkbb

157 Praditmanutham Road
 Bangkapi Bangkok 10240
 TEL: 0-2515-1162 FAX: 0-2515-1161
 WWW.decorchoice.co.th

Client : Ari789

Address :

Province :-

Phone :

Design : Master Walk-In Closet - 4B

Series : Elegance

Drawn by : บริษัท สุนทรจามร

Email :


View : Plan

Scale : 1:30


Date : 10/9/2569

Page : 01

INSIDE: MDF HMR E1 V313 DKP # PP 022 WM | American Walnut
 OUTSIDE: MDF HMR E1 V313 DKP # 836 NCT | Anti-Fingerprint
 FRONTAGE: MDF HMR E1 V313 DKP # 836 NCT | Anti-Fingerprint
 HANDLE: Aluminum DKP #5230 | Ivory
 HANDLE: Aluminum DKP #5230 | Dark Choco
 TOP: Quartz Vadara G1 #V743 | Ostara Dawn
 FRONTAGE: Aluminum DKP #5158 (มีมือจับในตัว) | Dark Choco ,
 กรุกระจกใส TYK | Euro Bronze 5 mm. (Tempered)

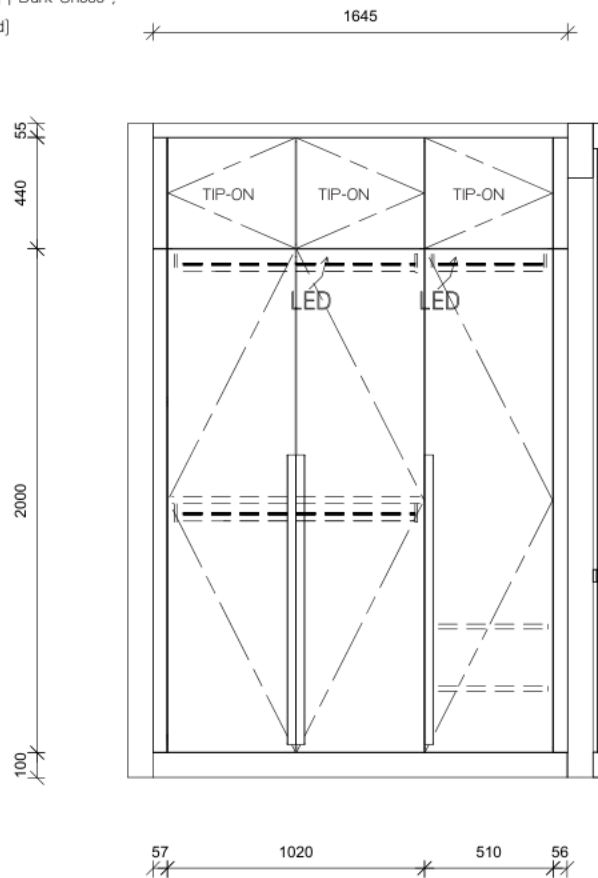

ELEVATION A

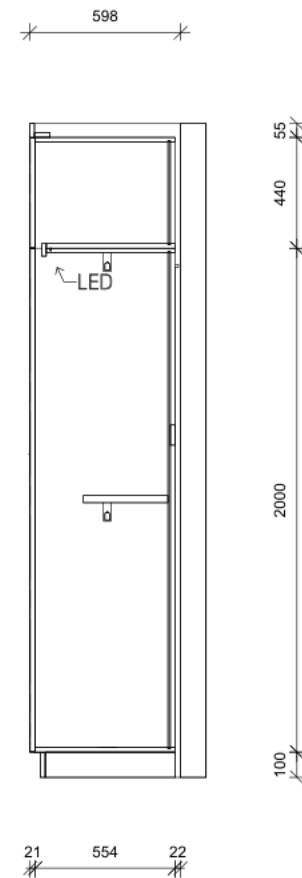

SECTION 1


 19-9-69

Dkbb

157 Praditmanutham Road
 Bangkapi Bangkok 10240
 TEL:0-2515-1162 FAX:0-2515-1161
 WWW.decorchoice.co.th

Client : Ari789

Address :

Province :-

Phone :

Design : Master Walk-In Closet - 4B

Series : Elegance

Drawn by : บริษัท สุนทรจามร

Email :


View : Elevation A , Section 1

Scale : 1:30


Date : 10/9/2569

Page : 02

INSIDE: MDF HMR E1 V313 DKP # PP 022 WM | American Walnut
 OUTSIDE: MDF HMR E1 V313 DKP # 836 NCT | Anti-Fingerprint
 FRONTAGE: MDF HMR E1 V313 DKP # 836 NCT | Anti-Fingerprint
 HANDLE: Aluminum DKP #5230 | Ivory
 HANDLE: Aluminum DKP #5230 | Dark Choco
 TOP: Quartz Vadara G1 #V743 | Ostara Dawn
 FRONTAGE: Aluminum DKP #5158 (มีมือจับในตัว) | Dark Choco ,
 กระจกใส TYK | Euro Bronze 5 mm. (Tempered)

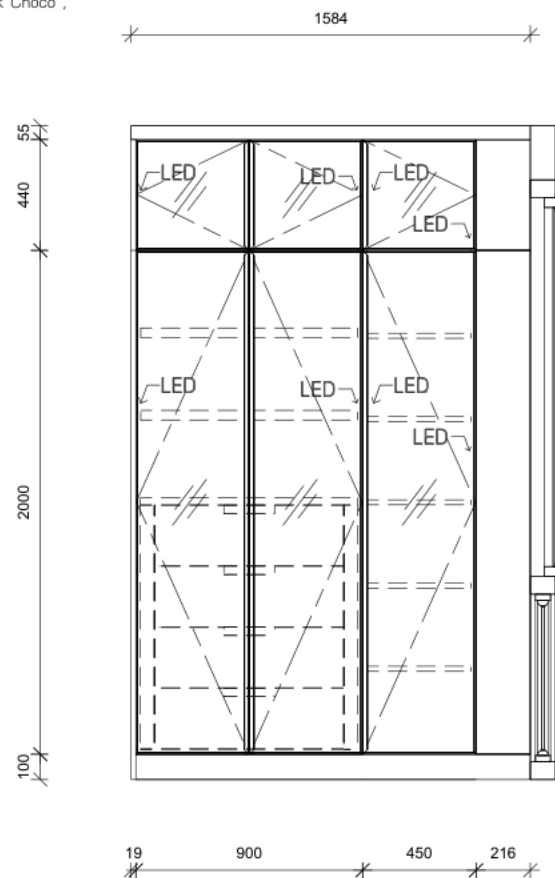

ELEVATION B

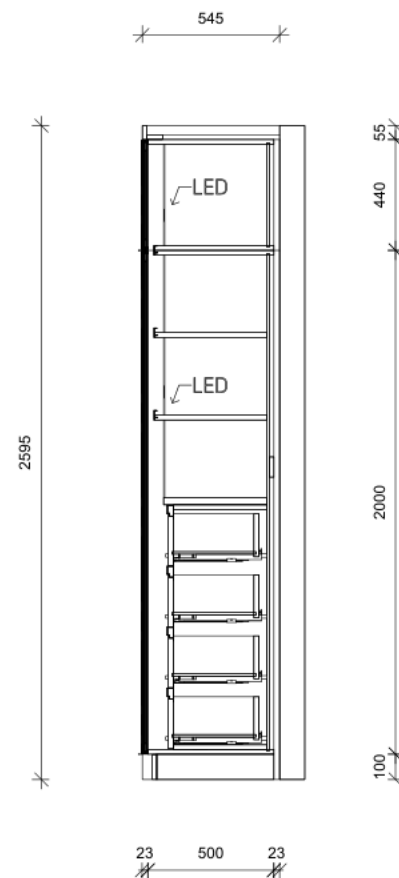

SECTION 2

Handwritten signature
 19-9-69

Dkbb

157 Praditmanutham Road
 Bangkapi Bangkok 10240
 TEL:0-2515-1162 FAX:0-2515-1161
 WWW.decorchoice.co.th

Client : Ari789

Address :

Province :-

Phone :

Design : Master Walk-In Closet - 4B

Series : Elegance

Drawn by : บริษัท สุนทรจามร

Email :


View : Elevation B , Section 2

Scale : 1:30


Date : 10/9/2569

Page : 03

INSIDE: MDF HMR E1 V313 DKP # PP 022 WM | American Walnut
 OUTSIDE: MDF HMR E1 V313 DKP # 836 NCT | Anti-Fingerprint
 FRONTAGE: MDF HMR E1 V313 DKP # 836 NCT | Anti-Fingerprint
 HANDLE: Aluminum DKP #5230 | Ivory
 HANDLE: Aluminum DKP #5230 | Dark Choco
 TOP: Quartz Vadara G1 #V743 | Ostara Dawn
 FRONTAGE: Aluminum DKP #5158 (มีมือจับในตัว) | Dark Choco ,
 กระจกเงา ใส TYK | Euro Bronze 5 mm. (Tempered)

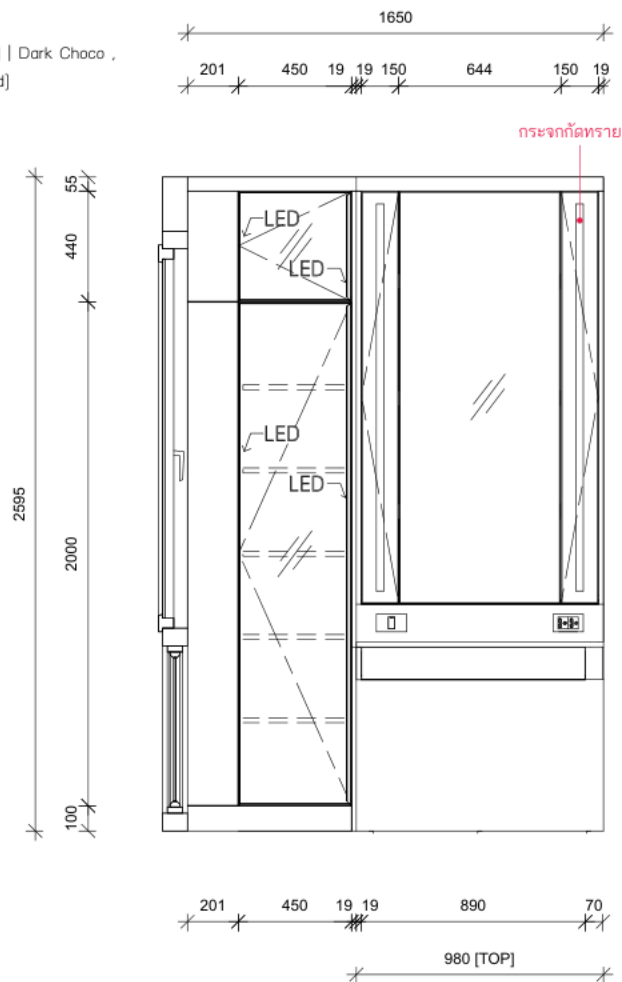

ELEVATION C

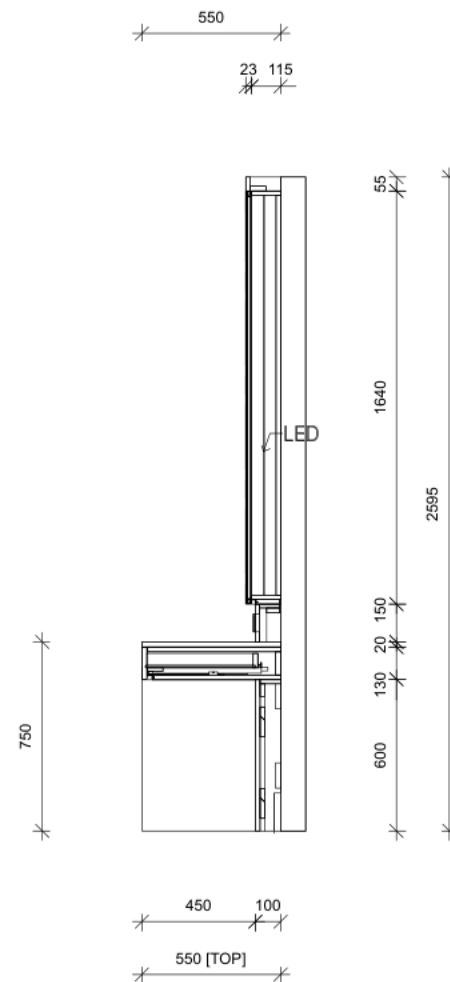

SECTION 3

Omaha
 19-9-69

Dkbb

157 Praditmanutham Road
 Bangkapi Bangkok 10240
 TEL:0-2515-1162 FAX:0-2515-1161
 WWW.decorchoice.co.th

Client : Ari789

Address :

Province :-

Phone :

Design : Master Walk-In Closet - 4B

Series : Elegance

Drawn by : บริษัท สุนทรจามร

Email :

View : Elevation C , Section 3

Scale : 1:30

Date : 10/9/2569

Page : 04