











INSIDE : DK Board Laminate DKBB #IAB 8101 | PLEASANT TEAK

OUTSIDE : DK Board Laminate FORMICA FENIX NTM #0748 | BEIGE ARIZONA

FRONTAGE : VI PLUS Laminate FORMICA FENIX NTM #0748 | BEIGE ARIZONA

ด้านหลังปิด Laminate PANAPLAST # S-B 28779PM | LATTE

TOP/BACK SPLASH : QUARTZ VADARA #V743 | OSTARA DAWN 20 mm.


HANDLE : ALUMINIUM PROFILE-C | ALUMINIUM

HANDLE : ALUMINIUM PROFILE-J | ALUMINIUM

HANDLE : HAFELE # 125.95.910

HANDLE : HAFELE #126.95.920

เสริมแข็ง : Ivory

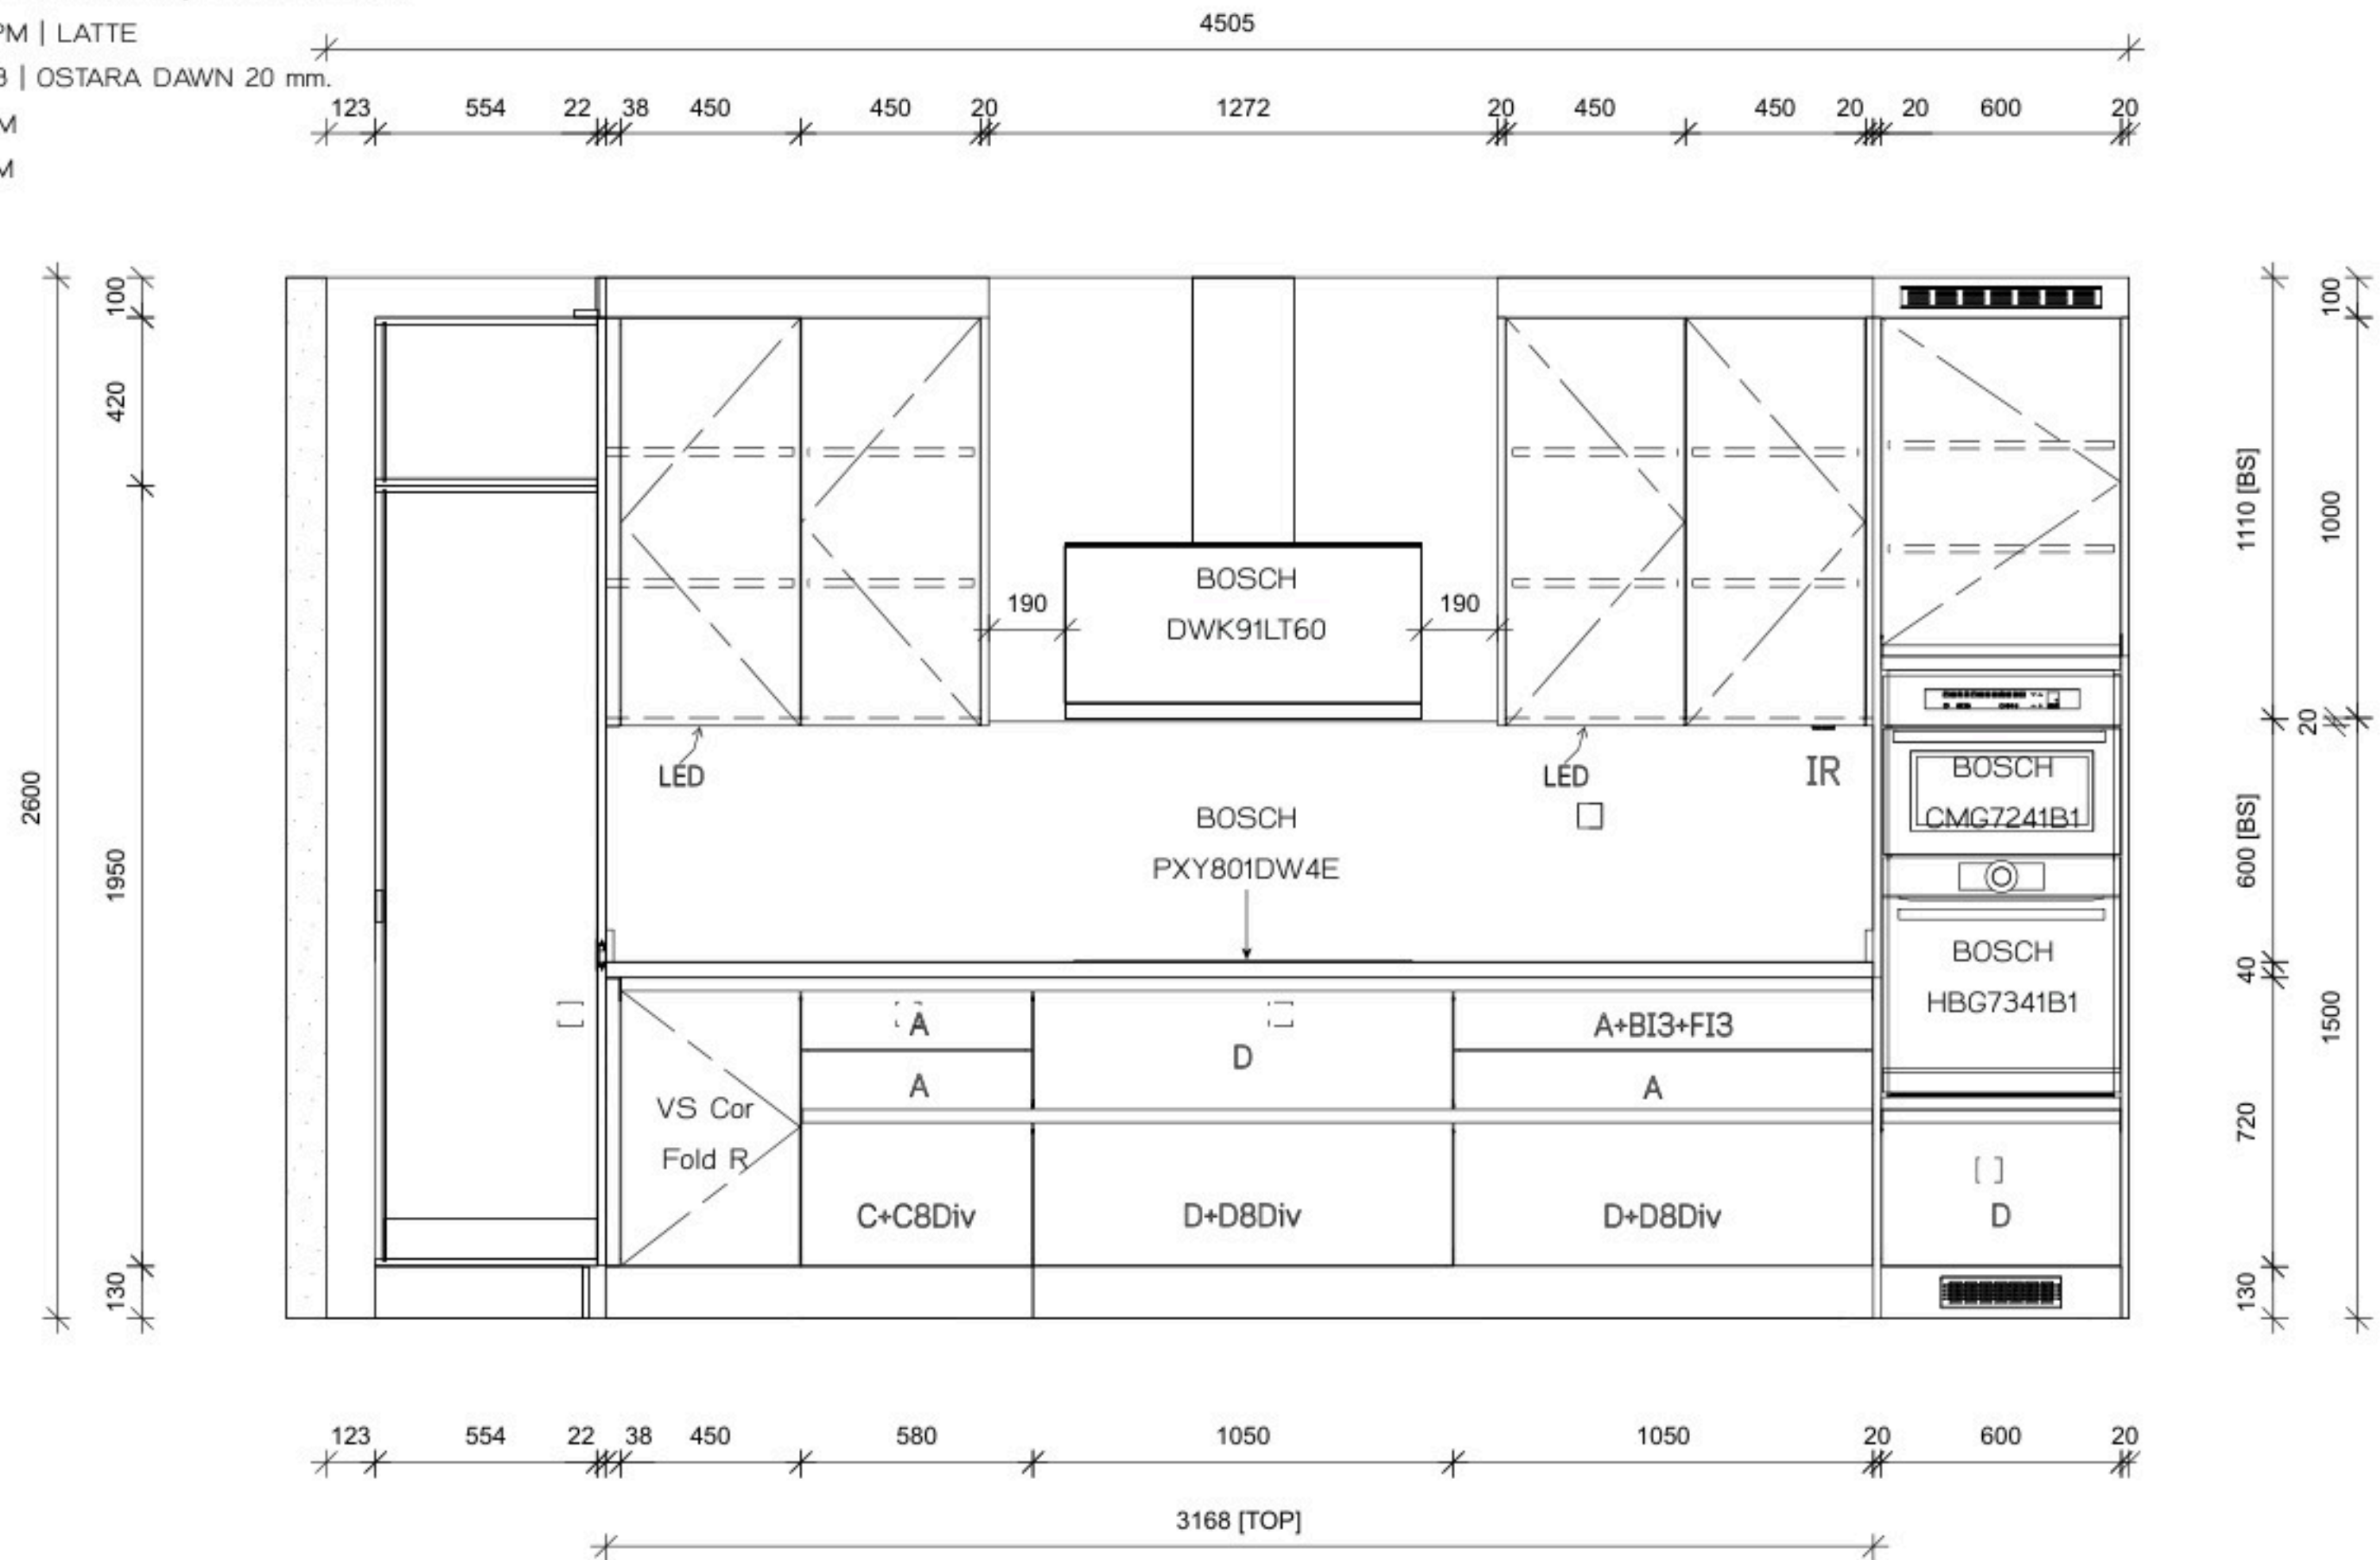

Dkbb[®]

157 Praditmanutham Road
Bangkapi Bangkok 10240

TEL:0-2515-1162 FAX:0-2515-1161
WWW.decorchoice.co.th

Client : ARI 789

Address :

Province :

Phone :

Design : Kitchen 5C

Series : Elegance Plus

Drawn by : บริษัท สุนทรจามร


Email :

View : Elevation A

Scale : 1:30

Date : 30/3/2569

Page : 02

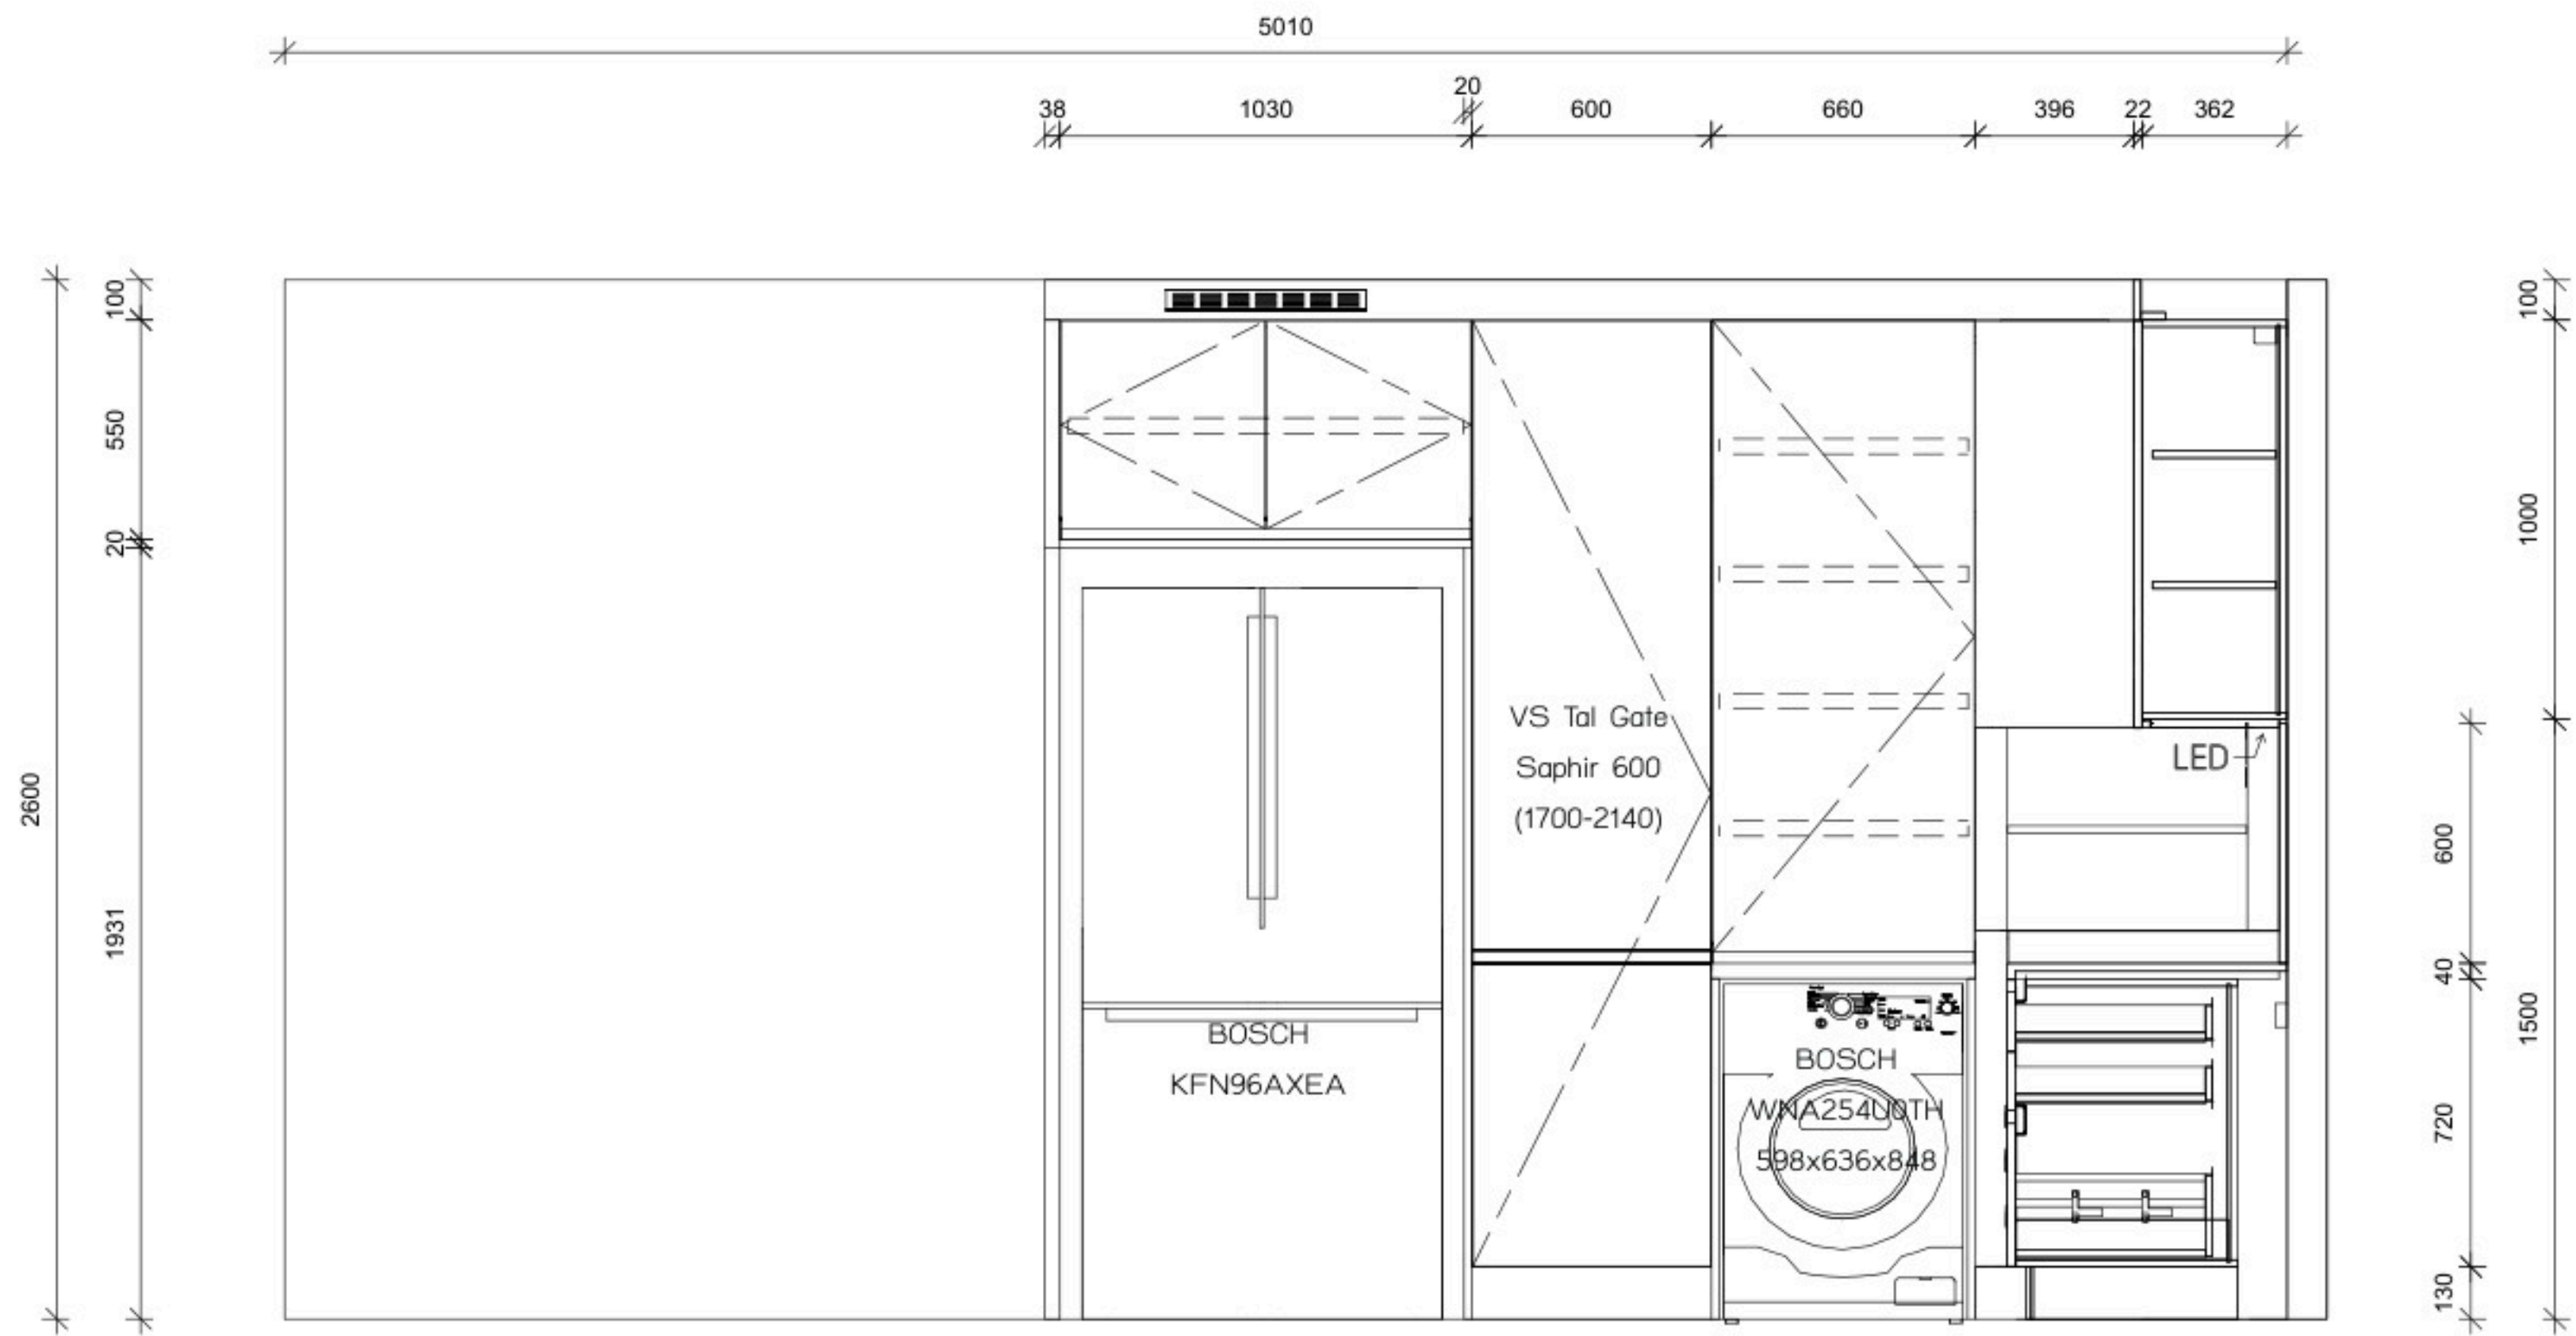

INSIDE : DK Board Laminate DKBB #IAB 8101 | PLEASANT TEAK

OUTSIDE : DK Board Laminate FORMICA FENIX NTM #0748 | BEIGE ARIZONA

FRONTAGE : VI PLUS Laminate FORMICA FENIX NTM #0748 | BEIGE ARIZONA

ด้านหลังปิด Laminate PANAPLAST # S-B 28779PM | LATTE

TOP/BACK SPLASH : QUARTZ VADARA #V743 | OSTARA DAWN 20 mm.

HANDLE : ALUMINIUM PROFILE-C | ALUMINIUM

HANDLE : ALUMINIUM PROFILE-J | ALUMINIUM

HANDLE : HAFELE # 125.95.910

HANDLE : HAFELE #126.95.920

เสริมแข็ง : Ivory

Dkbb

157 Praditmanutham Road
Bangkapi Bangkok 10240

TEL:0-2515-1162 FAX:0-2515-1161
WWW.decorchoice.co.th

Client : ARI 789

Address :

Province :

Phone :

Design : Kitchen 5C

Series : Elegance Plus

Drawn by : บริวัตร สุนทรจามร

Email :


View : Elevation B

Scale : 1:30


Date : 30/3/2569

Page : 03



INSIDE : DK Board Laminate DKBB #IAB 8101 | PLEASANT TEAK
OUTSIDE : DK Board Laminate FORMICA FENIX NTM #0748 | BEIGE ARIZONA
FRONTAGE : VI PLUS Laminate FORMICA FENIX NTM #0748 | BEIGE ARIZONA
ด้านหลังปิด Laminate PANAPLAST # S-B 28779PM | LATTE
TOP/BACK SPLASH : QUARTZ VADARA #V743 | OSTARA DAWN 20 mm.
HANDLE : ALUMINIUM PROFILE-C | ALUMINIUM
HANDLE : ALUMINIUM PROFILE-J | ALUMINIUM
HANDLE : HAFELE # 125.95.910
HANDLE : HAFELE #126.95.920
เสริมแข็ง : Ivory

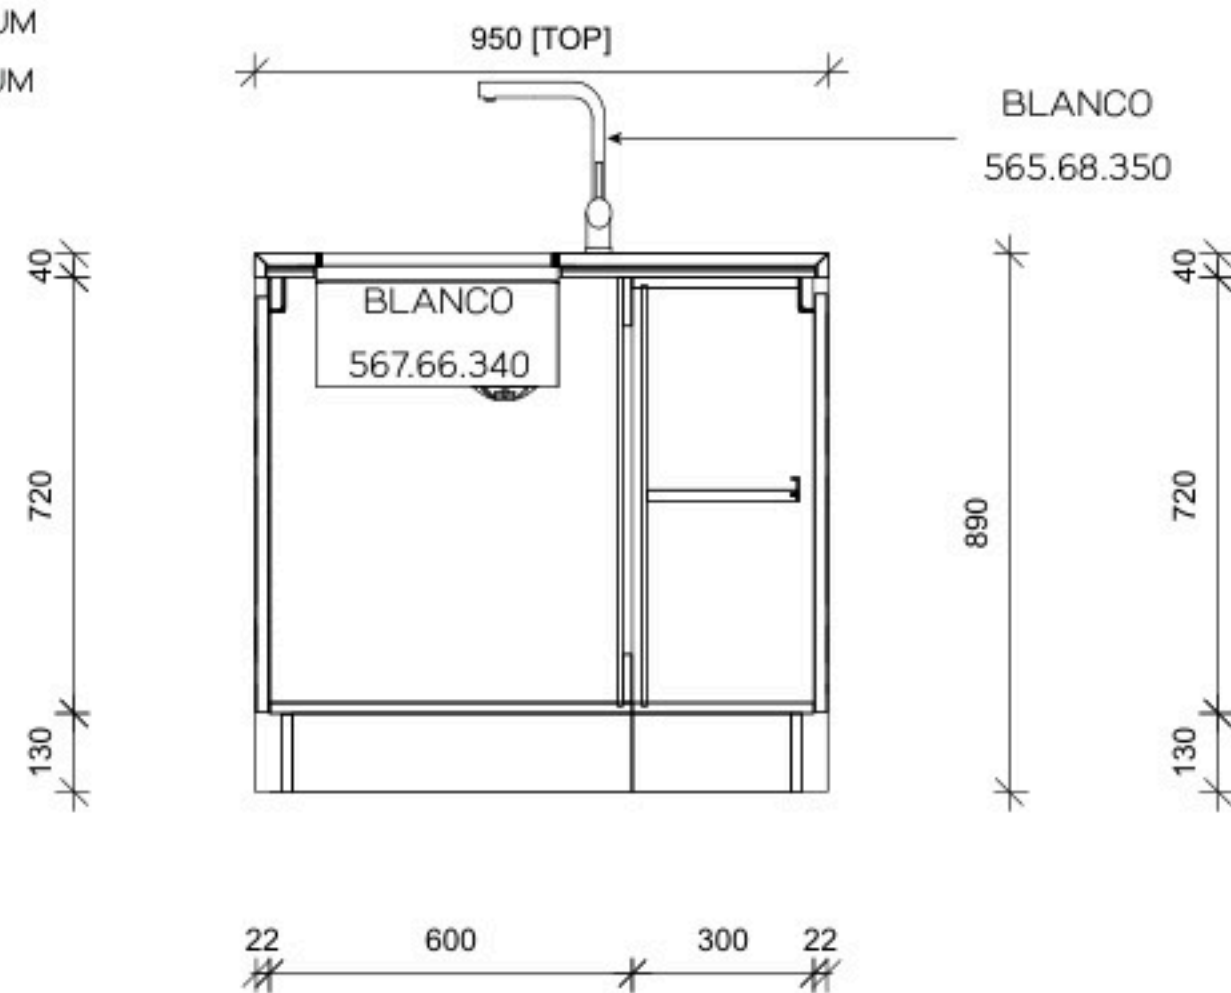

SECTION 1

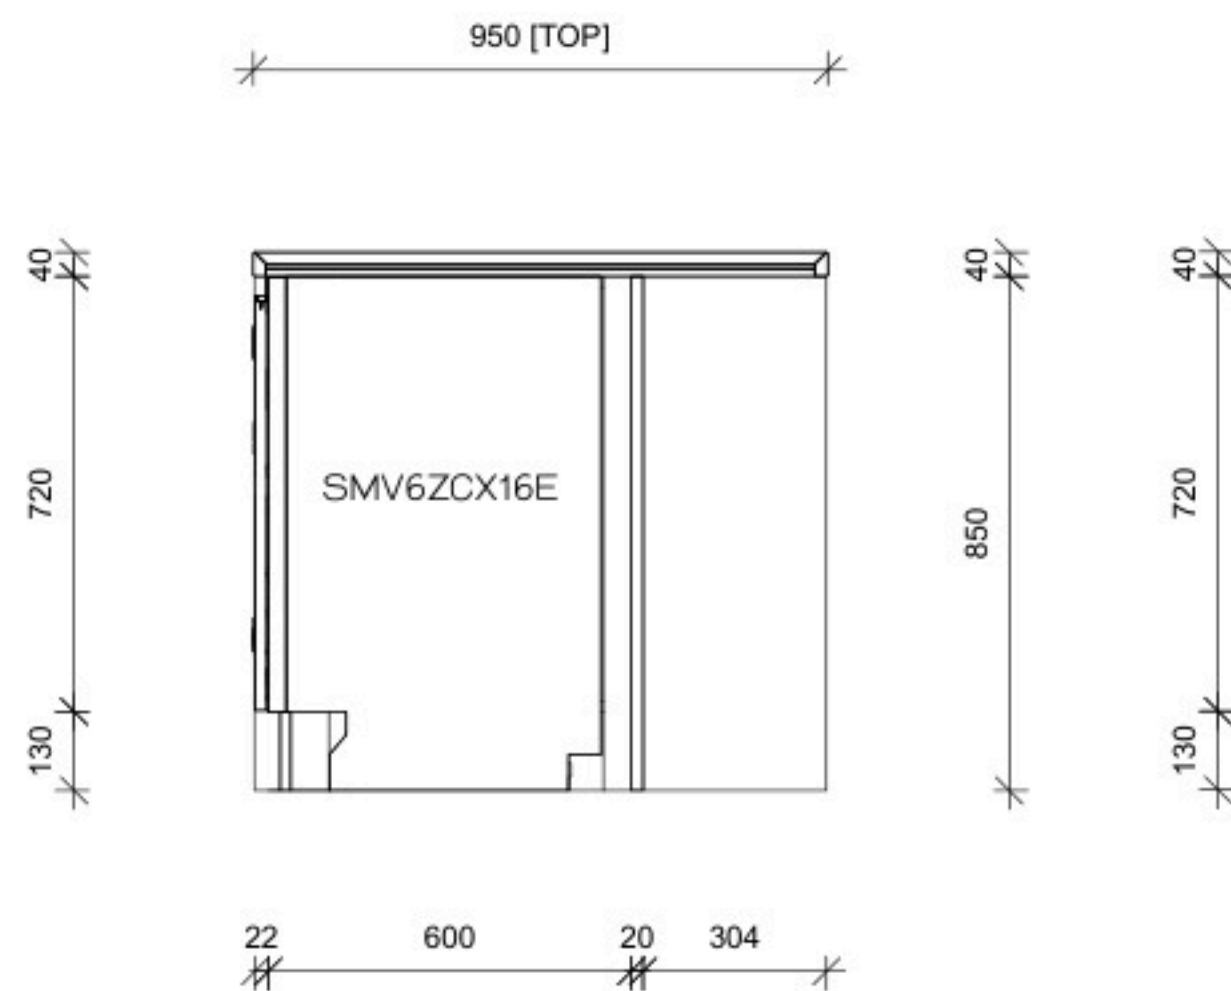

SECTION 2

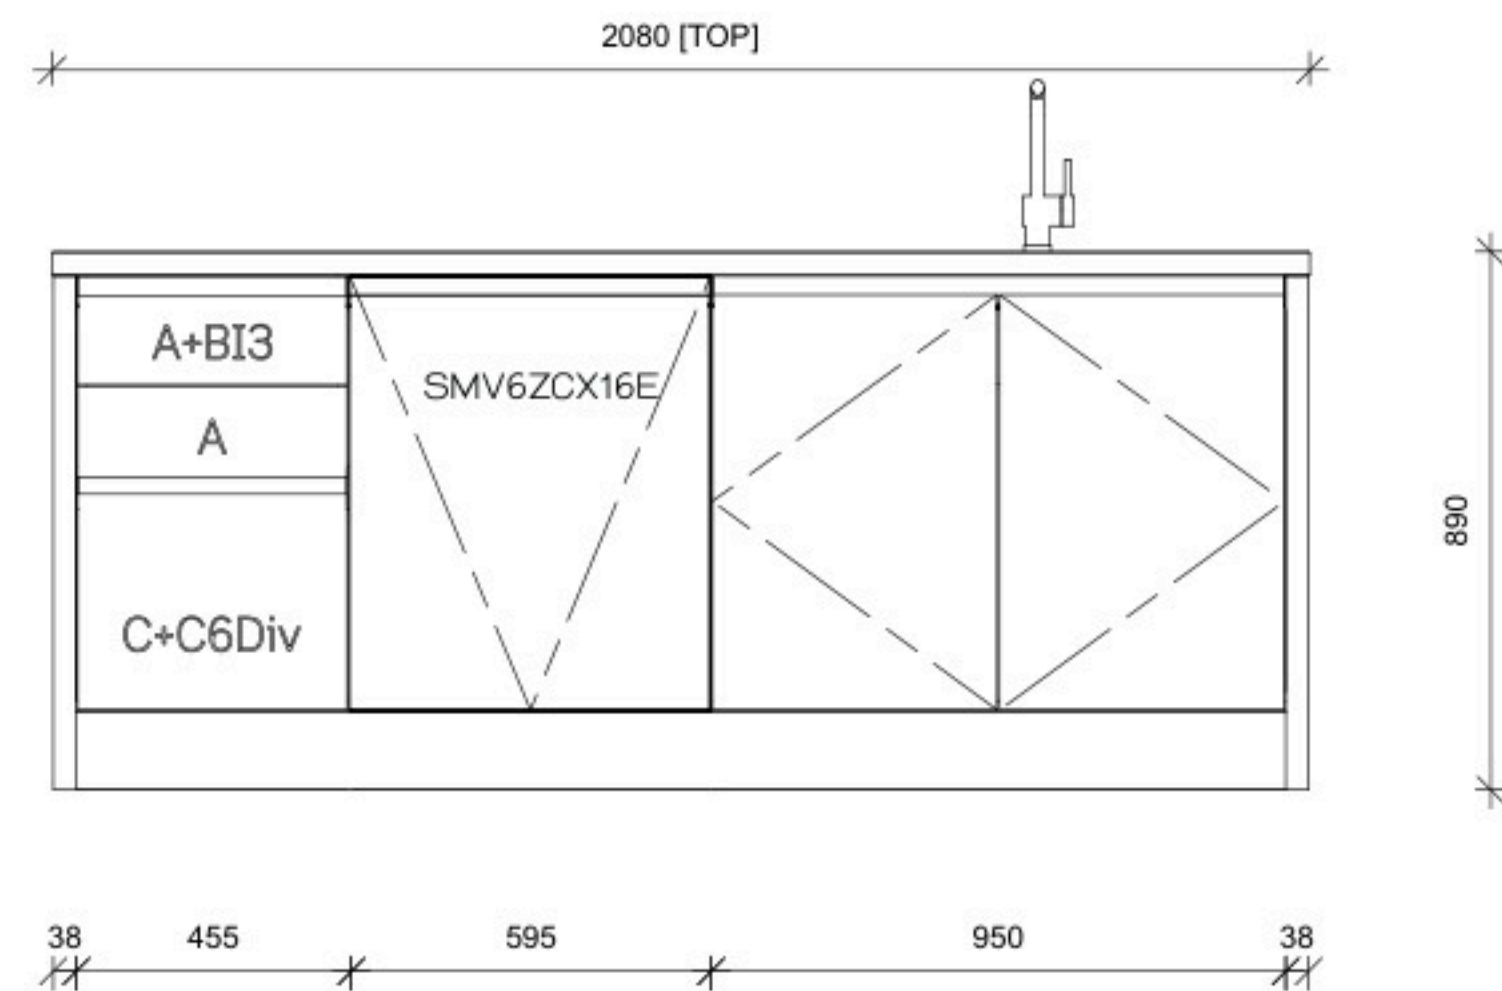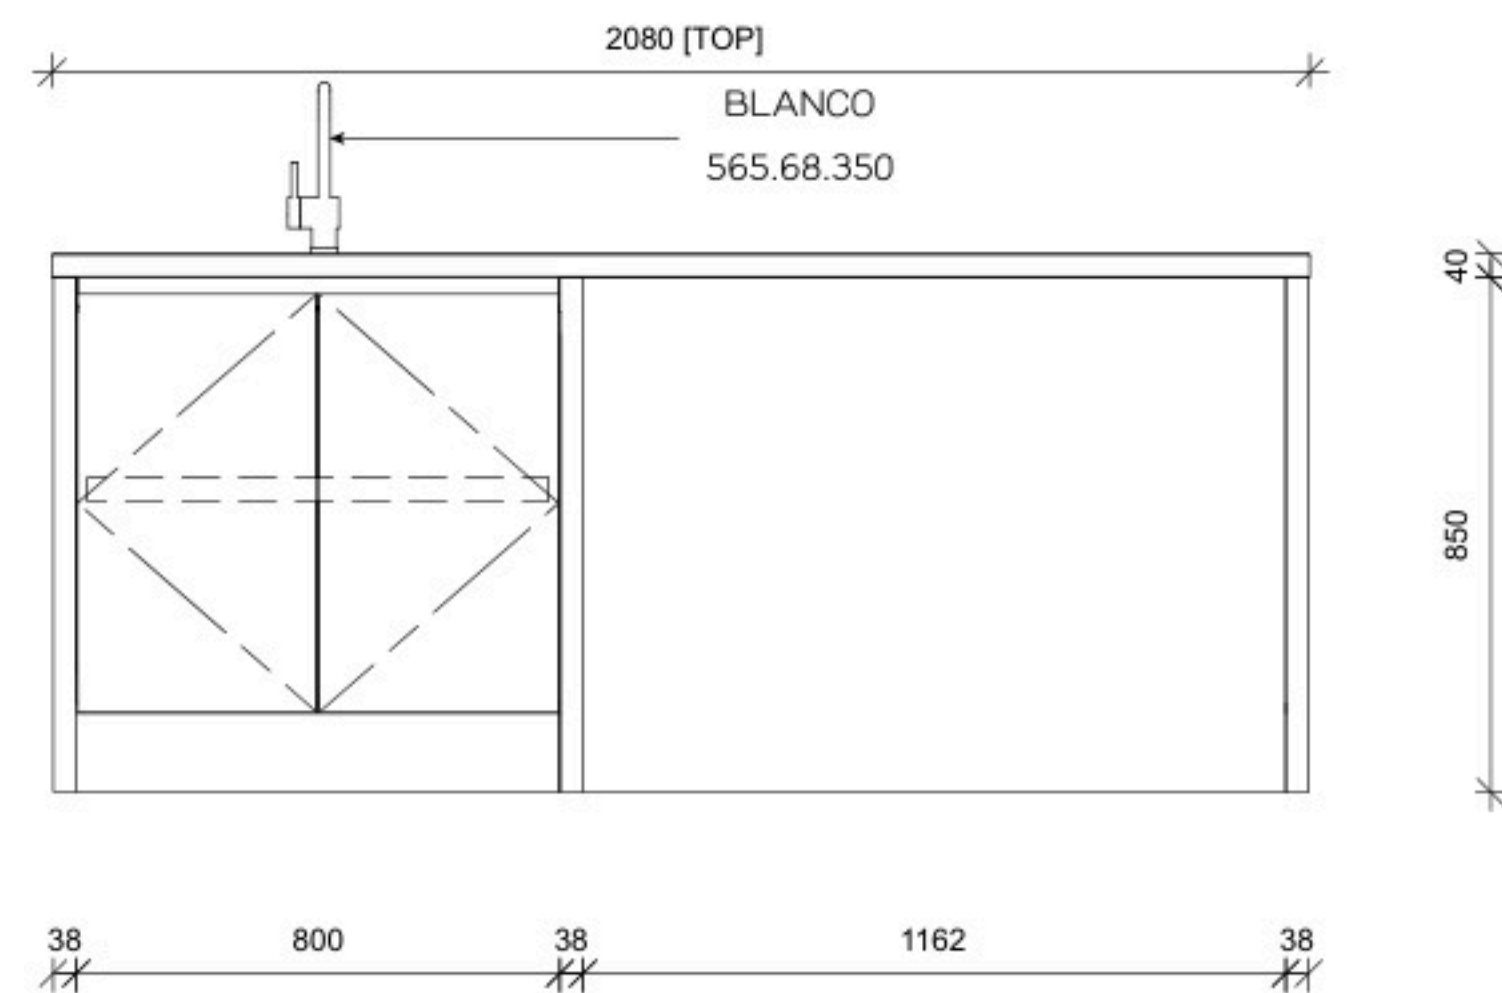

Dkbb®

157 Praditmanutham Road
Bangkapi Bangkok 10240
TEL:0-2515-1162 FAX:0-2515-1161
WWW.decorchoice.co.th

Client : ARI 789	Design : Kitchen 5C	View : Island
Address :	Series : Elegance Plus	Scale : 1:25
Province :	Drawn by : บริวัตร สุนทรจามร	Date : 30/3/2569
Phone :	Email :	Page : 04