


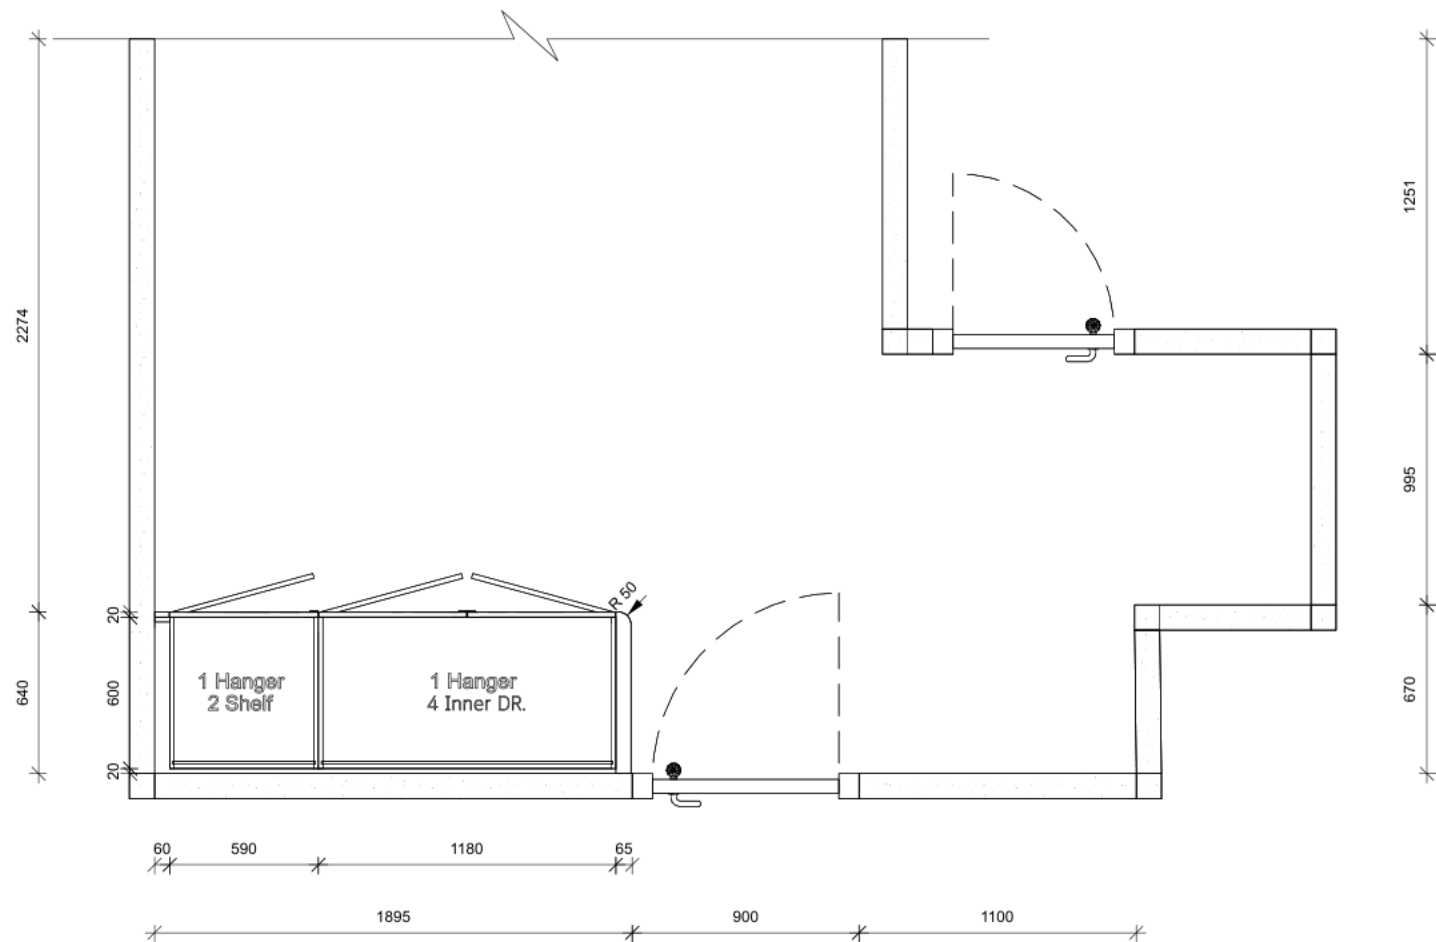


Dkbb

157 Praditmanutham Road
Bangkapi Bangkok 10240
TEL: 0-2515-1162 FAX: 0-2515-1161
WWW.decorchoice.co.th

Client : ARI789	Design : Bedroom 2 - Walk in 4B	View : Plan
Address :	Series : Elegance	Scale : 1:30
Province :-	Drawn by : Sunisa	Date : 20/6/2569
Phone :	Email :	Page : 01

INSIDE: MDF HMR E1 V313 DKP # PP 022 WM | American Walnut
 OUTSIDE: MDF HMR E1 V313 DKP # 836 NCT | Anti-Fingerprint
 FRONTAGE: MDF HMR E1 V313 DKP # 836 NCT | Anti-Fingerprint
 HANDLE: Aluminum DKP #5230 | Ivory
 HANDLE: Aluminum DKP #5230 | Dark Choco

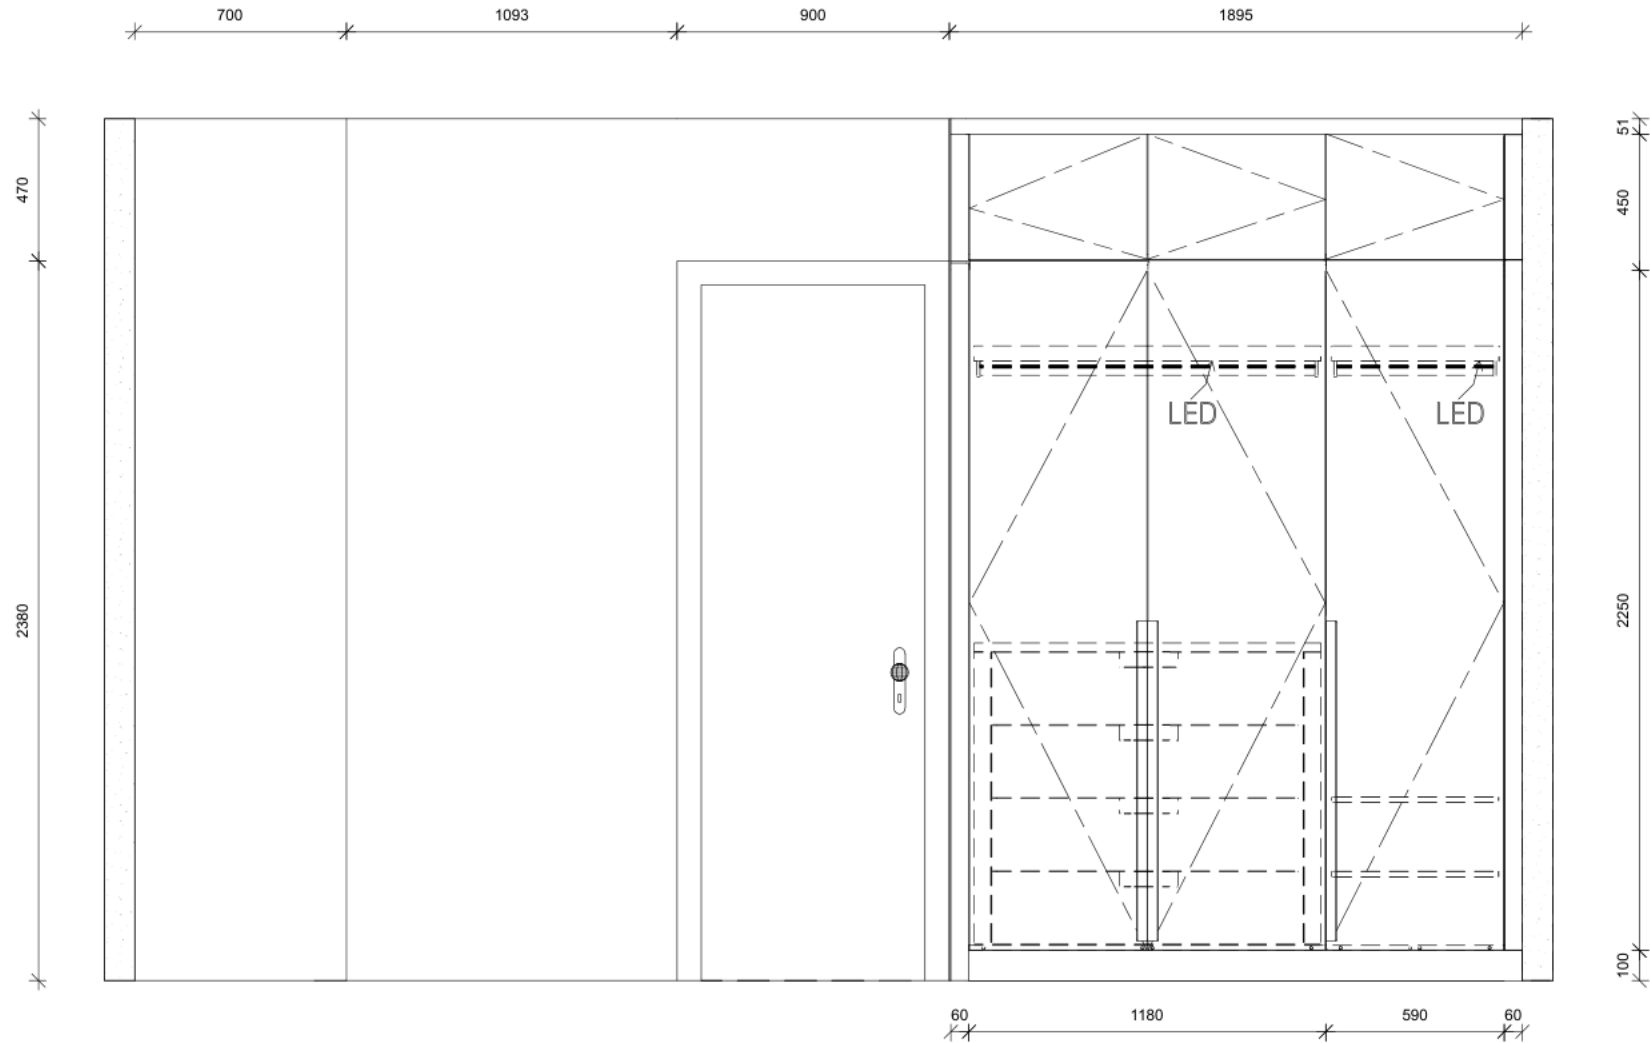


Dkbb

157 Praditmanutham Road
 Bangkapi Bangkok 10240
 TEL: 0-2515-1162 FAX: 0-2515-1161
 WWW.decorchoice.co.th

Client : ARI789	Design : Bedroom 2 - Walk in 4B	View : Elevation A
Address :	Series : Elegance	Scale : 1:25
Province :-	Drawn by : Sunisa	Date : 20/6/2569
Phone :	Email :	Page : 02


INSIDE: MDF HMR E1 V313 DKP # PP 022 WM | American Walnut
 OUTSIDE: MDF HMR E1 V313 DKP # 836 NCT | Anti-Fingerprint
 FRONTAGE: MDF HMR E1 V313 DKP # 836 NCT | Anti-Fingerprint
 HANDLE: Aluminum DKP #5230 | Ivory
 HANDLE: Aluminum DKP #5230 | Dark Choco

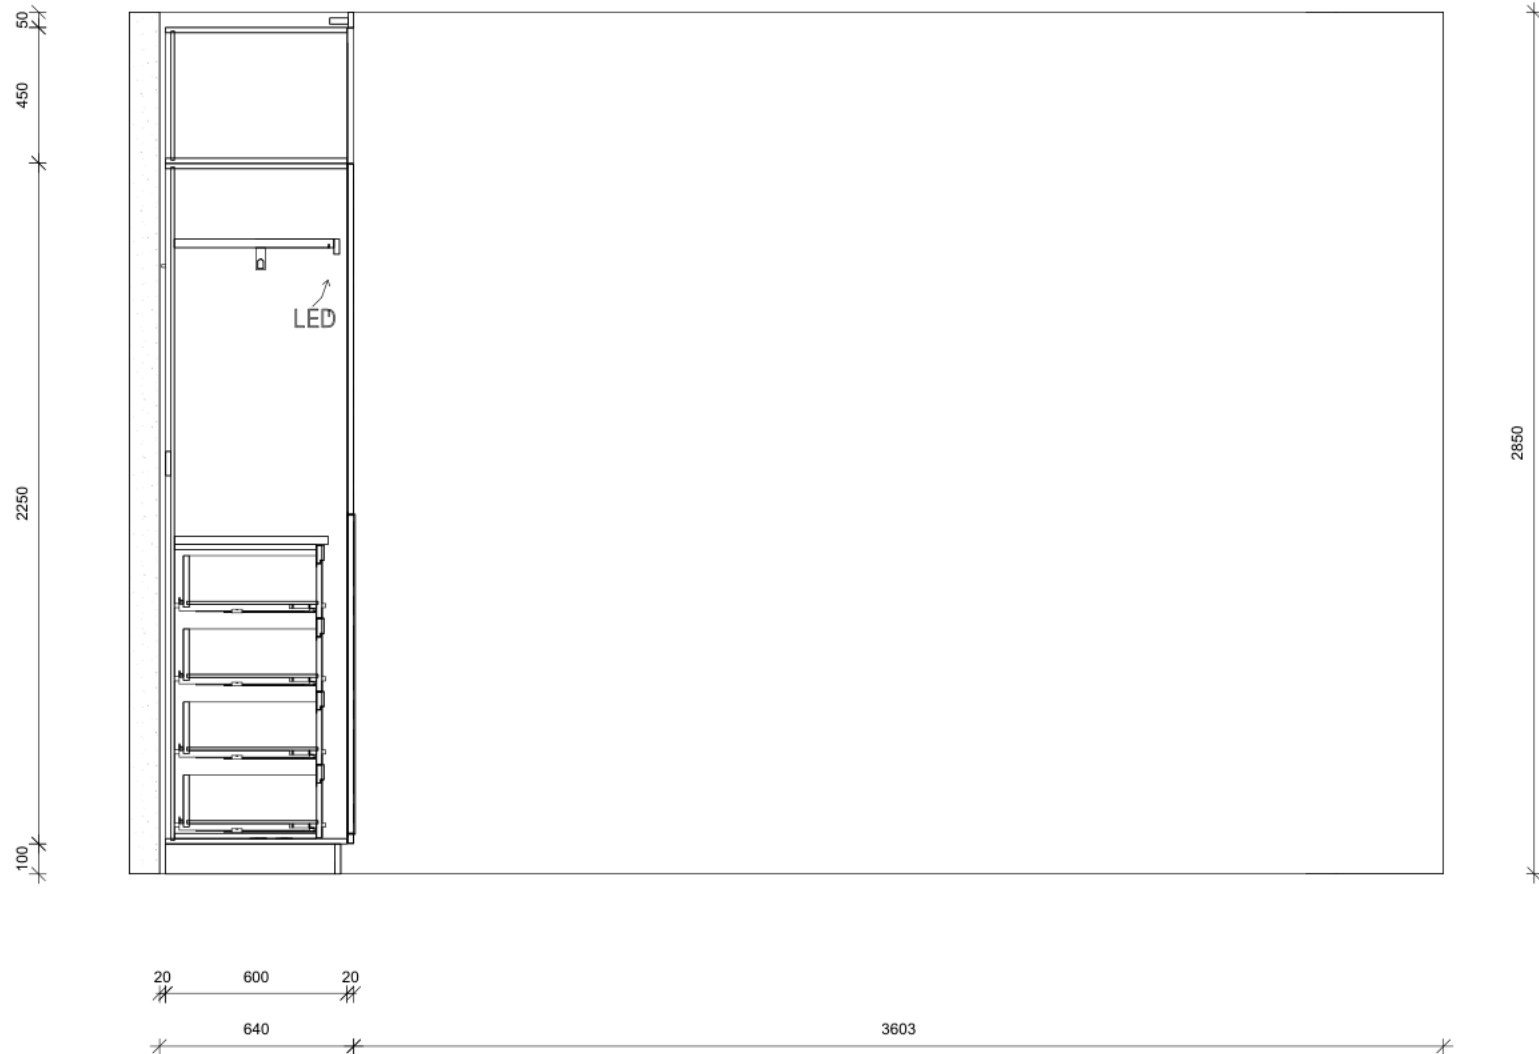

Dkbb

157 Praditmanutham Road
 Bangkapi Bangkok 10240
 TEL:0-2515-1162 FAX:0-2515-1161
 WWW.decorchoice.co.th

Client : ARI789	Design : Bedroom 2 - Walk in 4B	View : Section 1
Address :	Series : Elegance	Scale : 1:25
Province :-	Drawn by : Sunisa	Date : 20/6/2569
Phone :	Email :	Page : 03

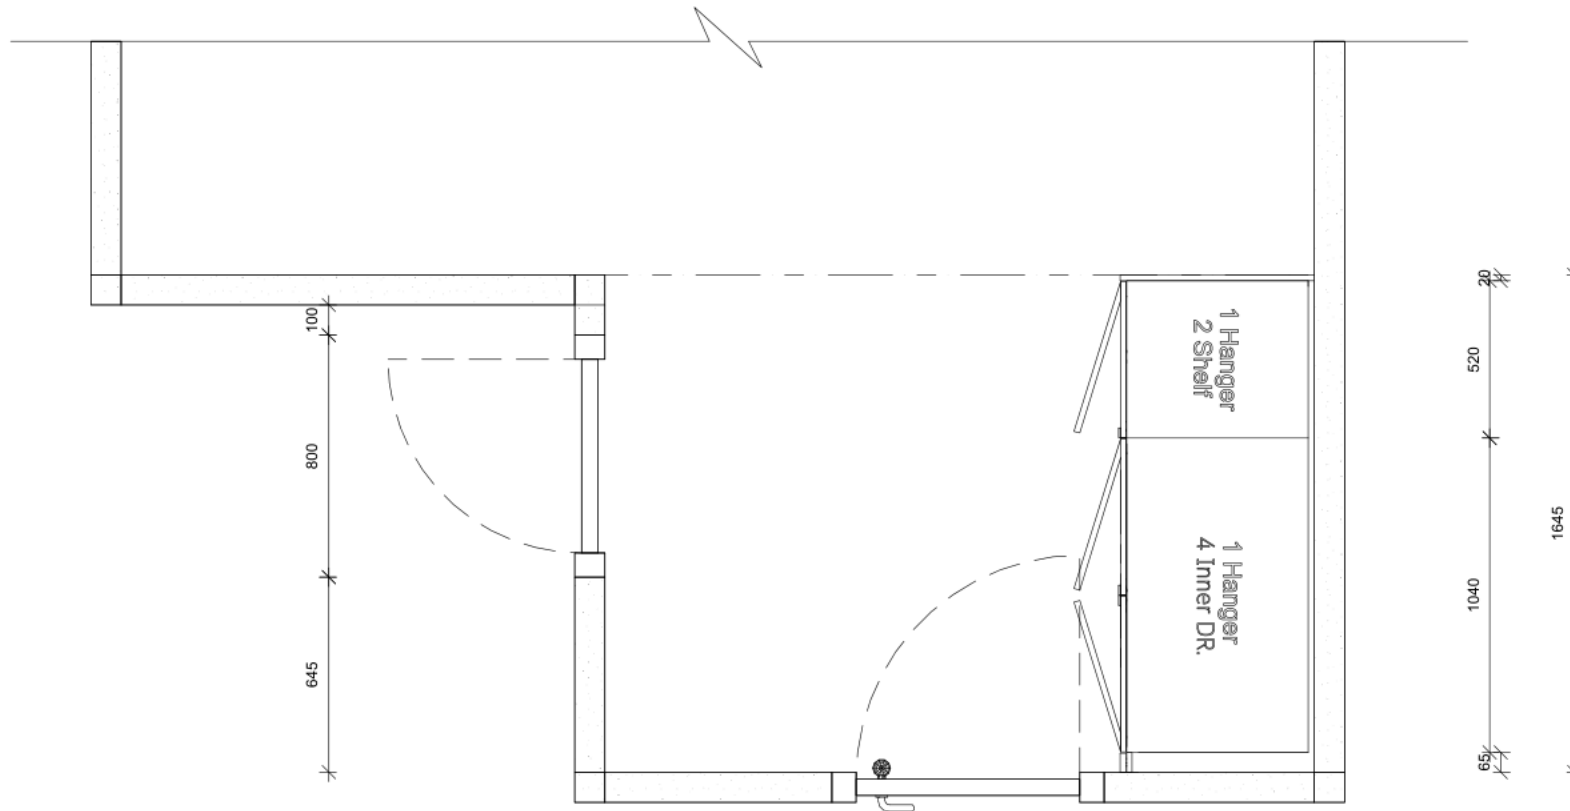

INSIDE: MDF HMR E1 V313 DKP # PP 022 WM | American Walnut

OUTSIDE: MDF HMR E1 V313 DKP # 836 NCT | Anti-Fingerprint

FRONTAGE: MDF HMR E1 V313 DKP # 836 NCT | Anti-Fingerprint


HANDLE: Aluminum DKP #5230 | Ivory

HANDLE: Aluminum DKP #5230 | Dark Choco

TOP: Vadara #G1 V743 | Ostara Dawn

FRONTAGE: Aluminum MEBEL (มีมือจับในตัว) | Dark Choco , กระจกใส TYK

| Euro Bronze 5 mm.

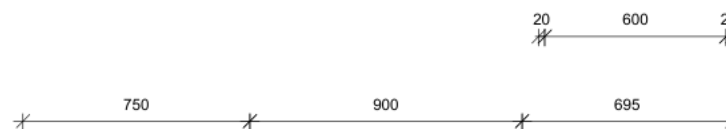

Dkbb

157 Praditmanutham Road
Bangkapi Bangkok 10240
TEL:0-2515-1162 FAX:0-2515-1161
WWW.decorchoice.co.th

Client : ARI789

Address :

Province :-

Phone :

Design : Bedroom 1 - Walk in 4B

Series : Elegance

Drawn by : Sunisa

Email :


View : Plan

Scale :1:25

Date : 11/6/2569

Page : 01

INSIDE: MDF HMR E1 V313 DKP # PP 022 WM | American Walnut
 OUTSIDE: MDF HMR E1 V313 DKP # 836 NCT | Anti-Fingerprint
 FRONTAGE: MDF HMR E1 V313 DKP # 836 NCT | Anti-Fingerprint
 HANDLE: Aluminum DKP #5230 | Ivory
 HANDLE: Aluminum DKP #5230 | Dark Choco
 TOP: Vadara #G1 V743 | Ostara Dawn
 FRONTAGE: Aluminum MEBEL [มีมือจับในตัว] | Dark Choco
 ,กรุกระจกใส TYK | Euro Bronze 5 mm.

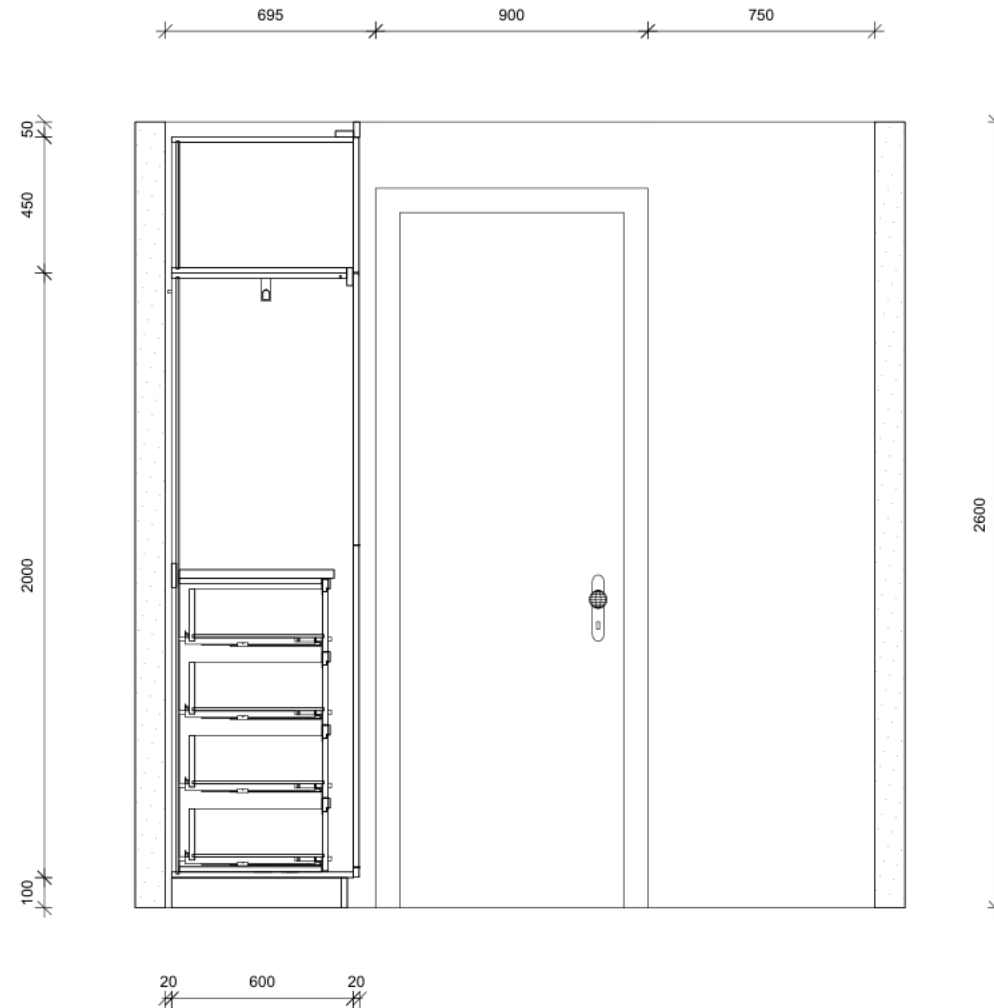

Dkbb

157 Praditmanutham Road
 Bangkapi Bangkok 10240
 TEL:0-2515-1162 FAX:0-2515-1161
 WWW.decorchoice.co.th

Client : ARI789	Design : Bedroom 1 - Walk in 4B	View : Section 1
Address :	Series : Elegance	Scale : 1:25
Province :-	Drawn by : Sunisa	Date : 11/6/2569
Phone :	Email :	Page : 03