



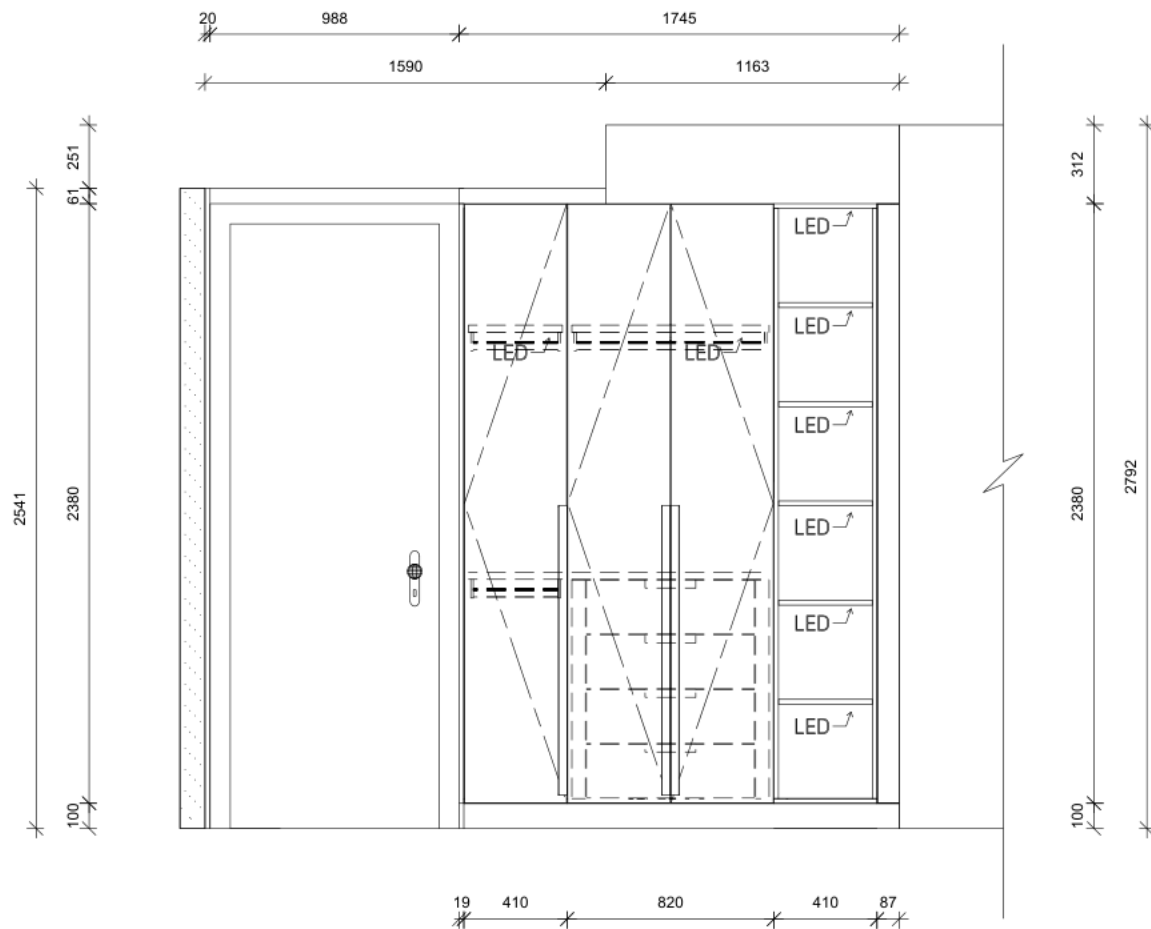

ELEVATION A

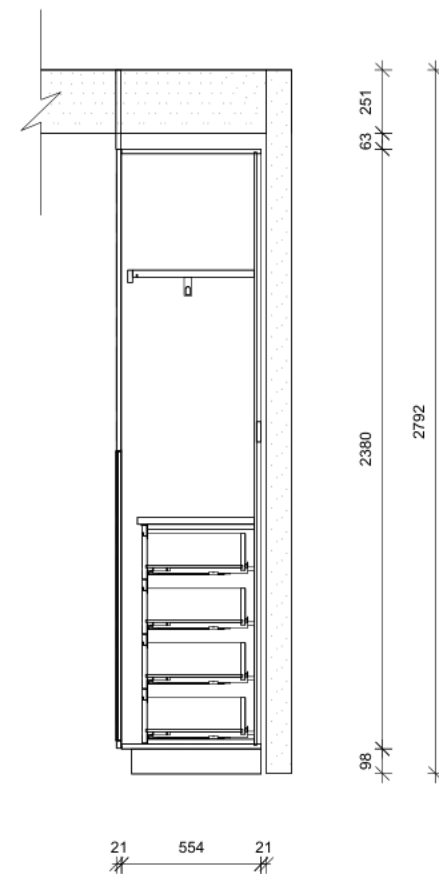

SECTION 1

Dkbb

157 Praditmanutham Road
Bangkapi Bangkok 10240
TEL:0-2515-1162 FAX:0-2515-1161
WWW.decorchoice.co.th

Client : Ari789	Design : WIC1-4C	View : Elevation A , Section 1
Address :	Series : Elegance	Scale : 1:30
Province :	Drawn by : บริษัท สุนทรจามร	Date : 19/9/2569
Phone :	Email :	Page : 02

INSIDE: MDF HMR E1 V313 DKP # PP 022 WM | American Walnut

OUTSIDE: MDF HMR E1 V313 DKP # 836 NCT | Anti-Fingerprint

FRONTAGE: MDF HMR E1 V313 DKP # 836 NCT | Anti-Fingerprint

HANDLE: Aluminum DKP #5230 | Ivory

HANDLE: Aluminum DKP #5230 | Dark Choco


TOP: Quartz Vadara G1 #V743 | Ostara Dawn

FRONTAGE: Aluminum DKP #5158 (มีมือจับในตัว) | Dark Choco ,

กรุกระจก ใส TYK | Euro Bronze 5 mm. (Tempered)

MIRROR: Aluminum DKP #5158 (มีมือจับในตัว) | Ivory ,

กรุกระจกเงา TYK 5 mm.

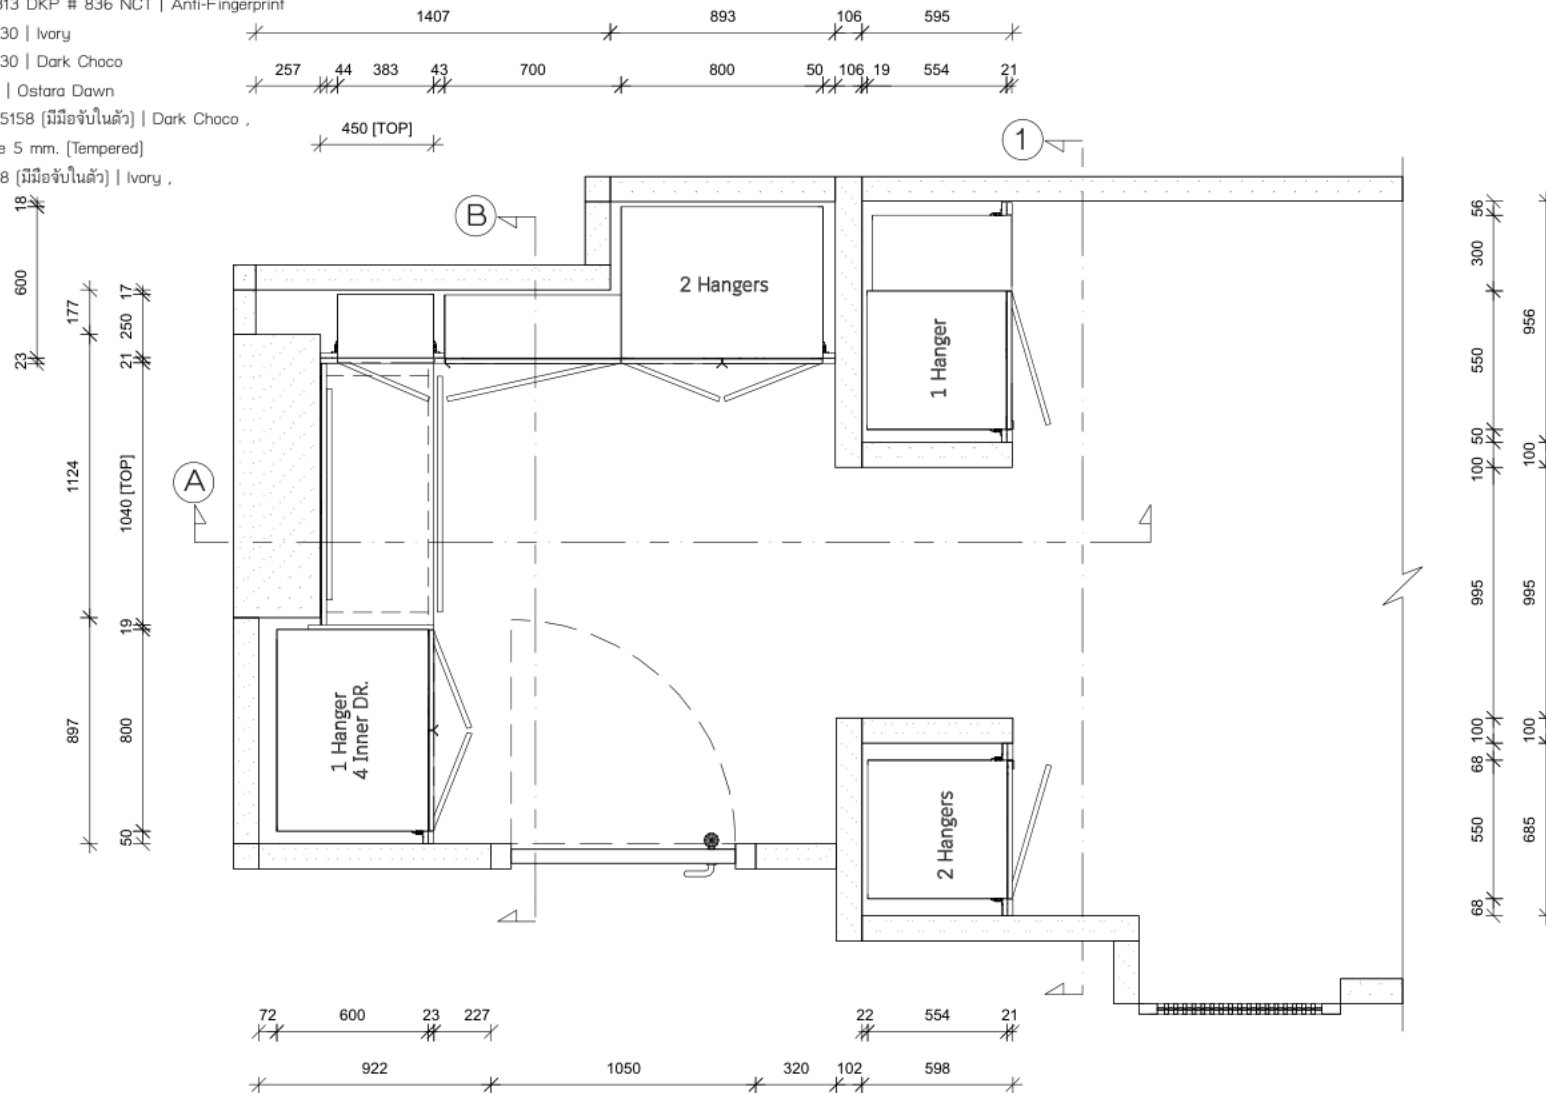


Dkbb

157 Praditmanutham Road
Bangkapi Bangkok 10240
TEL:0-2515-1162 FAX:0-2515-1161
WWW.decorchoice.co.th


Client : Ari789	Design : WICMB-4C	View : Plan
Address :	Series : Elegance	Scale : 1:30
Province :	Drawn by : บริษัท สุนทรจามร	Date : 22/9/2569
Phone :	Email :	Page : 01

INSIDE: MDF HMR E1 V313 DKP # PP 022 WM | American Walnut
 OUTSIDE: MDF HMR E1 V313 DKP # 836 NCT | Anti-Fingerprint
 FRONTAGE: MDF HMR E1 V313 DKP # 836 NCT | Anti-Fingerprint
 HANDLE: Aluminum DKP #5230 | Ivory
 HANDLE: Aluminum DKP #5230 | Dark Choco
 TOP: Quartz Vadara G1 #V743 | Ostara Dawn

FRONTAGE: Aluminum DKP #5158 (มีมือจับในตัว) | Dark Choco ,
 กรูกระຈก ใต TYK | Euro Bronze 5 mm. [Tempered]
 MIRROR: Aluminum DKP #5158 (มีมือจับในตัว) | Ivory ,
 กรูกระຈกเงา TYK 5 mm.

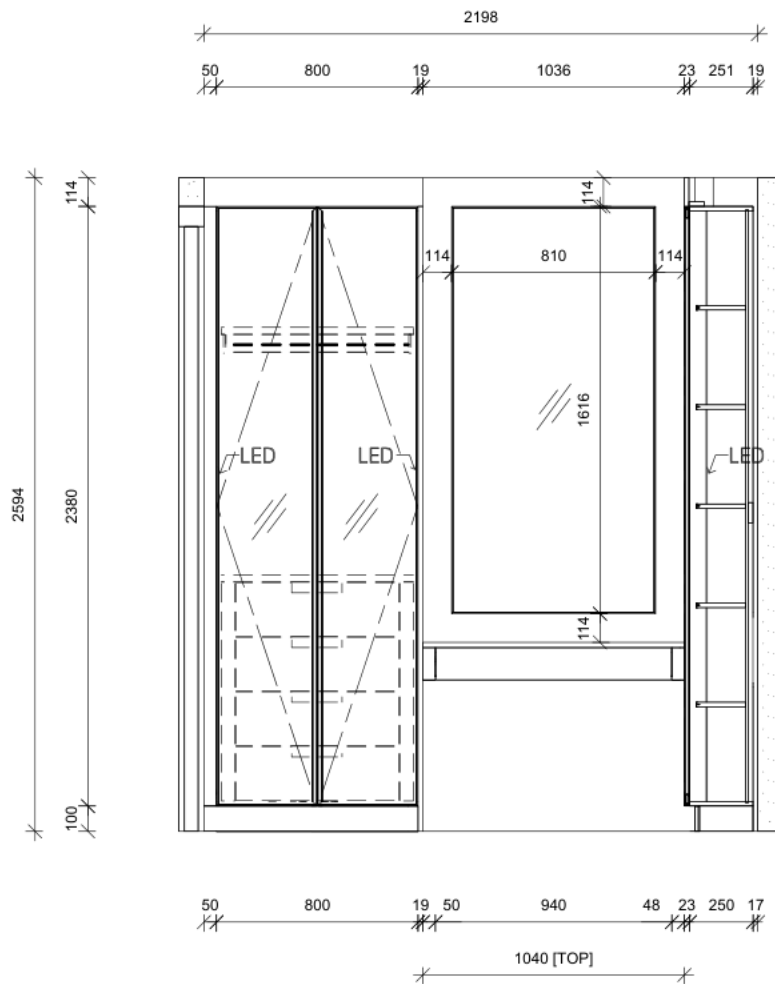

ELEVATION A

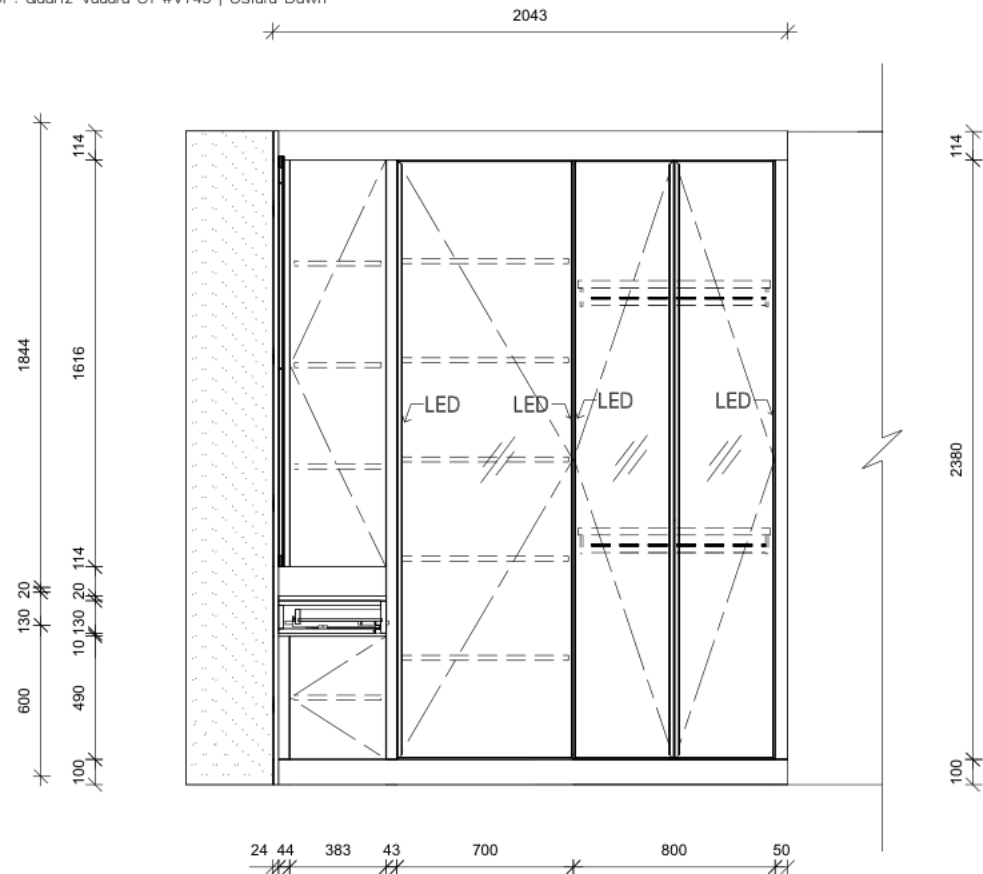


ELEVATION B

Dkbb

157 Praditmanutham Road
 Bangkapi Bangkok 10240
 TEL:0-2515-1162 FAX:0-2515-1161
 WWW.decorchoice.co.th

Client : Ari789	Design : WICMB-4C	View : Elevation A , Elevation B
Address :	Series : Elegance	Scale : 1:30
Province :	Drawn by : บริษัท สุนทรจามร	Date : 22/9/2569
Phone :	Email :	Page : 02

INSIDE: MDF HMR E1 V313 DKP # PP 022 WM | American Walnut
 OUTSIDE: MDF HMR E1 V313 DKP # 836 NCT | Anti-Fingerprint
 FRONTAGE: MDF HMR E1 V313 DKP # 836 NCT | Anti-Fingerprint
 HANDLE: Aluminum DKP #5230 | Ivory
 TOP: Quartz Vadara G1 #V743 | Ostara Dawn
 FRONTAGE: Aluminum DKP #5158 (มีมือจับในตัว) | Dark Choco ,
 กรูกระຈກ ใส TYK | Euro Bronze 5 mm. (Tempered)
 MIRROR: Aluminum DKP #5158 (มีมือจับในตัว) | Ivory ,
 กรูกระຈກเงา TYK 5 mm.

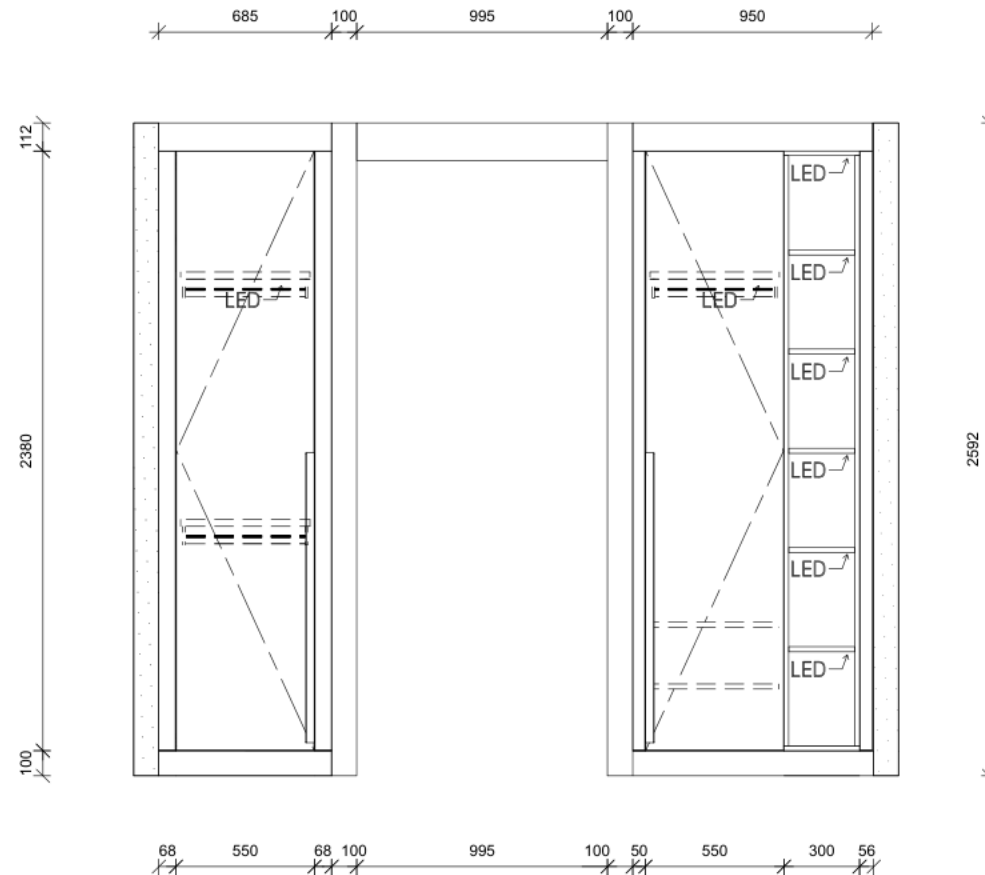

ELEVATION C

Dkbb

157 Praditmanutham Road
 Bangkapi Bangkok 10240
 TEL:0-2515-1162 FAX:0-2515-1161
 WWW.decorchoice.co.th

Client : Ari789	Design : WICMB-4C	View : Elevation C
Address :	Series : Elegance	Scale : 1:30
Province :	Drawn by : บริษัท สุนทรจามร	Date : 22/9/2569
Phone :	Email :	Page : 03