


INSIDE: MDF HMR E1 V313 DKP # PP 022 WM | American Walnut
OUTSIDE: MDF HMR E1 V313 DKP # 836 NCT | Anti-Fingerprint
FRONTAGE: MDF HMR E1 V313 DKP # 836 NCT | Anti-Fingerprint
HANDLE: Aluminum DKP #5230 | Ivory
HANDLE [DW]: Aluminum DKP #5230 | Dark Choco

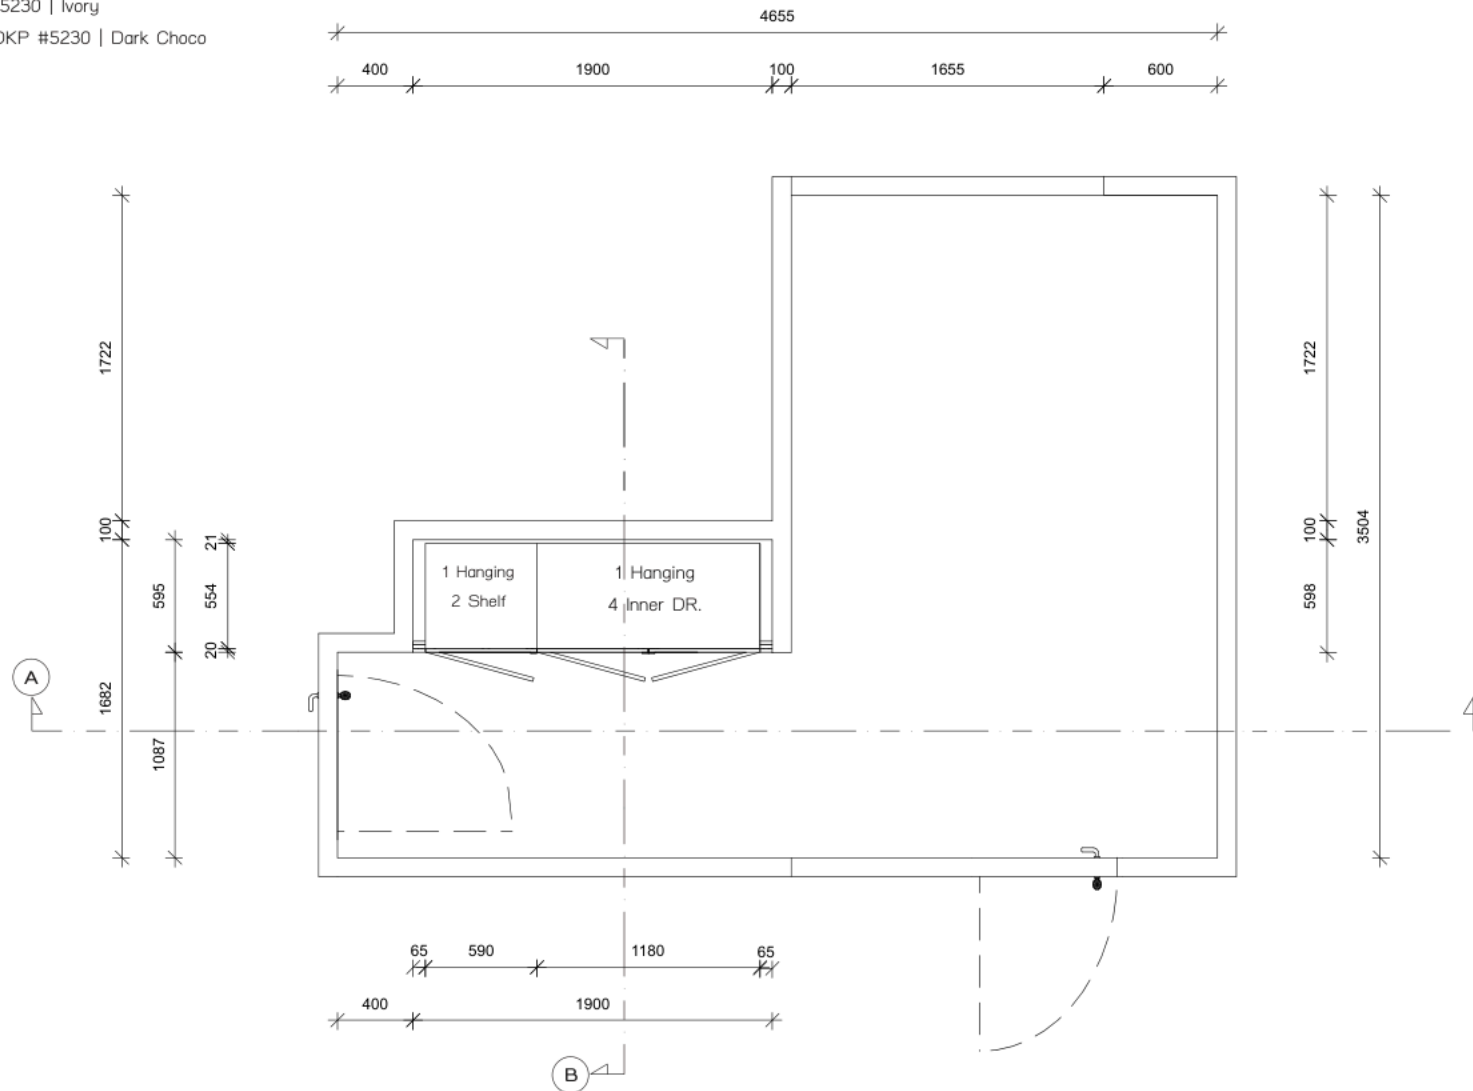


Dkbb

157 Praditmanutham Road
Bangkapi Bangkok 10240
TEL: 0-2515-1162 FAX: 0-2515-1161
WWW.decorschoice.co.th


Client : ARI789	Design : WALK-IN1 5B	View : Plan
Address :	Series : Elegance	Scale : 1:40
Province :	Drawn by : Nirarat	Date : 3/7/2569
Phone :	Email :	Page : 01

INSIDE: MDF HMR E1 V313 DKP # PP 022 WM | American Walnut
OUTSIDE: MDF HMR E1 V313 DKP # 836 NCT | Anti-Fingerprint
FRONTAGE: MDF HMR E1 V313 DKP # 836 NCT | Anti-Fingerprint
HANDLE: Aluminum DKP #5230 | Ivory
HANDLE [DW]: Aluminum DKP #5230 | Dark Choco

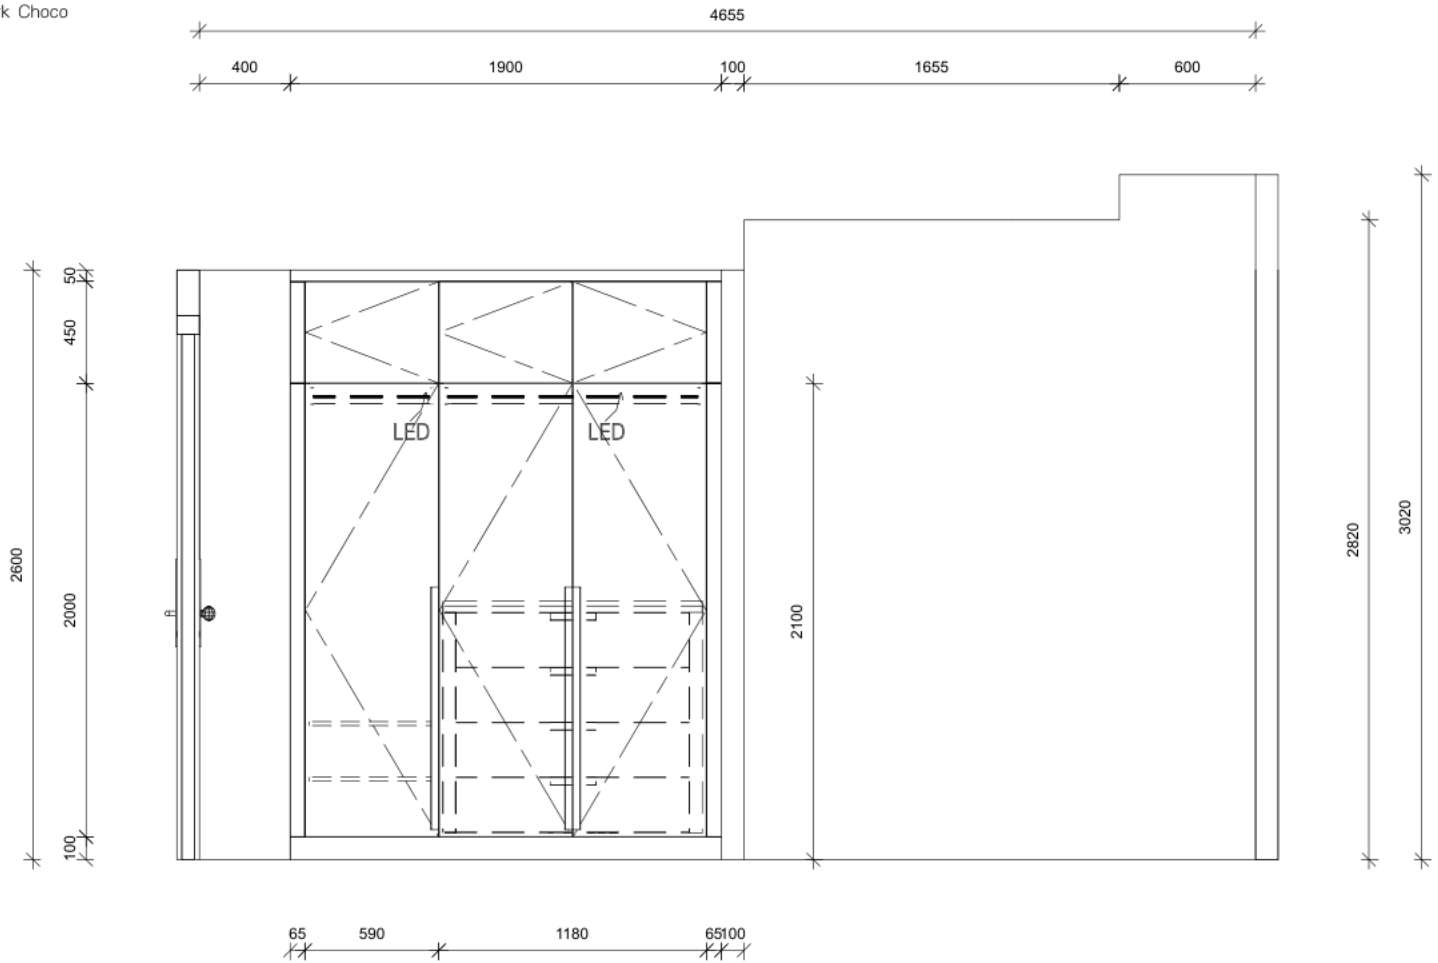

Dkbb 157 Praditmanutham Road Bangkapi Bangkok 10240 TEL:0-2515-1162 FAX:0-2515-1161 WWW.decorchoice.co.th	Client : ARI789	Design : WALK-IN1 5B	View : Elevation A
	Address :	Series : Elegance	Scale : 1:33.33
	Province :	Drawn by : Nirarat	Date : 3/7/2569
	Phone :	Email :	Page : 02

INSIDE: MDF HMR E1 V313 DKP # PP 022 WM | American Walnut
OUTSIDE: MDF HMR E1 V313 DKP # 836 NCT | Anti-Fingerprint
FRONTAGE: MDF HMR E1 V313 DKP # 836 NCT | Anti-Fingerprint
HANDLE: Aluminum DKP #5230 | Ivory
HANDLE [DW]: Aluminum DKP #5230 | Dark Choco

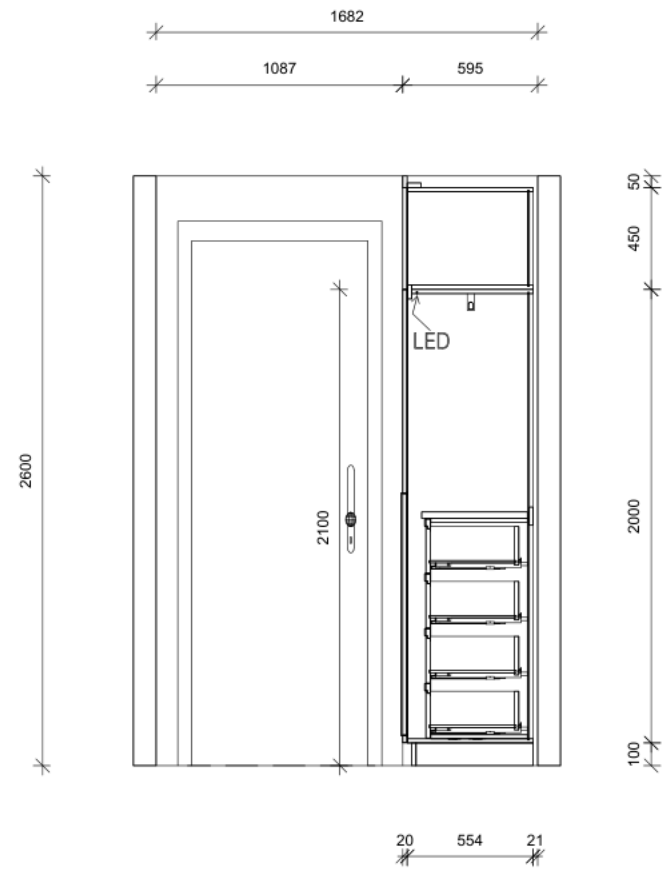

Dkbb

157 Praditmanutham Road
Bangkapi Bangkok 10240
TEL:0-2515-1162 FAX:0-2515-1161
WWW.decorschoice.co.th

Client : ARI789	Design : WALK-IN1 5B	View : Section B
Address :	Series : Elegance	Scale : 1:33.33
Province :	Drawn by : Nirarat	Date : 3/7/2569
Phone :	Email :	Page : 03