



INSIDE: MDF HMR E1 V313 DKP # PP 022 WM | American Walnut
OUTSIDE: MDF HMR E1 V313 DKP # 836 NCT | Anti-Fingerprint
FRONTAGE: MDF HMR E1 V313 DKP # 836 NCT | Anti-Fingerprint
FRONTAGE: Aluminum MEBEL #XGJB-5158 (มีมือจับในตัว)
| Dark Choco , กระจกจาก ใส TYK | Euro Bronze 5 mm.
HANDLE: Aluminum DKP #5230 | Ivory
HANDLE [DW]: Aluminum DKP #5230 | Dark Choco

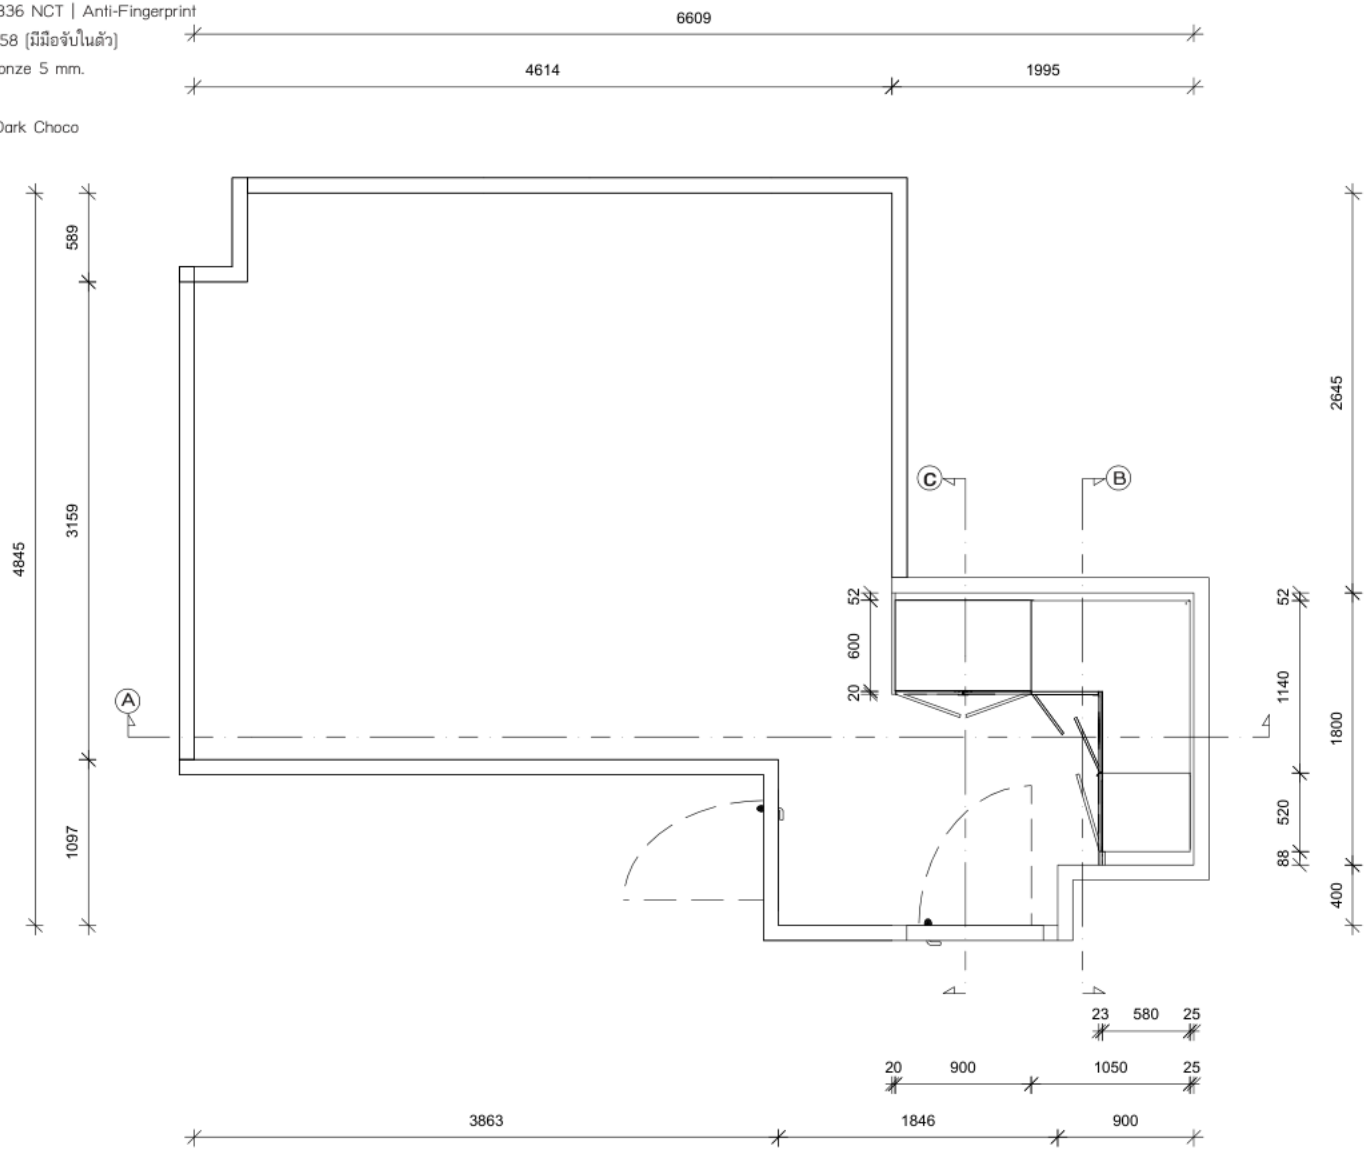

157 Praditmanutham Road
Bangkapi Bangkok 10240
TEL:0-2515-1162 FAX:0-2515-1161
WWW.decorchoice.co.th

Client :Ari 789	Design : MASTER WALK-IN 5B	View : PLAN
Address :	Series :	Scale : 1:50
Province :	Drawn by :Nirarat	Date : 7/7/2569
Phone :	Email :	Page : 01

INSIDE: MDF HMR E1 V313 DKP # PP 022 WM | American Walnut
 OUTSIDE: MDF HMR E1 V313 DKP # 836 NCT | Anti-Fingerprint
 FRONTAGE: MDF HMR E1 V313 DKP # 836 NCT | Anti-Fingerprint
 FRONTAGE: Aluminum MEBEL #XGJB-5158 [มีมือจับในตัว]
 | Dark Choco , กรูกระจุก ใส TYK | Euro Bronze 5 mm.
 HANDLE: Aluminum DKP #5230 | Ivory
 HANDLE [DW]: Aluminum DKP #5230 | Dark Choco

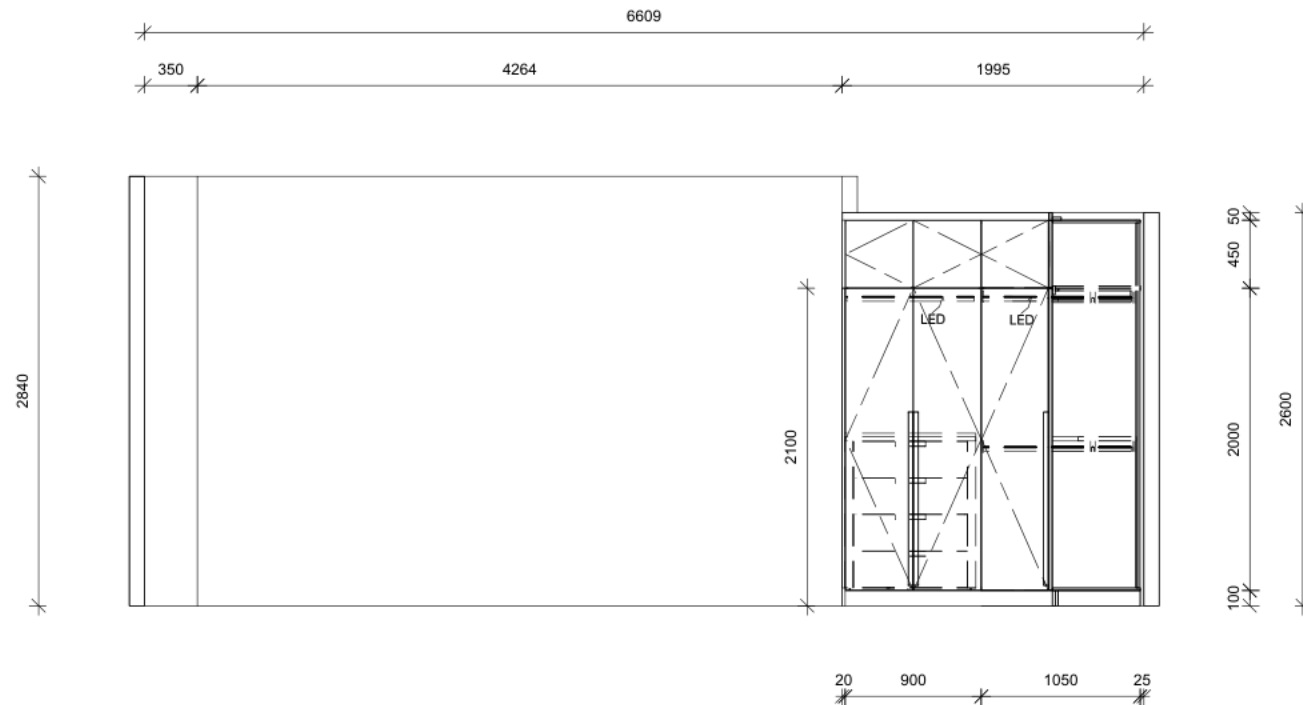


Dkbb

157 Praditmanutham Road
 Bangkapi Bangkok 10240
 TEL:0-2515-1162 FAX:0-2515-1161
 WWW.decorchoice.co.th

Client :Ari 789	Design : MASTER WALK-IN 5B	View : ELEVATION A
Address :	Series :	Scale : 1:50
Province :	Drawn by :Nirarat	Date : 7/7/2569
Phone :	Email :	Page : 02

INSIDE: MDF HMR E1 V313 DKP # PP 022 WM | American Walnut
OUTSIDE: MDF HMR E1 V313 DKP # 836 NCT | Anti-Fingerprint
FRONTAGE: MDF HMR E1 V313 DKP # 836 NCT | Anti-Fingerprint
FRONTAGE: Aluminum MEBEL #XGJB-5158 [มีมือจับในตัว]
| Dark Choco , กระจกใส TYK | Euro Bronze 5 mm.
HANDLE: Aluminum DKP #5230 | Ivory
HANDLE [DW]: Aluminum DKP #5230 | Dark Choco

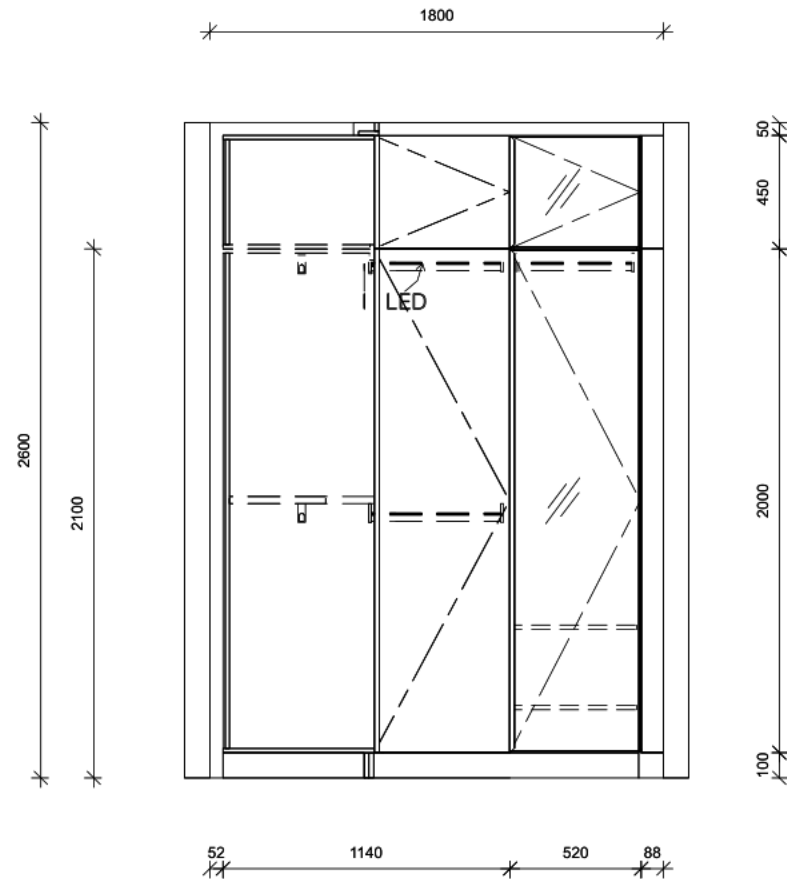


Dkbb

157 Praditmanutham Road
Bangkapi Bangkok 10240
TEL:0-2515-1162 FAX:0-2515-1161
WWW.decorchoice.co.th

Client :Ari 789	Design : MASTER WALK-IN 5B	View : ELEVATION B
Address :	Series :	Scale : 1:30
Province :	Drawn by :Nirarat	Date : 7/7/2569
Phone :	Email :	Page : 03

INSIDE: MDF HMR E1 V313 DKP # PP 022 WM | American Walnut
OUTSIDE: MDF HMR E1 V313 DKP # 836 NCT | Anti-Fingerprint
FRONTAGE: MDF HMR E1 V313 DKP # 836 NCT | Anti-Fingerprint
FRONTAGE: Aluminum MEBEL #XGJB-5158 (มีมือจับในตัว)
| Dark Choco , กระจกใส TYK | Euro Bronze 5 mm.
HANDLE: Aluminum DKP #5230 | Ivory
HANDLE [DW]: Aluminum DKP #5230 | Dark Choco

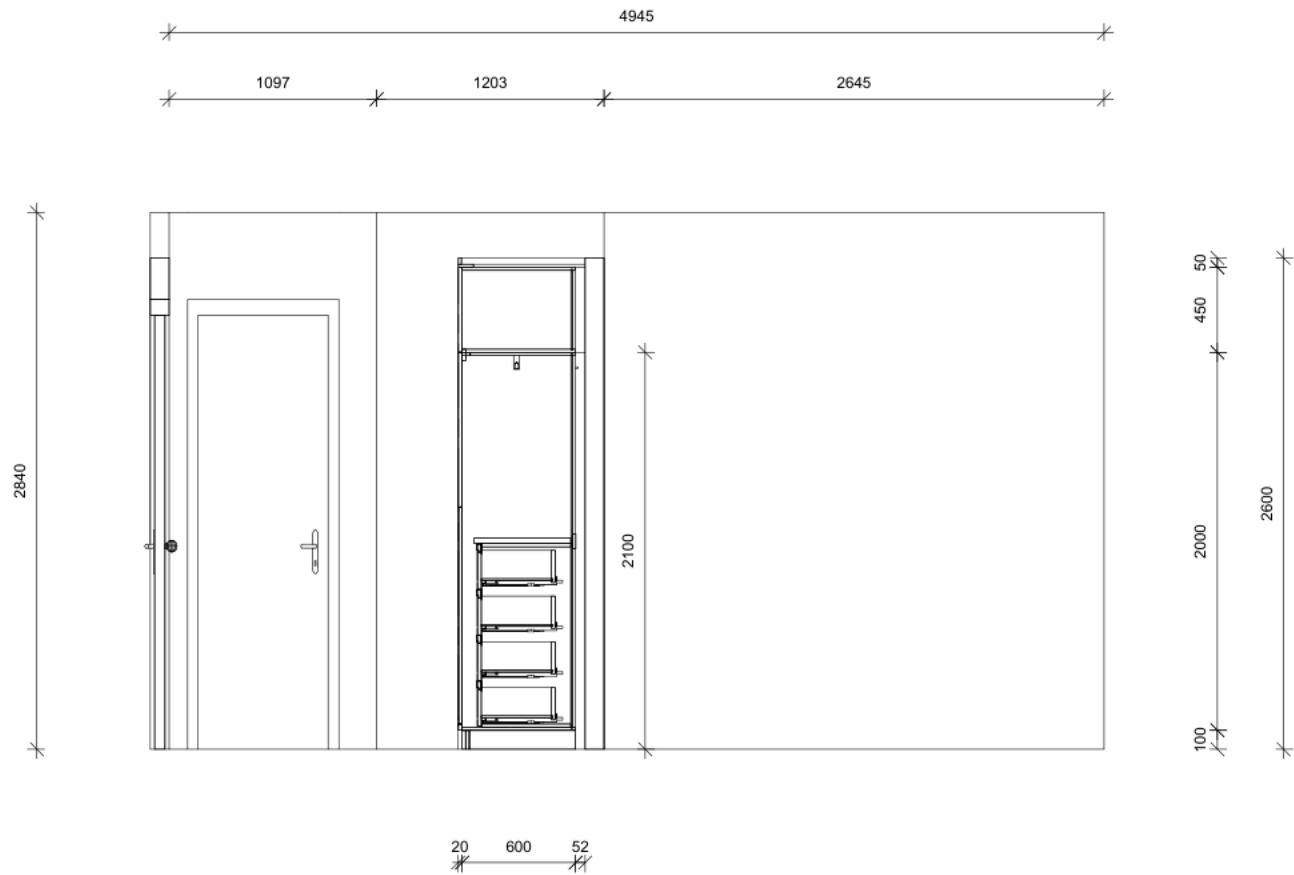

Dkbb

157 Praditmanutham Road
Bangkapi Bangkok 10240
TEL:0-2515-1162 FAX:0-2515-1161
WWW.decorchoice.co.th

Client :Ari 789	Design : MASTER WALK-IN 5B	View : SECTION C
Address :	Series :	Scale : 1:50
Province :	Drawn by :Nirarat	Date : 7/7/2569
Phone :	Email :	Page : 04