


INSIDE: MDF HMR E1 V313 DKP # PP 022 WM | American Walnut  
OUTSIDE: MDF HMR E1 V313 DKP # 836 NCT | Anti-Fingerprint  
FRONTAGE: MDF HMR E1 V313 DKP # 836 NCT | Anti-Fingerprint  
FRONTAGE: Aluminum MEBEL #XGJB-5158 [มีมือจับในตัว]  
| Dark Choco , กระจกใส TYK | Euro Bronze 5 mm.  
HANDLE: Aluminum DKP #5230 | Ivory  
HANDLE [DW]: Aluminum DKP #5230 | Dark Choco

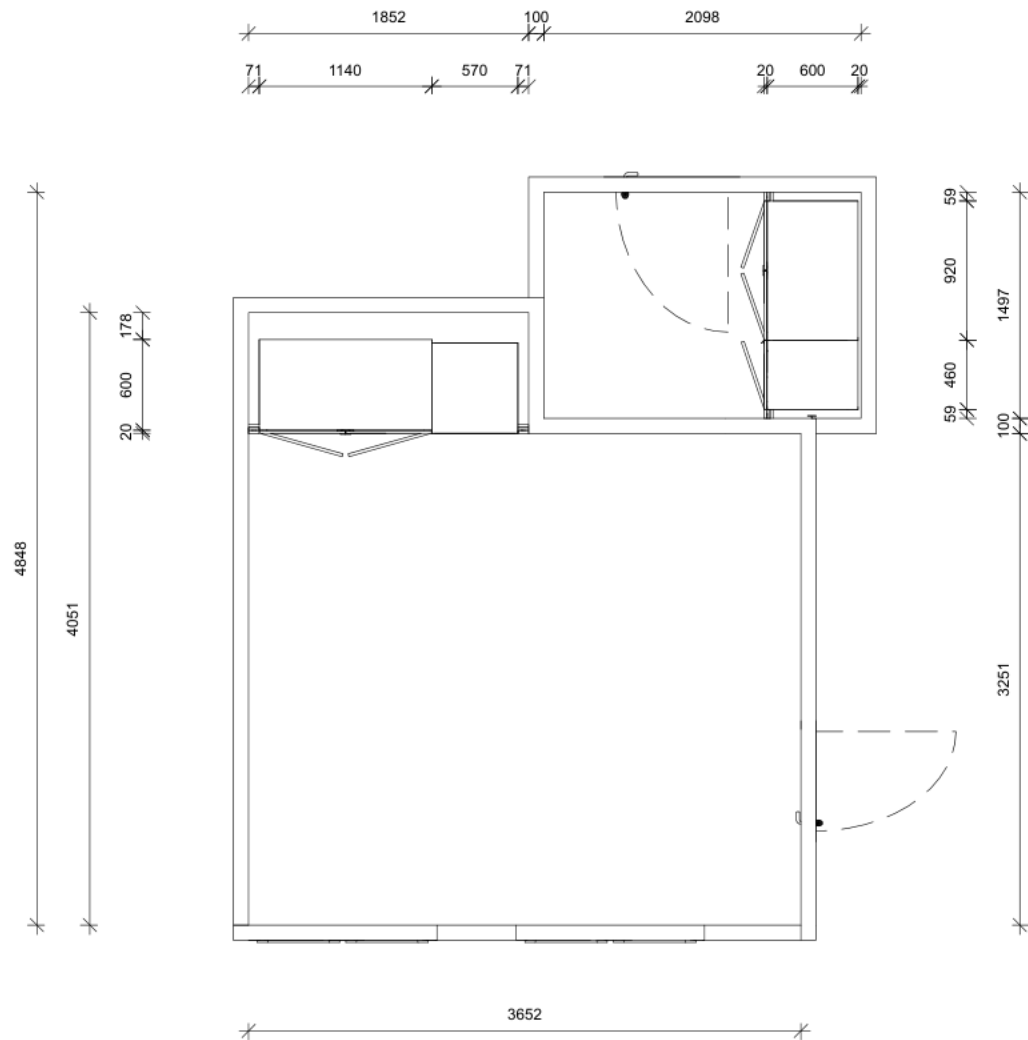


**Dkbb**

157 Praditmanutham Road  
Bangkapi Bangkok 10240  
TEL:0-2515-1162 FAX:0-2515-1161  
WWW.decorchoice.co.th

|                 |                    |                  |
|-----------------|--------------------|------------------|
| Client : Ari789 | Design :Walk-in 5C | View : Plan      |
| Address :       | Series : Elegance  | Scale : 1:50     |
| Province :      | Drawn by :Nirarat  | Date : 11/7/2569 |
| Phone :         | Email :            | Page : 01        |

INSIDE: MDF HMR E1 V313 DKP # PP 022 WM | American Walnut  
OUTSIDE: MDF HMR E1 V313 DKP # 836 NCT | Anti-Fingerprint  
FRONTAGE: MDF HMR E1 V313 DKP # 836 NCT | Anti-Fingerprint  
FRONTAGE: Aluminum MEBEL #XGJB-5158 [มีมือจับในตัว]  
| Dark Choco , กรูกระจุก ใส TYK | Euro Bronze 5 mm.  
HANDLE: Aluminum DKP #5230 | Ivory  
HANDLE [DW]: Aluminum DKP #5230 | Dark Choco

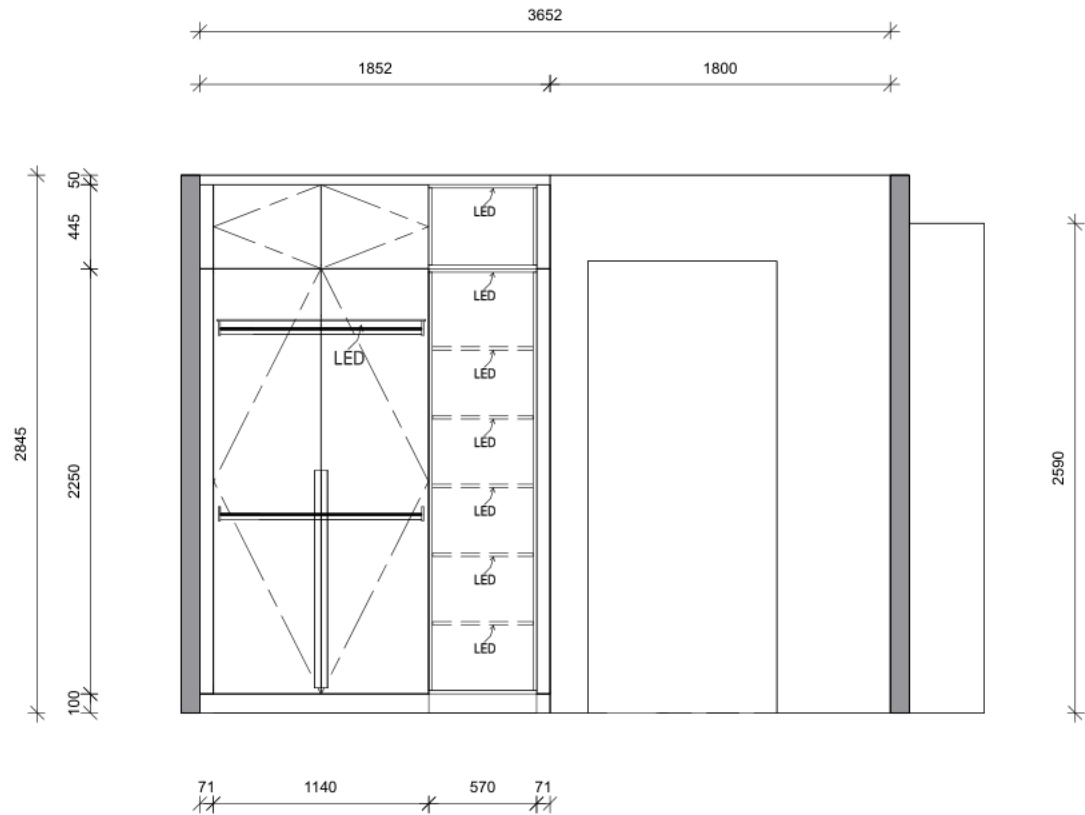


**Dkbb**

157 Praditmanutham Road  
Bangkapi Bangkok 10240  
TEL:0-2515-1162 FAX:0-2515-1161  
WWW.decorchoice.co.th

|                 |                    |                    |
|-----------------|--------------------|--------------------|
| Client : Ari789 | Design :Walk-in 5C | View : Elevation A |
| Address :       | Series : Elegance  | Scale : 1:40       |
| Province :      | Drawn by :Nirarat  | Date : 11/7/2569   |
| Phone :         | Email :            | Page : 02          |

INSIDE: MDF HMR E1 V313 DKP # PP 022 WM | American Walnut  
OUTSIDE: MDF HMR E1 V313 DKP # 836 NCT | Anti-Fingerprint  
FRONTAGE: MDF HMR E1 V313 DKP # 836 NCT | Anti-Fingerprint  
FRONTAGE: Aluminum MEBEL #XGJB-5158 [มีมือจับในตัว]  
| Dark Choco , กรูกระจุก ใส TYK | Euro Bronze 5 mm.  
HANDLE: Aluminum DKP #5230 | Ivory  
HANDLE [DW]: Aluminum DKP #5230 | Dark Choco

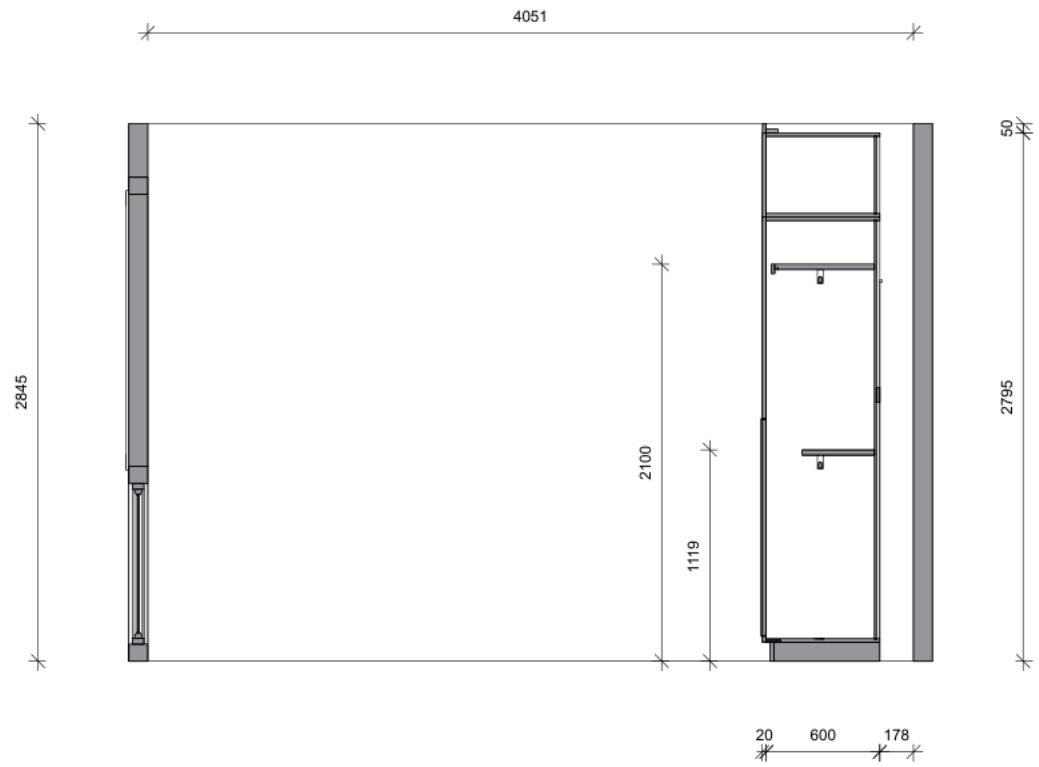


**Dkbb**

157 Praditmanutham Road  
Bangkapi Bangkok 10240  
TEL:0-2515-1162 FAX:0-2515-1161  
WWW.decorchoice.co.th

|                 |                    |                  |
|-----------------|--------------------|------------------|
| Client : Ari789 | Design :Walk-in 5C | View : Section B |
| Address :       | Series : Elegance  | Scale : 1:40     |
| Province :      | Drawn by :Nirarat  | Date : 11/7/2569 |
| Phone :         | Email :            | Page : 03        |


INSIDE: MDF HMR E1 V313 DKP # PP 022 WM | American Walnut  
OUTSIDE: MDF HMR E1 V313 DKP # 836 NCT | Anti-Fingerprint  
FRONTAGE: MDF HMR E1 V313 DKP # 836 NCT | Anti-Fingerprint  
FRONTAGE: Aluminum MEBEL #XGJB-5158 [มีมือจับในตัว]  
| Dark Choco , กระจกจาก ไทย TYK | Euro Bronze 5 mm.  
HANDLE: Aluminum DKP #5230 | Ivory  
HANDLE [DW]: Aluminum DKP #5230 | Dark Choco

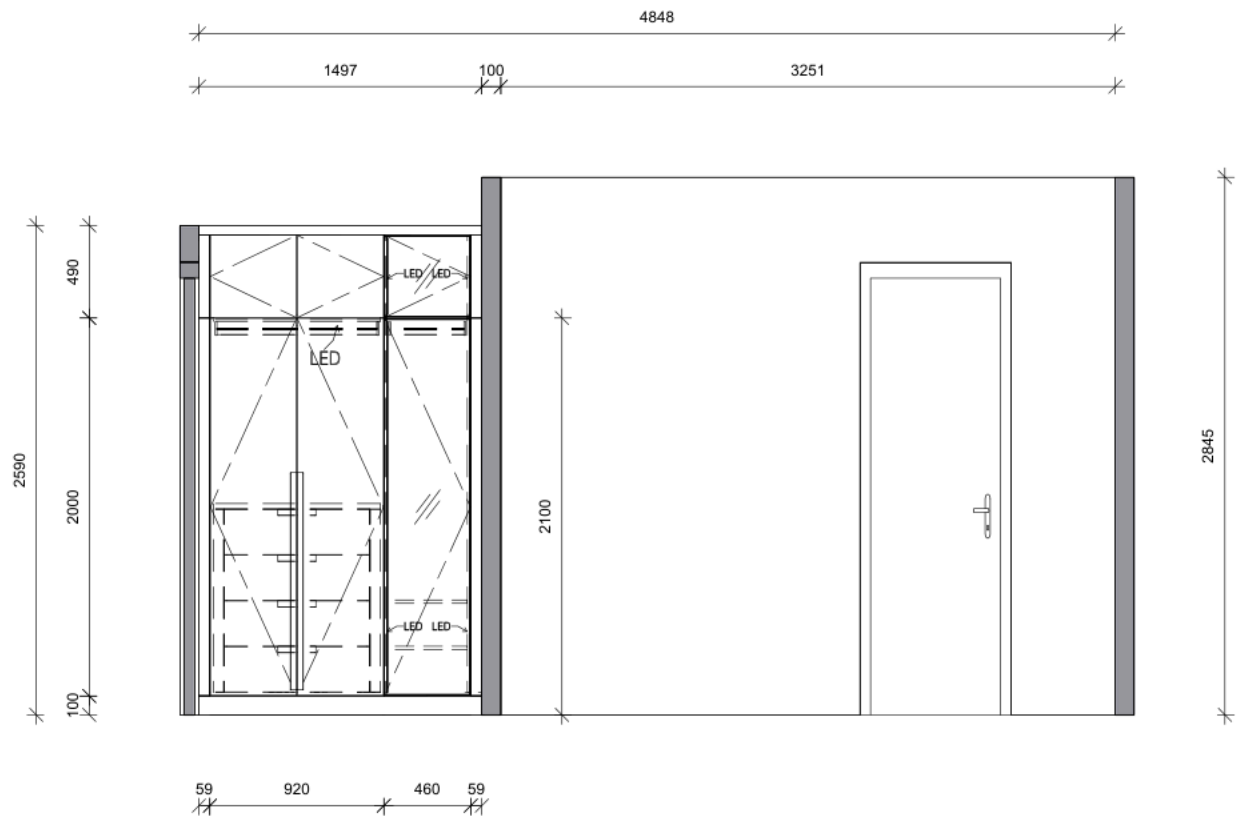

157 Praditmanutham Road  
Bangkapi Bangkok 10240  
TEL:0-2515-1162 FAX:0-2515-1161  
WWW.decorchoice.co.th

|                 |                    |                    |
|-----------------|--------------------|--------------------|
| Client : Ari789 | Design :Walk-in 5C | View : Elevation C |
| Address :       | Series : Elegance  | Scale : 1:40       |
| Province :      | Drawn by :Nirarat  | Date : 11/7/2569   |
| Phone :         | Email :            | Page : 04          |

INSIDE: MDF HMR E1 V313 DKP # PP 022 WM | American Walnut  
OUTSIDE: MDF HMR E1 V313 DKP # 836 NCT | Anti-Fingerprint  
FRONTAGE: MDF HMR E1 V313 DKP # 836 NCT | Anti-Fingerprint  
FRONTAGE: Aluminum MEBEL #XGJB-5158 [มีมือจับในตัว]  
| Dark Choco , กระจกใส TYK | Euro Bronze 5 mm.  
HANDLE: Aluminum DKP #5230 | Ivory  
HANDLE [DW]: Aluminum DKP #5230 | Dark Choco

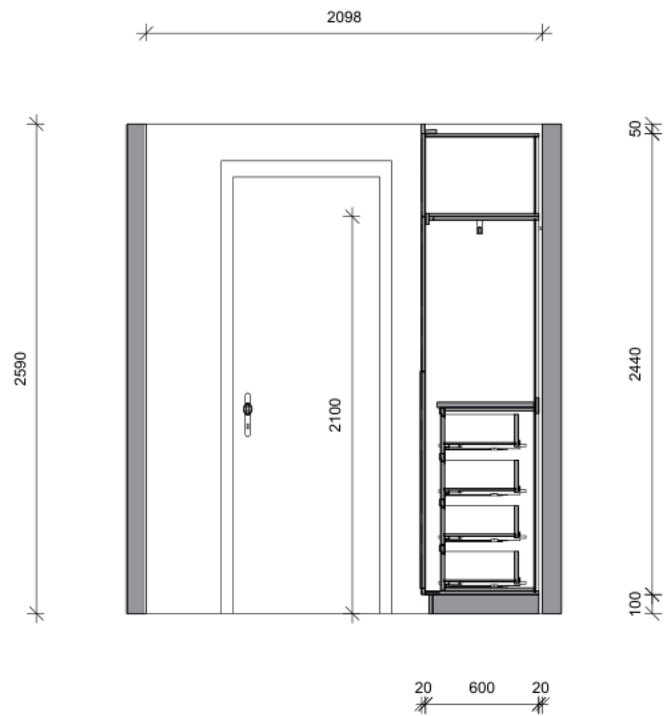

**Dkbb**

157 Praditmanutham Road  
Bangkapi Bangkok 10240  
TEL:0-2515-1162 FAX:0-2515-1161  
WWW.decorchoice.co.th

|                 |                    |                  |
|-----------------|--------------------|------------------|
| Client : Ari789 | Design :Walk-in 5C | View : Section D |
| Address :       | Series : Elegance  | Scale : 1:40     |
| Province :      | Drawn by :Nirarat  | Date : 11/7/2569 |
| Phone :         | Email :            | Page : 05        |