
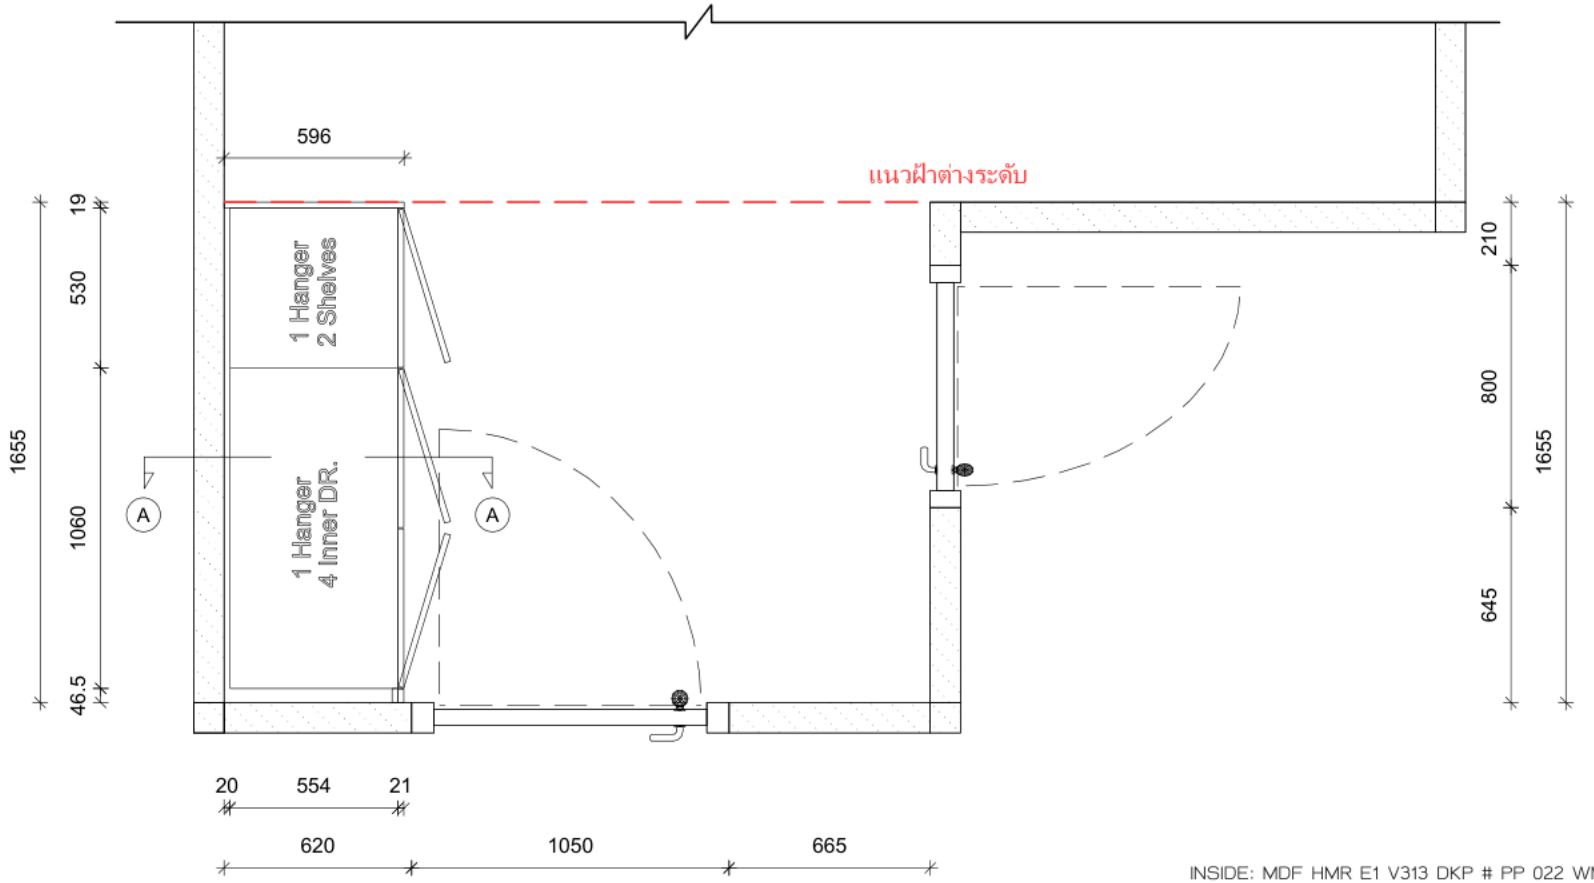


INSIDE: MDF HMR E1 V313 DKP # PP 022 WM | American Walnut
OUTSIDE: MDF HMR E1 V313 DKP # 836-S NCT | Anti-Fingerprint
FRONTAGE: MDF HMR E1 V313 DKP # 836-S NCT | Anti-Fingerprint
HANDLE: Aluminum DKP #5230 | Ivory
HANDLE: Aluminum DKP #5230 | Dark Choco

Dkbb
157 Praditmanutham Road
Bangkapi Bangkok 10240
TEL:0-2515-1162 FAX:0-2515-1161
WWW.decorschoice.co.th

Client : Ari789	Design : WIC2 - 4A	View : Plan
Address :	Series : Elegance	Scale : 1:25
Province :	Drawn by : Jirayu Kidrakmuang	Date : 16/10/2569
Phone :	Email :	Page : 01

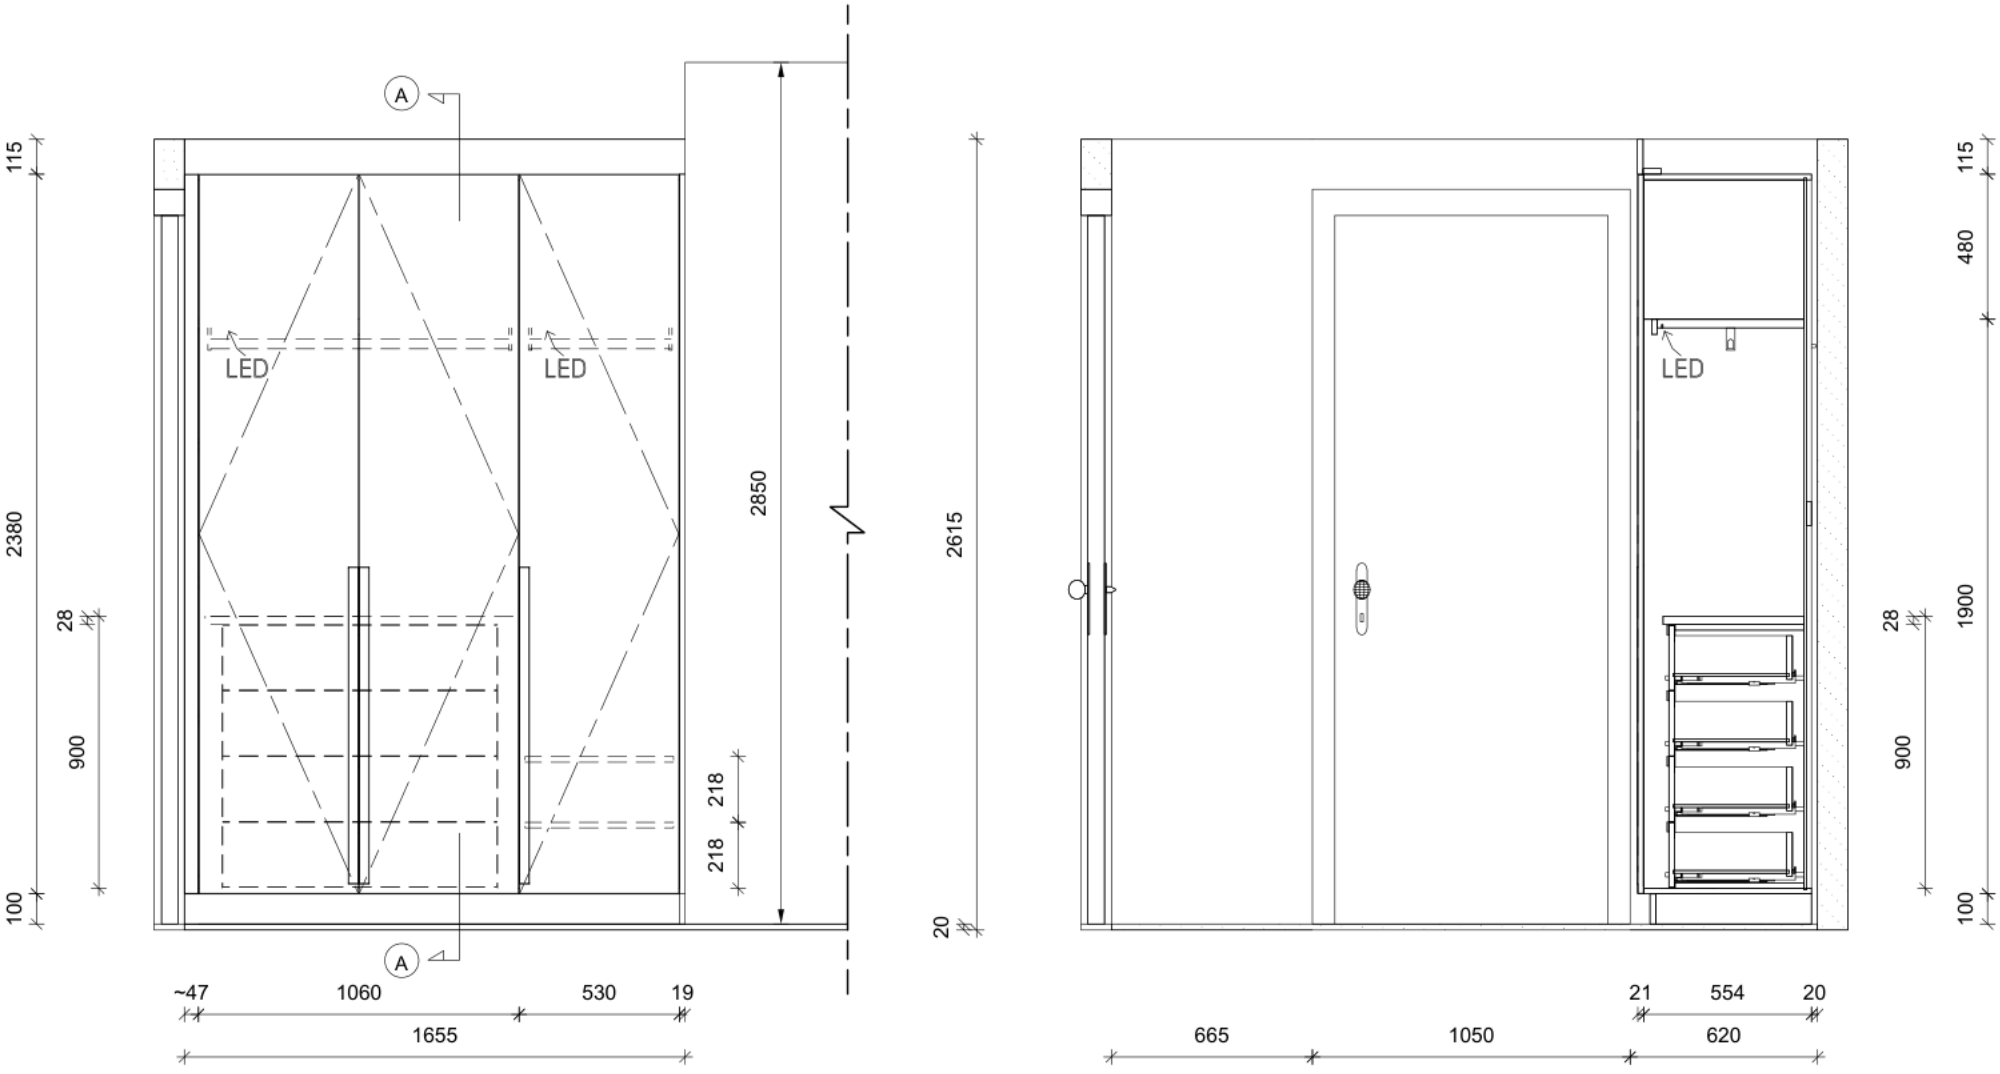

ELEVATION

SECTION


INSIDE: MDF HMR E1 V313 DKP # PP 022 WM | American Walnut
OUTSIDE: MDF HMR E1 V313 DKP # 836-S NCT | Anti-Fingerprint
FRONTAGE: MDF HMR E1 V313 DKP # 836-S NCT | Anti-Fingerprint

HANDLE: Aluminum DKP #5230 | Ivory
HANDLE: Aluminum DKP #5230 | Dark Choco

Dkbb
157 Praditmanutham Road
Bangkapi Bangkok 10240
TEL:0-2515-1162 FAX:0-2515-1161
WWW.decorschoice.co.th

Client : Ari789	Design : WIC2 - 4A	View : Elevation , Section
Address :	Series : Elegance	Scale : 1:25
Province :	Drawn by : Jirayu Kidrakmuang	Date : 16/10/2569
Phone :	Email :	Page : 02

INSIDE: MDF HMR E1 V313 DKP # PP 022 WM | American Walnut
OUTSIDE: MDF HMR E1 V313 DKP # 836 NCT | Anti-Fingerprint
FRONTAGE: MDF HMR E1 V313 DKP # 836 NCT | Anti-Fingerprint
HANDLE: Aluminum DKP #5230 | Ivory
HANDLE: Aluminum DKP #5230 | Dark Choco
TOP: Quartz Vadara G1 #V743 | Ostara Dawn
FRONTAGE: Aluminum DKP #5158 (มีมือจับในตัว) | Dark Choco ,
กรุกระจก ใส TYK | Euro Bronze 5 mm. (Tempered)

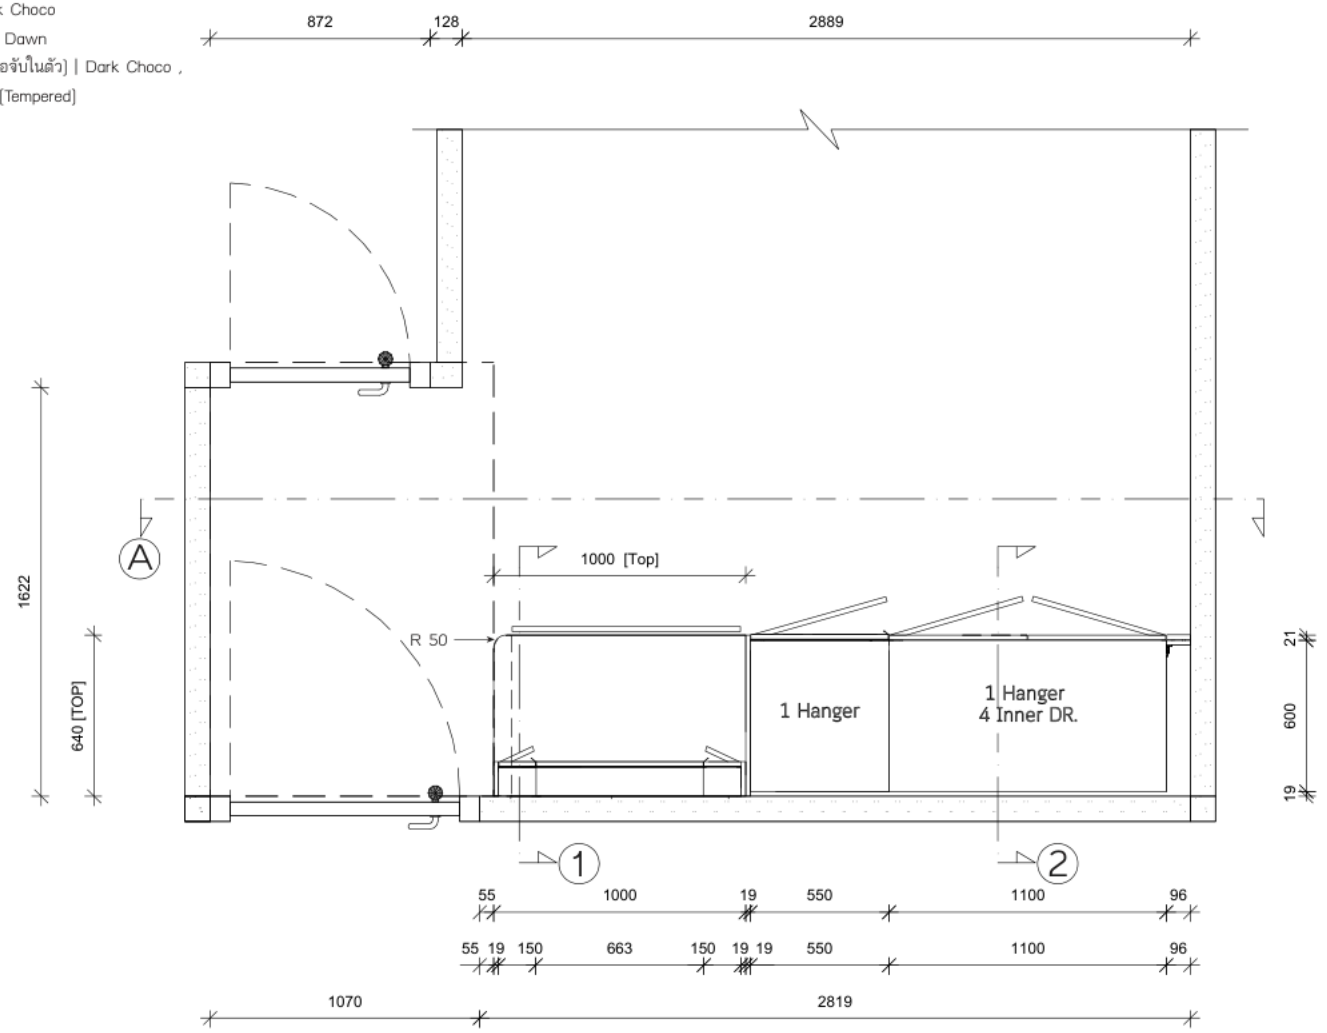

Dkbb
157 Praditmanutham Road
Bangkapi Bangkok 10240
TEL:0-2515-1162 FAX:0-2515-1161
WWW.decorschoice.co.th


Client : Ari789	Design : WIC1-4A	View : Plan
Address :	Series : Elegance	Scale : 1:30
Province :	Drawn by : บริวัตร สุนทรจามร	Date : 18/9/2569
Phone :	Email :	Page : 01

INSIDE: MDF HMR E1 V313 DKP # PP 022 WM | American Walnut
OUTSIDE: MDF HMR E1 V313 DKP # 836 NCT | Anti-Fingerprint
FRONTAGE: MDF HMR E1 V313 DKP # 836 NCT | Anti-Fingerprint
HANDLE: Aluminum DKP #5230 | Ivory
HANDLE: Aluminum DKP #5230 | Dark Choco
TOP: Quartz Vadara G1 #V743 | Ostara Dawn
FRONTAGE: Aluminum DKP #5158 (มีมือจับในตัว) | Dark Choco ,
กรุกระจก ใส TYK | Euro Bronze 5 mm. (Tempered)




Dkbb 157 Praditmanutham Road Bangkapi Bangkok 10240 TEL:0-2515-1162 FAX:0-2515-1161 WWW.decorschoice.co.th	Client : Ari789	Design : WIC1-4A	View : Elevation A
	Address :	Series : Elegance	Scale : 1:30
	Province :	Drawn by : บริวัตร สุนทรจามร	Date : 18/9/2569
	Phone :	Email :	Page : 02

INSIDE: MDF HMR E1 V313 DKP # PP 022 WM | American Walnut
OUTSIDE: MDF HMR E1 V313 DKP # 836 NCT | Anti-Fingerprint
FRONTAGE: MDF HMR E1 V313 DKP # 836 NCT | Anti-Fingerprint
HANDLE: Aluminum DKP #5230 | Ivory
HANDLE: Aluminum DKP #5230 | Dark Choco
TOP: Quartz Vadara G1 #V743 | Ostara Dawn
FRONTAGE: Aluminum DKP #5158 [มีมือจับในตัว] | Dark Choco ,
กรุกระจก ใส TYK | Euro Bronze 5 mm. [Tempered]

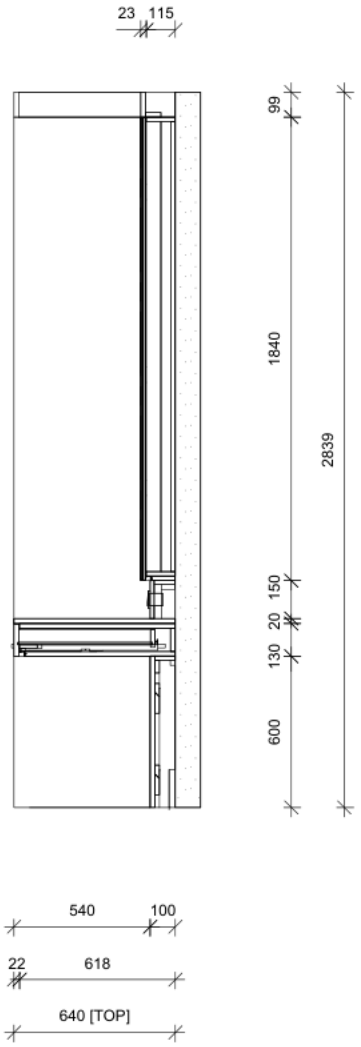

SECTION 1

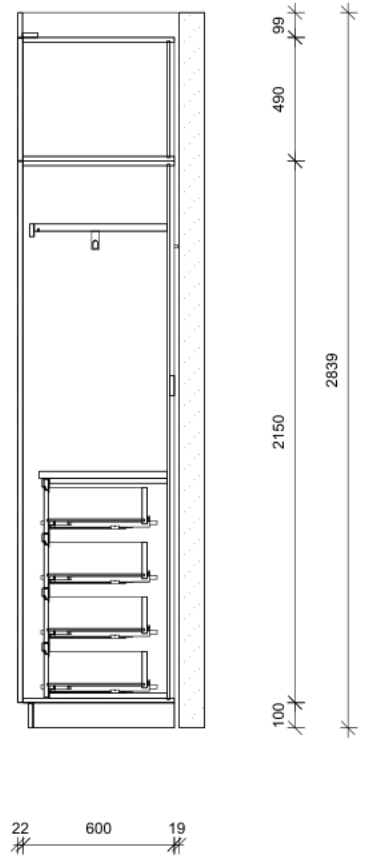


SECTION 2

Dkbb
157 Praditmanutham Road
Bangkapi Bangkok 10240
TEL:0-2515-1162 FAX:0-2515-1161
WWW.decorschoice.co.th

Client : Ari789	Design : WIC1-4A	View : Section 1
Address :	Series : Elegance	Scale : 1:30
Province :	Drawn by : บริวัตร สุนทรจามร	Date : 18/9/2569
Phone :	Email :	Page : 03


INSIDE: MDF HMR E1 V313 DKP # PP 022 WM | American Walnut
OUTSIDE: MDF HMR E1 V313 DKP # 836 NCT | Anti-Fingerprint
FRONTAGE: MDF HMR E1 V313 DKP # 836 NCT | Anti-Fingerprint
HANDLE: Aluminum DKP #5230 | Ivory
HANDLE: Aluminum DKP #5230 | Dark Choco
TOP: Quartz Vadara G1 #V743 | Ostara Dawn
เสริมแข็ง: Ivory

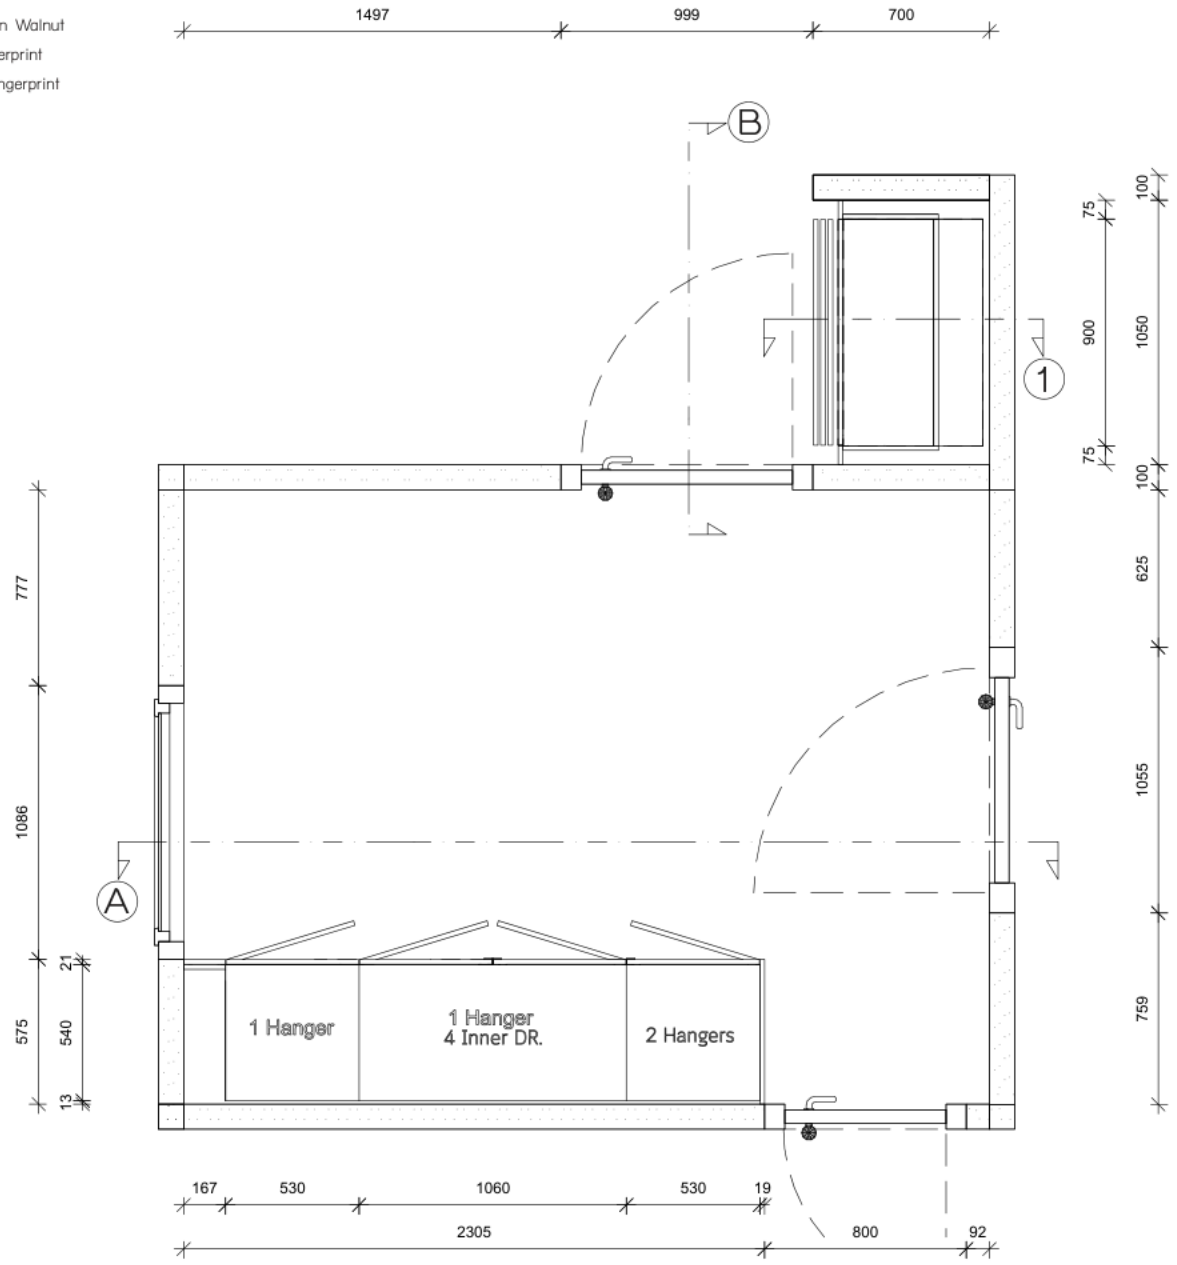

Dkbb
157 Praditmanutham Road
Bangkapi Bangkok 10240
TEL:0-2515-1162 FAX:0-2515-1161
WWW.decorschoice.co.th

Client : Ari789	Design : WICMB-4A	View : Plan
Address :	Series : Elegance	Scale : 1:30
Province :	Drawn by : บริวัตร สุนทรจามร	Date : 19/10/2569
Phone :	Email :	Page : 01


INSIDE: MDF HMR E1 V313 DKP # PP 022 WM | American Walnut
OUTSIDE: MDF HMR E1 V313 DKP # 836 NCT | Anti-Fingerprint
FRONTAGE: MDF HMR E1 V313 DKP # 836 NCT | Anti-Fingerprint
HANDLE: Aluminum DKP #5230 | Ivory
HANDLE: Aluminum DKP #5230 | Dark Choco
TOP: Quartz Vadara G1 #V743 | Ostara Dawn
เสริมแข็ง: Ivory

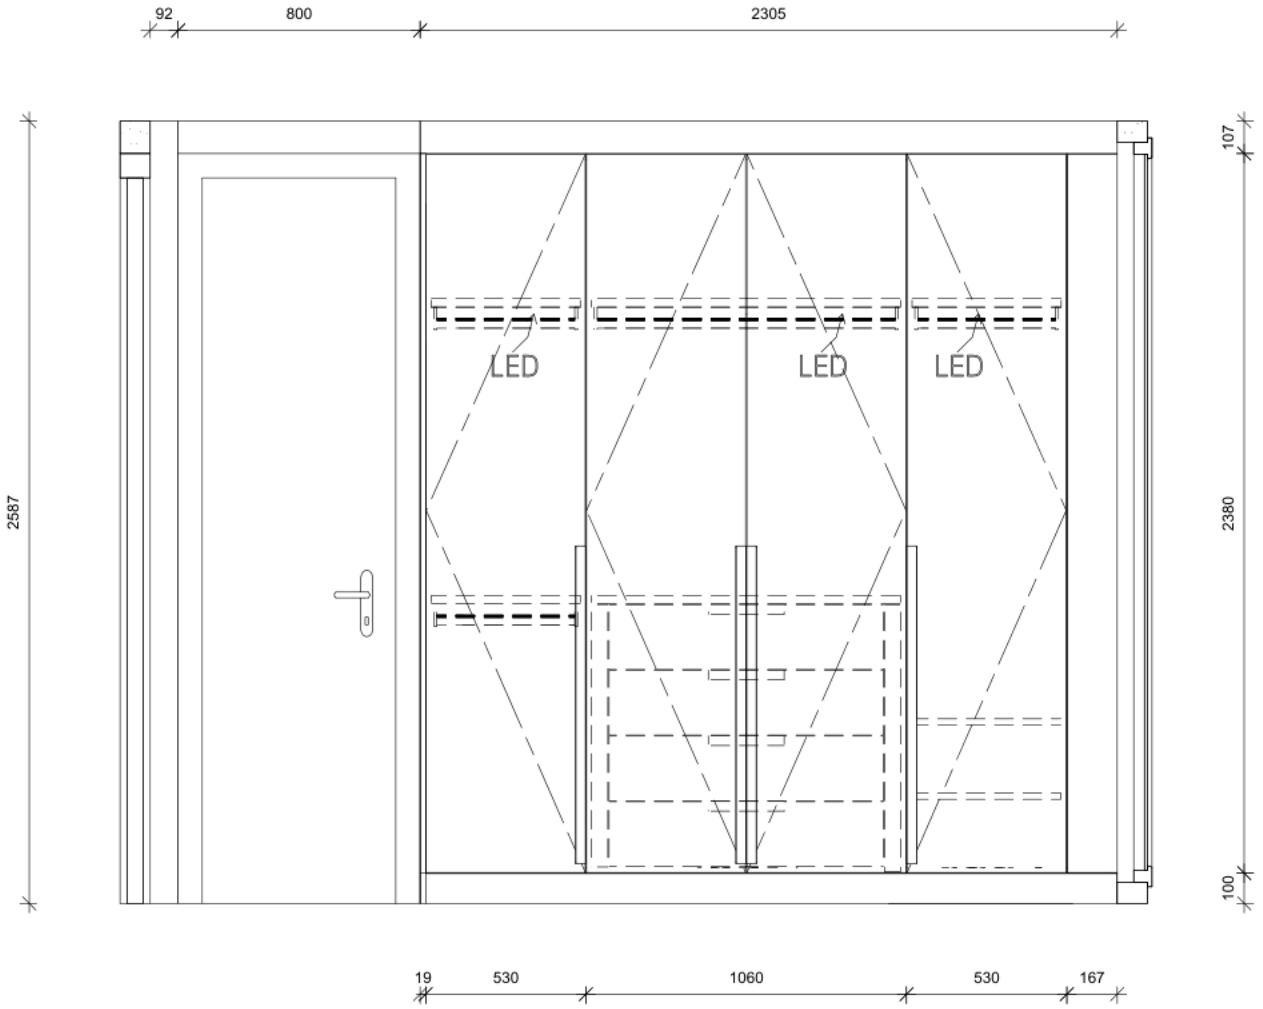


Dkbb
157 Praditmanutham Road
Bangkapi Bangkok 10240
TEL:0-2515-1162 FAX:0-2515-1161
WWW.decorschoice.co.th

Client : Ari789	Design : WICMB-4A	View : Elevation A
Address :	Series : Elegance	Scale : 1:25
Province :	Drawn by : บริวัตร สุนทรจามร	Date : 19/10/2569
Phone :	Email :	Page : 02

INSIDE: MDF HMR E1 V313 DKP # PP 022 WM | American Walnut
OUTSIDE: MDF HMR E1 V313 DKP # 836 NCT | Anti-Fingerprint
FRONTAGE: MDF HMR E1 V313 DKP # 836 NCT | Anti-Fingerprint
HANDLE: Aluminum DKP #5230 | Ivory
HANDLE: Aluminum DKP #5230 | Dark Choco
TOP: Quartz Vadara G1 #V743 | Ostara Dawn
เสริมแข็ง: Ivory

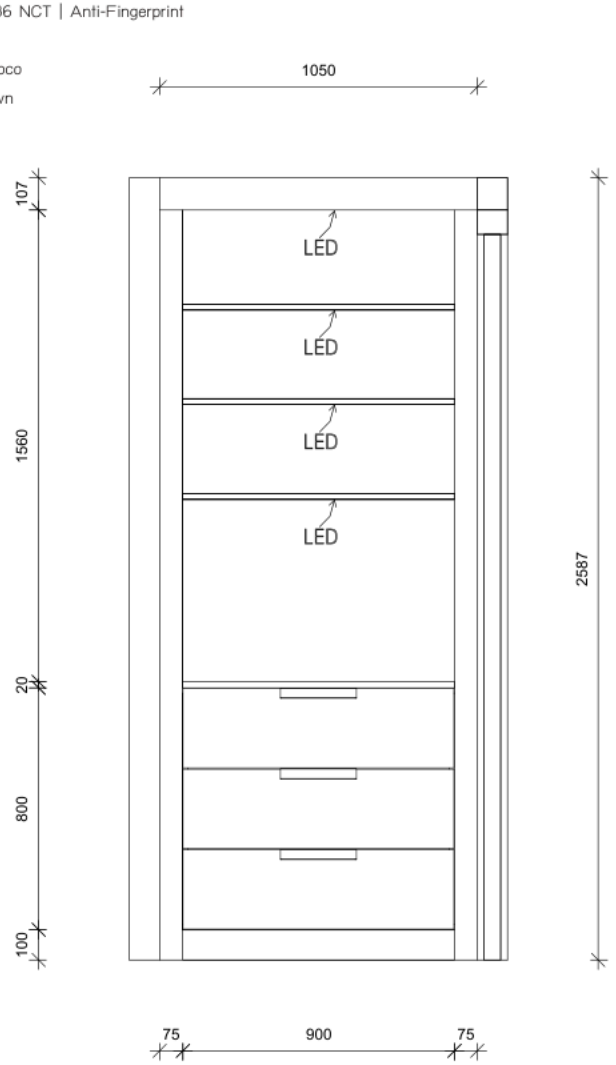

ELEVATION B

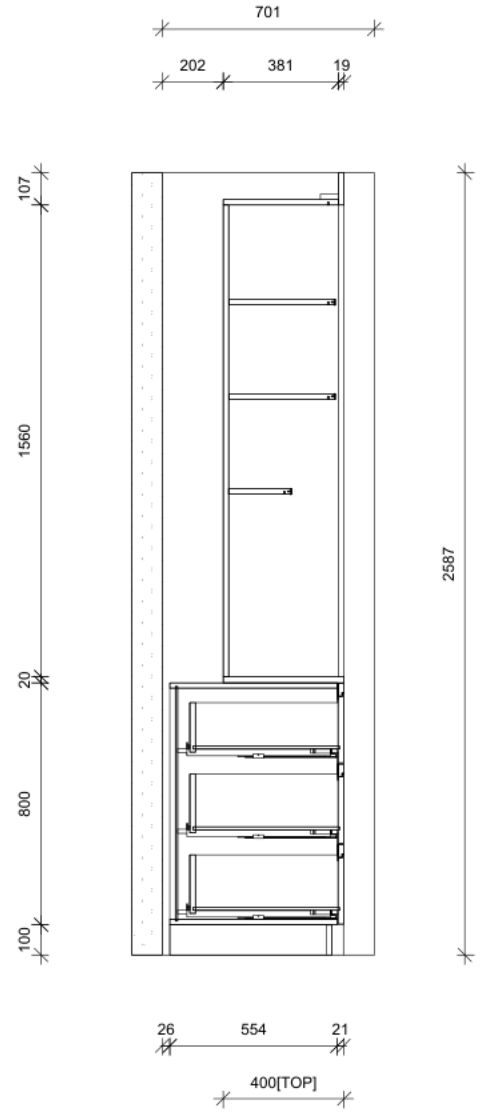

SECTION 1

Dkbb
157 Praditmanutham Road
Bangkapi Bangkok 10240
TEL:0-2515-1162 FAX:0-2515-1161
WWW.decorschoice.co.th

Client : Ari789	Design : WICMB-4A	View : Elevation B , Section 1
Address :	Series : Elegance	Scale : 1:25
Province :	Drawn by : บริวัตร สุนทรจามร	Date : 19/10/2569
Phone :	Email :	Page : 03