

INSIDE: MDF HMR E1 V313 DKP # PP 022 WM | American Walnut
OUTSIDE: MDF HMR E1 V313 DKP # 836 NCT | Anti-Fingerprint
FRONTAGE: MDF HMR E1 V313 DKP # 836 NCT | Anti-Fingerprint
HANDLE: Aluminum DKP #5230 | Ivory
HANDLE: Aluminum DKP #5230 | Dark Choco
TOP: Quartz Vadara G1 #V743 | Ostara Dawn
FRONTAGE: Aluminum DKP #5158 (มีมือจับในตัว) | Dark Choco ,
กรุกระจก ใส TYK | Euro Bronze 5 mm. [Tempered]
เสริมแข็ง: Ivory

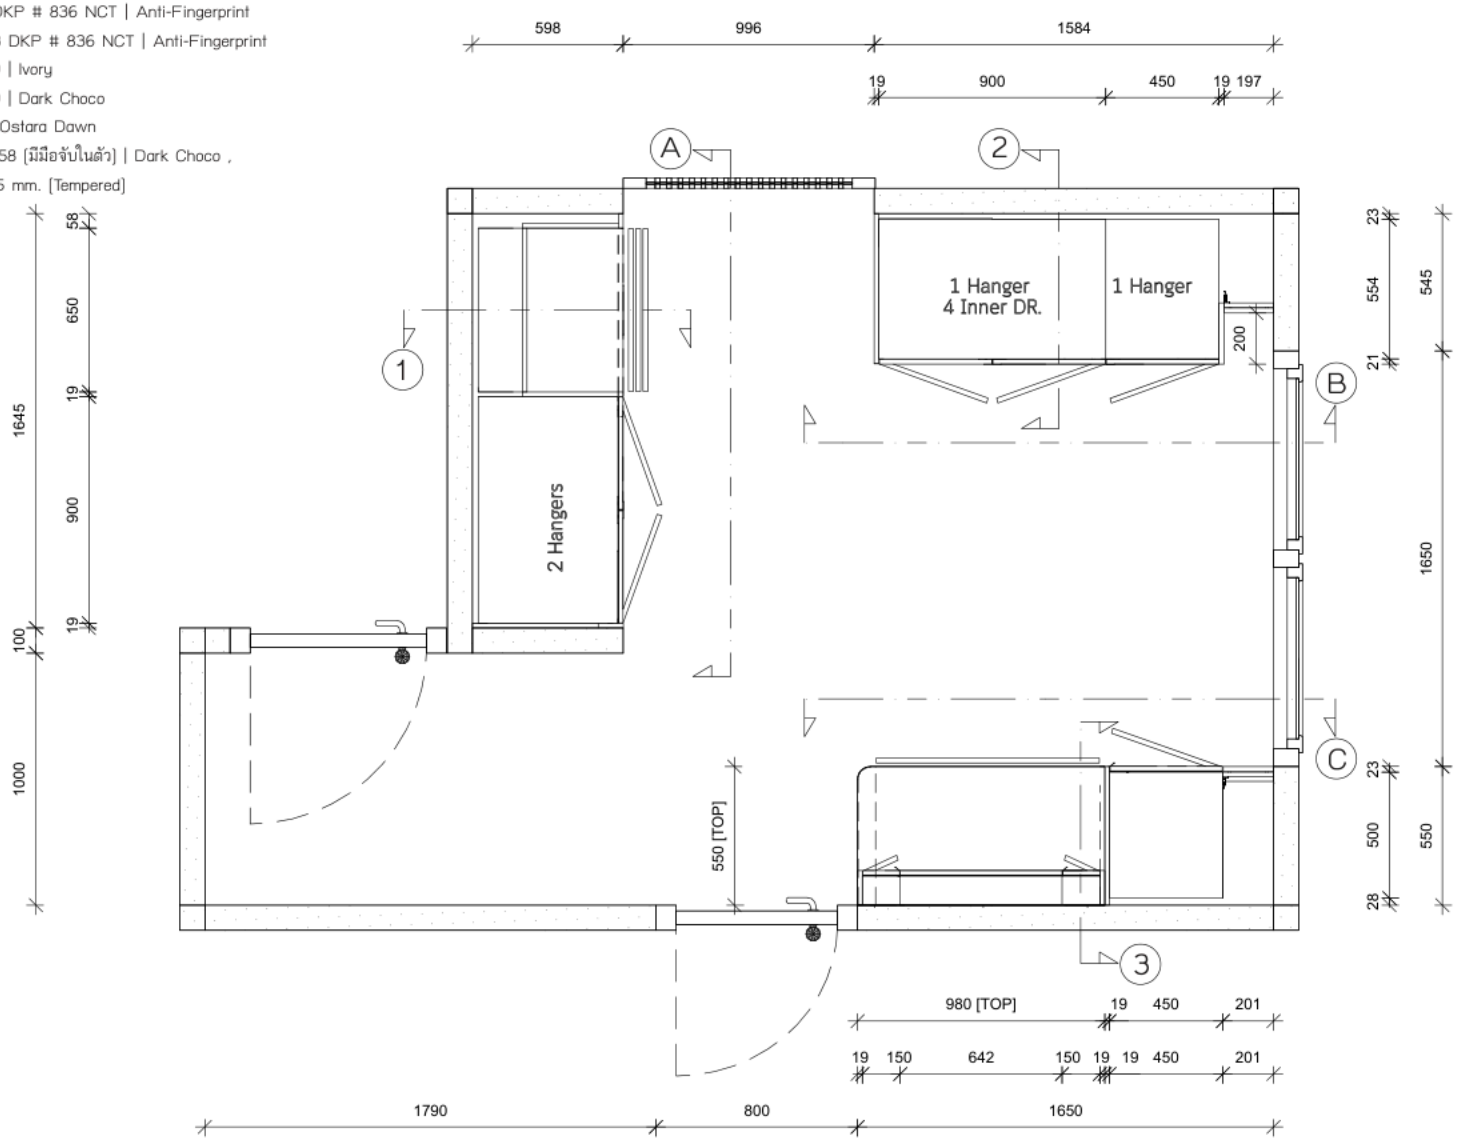


Dkbb
157 Praditmanutham Road
Bangkapi Bangkok 10240
TEL:0-2515-1162 FAX:0-2515-1161
WWW.decorschoice.co.th

Client : Ari789	Design : WICMB-4B	View : Plan
Address :	Series : Elegance	Scale : 1:30
Province :-	Drawn by : บริวัตร สุนทรจามร	Date : 10/10/2569
Phone :	Email :	Page : 01

INSIDE: MDF HMR E1 V313 DKP # PP 022 WM | American Walnut
OUTSIDE: MDF HMR E1 V313 DKP # 836 NCT | Anti-Fingerprint
FRONTAGE: MDF HMR E1 V313 DKP # 836 NCT | Anti-Fingerprint
HANDLE: Aluminum DKP #5230 | Ivory
HANDLE: Aluminum DKP #5230 | Dark Choco
TOP: Quartz Vadara G1 #V743 | Ostara Dawn
FRONTAGE: Aluminum DKP #5158 (มีมือจับในตัว) | Dark Choco ,
กรุกระจก ใส TYK | Euro Bronze 5 mm. [Tempered]
เสริมแข็ง: Ivory

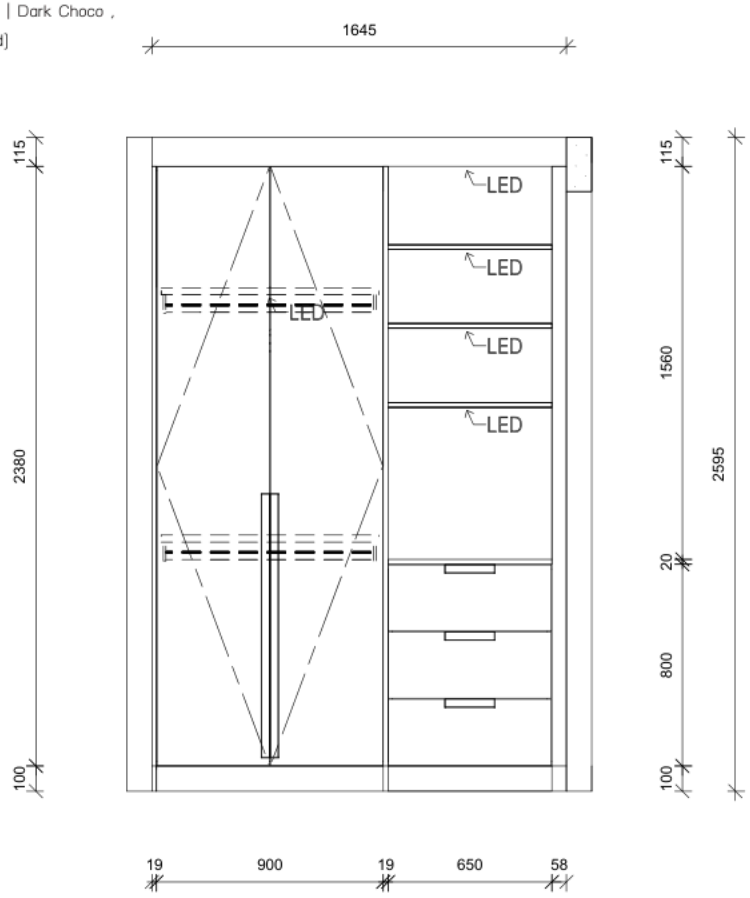

ELEVATION A

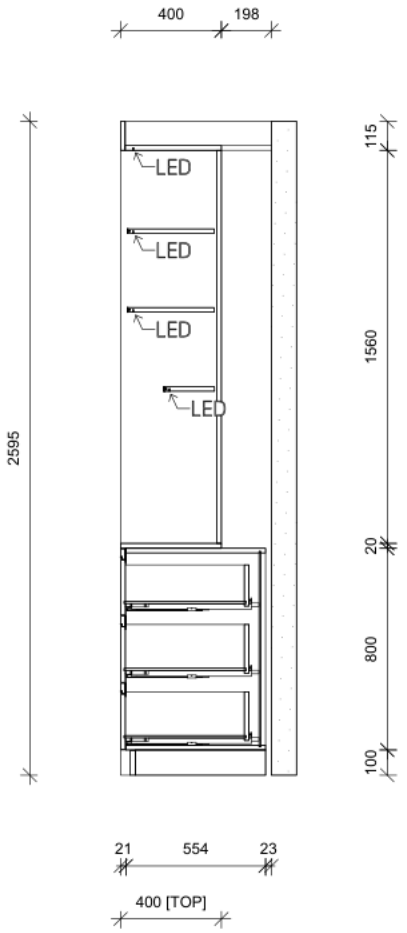


SECTION 1


Dkbb
157 Praditmanutham Road
Bangkapi Bangkok 10240
TEL:0-2515-1162 FAX:0-2515-1161
WWW.decorschoice.co.th

Client : Ari789	Design : WICMB-4B	View : Elevation A , Section 1
Address :	Series : Elegance	Scale : 1:30
Province :-	Drawn by : บริวัตร สุนทรจามร	Date : 10/10/2569
Phone :	Email :	Page : 02

INSIDE: MDF HMR E1 V313 DKP # PP 022 WM | American Walnut
OUTSIDE: MDF HMR E1 V313 DKP # 836 NCT | Anti-Fingerprint
FRONTAGE: MDF HMR E1 V313 DKP # 836 NCT | Anti-Fingerprint
HANDLE: Aluminum DKP #5230 | Ivory
HANDLE: Aluminum DKP #5230 | Dark Choco
TOP: Quartz Vadara G1 #V743 | Ostara Dawn
FRONTAGE: Aluminum DKP #5158 (มีมือจับในตัว) | Dark Choco ,
กรุกระจก ใส TYK | Euro Bronze 5 mm. (Tempered)
เสริมแข็ง: Ivory

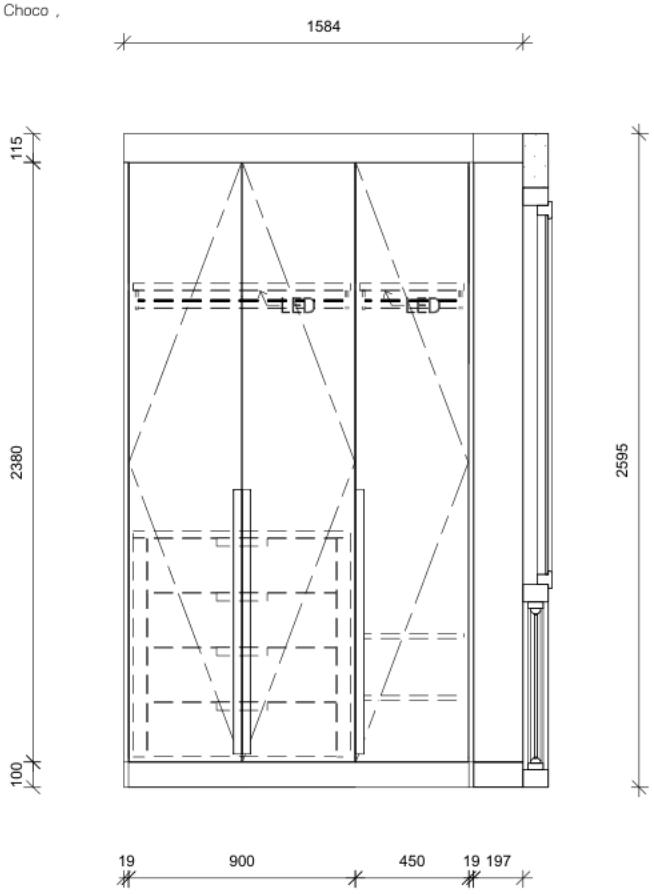

ELEVATION B

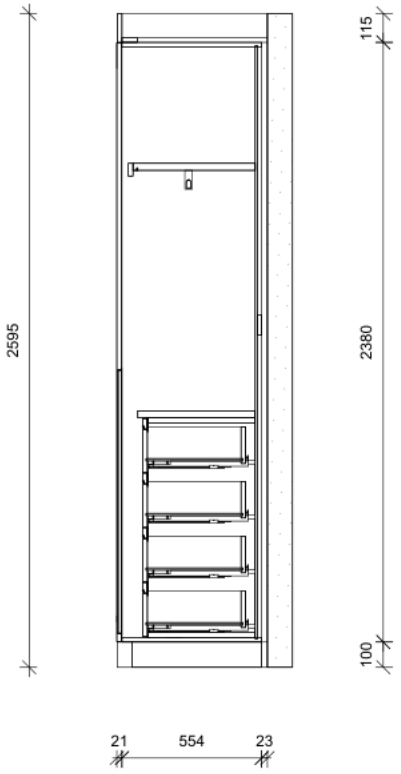


SECTION 2


Dkbb
157 Praditmanutham Road
Bangkapi Bangkok 10240
TEL:0-2515-1162 FAX:0-2515-1161
WWW.decorschoice.co.th

Client : Ari789	Design : WICMB-4B	View : Elevation B , Section 2
Address :	Series : Elegance	Scale : 1:30
Province :-	Drawn by : บริวัตร สุนทรจามร	Date : 10/10/2569
Phone :	Email :	Page : 03

INSIDE: MDF HMR E1 V313 DKP # PP 022 WM | American Walnut
OUTSIDE: MDF HMR E1 V313 DKP # 836 NCT | Anti-Fingerprint
FRONTAGE: MDF HMR E1 V313 DKP # 836 NCT | Anti-Fingerprint
HANDLE: Aluminum DKP #5230 | Ivory
HANDLE: Aluminum DKP #5230 | Dark Choco
TOP: Quartz Vadara G1 #V743 | Ostara Dawn
FRONTAGE: Aluminum DKP #5158 [มีมือจับในตัว] | Dark Choco ,
กรุกระจก ใส TYK | Euro Bronze 5 mm. [Tempered]
เสริมแข็ง: Ivory

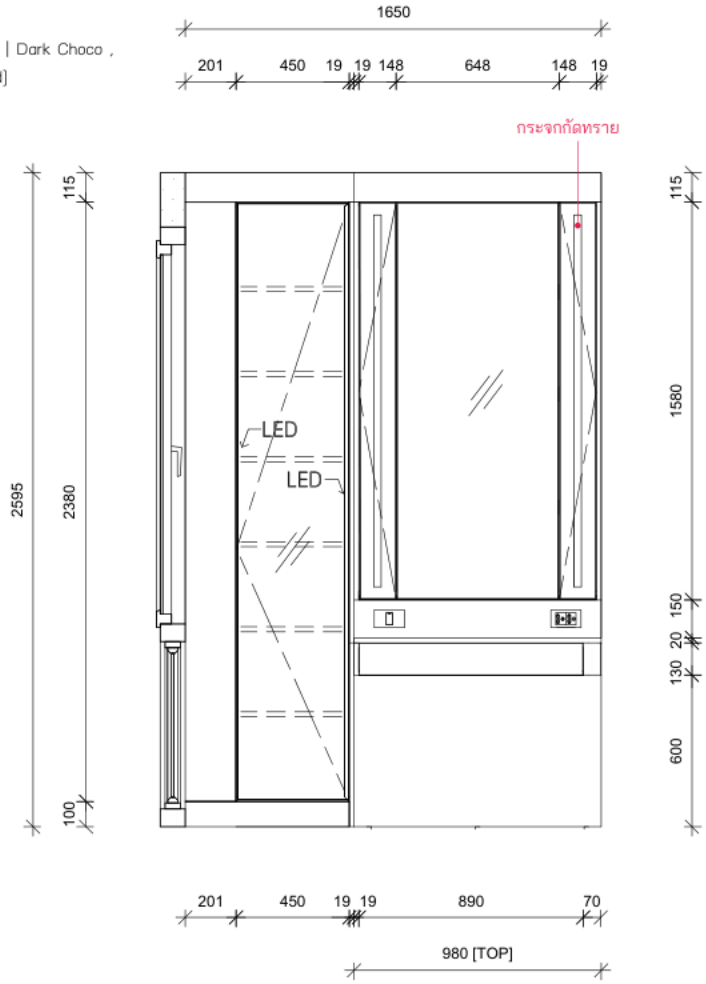


ELEVATION C

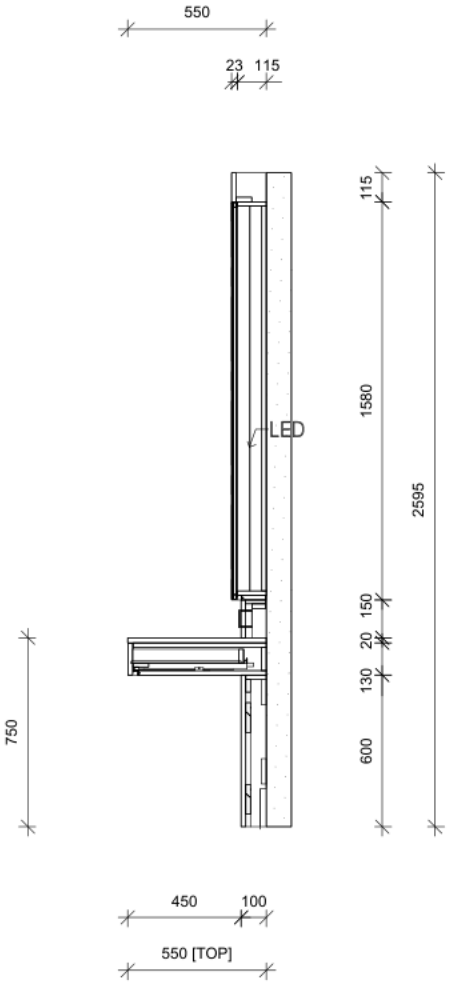

SECTION 3


Dkbb 157 Praditmanutham Road Bangkapi Bangkok 10240 TEL:0-2515-1162 FAX:0-2515-1161 WWW.decorschoice.co.th	Client : Ari789	Design : WICMB-4B	View : Elevation C , Section 3
	Address :	Series : Elegance	Scale : 1:30
	Province :-	Drawn by : บริวัตร สุนทรจามร	Date : 10/10/2569
	Phone :	Email :	Page : 04

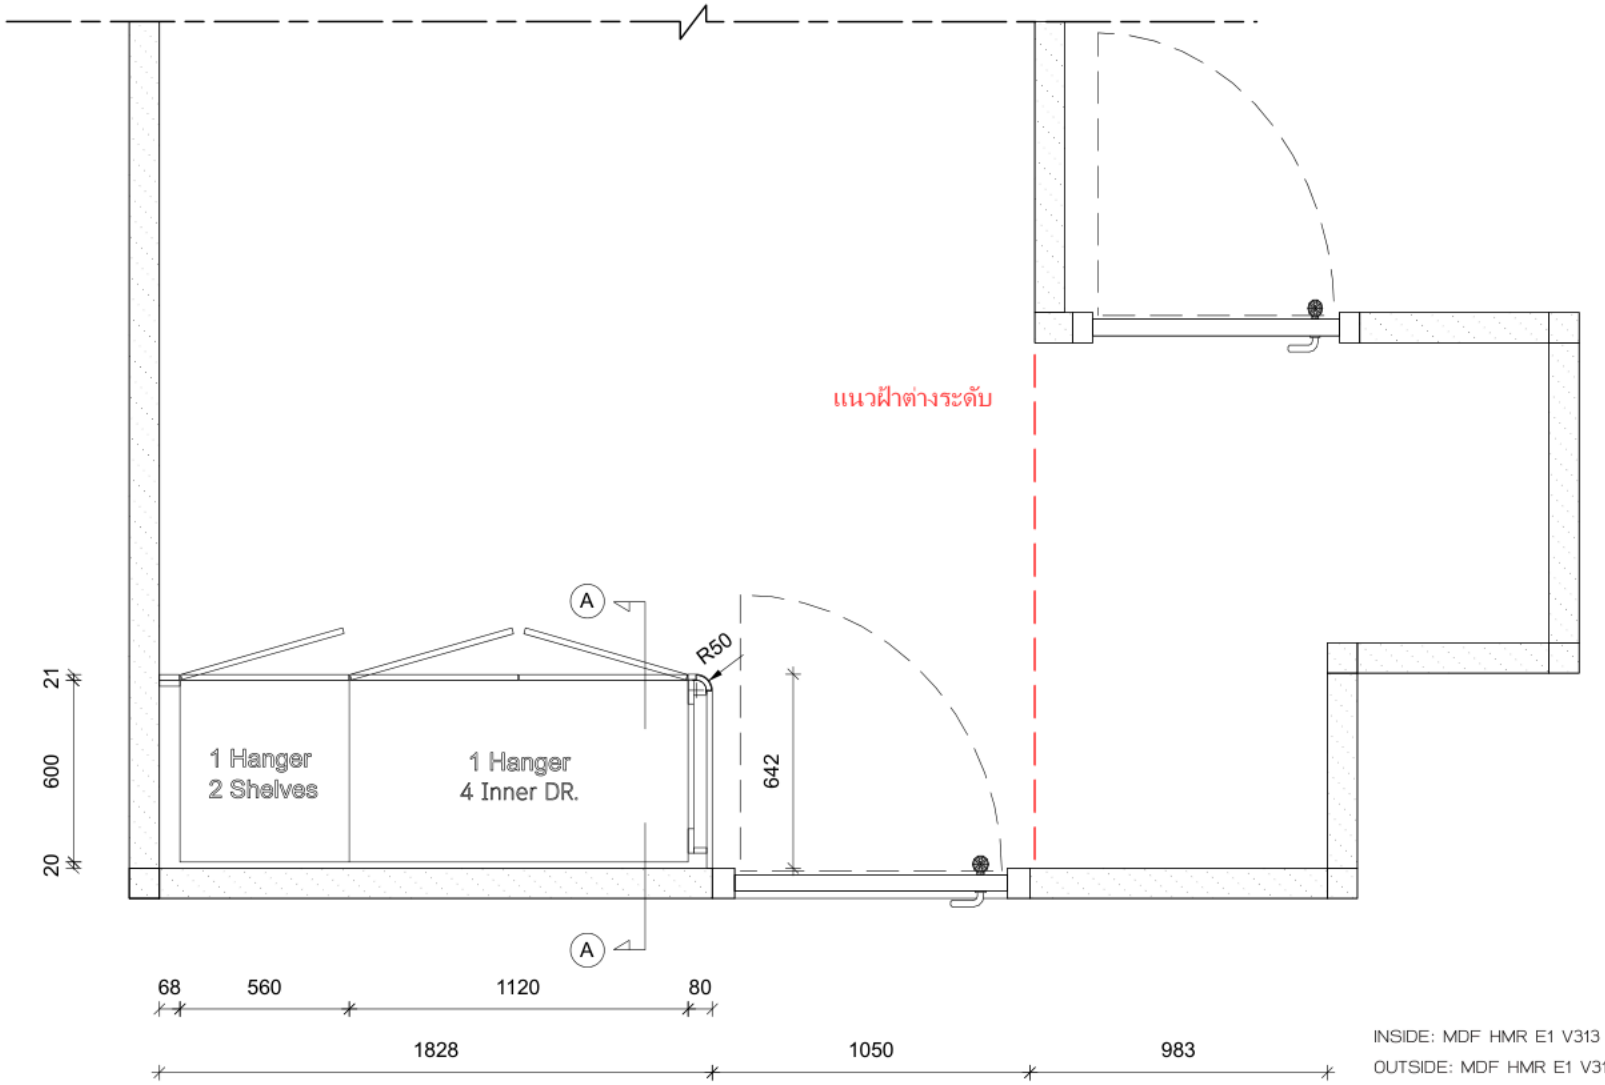

INSIDE: MDF HMR E1 V313 DKP # PP 022 WM | American Walnut
OUTSIDE: MDF HMR E1 V313 DKP # 836-S NCT | Anti-Fingerprint
FRONTAGE: MDF HMR E1 V313 DKP # 836-S NCT | Anti-Fingerprint
HANDLE: Aluminum DKP #5230 | Ivory
HANDLE: Aluminum DKP #5230 | Dark Choco

Dkbb
157 Praditmanutham Road
Bangkapi Bangkok 10240
TEL:0-2515-1162 FAX:0-2515-1161
WWW.decorschoice.co.th


Client : Ari789	Design : WIC2-4B	View : Plan
Address :	Series : Elegance	Scale : 1:25
Province :	Drawn by :Jirayu Kidrakmuang	Date : 17/10/2569
Phone :	Email :	Page : 1-3

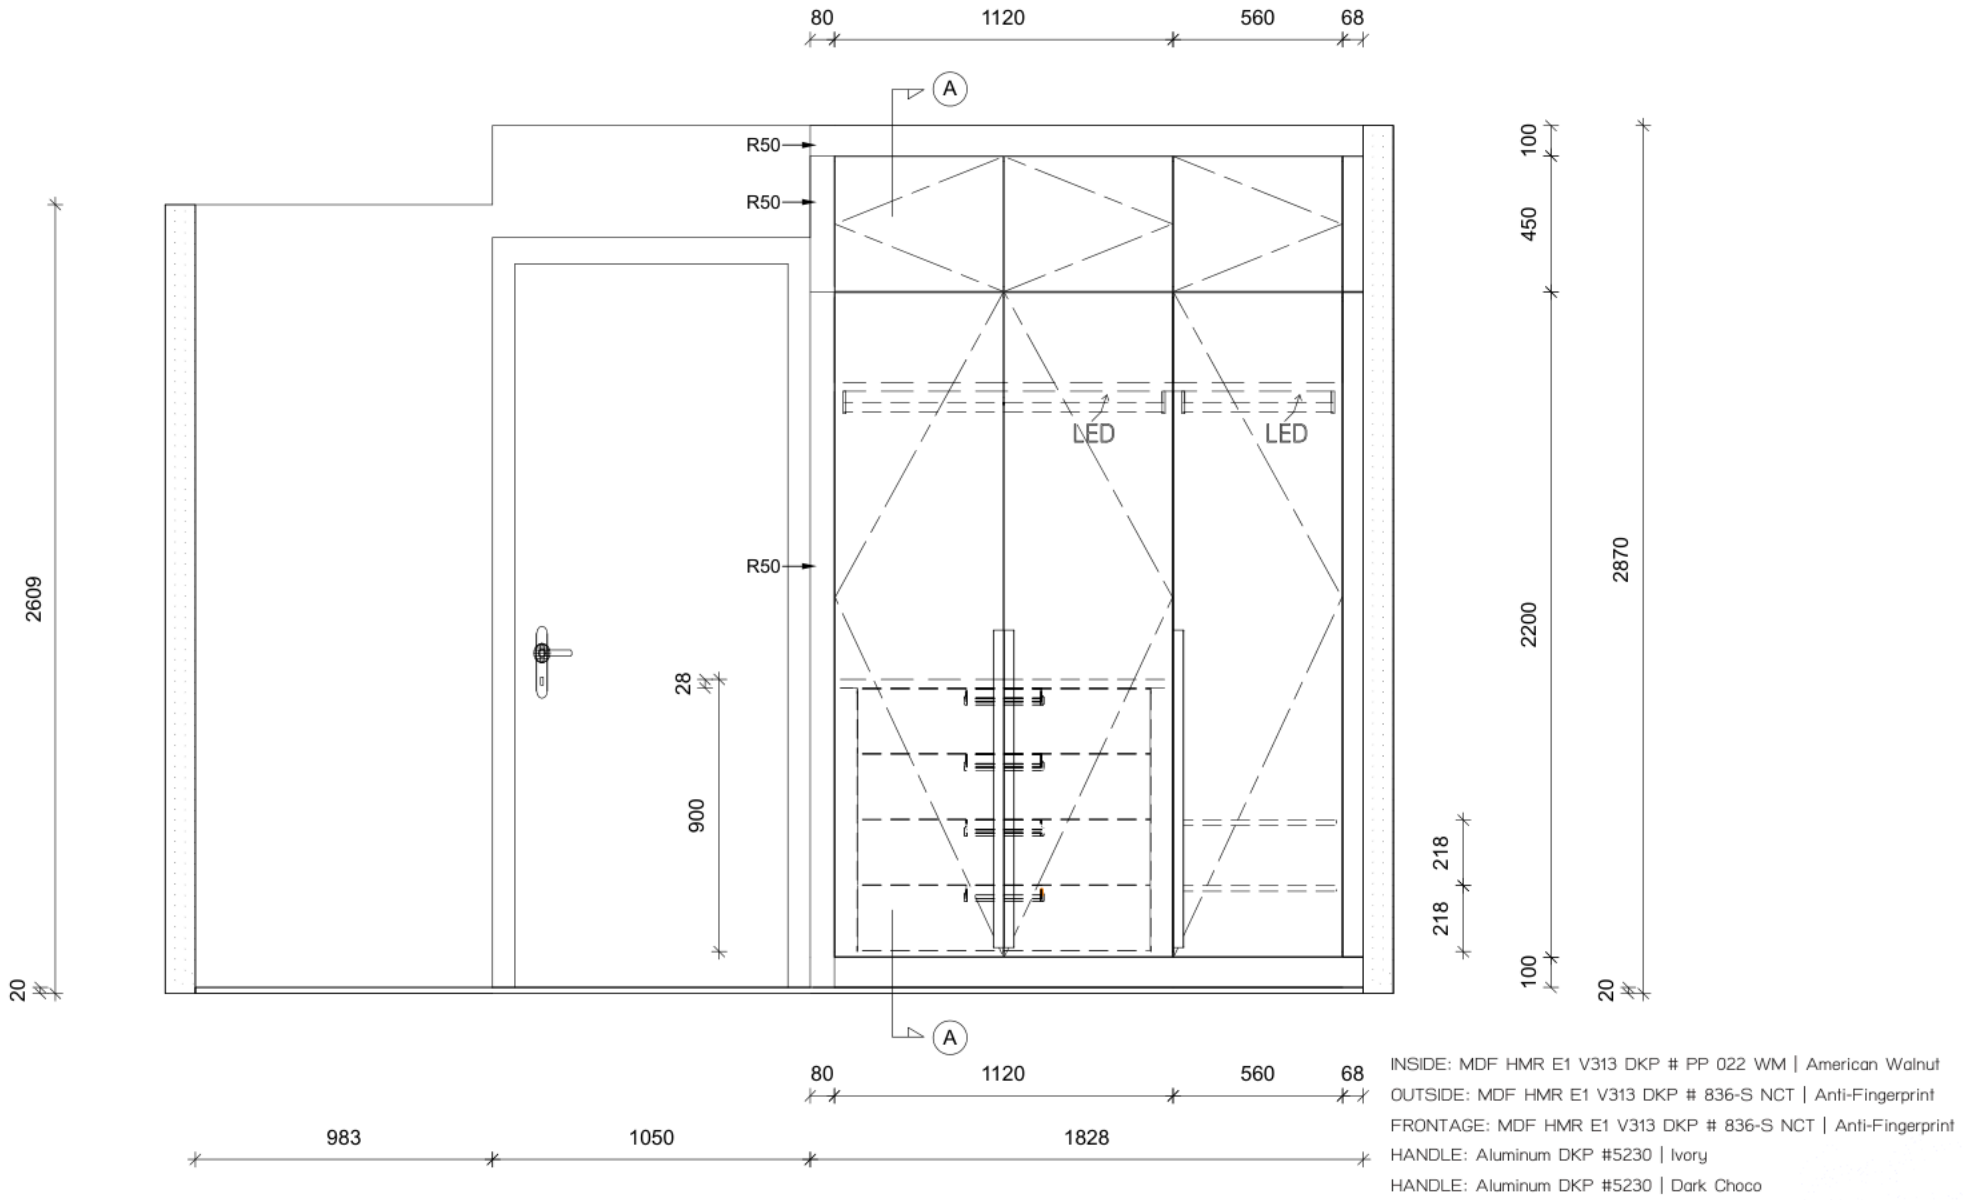

INSIDE: MDF HMR E1 V313 DKP # PP 022 WM | American Walnut
OUTSIDE: MDF HMR E1 V313 DKP # 836-S NCT | Anti-Fingerprint
FRONTAGE: MDF HMR E1 V313 DKP # 836-S NCT | Anti-Fingerprint
HANDLE: Aluminum DKP #5230 | Ivory
HANDLE: Aluminum DKP #5230 | Dark Choco

Dkbb
157 Praditmanutham Road
Bangkapi Bangkok 10240
TEL:0-2515-1162 FAX:0-2515-1161
WWW.decorschoice.co.th


Client : Ari789	Design : WIC2-4B	View : Elevation
Address :	Series : Elegance	Scale : 1:25
Province :	Drawn by :Jirayu Kidrakmuang	Date : 17/10/2569
Phone :	Email :	Page : 2-3

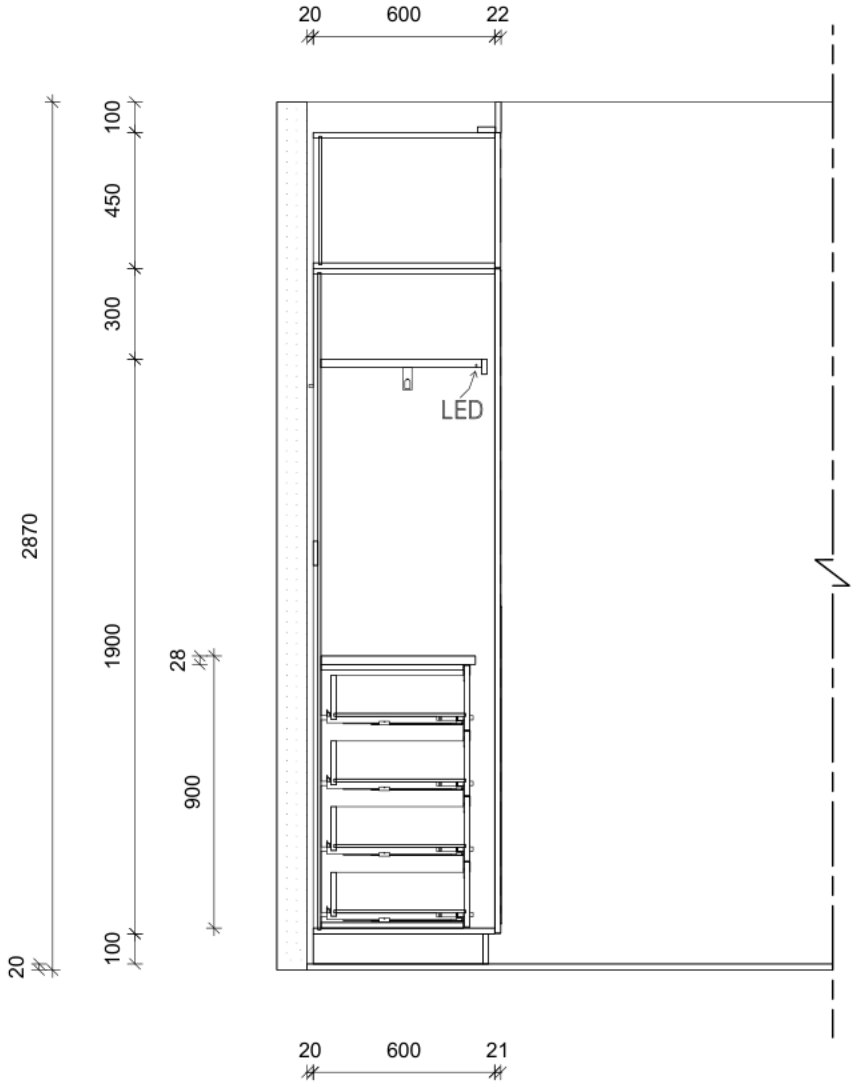

INSIDE: MDF HMR E1 V313 DKP # PP 022 WM | American Walnut
OUTSIDE: MDF HMR E1 V313 DKP # 836-S NCT | Anti-Fingerprint
FRONTAGE: MDF HMR E1 V313 DKP # 836-S NCT | Anti-Fingerprint
HANDLE: Aluminum DKP #5230 | Ivory
HANDLE: Aluminum DKP #5230 | Dark Choco

Dkbb
157 Praditmanutham Road
Bangkapi Bangkok 10240
TEL:0-2515-1162 FAX:0-2515-1161
WWW.decorschoice.co.th


Client : Ari789	Design : WIC2-4B	View : Section
Address :	Series : Elegance	Scale : 1:25
Province :	Drawn by :Jirayu Kidrakmuang	Date : 17/10/2569
Phone :	Email :	Page : 3-3

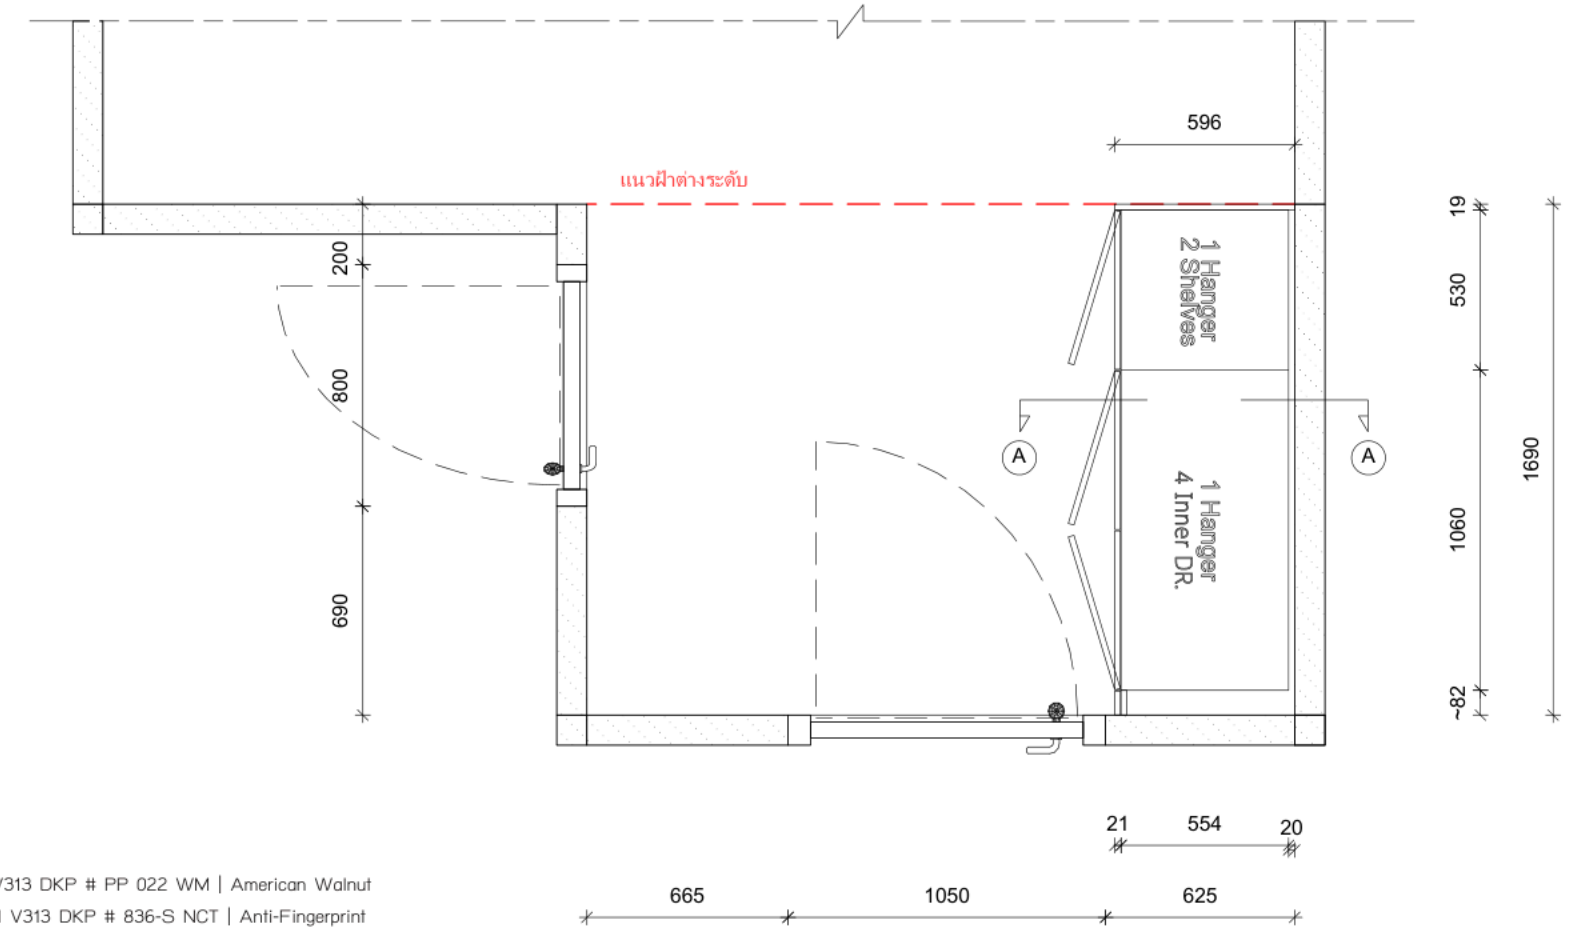


INSIDE: MDF HMR E1 V313 DKP # PP 022 WM | American Walnut
OUTSIDE: MDF HMR E1 V313 DKP # 836-S NCT | Anti-Fingerprint
FRONTAGE: MDF HMR E1 V313 DKP # 836-S NCT | Anti-Fingerprint
HANDLE: Aluminum DKP #5230 | Ivory
HANDLE: Aluminum DKP #5230 | Dark Choco

Dkbb
157 Praditmanutham Road
Bangkapi Bangkok 10240
TEL:0-2515-1162 FAX:0-2515-1161
WWW.decorschoice.co.th

Client : Ari789	Design : WIC1 - 4B	View : Plan
Address :	Series : Elegance	Scale : 1:25
Province :	Drawn by : Jirayu Kidrakmuang	Date : 19/10/2569
Phone :	Email :	Page : 1-2

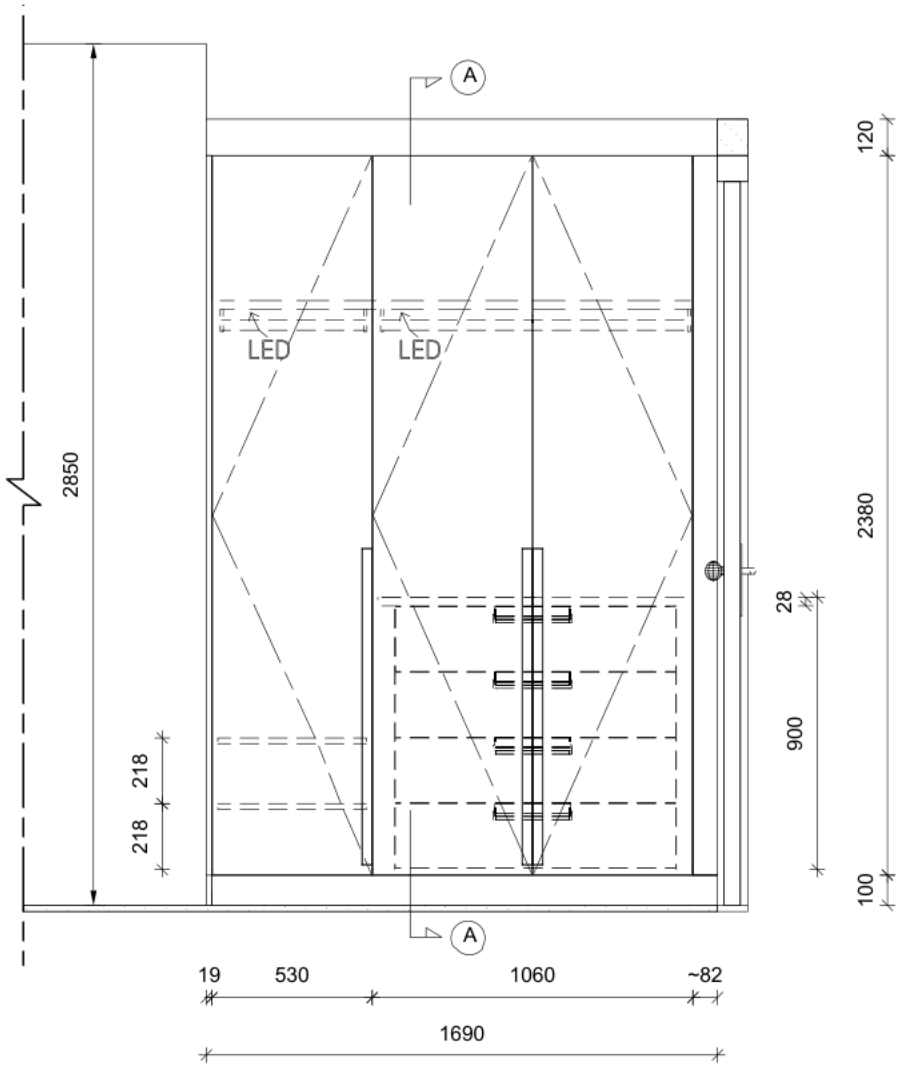

ELEVATION

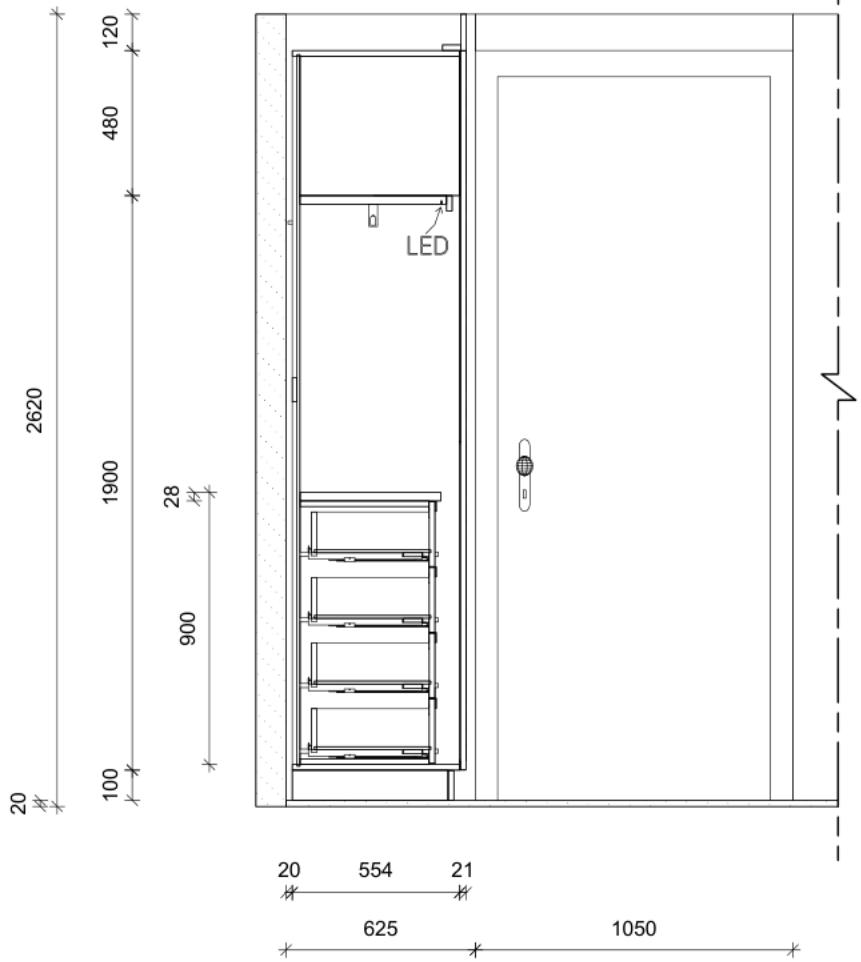

SECTION

INSIDE: MDF HMR E1 V313 DKP # PP 022 WM | American Walnut
OUTSIDE: MDF HMR E1 V313 DKP # 836-S NCT | Anti-Fingerprint
FRONTAGE: MDF HMR E1 V313 DKP # 836-S NCT | Anti-Fingerprint

HANDLE: Aluminum DKP #5230 | Ivory
HANDLE: Aluminum DKP #5230 | Dark Choco

Dkbb
157 Praditmanutham Road
Bangkapi Bangkok 10240
TEL:0-2515-1162 FAX:0-2515-1161
WWW.decorschoice.co.th

Client : Ari789	Design : WIC1 - 4B	View : Elevation , Section
Address :	Series : Elegance	Scale : 1:25
Province :	Drawn by : Jirayu Kidrakmuang	Date : 19/10/2569
Phone :	Email :	Page : 2-2