

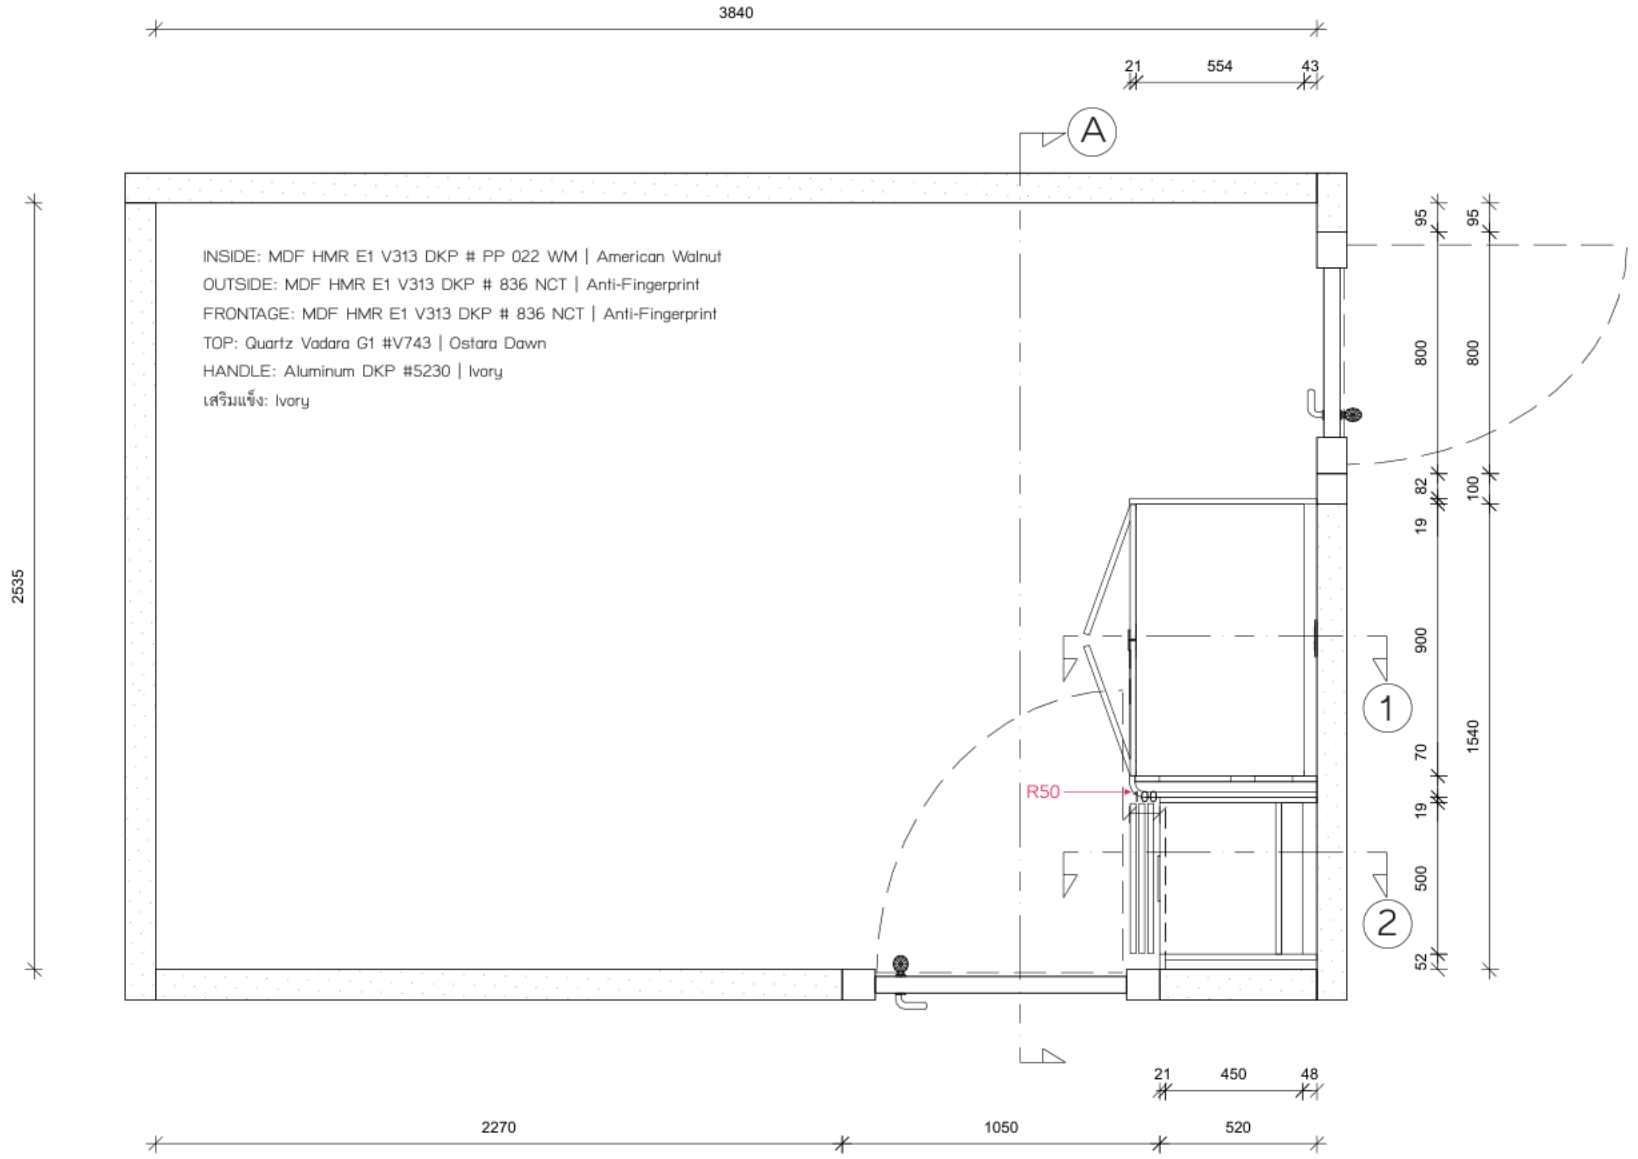


Dkbb 157 Praditmanutham Road Bangkapi Bangkok 10240 TEL:0-2515-1162 FAX:0-2515-1161 WWW.decorschoice.co.th	Client : Ari789	Design : WIC2-4C	View : Plan
	Address :	Series : Elegance	Scale : 1:25
	Province :	Drawn by : บริวัตร สุนทรจามร	Date : 19/10/2569
	Phone :	Email :	Page : 01


INSIDE: MDF HMR E1 V313 DKP # PP 022 WM | American Walnut
OUTSIDE: MDF HMR E1 V313 DKP # 836 NCT | Anti-Fingerprint
FRONTAGE: MDF HMR E1 V313 DKP # 836 NCT | Anti-Fingerprint
TOP: Quartz Vadara G1 #V743 | Ostara Dawn
HANDLE: Aluminum DKP #5230 | Ivory
เสริมแข็ง: Ivory

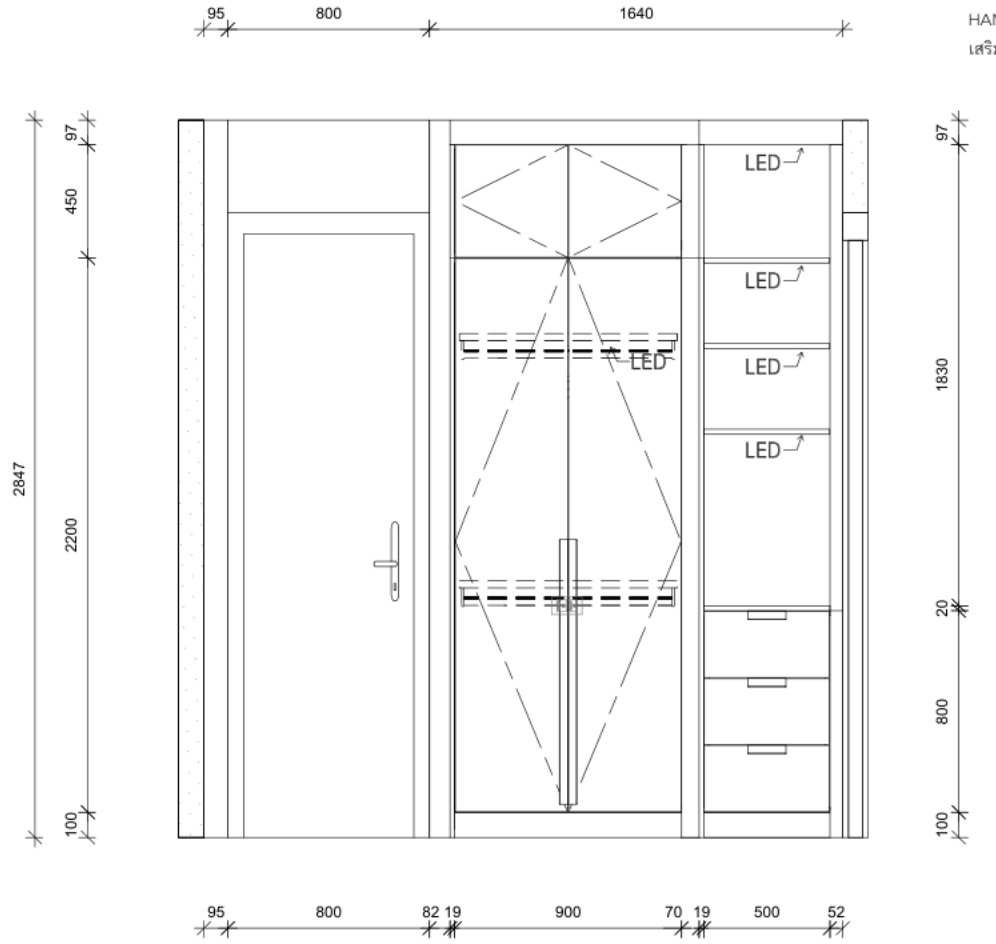

ELEVATION A

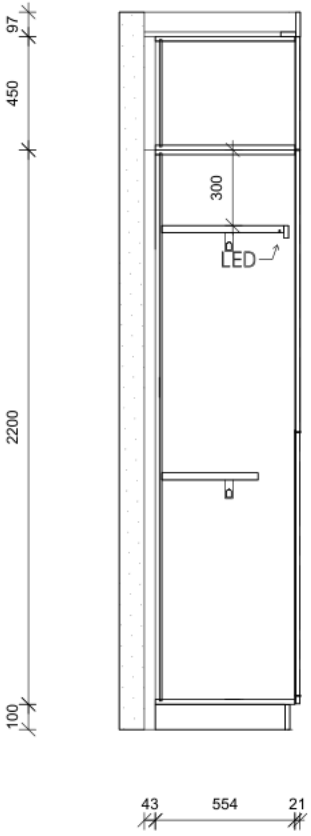


SECTION 1

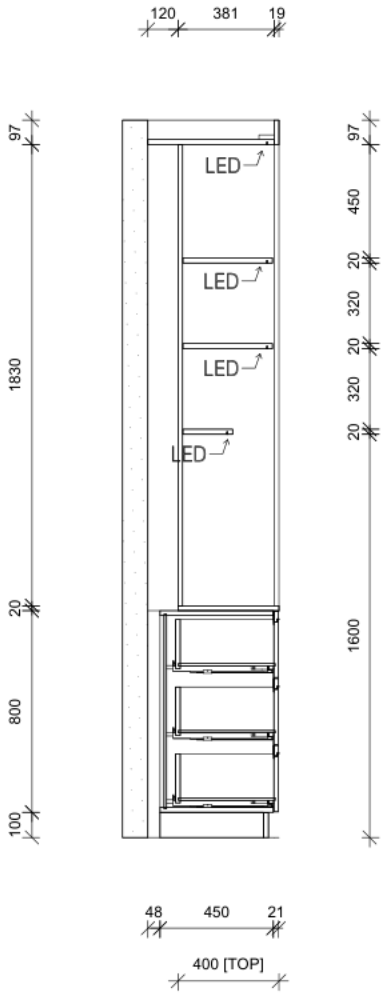

SECTION 2

Dkbb
157 Praditmanutham Road
Bangkapi Bangkok 10240
TEL:0-2515-1162 FAX:0-2515-1161
WWW.decorschoice.co.th


Client : Ari789	Design : WIC2-4C	View : Elevation A , Section1-2
Address :	Series : Elegance	Scale : 1:30
Province :	Drawn by : บริวัตร สุนทรจามร	Date : 19/10/2569
Phone :	Email :	Page : 02

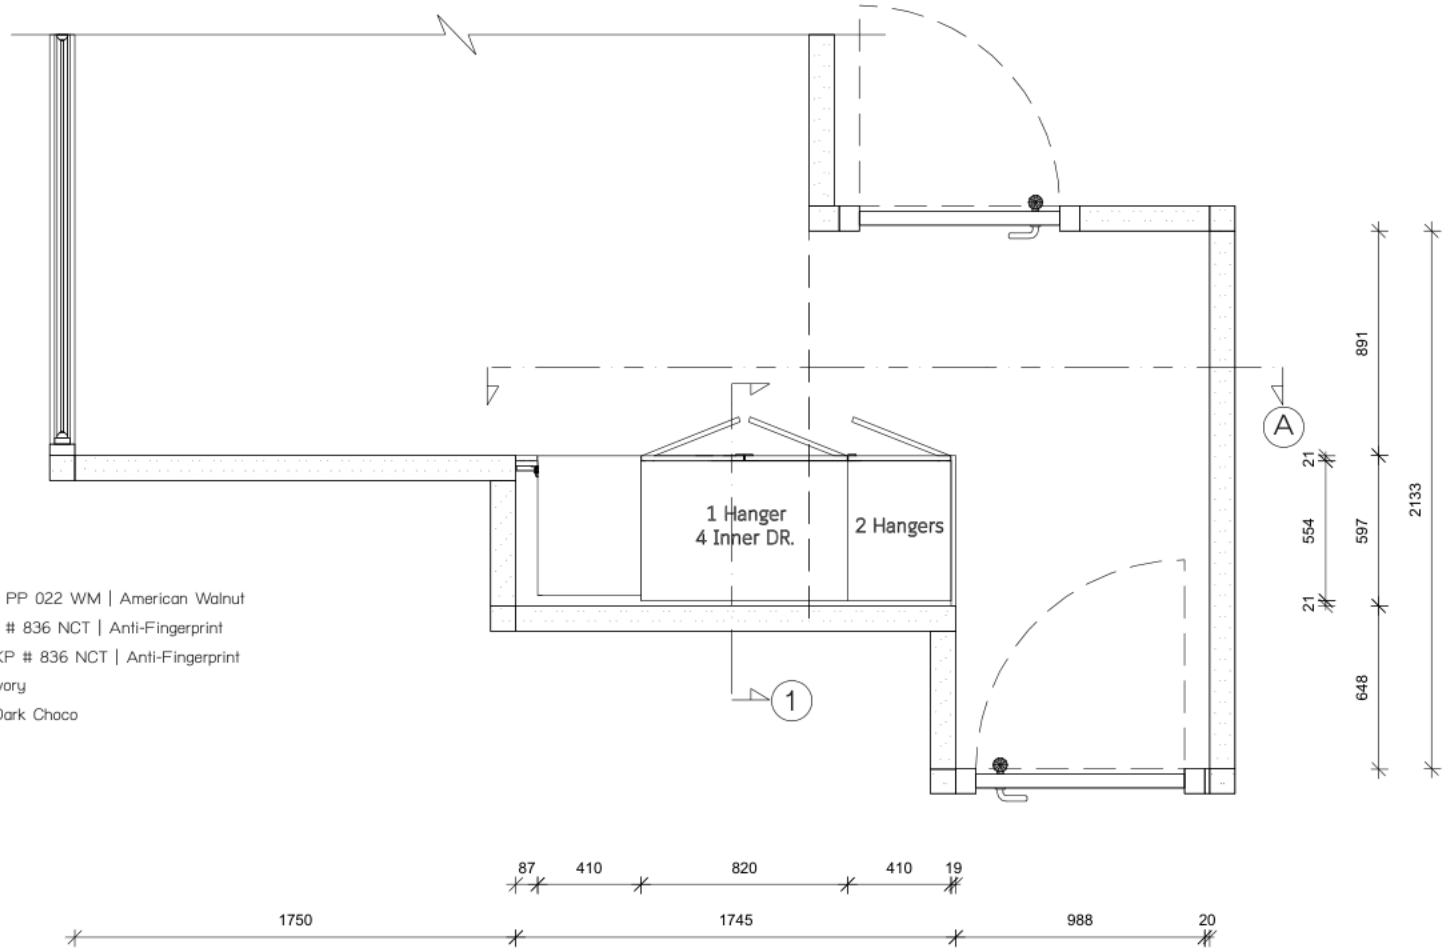


INSIDE: MDF HMR E1 V313 DKP # PP 022 WM | American Walnut
OUTSIDE: MDF HMR E1 V313 DKP # 836 NCT | Anti-Fingerprint
FRONTAGE: MDF HMR E1 V313 DKP # 836 NCT | Anti-Fingerprint
HANDLE: Aluminum DKP #5230 | Ivory
HANDLE: Aluminum DKP #5230 | Dark Choco

Dkbb
157 Praditmanutham Road
Bangkapi Bangkok 10240
TEL:0-2515-1162 FAX:0-2515-1161
WWW.decorschoice.co.th

Client : Ari789	Design : WIC1-4C	View : Plan
Address :	Series : Elegance	Scale : 1:30
Province :	Drawn by : บริวัตร สุนทรจามร	Date : 19/9/2569
Phone :	Email :	Page : 01

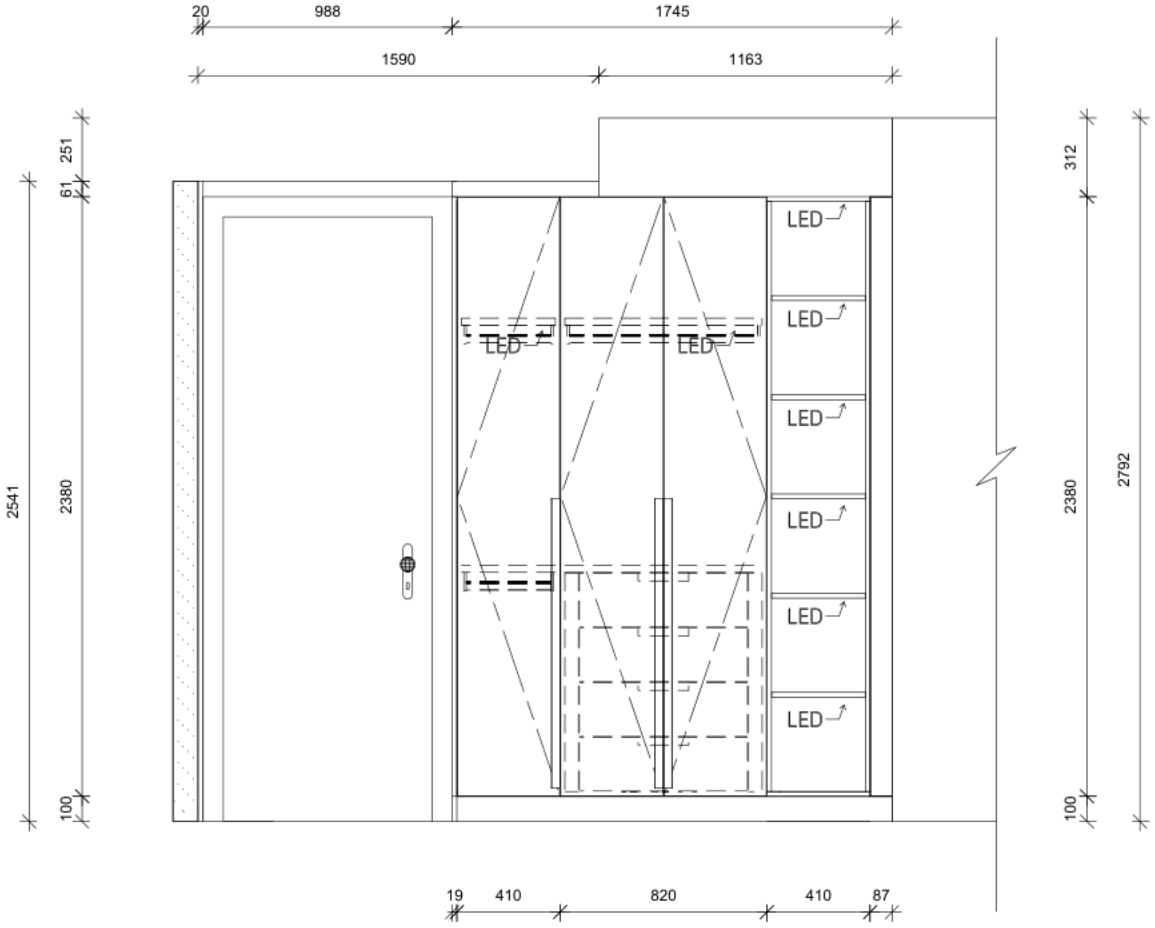

ELEVATION A

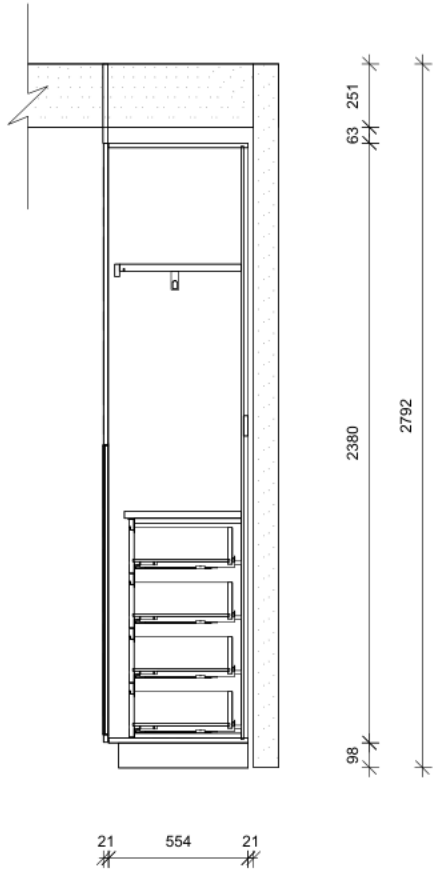


SECTION 1

Dkbb
157 Praditmanutham Road
Bangkapi Bangkok 10240
TEL:0-2515-1162 FAX:0-2515-1161
WWW.decorschoice.co.th

Client : Ari789	Design : WIC1-4C	View : Elevation A , Section 1
Address :	Series : Elegance	Scale : 1:30
Province :	Drawn by : บริวัตร สุนทรจามร	Date : 19/9/2569
Phone :	Email :	Page : 02

FOR REVIEW - NOT FINAL

INSIDE: MDF HMR E1 V313 DKP # PP 022 WM | American Walnut
OUTSIDE: MDF HMR E1 V313 DKP # 836 NCT | Anti-Fingerprint
FRONTAGE: MDF HMR E1 V313 DKP # 836 NCT | Anti-Fingerprint
HANDLE: Aluminum DKP #5230 | Ivory
HANDLE: Aluminum DKP #5230 | Dark Choco
TOP: Quartz Vadara G1 #V743 | Ostara Dawn
FRONTAGE: Aluminum DKP #5158 (มีมือจับในตัว) | Dark Choco ,
กรุกระจก ใส TYK | Euro Bronze 5 mm. (Tempered)
MIRROR: Aluminum DKP #5158 (มีมือจับในตัว) | Ivory ,
กรุกระจกเงา TYK 5 mm.

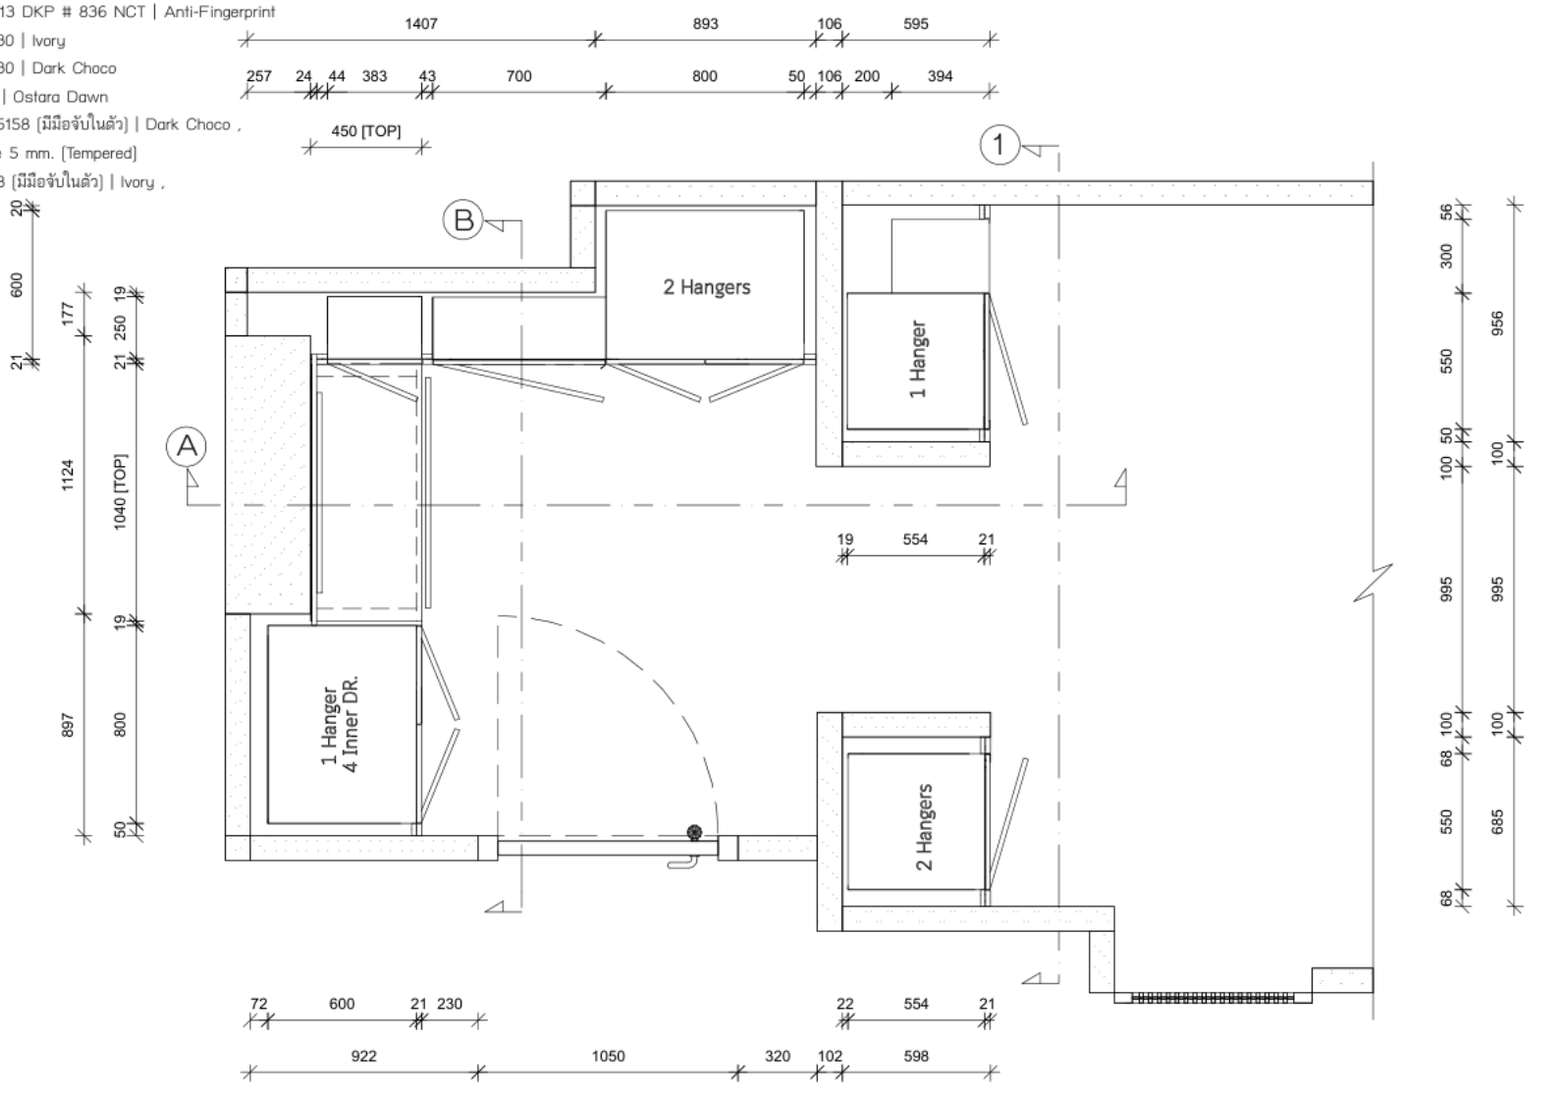


Dkbb 157 Praditmanutham Road Bangkapi Bangkok 10240 TEL:0-2515-1162 FAX:0-2515-1161 WWW.decorschoice.co.th	Client : Ari789	Design : WICMB-4C	View : Plan
	Address :	Series : Elegance	Scale : 1:30
	Province :	Drawn by : บริวัตร สุนทรจามร	Date : 8/10/2569
	Phone :	Email :	Page : 01


FOR REVIEW - NOT FINAL

INSIDE: MDF HMR E1 V313 DKP # PP 022 WM | American Walnut
OUTSIDE: MDF HMR E1 V313 DKP # 836 NCT | Anti-Fingerprint
FRONTAGE: MDF HMR E1 V313 DKP # 836 NCT | Anti-Fingerprint
HANDLE: Aluminum DKP #5230 | Ivory
HANDLE: Aluminum DKP #5230 | Dark Choco
TOP: Quartz Vadara G1 #V743 | Ostara Dawn

FRONTAGE: Aluminum DKP #5158 (มีมือจับในตัว) | Dark Choco , กรุกระจก ใส TYK | Euro Bronze 5 mm. (Tempered)
MIRROR: Aluminum DKP #5158 (มีมือจับในตัว) | Ivory , กรุกระจกเงา TYK 5 mm.

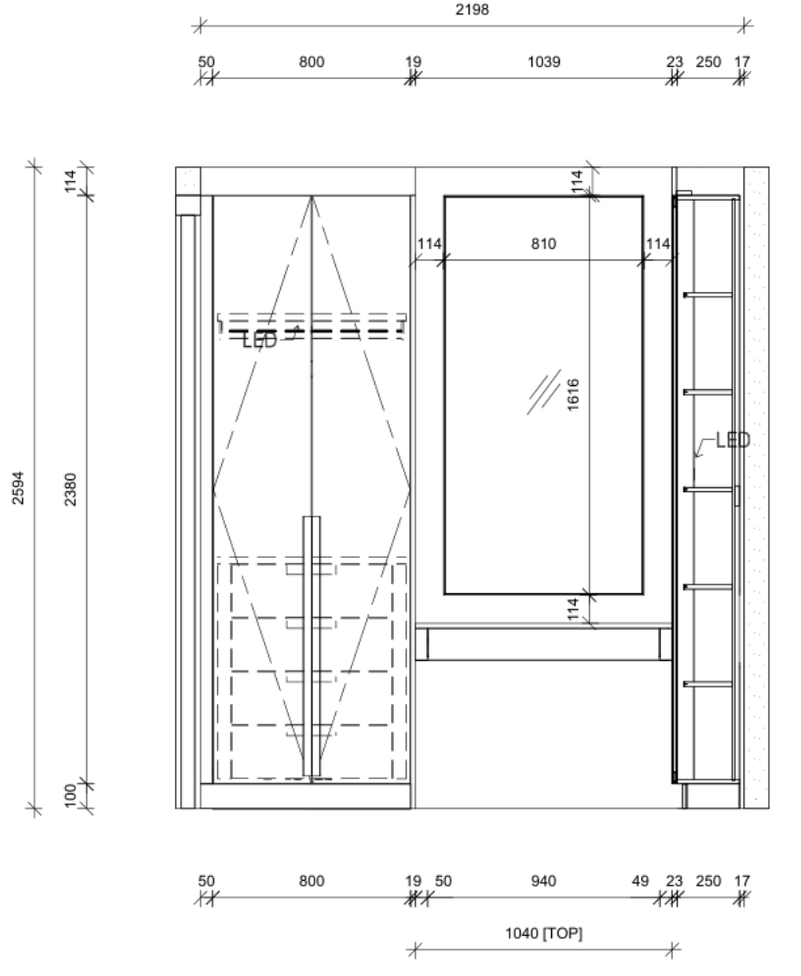

ELEVATION A

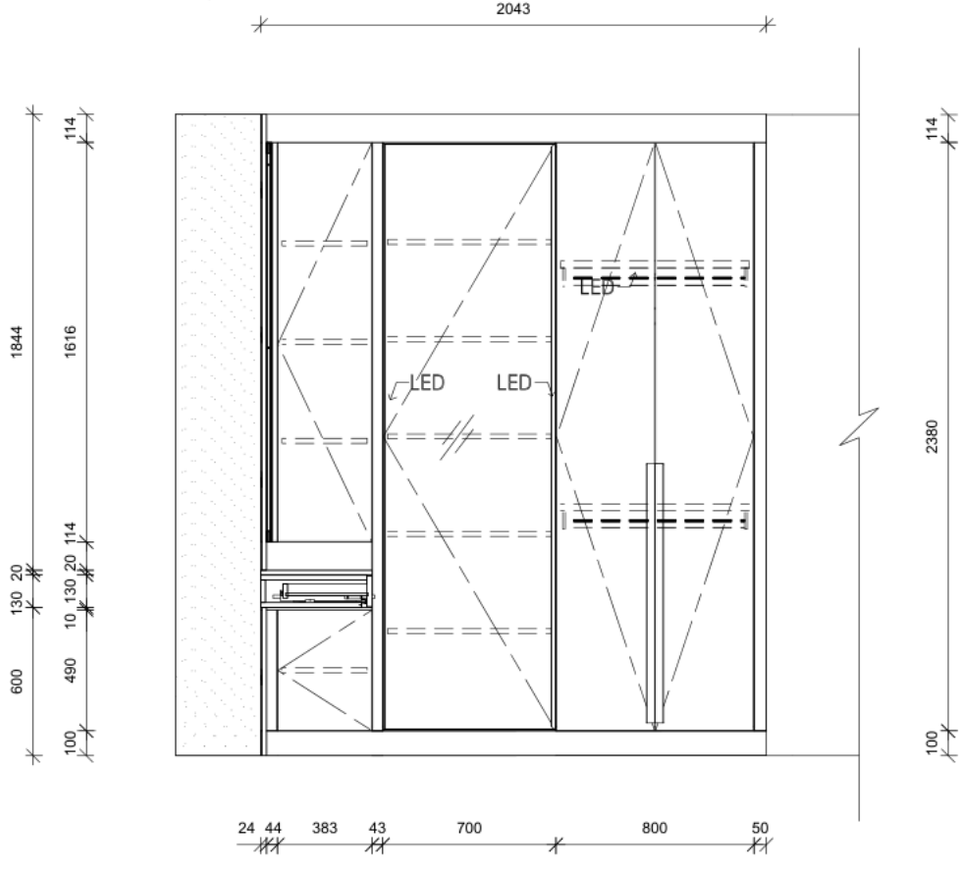


ELEVATION B

Dkbb 157 Praditmanutham Road Bangkapi Bangkok 10240 TEL:0-2515-1162 FAX:0-2515-1161 WWW.decorschoice.co.th	Client : Ari789	Design : WICMB-4C	View : Elevation A , Elevation B
	Address :	Series : Elegance	Scale : 1:30
	Province :	Drawn by : บริวัตร สุนทรจามร	Date : 8/10/2569
	Phone :	Email :	Page : 02

FOR REVIEW - NOT FINAL

INSIDE: MDF HMR E1 V313 DKP # PP 022 WM | American Walnut
OUTSIDE: MDF HMR E1 V313 DKP # 836 NCT | Anti-Fingerprint
FRONTAGE: MDF HMR E1 V313 DKP # 836 NCT | Anti-Fingerprint
HANDLE: Aluminum DKP #5230 | Ivory
HANDLE: Aluminum DKP #5230 | Dark Choco
TOP: Quartz Vadara G1 #V743 | Ostara Dawn
FRONTAGE: Aluminum DKP #5158 (มีมือจับในตัว) | Dark Choco ,
กรุกระจก ใส TYK | Euro Bronze 5 mm. (Tempered)
MIRROR: Aluminum DKP #5158 (มีมือจับในตัว) | Ivory ,
กรุกระจกเงา TYK 5 mm.

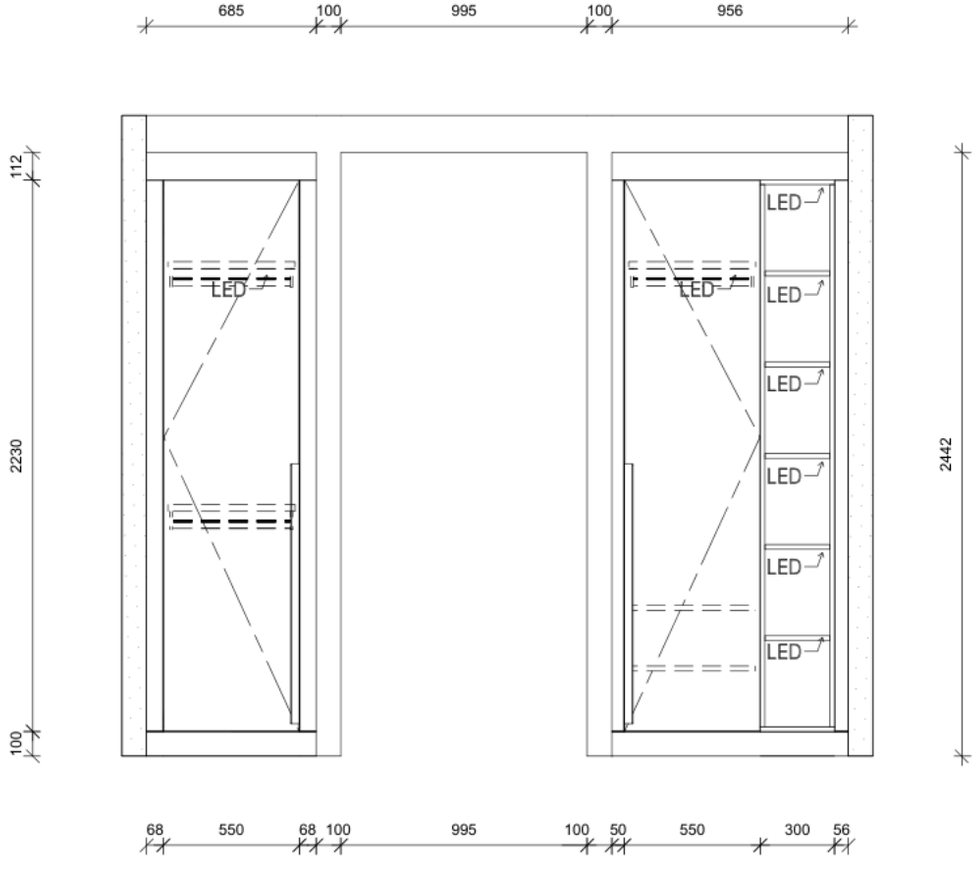

ELEVATION C

Dkbb
157 Praditmanutham Road
Bangkapi Bangkok 10240
TEL:0-2515-1162 FAX:0-2515-1161
WWW.decorschoice.co.th

Client : Ari789	Design : WICMB-4C	View : Elevation C
Address :	Series : Elegance	Scale : 1:30
Province :	Drawn by : บริวัตร สุนทรจามร	Date : 8/10/2569
Phone :	Email :	Page : 03