



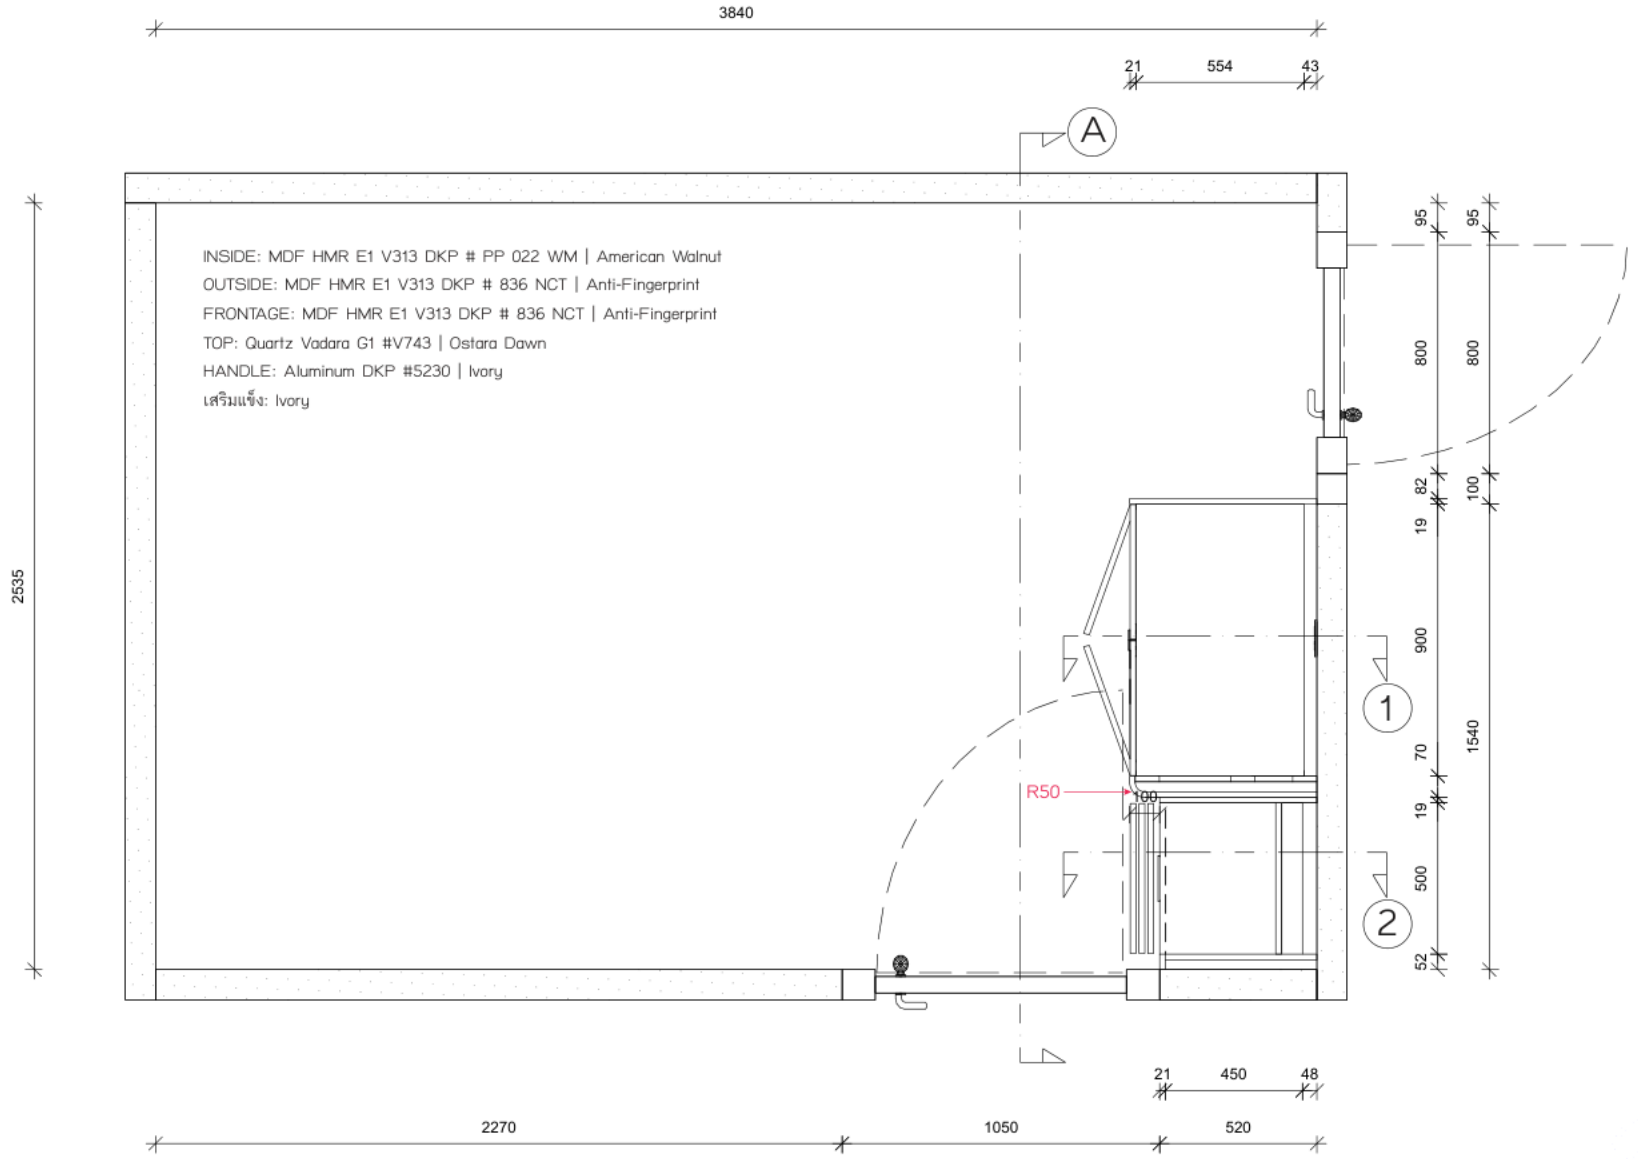




Dkbb 157 Praditmanutham Road Bangkapi Bangkok 10240 TEL:0-2515-1162 FAX:0-2515-1161 WWW.decorschoice.co.th	Client : Ari789	Design : WIC2-4C	View : Plan
	Address :	Series : Elegance	Scale : 1:25
	Province :	Drawn by : บริวัตร สุนทรจามร	Date : 19/10/2569
	Phone :	Email :	Page : 01


INSIDE: MDF HMR E1 V313 DKP # PP 022 WM | American Walnut
OUTSIDE: MDF HMR E1 V313 DKP # 836 NCT | Anti-Fingerprint
FRONTAGE: MDF HMR E1 V313 DKP # 836 NCT | Anti-Fingerprint
TOP: Quartz Vadara G1 #V743 | Ostara Dawn
HANDLE: Aluminum DKP #5230 | Ivory
เสริมแข็ง: Ivory

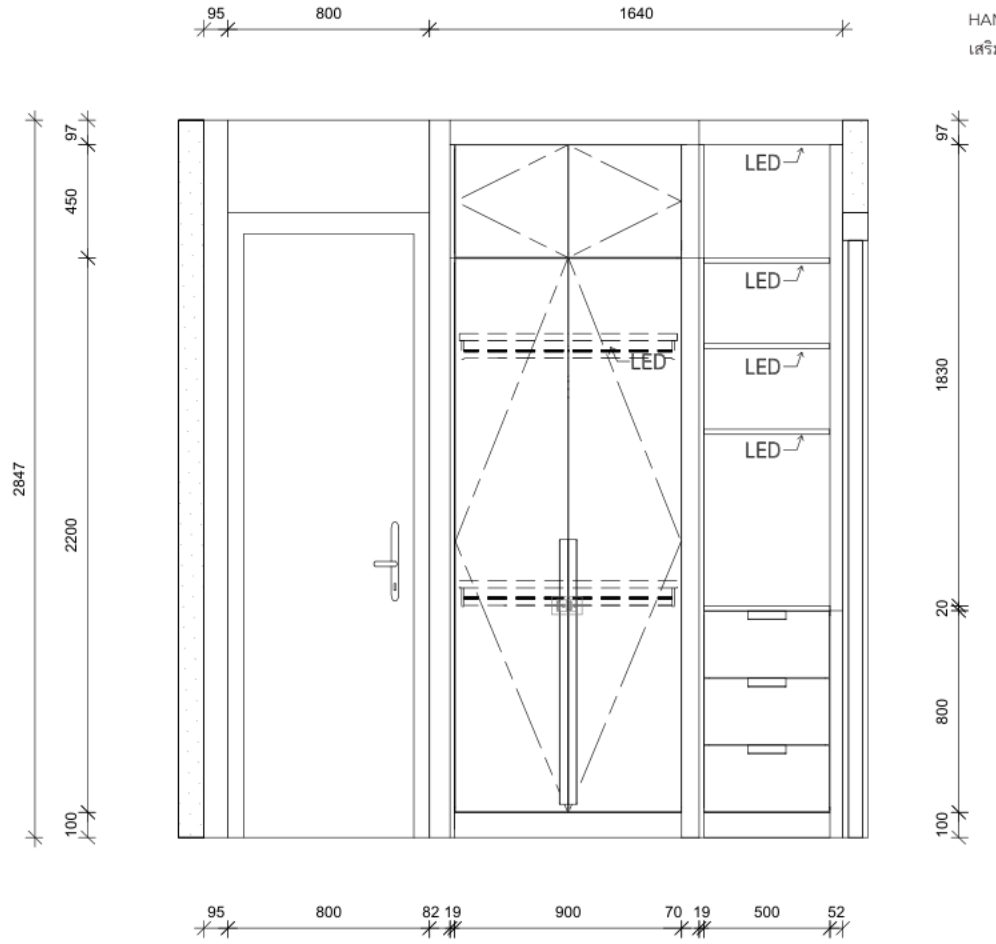

ELEVATION A

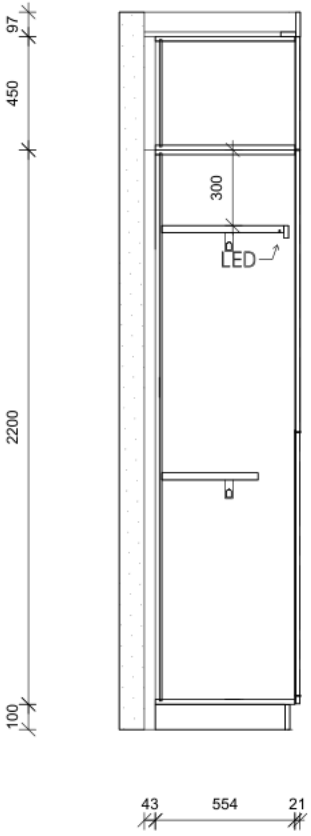

SECTION 1

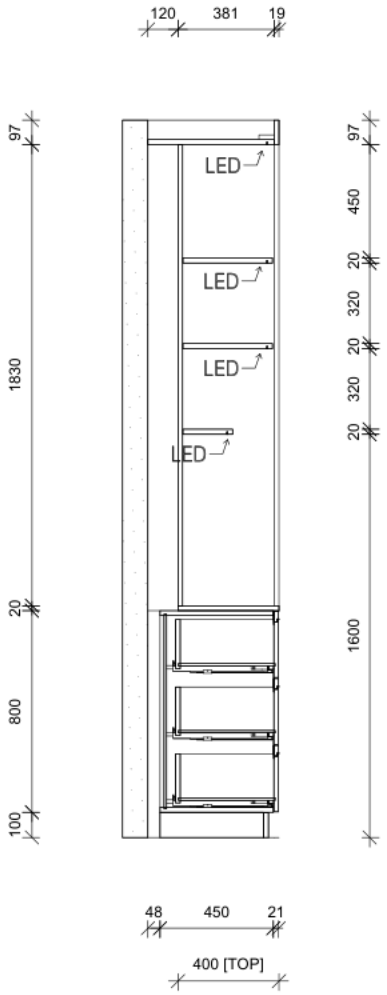

SECTION 2

Dkbb
157 Praditmanutham Road
Bangkapi Bangkok 10240
TEL:0-2515-1162 FAX:0-2515-1161
WWW.decorschoice.co.th

Client : Ari789	Design : WIC2-4C	View : Elevation A , Section1-2
Address :	Series : Elegance	Scale : 1:30
Province :	Drawn by : บริวัตร สุนทรจามร	Date : 19/10/2569
Phone :	Email :	Page : 02

Dkbb

ใบสรุปเฟอร์นิเจอร์ บริษัท อารี789 ดีเวลลอปเมนท์ จากัด

เลขที่ 10/1 ซอยพหลโยธิน 5 ถนนพหลโยธิน แขวงพญาไท เขตพญาไท

กรุงเทพมหานคร 10400 โทร : 044-110218

เลขประจาตัวผู้เสียภาษีอากร 0105565012642 (สานักงานใหญ่)

20 ตุลาคม 2569

Q.26/0906-1

4C Floor 4 : Walk-in closet (Bedroom 2) รุ่น ELEGANCE

1	ตู้เสื้อผ้าบานเปิด ขนาด 0.618 X 0.989 X 2.847 ม./	114,960.00
	รวม	114,960.00
	ส่วนลด 15%	-17,244.00
	ยอดรวม หลังหักส่วนลด	97,716.00
2	ไฟ LED ในตู้เสื้อผ้าบานเปิด / ตู้เก็บของ	5,000.00
	รวมเงิน Ex. Vat	**102,716.00**
	VAT 7%	**7,190.12**
	ยอดสุทธิ	**109,906.12**

หมายเหตุ - ก่อนเซ็นสั่งซื้อสินค้า กรุณาตรวจสอบแบบและรายละเอียดต่างๆ ให้ครบถ้วน เนื่องจากเป็นการสั่งผลิตเฉพาะงาน

- ไฟแสงสว่าง, สีของไฟ LED, ตำแหน่งปลั๊กใช้งาน, กุญแจล็อคต่างๆ ไม่สามารถเพิ่มภายหลังได้ กรุณาตรวจสอบก่อนว่ามีครบตามต้องการหรือไม่
- หลังจากสั่งซื้อสินค้าแล้ว ทางบริษัทฯ ขอสงวนสิทธิ์ในการแก้ไขใดๆทั้งสิ้น

บริษัท เดคคอร์ส ช้อยส์ จำกัด

157 ซ.โยธินพัฒนา ถ.ประดิษฐ์มนูธรรม แขวงคลองจั่น เขตบางกะปิ กรุงเทพฯ 10240


Tel : 0 2515 1162 Fax : 0 2515 1161 Call Center : 08-1954-5550

E-mail : decorchoice@gmail.com www.decorschoice.co.th


Samsung Apps
Your Video
Web Browser
USA TODAY
AllShare Play
ESPN ScoreCenter


Samsung Apps
Your Video
Web Browser
USA TODAY
AllShare Play




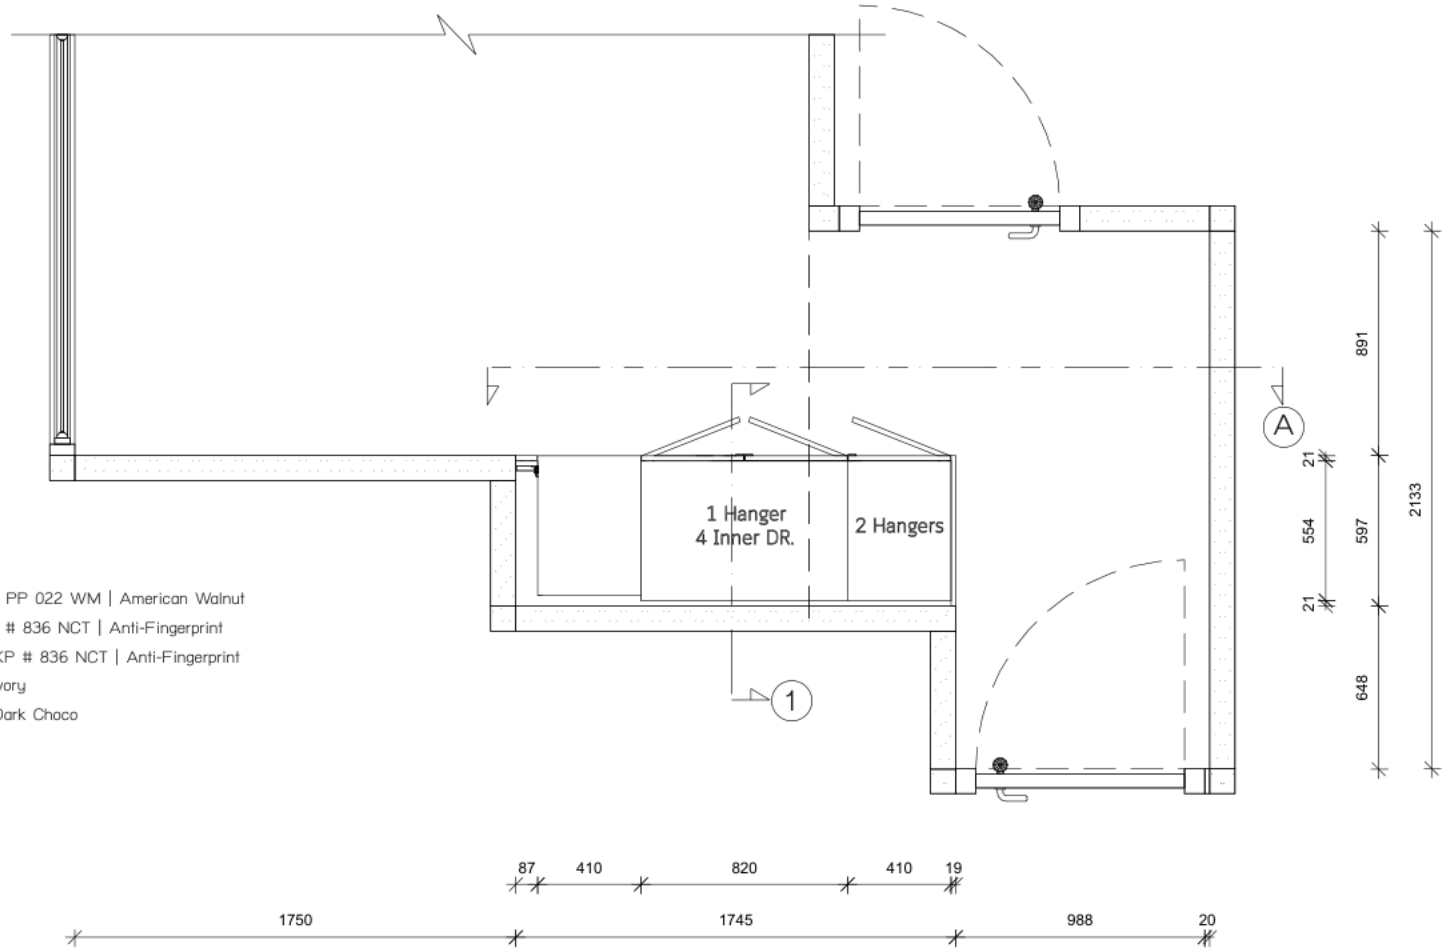


INSIDE: MDF HMR E1 V313 DKP # PP 022 WM | American Walnut
OUTSIDE: MDF HMR E1 V313 DKP # 836 NCT | Anti-Fingerprint
FRONTAGE: MDF HMR E1 V313 DKP # 836 NCT | Anti-Fingerprint
HANDLE: Aluminum DKP #5230 | Ivory
HANDLE: Aluminum DKP #5230 | Dark Choco

Dkbb
157 Praditmanutham Road
Bangkapi Bangkok 10240
TEL:0-2515-1162 FAX:0-2515-1161
WWW.decorschoice.co.th

Client : Ari789	Design : WIC1-4C	View : Plan
Address :	Series : Elegance	Scale : 1:30
Province :	Drawn by : บริวัตร สุนทรจามร	Date : 19/9/2569
Phone :	Email :	Page : 01

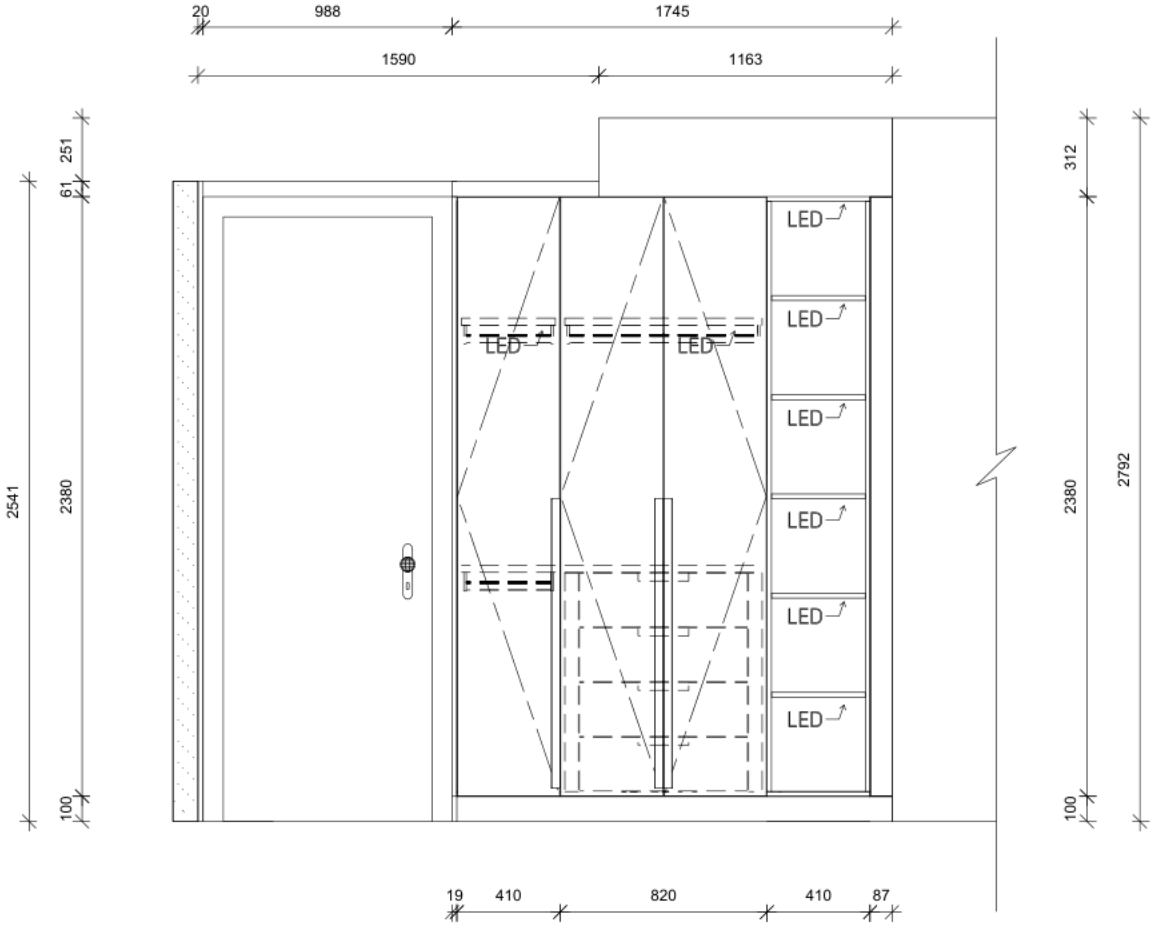

ELEVATION A

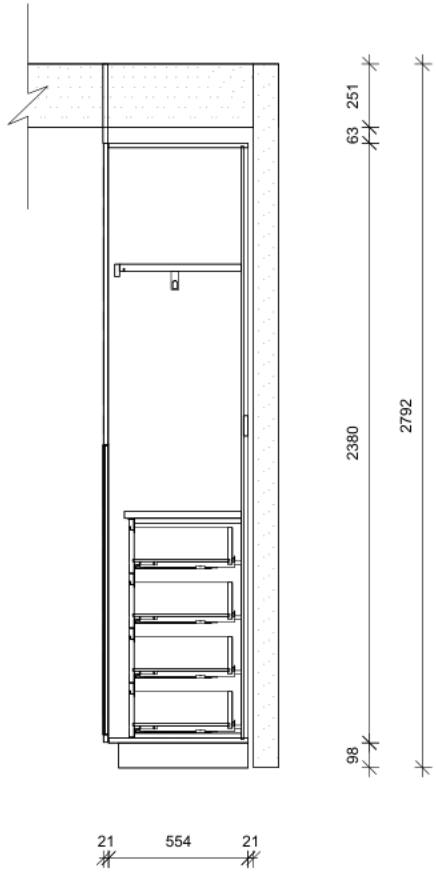

SECTION 1

Dkbb
157 Praditmanutham Road
Bangkapi Bangkok 10240
TEL:0-2515-1162 FAX:0-2515-1161
WWW.decorschoice.co.th

Client : Ari789	Design : WIC1-4C	View : Elevation A , Section 1
Address :	Series : Elegance	Scale : 1:30
Province :	Drawn by : บริวัตร สุนทรจามร	Date : 19/9/2569
Phone :	Email :	Page : 02

Dkbb

ใบสรุปเฟอร์นิเจอร์ บริษัท อารี789 ดีเวลลอปเมนท์ จากัด

เลขที่ 10/1 ซอยพหลโยธิน 5 ถนนพหลโยธิน แขวงพญาไท เขตพญาไท

กรุงเทพมหานคร 10400 โทร : 044-110218

เลขประจาตัวผู้เสียภาษีอากร 0105565012642 (สานักงานใหญ่)

2 ตุลาคม 2569

Q.26/1005

4C Floor 4 : Walk-in closet (Bedroom 1) รุ่น ELEGANCE

1	ตู้เสื้อผ้าบานเปิดตัว I ขนาด 0.596 X 1.745 X 2.792 ม.	118,587.00
	รวม	118,587.00
	ส่วนลด 15%	-17,788.00
	ยอดรวม หลังหักส่วนลด	100,799.00
2	ไฟ LED ในตู้เสื้อผ้าบานเปิดตัว I	5,490.00
	รวมเงิน Ex. Vat	**106,289.00**
	VAT 7%	**7,440.23**
	ยอดสุทธิ	**113,729.23**

หมายเหตุ - ก่อนเซ็นสั่งซื้อสินค้า กรุณาตรวจสอบแบบและรายละเอียดต่างๆ ให้ครบถ้วน เนื่องจากเป็นการสั่งผลิตเฉพาะงาน

- ไฟแสงสว่าง, สีของไฟ LED, ตำแหน่งปลั๊กใช้งาน, กุญแจล็อคต่างๆ ไม่สามารถเพิ่มภายหลังได้ กรุณาตรวจสอบก่อนว่ามีครบตามต้องการหรือไม่
- หลังจากสั่งซื้อสินค้าแล้ว ทางบริษัทฯ ขอสงวนสิทธิ์ในการแก้ไขใดๆทั้งสิ้น

บริษัท เดคคอร์ส ช้อยส์ จำกัด

157 ซ.โยธินพัฒนา ถ.ประดิษฐ์มนูธรรม แขวงคลองจั่น เขตบางกะปิ กรุงเทพฯ 10240

Tel : 0 2515 1162 Fax : 0 2515 1161 Call Center : 08-1954-5550

E-mail : decorchoice@gmail.com www.decorschoice.co.th


MACBETH
PARIS
THE ODYSSEY


MACBETH
PARIS
THE ODYSSEY


DIOR



CHANEL


CHANEL



FOR REVIEW - NOT FINAL

INSIDE: MDF HMR E1 V313 DKP # PP 022 WM | American Walnut
OUTSIDE: MDF HMR E1 V313 DKP # 836 NCT | Anti-Fingerprint
FRONTAGE: MDF HMR E1 V313 DKP # 836 NCT | Anti-Fingerprint
HANDLE: Aluminum DKP #5230 | Ivory
HANDLE: Aluminum DKP #5230 | Dark Choco
TOP: Quartz Vadara G1 #V743 | Ostara Dawn
FRONTAGE: Aluminum DKP #5158 (มีมือจับในตัว) | Dark Choco ,
กรุกระจก ใส TYK | Euro Bronze 5 mm. (Tempered)
MIRROR: Aluminum DKP #5158 (มีมือจับในตัว) | Ivory ,
กรุกระจกเงา TYK 5 mm.

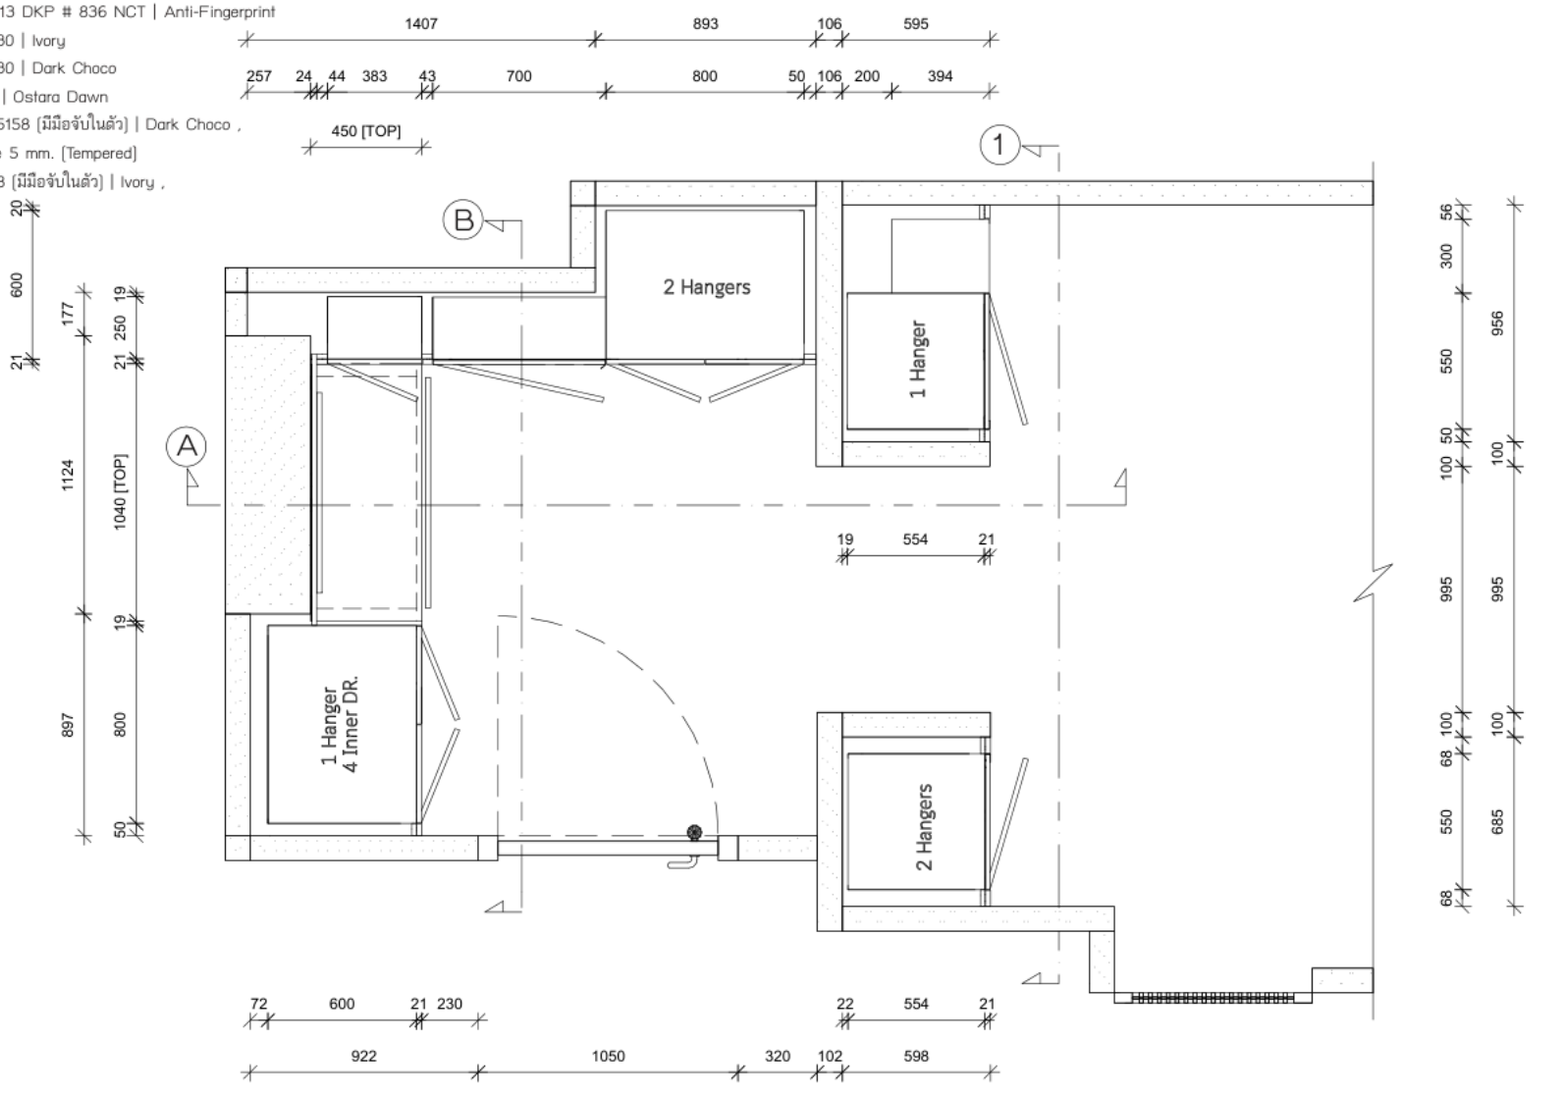


Dkbb 157 Praditmanutham Road Bangkapi Bangkok 10240 TEL:0-2515-1162 FAX:0-2515-1161 WWW.decorschoice.co.th	Client : Ari789	Design : WICMB-4C	View : Plan
	Address :	Series : Elegance	Scale : 1:30
	Province :	Drawn by : บริวัตร สุนทรจามร	Date : 8/10/2569
	Phone :	Email :	Page : 01


FOR REVIEW - NOT FINAL

INSIDE: MDF HMR E1 V313 DKP # PP 022 WM | American Walnut
OUTSIDE: MDF HMR E1 V313 DKP # 836 NCT | Anti-Fingerprint
FRONTAGE: MDF HMR E1 V313 DKP # 836 NCT | Anti-Fingerprint
HANDLE: Aluminum DKP #5230 | Ivory
HANDLE: Aluminum DKP #5230 | Dark Choco
TOP: Quartz Vadara G1 #V743 | Ostara Dawn

FRONTAGE: Aluminum DKP #5158 (มีมือจับในตัว) | Dark Choco , กรุกระจก ใส TYK | Euro Bronze 5 mm. (Tempered)
MIRROR: Aluminum DKP #5158 (มีมือจับในตัว) | Ivory , กรุกระจกเงา TYK 5 mm.

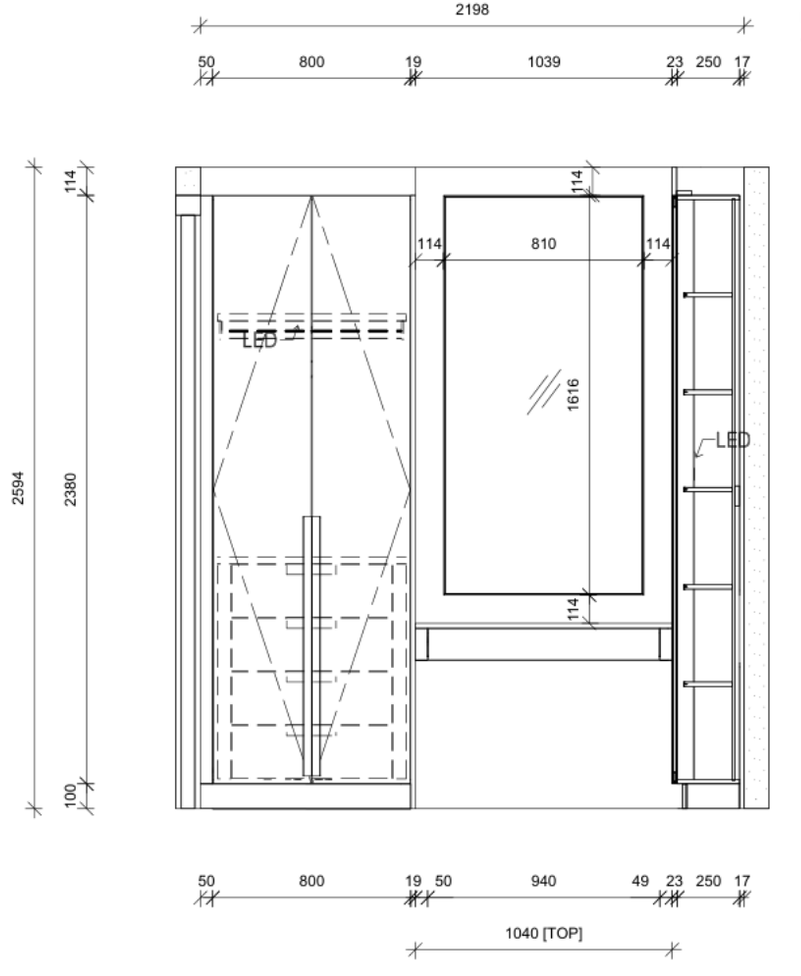

ELEVATION A

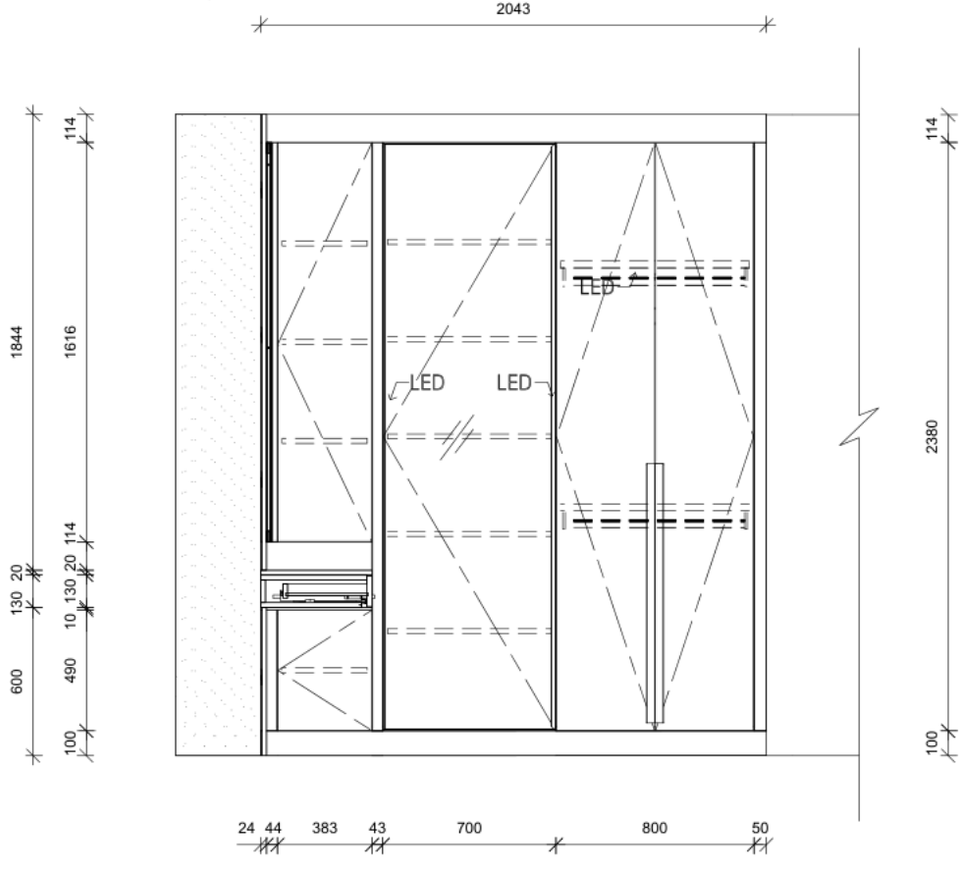


ELEVATION B

Dkbb 157 Praditmanutham Road Bangkapi Bangkok 10240 TEL:0-2515-1162 FAX:0-2515-1161 WWW.decorschoice.co.th	Client : Ari789	Design : WICMB-4C	View : Elevation A , Elevation B
	Address :	Series : Elegance	Scale : 1:30
	Province :	Drawn by : บริวัตร สุนทรจามร	Date : 8/10/2569
	Phone :	Email :	Page : 02

FOR REVIEW - NOT FINAL

INSIDE: MDF HMR E1 V313 DKP # PP 022 WM | American Walnut
OUTSIDE: MDF HMR E1 V313 DKP # 836 NCT | Anti-Fingerprint
FRONTAGE: MDF HMR E1 V313 DKP # 836 NCT | Anti-Fingerprint
HANDLE: Aluminum DKP #5230 | Ivory
HANDLE: Aluminum DKP #5230 | Dark Choco
TOP: Quartz Vadara G1 #V743 | Ostara Dawn
FRONTAGE: Aluminum DKP #5158 (มีมือจับในตัว) | Dark Choco ,
กรุกระจก ใส TYK | Euro Bronze 5 mm. (Tempered)
MIRROR: Aluminum DKP #5158 (มีมือจับในตัว) | Ivory ,
กรุกระจกเงา TYK 5 mm.

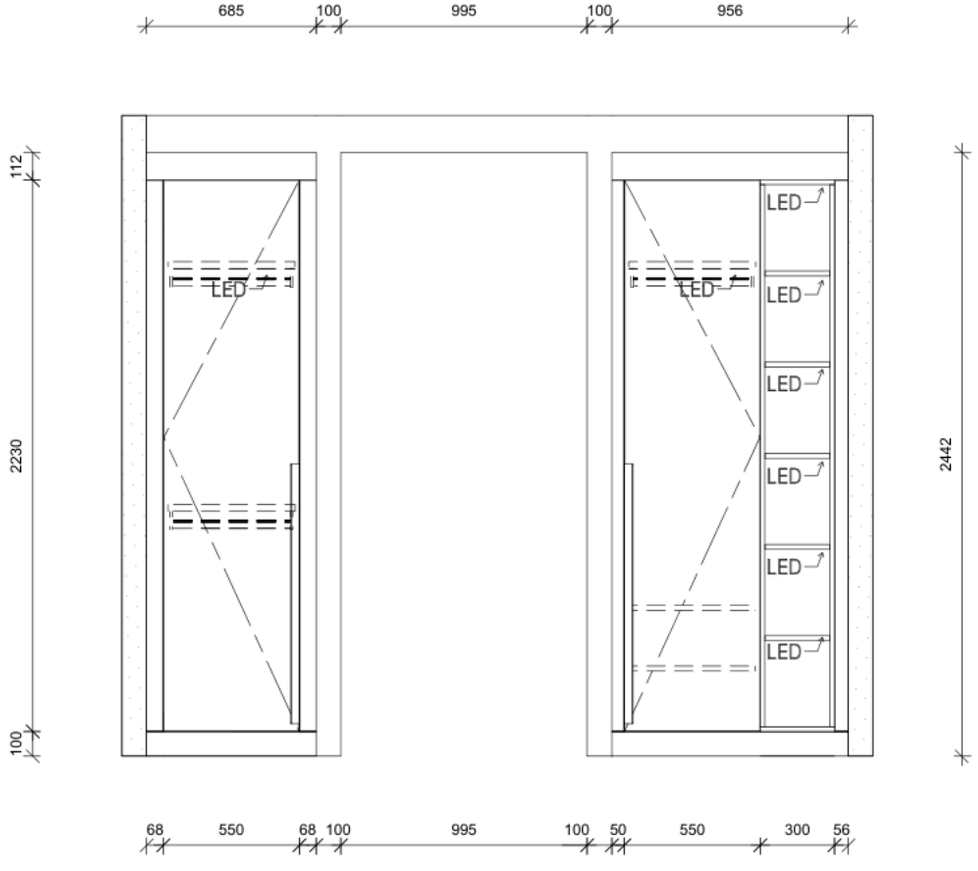

ELEVATION C

Dkbb
157 Praditmanutham Road
Bangkapi Bangkok 10240
TEL:0-2515-1162 FAX:0-2515-1161
WWW.decorschoice.co.th

Client : Ari789	Design : WICMB-4C	View : Elevation C
Address :	Series : Elegance	Scale : 1:30
Province :	Drawn by : บริวัตร สุนทรจามร	Date : 8/10/2569
Phone :	Email :	Page : 03

FOR REVIEW - NOT FINAL

Dkbb®

ใบสรุปเฟอร์นิเจอร์ บริษัท อารี789 ดีเวลลอปเมนท์ จากัด
เลขที่ 10/1 ซอยพหลโยธิน 5 ถนนพหลโยธิน แขวงพญาไท เขตพญาไท
กรุงเทพมหานคร 10400 โทร : 044-110218
เลขประจาตัวผู้เสียภาษีอากร 0105565012642 (สานักงานใหญ่)

Q.26/1006-1 **20 ตุลาคม 2569**

4C Floor 4 : Walk-in closet (Master Bedroom) รุ่น ELEGANCE

1	ตู้เสื้อผ้าพร้อมโต๊ะแต่งตัว ขนาด 0.641 X 4.241 X 2.594 ม.		202,383.00
2	ตู้เสื้อผ้าบานเปิดตัว I ขนาด 0.597 X 0.686 X 2.442 ม.		30,909.00
3	ตู้เสื้อผ้าบานเปิดตัว I ขนาด 0.595 X 0.956 X 2.442 ม.		43,171.00
		รวม	276,463.00
		ส่วนลด 15%	-41,469.00
		ยอดรวม หลังหักส่วนลด	234,994.00
4	ไฟ LED ในตู้เสื้อผ้าพร้อมโต๊ะแต่งตัว		9,910.00
5	ไฟ LED ในตู้เสื้อผ้าบานเปิดตัว I		1,600.00
6	ไฟ LED ในตู้เสื้อผ้าบานเปิดตัว I		3,700.00
		รวมเงิน Ex. Vat	**250,204.00**
		VAT 7%	**17,514.28**
		ยอดสุทธิ	**267,718.28**

หมายเหตุ - ก่อนเซ็นสั่งซื้อสินค้า กรุณาตรวจสอบแบบและรายละเอียดต่างๆ ให้ครบถ้วน
เนื่องจากเป็นการสั่งผลิตเฉพาะงาน
- ไฟแสงสว่าง, สีของไฟ LED, ตำแหน่งปลั๊กใช้งาน, กุญแจล็อคต่างๆ ไม่สามารถเพิ่มภายหลังได้
กรุณาตรวจสอบก่อนว่ามีครบตามต้องการหรือไม่
- หลังจากสั่งซื้อสินค้าแล้ว ทางบริษัทฯ ขอสงวนสิทธิ์ในการแก้ไขใดๆทั้งสิ้น

บริษัท เดคคอร์ส ช้อยส์ จำกัด
157 ซ.โยธินพัฒนา ถ.ประดิษฐ์มนูธรรม แขวงคลองจั่น เขตบางกะปิ กรุงเทพฯ 10240
Tel : 0 2515 1162 Fax : 0 2515 1161 Call Center : 08-1954-5550
E-mail : decorchoice@gmail.com www.decorschoice.co.th