

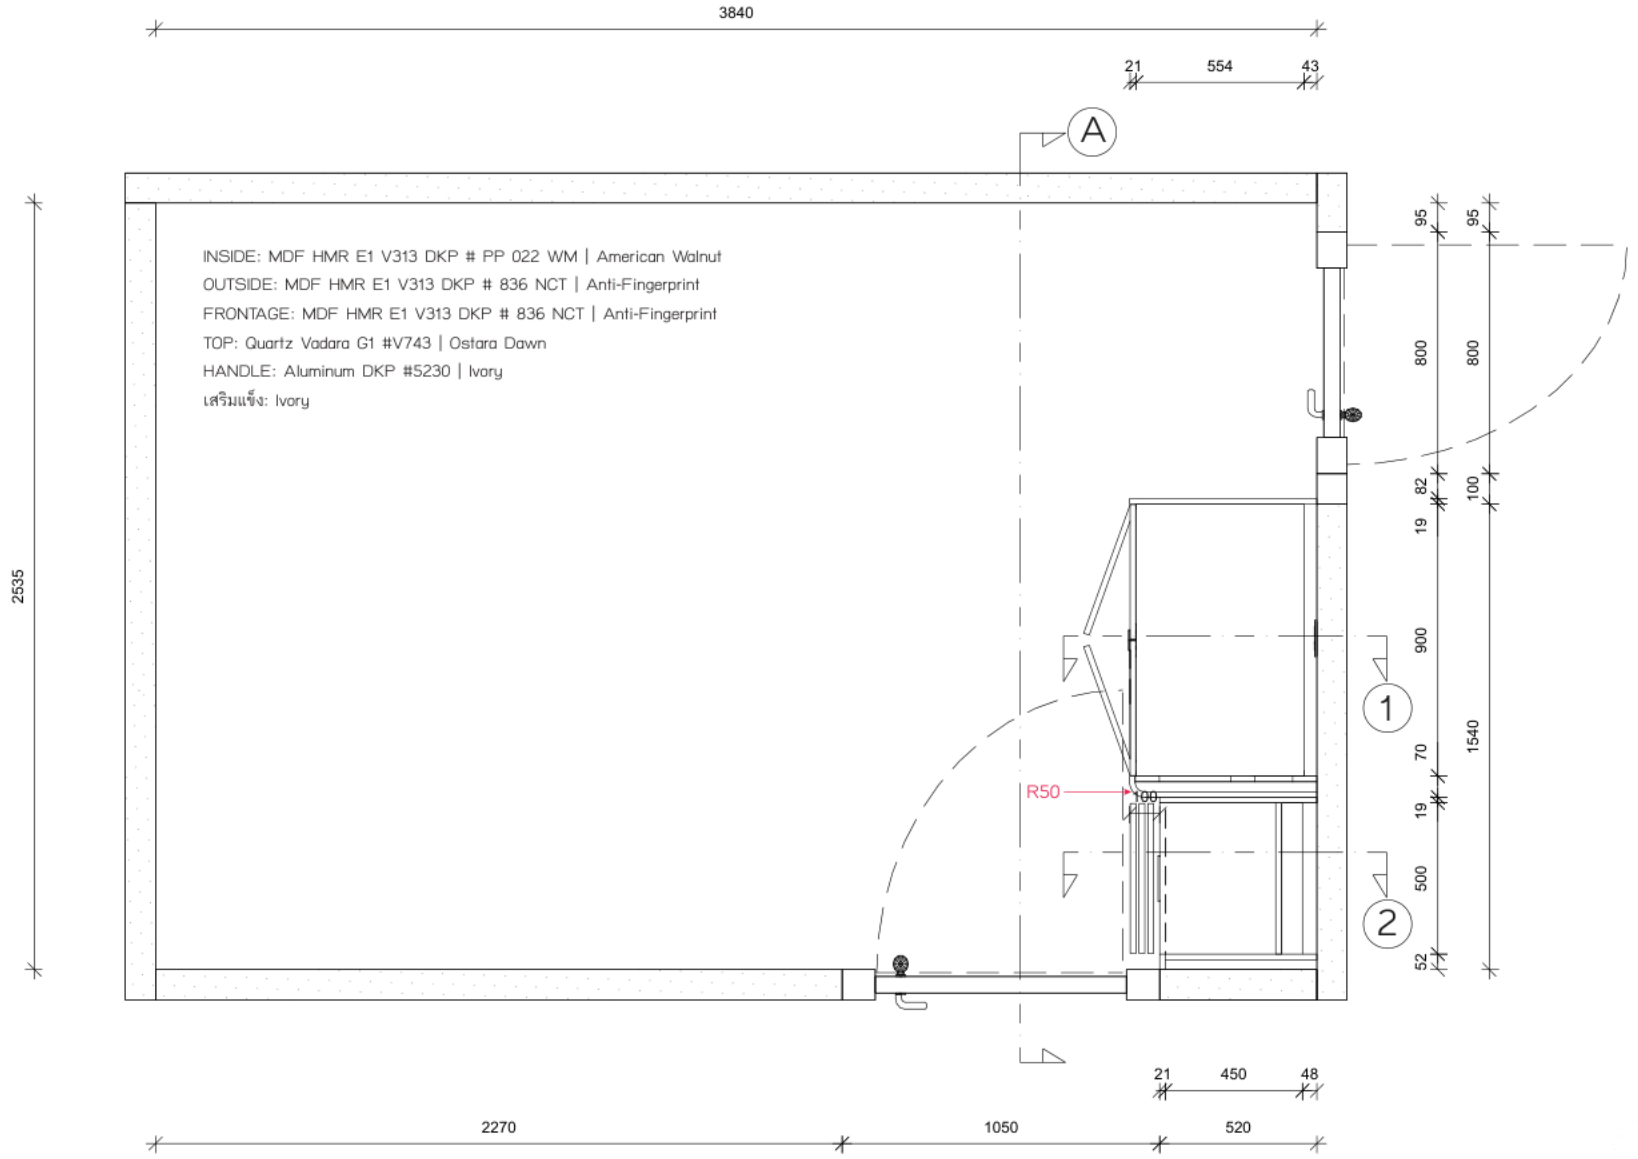


Dkbb 157 Praditmanutham Road Bangkapi Bangkok 10240 TEL:0-2515-1162 FAX:0-2515-1161 WWW.decorschoice.co.th	Client : Ari789	Design : WIC2-4C	View : Plan
	Address :	Series : Elegance	Scale : 1:25
	Province :	Drawn by : บริวัตร สุนทรจามร	Date : 19/10/2569
	Phone :	Email :	Page : 01


INSIDE: MDF HMR E1 V313 DKP # PP 022 WM | American Walnut
OUTSIDE: MDF HMR E1 V313 DKP # 836 NCT | Anti-Fingerprint
FRONTAGE: MDF HMR E1 V313 DKP # 836 NCT | Anti-Fingerprint
TOP: Quartz Vadara G1 #V743 | Ostara Dawn
HANDLE: Aluminum DKP #5230 | Ivory
เสริมแข็ง: Ivory

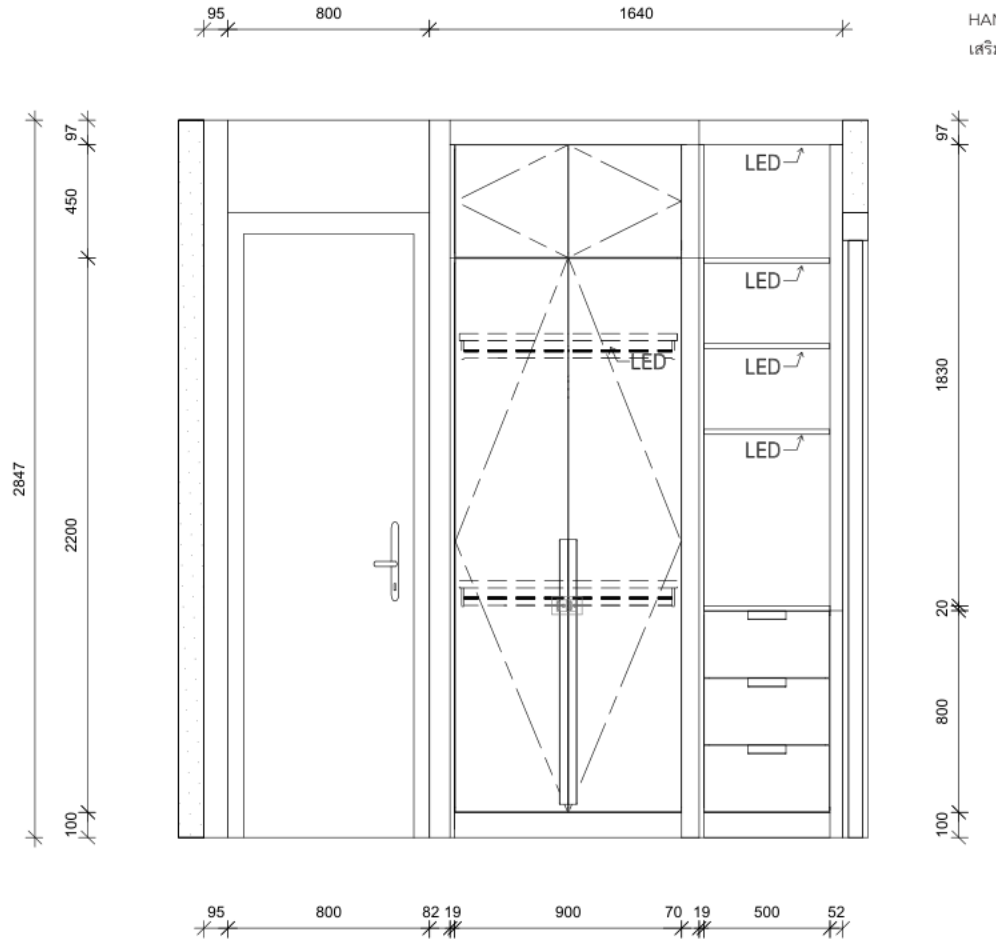

ELEVATION A

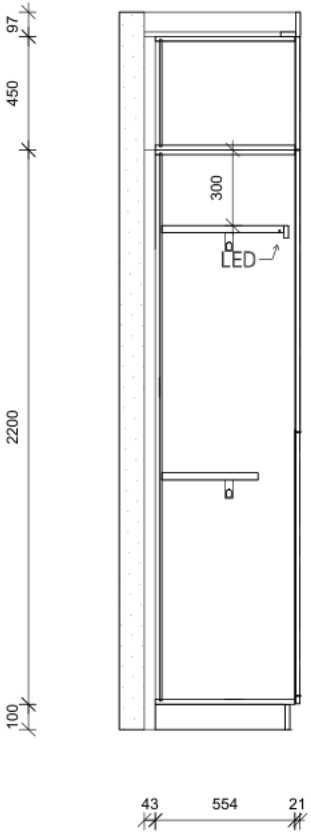

SECTION 1

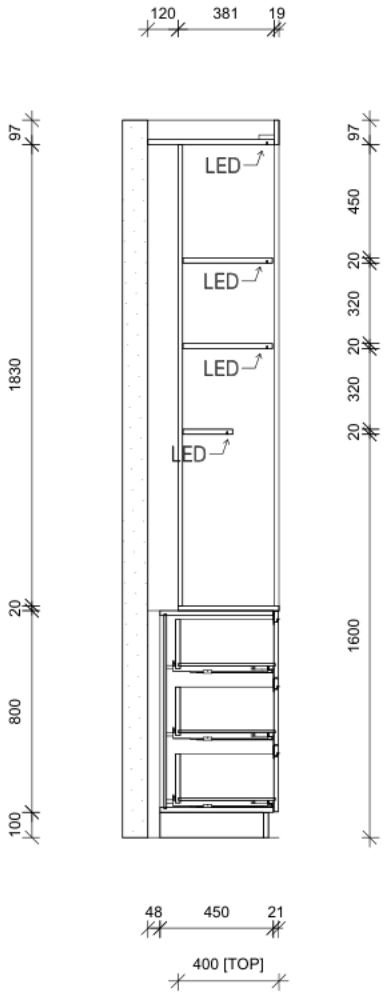

SECTION 2

Dkbb
157 Praditmanutham Road
Bangkapi Bangkok 10240
TEL:0-2515-1162 FAX:0-2515-1161
WWW.decorschoice.co.th

Client : Ari789	Design : WIC2-4C	View : Elevation A , Section1-2
Address :	Series : Elegance	Scale : 1:30
Province :	Drawn by : บริวัตร สุนทรจามร	Date : 19/10/2569
Phone :	Email :	Page : 02