



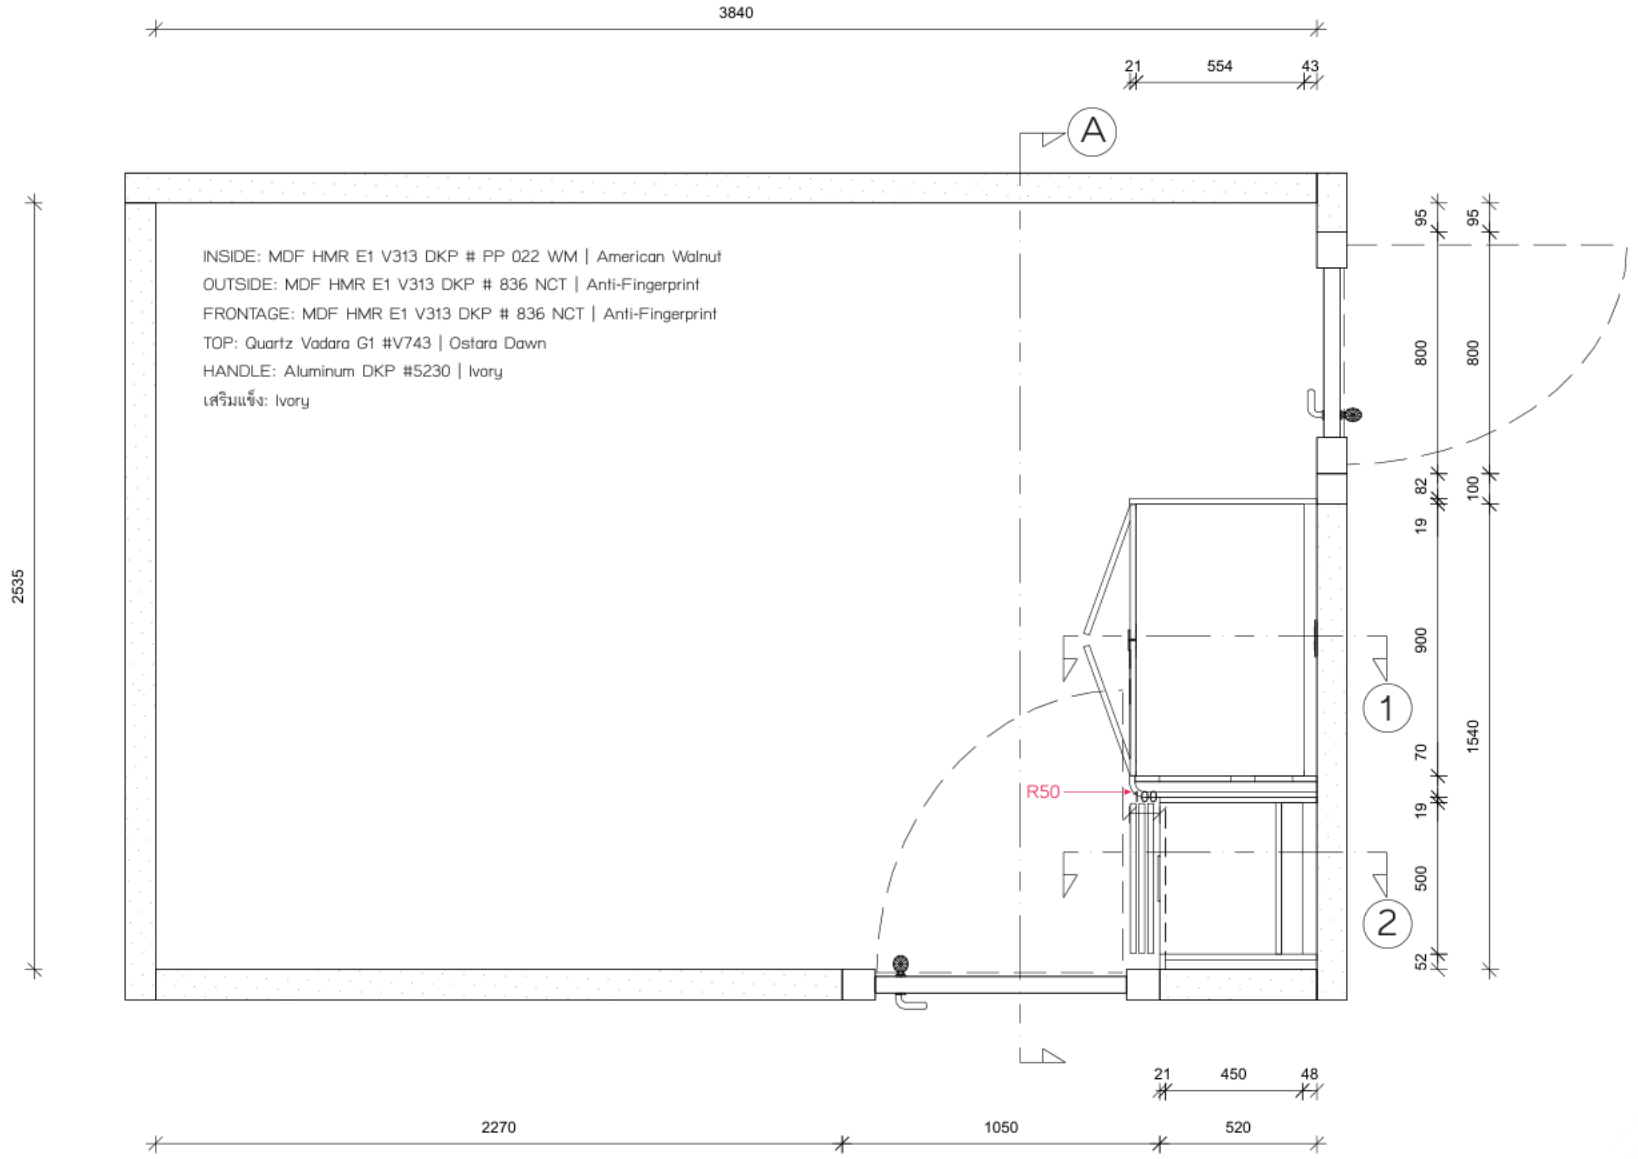




Dkbb 157 Praditmanutham Road Bangkapi Bangkok 10240 TEL:0-2515-1162 FAX:0-2515-1161 WWW.decorschoice.co.th	Client : Ari789	Design : WIC2-4C	View : Plan
	Address :	Series : Elegance	Scale : 1:25
	Province :	Drawn by : บริวัตร สุนทรจามร	Date : 19/10/2569
	Phone :	Email :	Page : 01


INSIDE: MDF HMR E1 V313 DKP # PP 022 WM | American Walnut
OUTSIDE: MDF HMR E1 V313 DKP # 836 NCT | Anti-Fingerprint
FRONTAGE: MDF HMR E1 V313 DKP # 836 NCT | Anti-Fingerprint
TOP: Quartz Vadara G1 #V743 | Ostara Dawn
HANDLE: Aluminum DKP #5230 | Ivory
เสริมแข็ง: Ivory

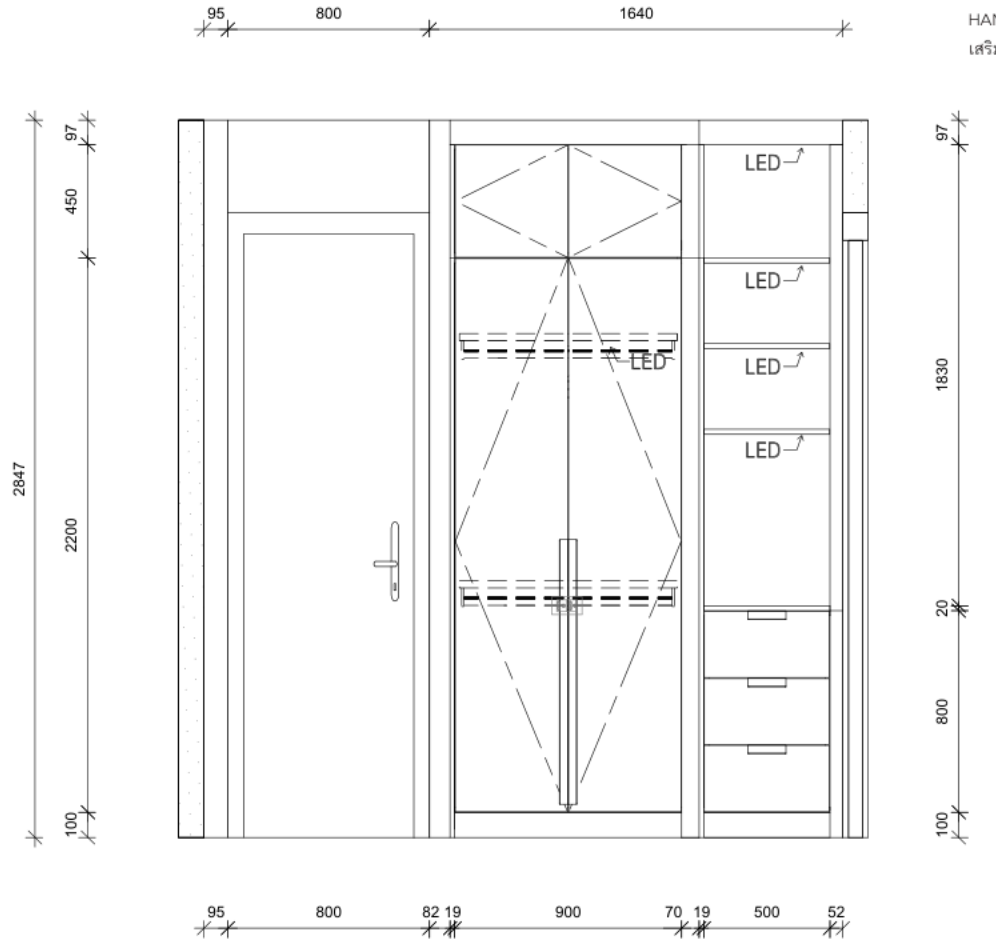

ELEVATION A

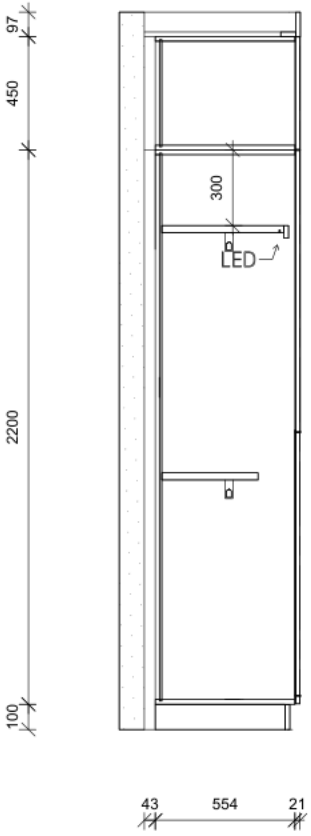

SECTION 1

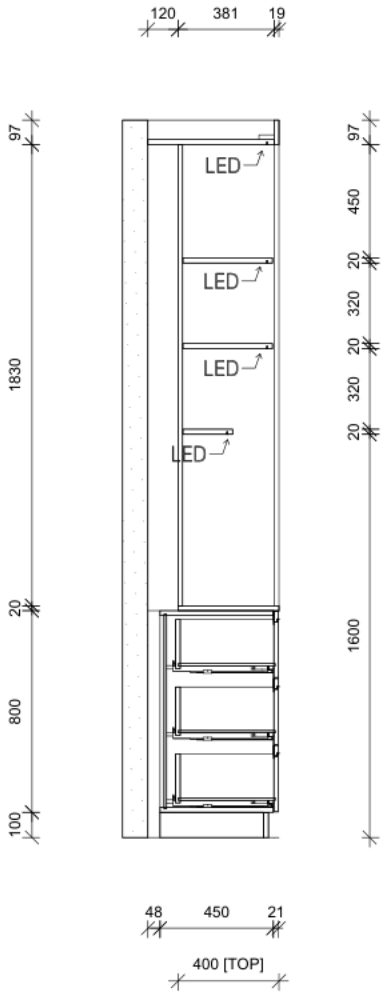

SECTION 2

Dkbb
157 Praditmanutham Road
Bangkapi Bangkok 10240
TEL:0-2515-1162 FAX:0-2515-1161
WWW.decorschoice.co.th

Client : Ari789	Design : WIC2-4C	View : Elevation A , Section1-2
Address :	Series : Elegance	Scale : 1:30
Province :	Drawn by : บริวัตร สุนทรจามร	Date : 19/10/2569
Phone :	Email :	Page : 02

Dkbb

ใบสรุปเฟอร์นิเจอร์ บริษัท อารี789 ดีเวลลอปเมนท์ จากัด

เลขที่ 10/1 ซอยพหลโยธิน 5 ถนนพหลโยธิน แขวงพญาไท เขตพญาไท

กรุงเทพมหานคร 10400 โทร : 044-110218

เลขประจาตัวผู้เสียภาษีอากร 0105565012642 (สานักงานใหญ่)

20 ตุลาคม 2569

Q.26/0906-1

4C Floor 4 : Walk-in closet (Bedroom 2) รุ่น ELEGANCE

1	ตู้เสื้อผ้าบานเปิด ขนาด 0.618 X 0.989 X 2.847 ม./	114,960.00
	รวม	114,960.00
	ส่วนลด 15%	-17,244.00
	ยอดรวม หลังหักส่วนลด	97,716.00
2	ไฟ LED ในตู้เสื้อผ้าบานเปิด / ตู้เก็บของ	5,000.00
	รวมเงิน Ex. Vat	**102,716.00**
	VAT 7%	**7,190.12**
	ยอดสุทธิ	**109,906.12**

หมายเหตุ - ก่อนเซ็นสั่งซื้อสินค้า กรุณาตรวจสอบแบบและรายละเอียดต่างๆ ให้ครบถ้วน เนื่องจากเป็นการสั่งผลิตเฉพาะงาน

- ไฟแสงสว่าง, สีของไฟ LED, ตำแหน่งปลั๊กใช้งาน, กุญแจล็อคต่างๆ ไม่สามารถเพิ่มภายหลังได้ กรุณาตรวจสอบก่อนว่ามีครบตามต้องการหรือไม่
- หลังจากสั่งซื้อสินค้าแล้ว ทางบริษัทฯ ขอสงวนสิทธิ์ในการแก้ไขใดๆทั้งสิ้น

บริษัท เดคคอร์ส ช้อยส์ จำกัด

157 ซ.โยธินพัฒนา ถ.ประดิษฐ์มนูธรรม แขวงคลองจั่น เขตบางกะปิ กรุงเทพฯ 10240

Tel : 0 2515 1162 Fax : 0 2515 1161 Call Center : 08-1954-5550

E-mail : decorchoice@gmail.com www.decorschoice.co.th