





DIOR

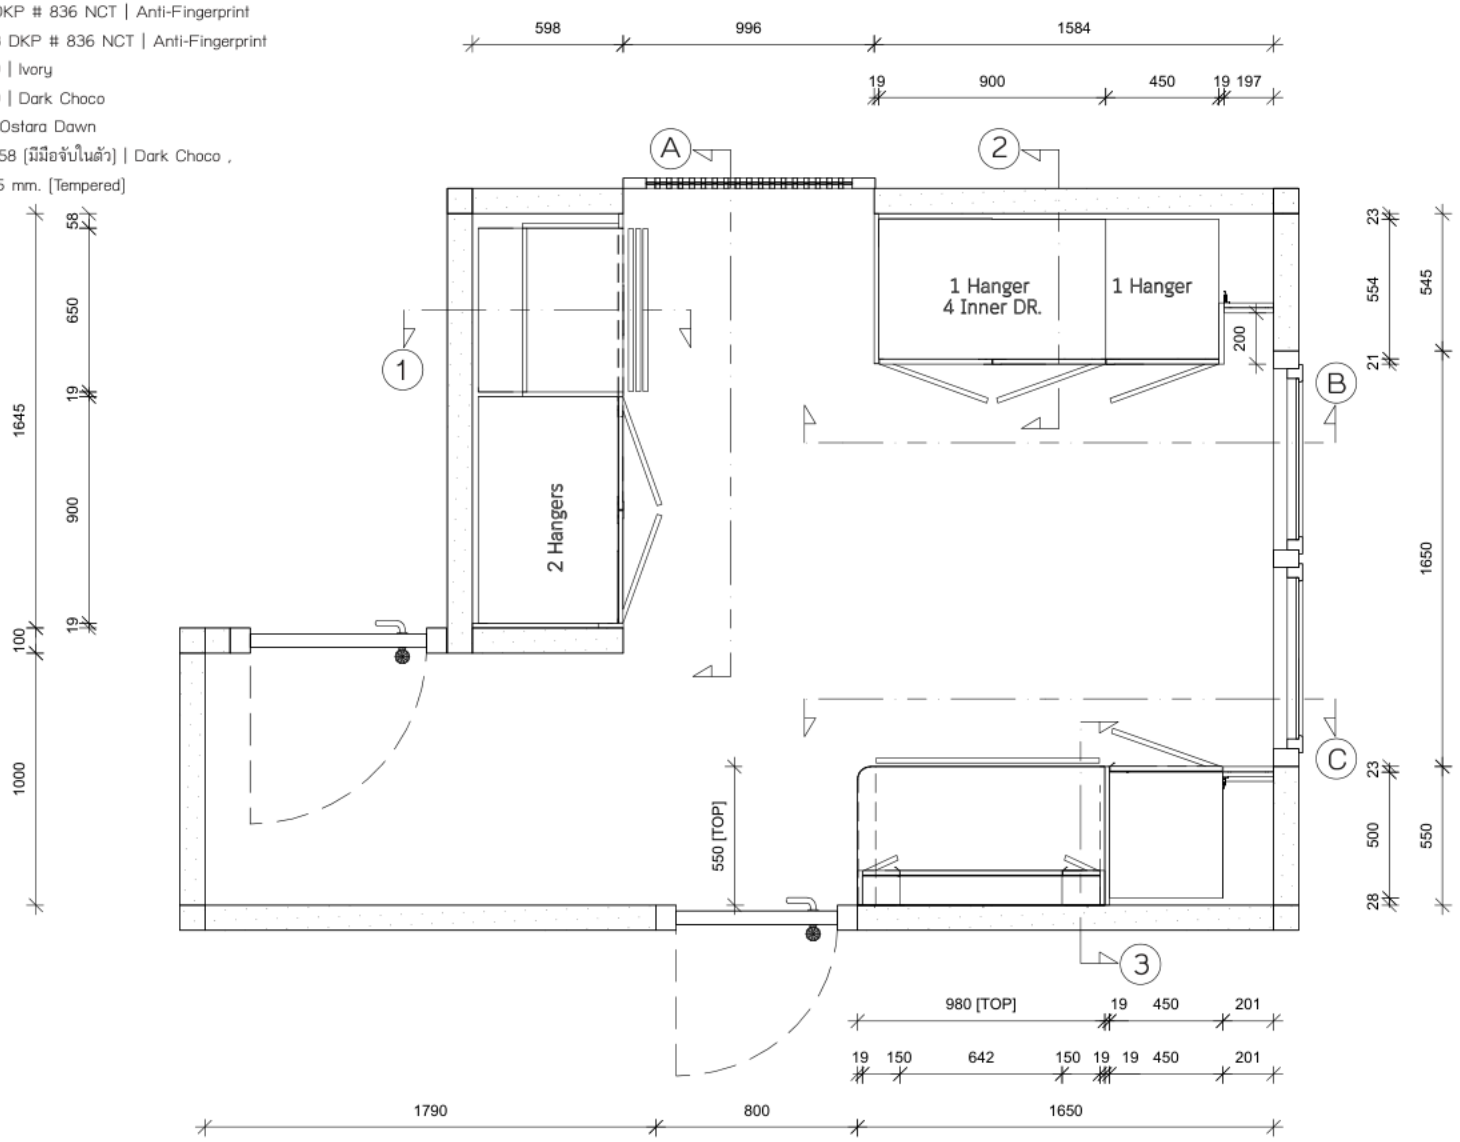


INSIDE: MDF HMR E1 V313 DKP # PP 022 WM | American Walnut
OUTSIDE: MDF HMR E1 V313 DKP # 836 NCT | Anti-Fingerprint
FRONTAGE: MDF HMR E1 V313 DKP # 836 NCT | Anti-Fingerprint
HANDLE: Aluminum DKP #5230 | Ivory
HANDLE: Aluminum DKP #5230 | Dark Choco
TOP: Quartz Vadara G1 #V743 | Ostara Dawn
FRONTAGE: Aluminum DKP #5158 (มีมือจับในตัว) | Dark Choco ,
กรุกระจก ใส TYK | Euro Bronze 5 mm. [Tempered]
เสริมแข็ง: Ivory




Dkbb
157 Praditmanutham Road
Bangkapi Bangkok 10240
TEL:0-2515-1162 FAX:0-2515-1161
WWW.decorschoice.co.th

Client : Ari789	Design : WICMB-4B	View : Plan
Address :	Series : Elegance	Scale : 1:30
Province :-	Drawn by : บริวัตร สุนทรจามร	Date : 10/10/2569
Phone :	Email :	Page : 01

INSIDE: MDF HMR E1 V313 DKP # PP 022 WM | American Walnut
OUTSIDE: MDF HMR E1 V313 DKP # 836 NCT | Anti-Fingerprint
FRONTAGE: MDF HMR E1 V313 DKP # 836 NCT | Anti-Fingerprint
HANDLE: Aluminum DKP #5230 | Ivory
HANDLE: Aluminum DKP #5230 | Dark Choco
TOP: Quartz Vadara G1 #V743 | Ostara Dawn
FRONTAGE: Aluminum DKP #5158 (มีมือจับในตัว) | Dark Choco ,
กรุกระจก ใส TYK | Euro Bronze 5 mm. [Tempered]
เสริมแข็ง: Ivory

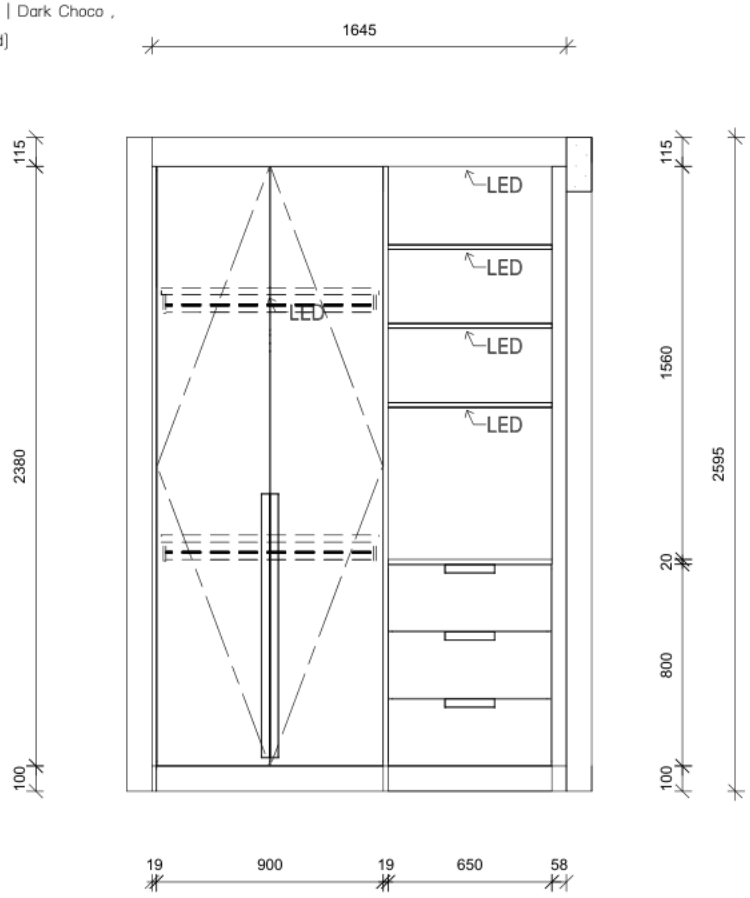

ELEVATION A

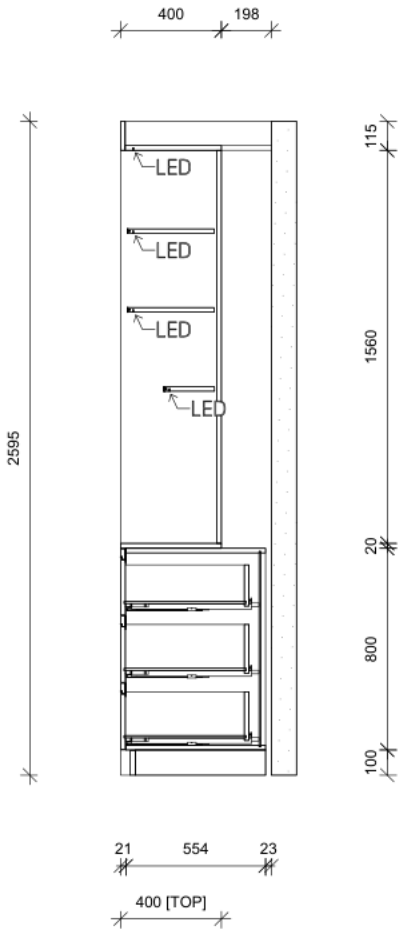


SECTION 1


Dkbb
157 Praditmanutham Road
Bangkapi Bangkok 10240
TEL:0-2515-1162 FAX:0-2515-1161
WWW.decorschoice.co.th

Client : Ari789	Design : WICMB-4B	View : Elevation A , Section 1
Address :	Series : Elegance	Scale : 1:30
Province :-	Drawn by : บริวัตร สุนทรจามร	Date : 10/10/2569
Phone :	Email :	Page : 02

INSIDE: MDF HMR E1 V313 DKP # PP 022 WM | American Walnut
OUTSIDE: MDF HMR E1 V313 DKP # 836 NCT | Anti-Fingerprint
FRONTAGE: MDF HMR E1 V313 DKP # 836 NCT | Anti-Fingerprint
HANDLE: Aluminum DKP #5230 | Ivory
HANDLE: Aluminum DKP #5230 | Dark Choco
TOP: Quartz Vadara G1 #V743 | Ostara Dawn
FRONTAGE: Aluminum DKP #5158 (มีมือจับในตัว) | Dark Choco ,
กรุกระจก ใส TYK | Euro Bronze 5 mm. (Tempered)
เสริมแข็ง: Ivory

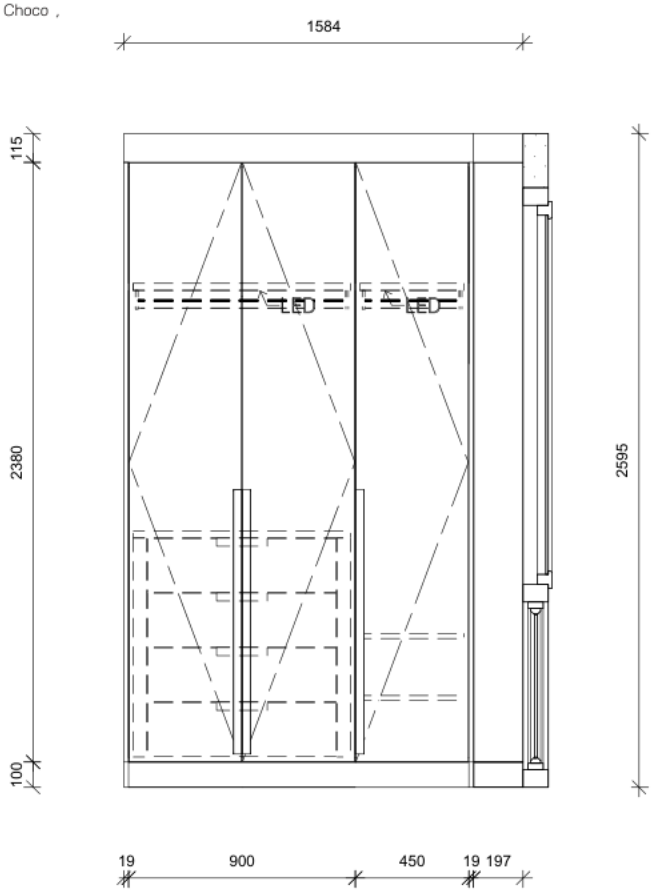

ELEVATION B

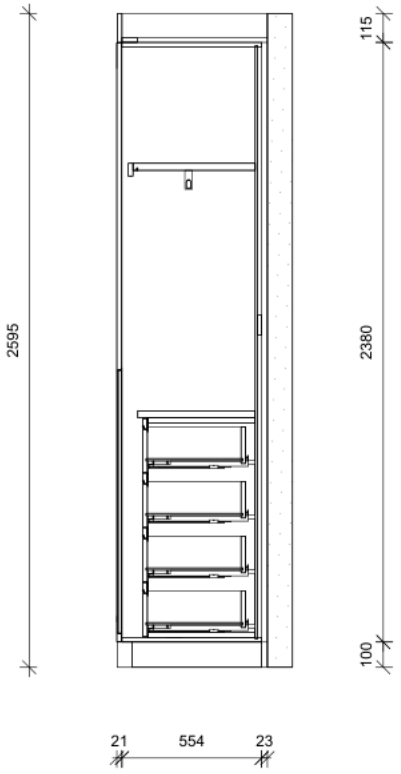


SECTION 2


Dkbb
157 Praditmanutham Road
Bangkapi Bangkok 10240
TEL:0-2515-1162 FAX:0-2515-1161
WWW.decorschoice.co.th

Client : Ari789	Design : WICMB-4B	View : Elevation B , Section 2
Address :	Series : Elegance	Scale : 1:30
Province :-	Drawn by : บริวัตร สุนทรจามร	Date : 10/10/2569
Phone :	Email :	Page : 03

INSIDE: MDF HMR E1 V313 DKP # PP 022 WM | American Walnut
OUTSIDE: MDF HMR E1 V313 DKP # 836 NCT | Anti-Fingerprint
FRONTAGE: MDF HMR E1 V313 DKP # 836 NCT | Anti-Fingerprint
HANDLE: Aluminum DKP #5230 | Ivory
HANDLE: Aluminum DKP #5230 | Dark Choco
TOP: Quartz Vadara G1 #V743 | Ostara Dawn
FRONTAGE: Aluminum DKP #5158 [มีมือจับในตัว] | Dark Choco ,
กรุกระจก ใส TYK | Euro Bronze 5 mm. [Tempered]
เสริมแข็ง: Ivory

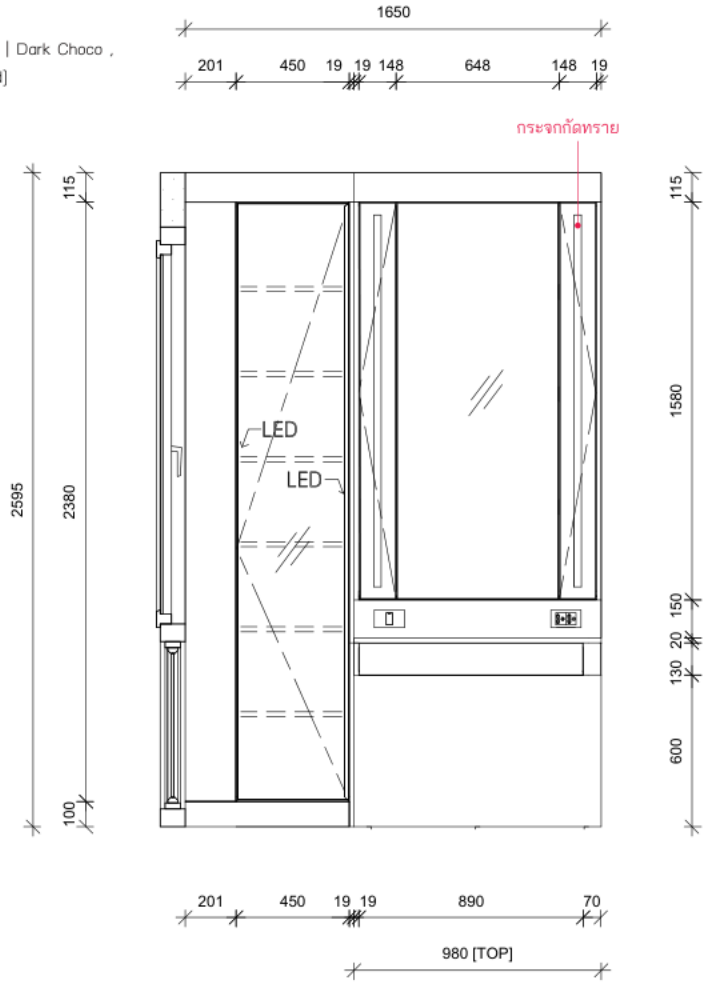

ELEVATION C

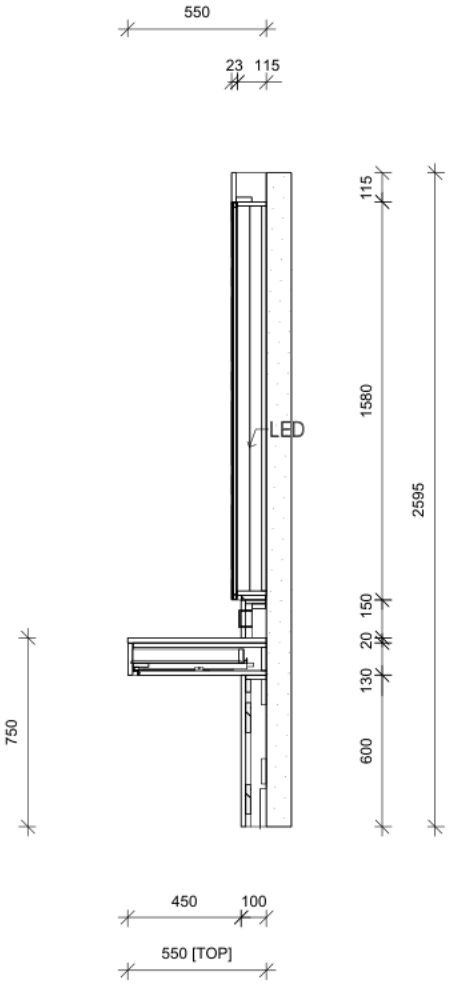

SECTION 3

Dkbb 157 Praditmanutham Road Bangkapi Bangkok 10240 TEL:0-2515-1162 FAX:0-2515-1161 WWW.decorschoice.co.th	Client : Ari789	Design : WICMB-4B	View : Elevation C , Section 3
	Address :	Series : Elegance	Scale : 1:30
	Province :-	Drawn by : บริวัตร สุนทรจามร	Date : 10/10/2569
	Phone :	Email :	Page : 04

Dkbb

ใบสรุปเฟอร์นิเจอร์ บริษัท อารี789 ดีเวลลอปเมนท์ จากัด

เลขที่ 10/1 ซอยพหลโยธิน 5 ถนนพหลโยธิน แขวงพญาไท เขตพญาไท

กรุงเทพมหานคร 10400 โทร : 044-110218

เลขประจาตัวผู้เสียภาษีอากร 0105565012642 (สานักงานใหญ่)

Q.26/0917-1 **20 ตุลาคม 2569**

4B Floor 4 : Walk-in closet (Master Bedroom) รุ่น ELEGANCE

1	ตู้เก็บของพร้อมโต๊ะแต่งตัว ขนาด 0.55 X 1.65 X 2.595 ม.		69,196.00
2	ตู้เสื้อผ้าบานเปิด ขนาด 0.598 X 0.938 X 2.595 ม./ ตู้เก็บของ ขนาด 0.598 X 0.708 X 2.595 ม.		111,823.00
3	ตู้เสื้อผ้าบานเปิดตัว I ขนาด 0.598 X 1.584 X 2.595 ม.		108,442.00
		รวม	289,461.00
		ส่วนลด 15%	-43,419.00
		ยอดรวม หลังหักส่วนลด	246,042.00
4	ไฟ LED ในตู้เก็บของพร้อมโต๊ะแต่งตัว		10,120.00
5	ไฟ LED ในตู้เสื้อผ้าบานเปิด / ตู้เก็บของ		5,650.00
6	ไฟ LED ในตู้เสื้อผ้าบานเปิดตัว I		3,300.00
		รวมเงิน Ex. Vat	**265,112.00**
		VAT 7%	**18,557.84**
		ยอดสุทธิ	**283,669.84**

หมายเหตุ - ก่อนเซ็นสั่งซื้อสินค้า กรุณาตรวจสอบแบบและรายละเอียดต่างๆ ให้ครบถ้วน เนื่องจากเป็นการสั่งผลิตเฉพาะงาน

- ไฟแสงสว่าง, สีของไฟ LED, ตำแหน่งปลั๊กใช้งาน, กุญแจล็อคต่างๆ ไม่สามารถเพิ่มภายหลังได้ กรุณาตรวจสอบก่อนว่ามีครบตามต้องการหรือไม่
- หลังจากสั่งซื้อสินค้าแล้ว ทางบริษัทฯ ขอสงวนสิทธิ์ในการแก้ไขใดๆทั้งสิ้น

บริษัท เดคคอร์ส ช้อยส์ จำกัด

157 ซ.โยธินพัฒนา ถ.ประดิษฐ์มนูธรรม แขวงคลองจั่น เขตบางกะปิ กรุงเทพฯ 10240

Tel : 0 2515 1162 Fax : 0 2515 1161 Call Center : 08-1954-5550

E-mail : decorchoice@gmail.com www.decorschoice.co.th