


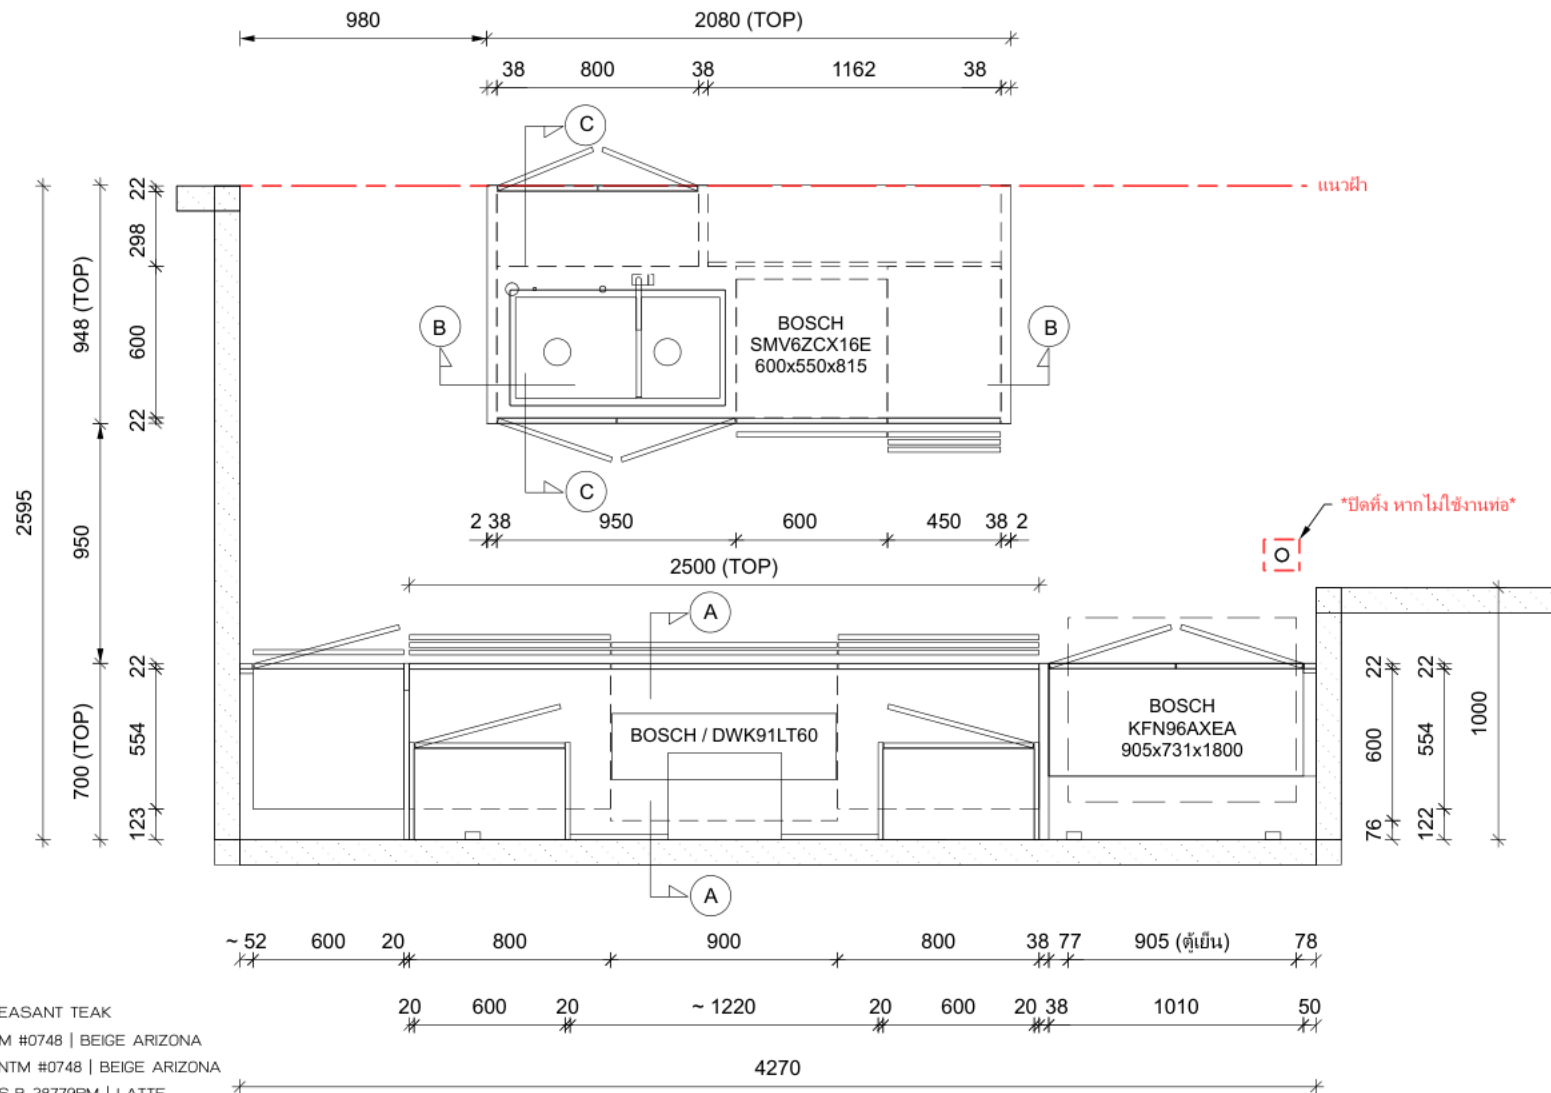


INSIDE : DK Board Laminate DKBB #IAB 8101 | PLEASANT TEAK
 OUTSIDE : DK Board Laminate FORMICA FENIX NTM #0748 | BEIGE ARIZONA
 FRONTAGE : VI PLUS Laminate FORMICA FENIX NTM #0748 | BEIGE ARIZONA
 ด้านหลังปิด Laminate PANAPLAST # S-B 28779PM | LATTE
 TOP/BACK SPLASH : QUARTZ VADARA | OSTARA DAWN 20 mm.
 HANDLE : ALUMINIUM PROFILE-C | ALUMINIUM
 HANDLE : ALUMINIUM PROFILE-J | ALUMINIUM
 เสร็จแข็งแรง : DKP #1907 | Ivory

Client :ARI 789	Design :KITCHEN (5B)	View : PLAN
Address :	Series :ELEGANCE PLUS	Scale : 1:30
Province :	Drawn by :Jirayu	Date : 20/2/2569
Phone :	Email :	Page : 1-5

Dkbb

157 Praditmanutham Road
 Bangkapi Bangkok 10240
 TEL:0-2515-1162 FAX:0-2515-1161
 WWW.decorchoice.co.th

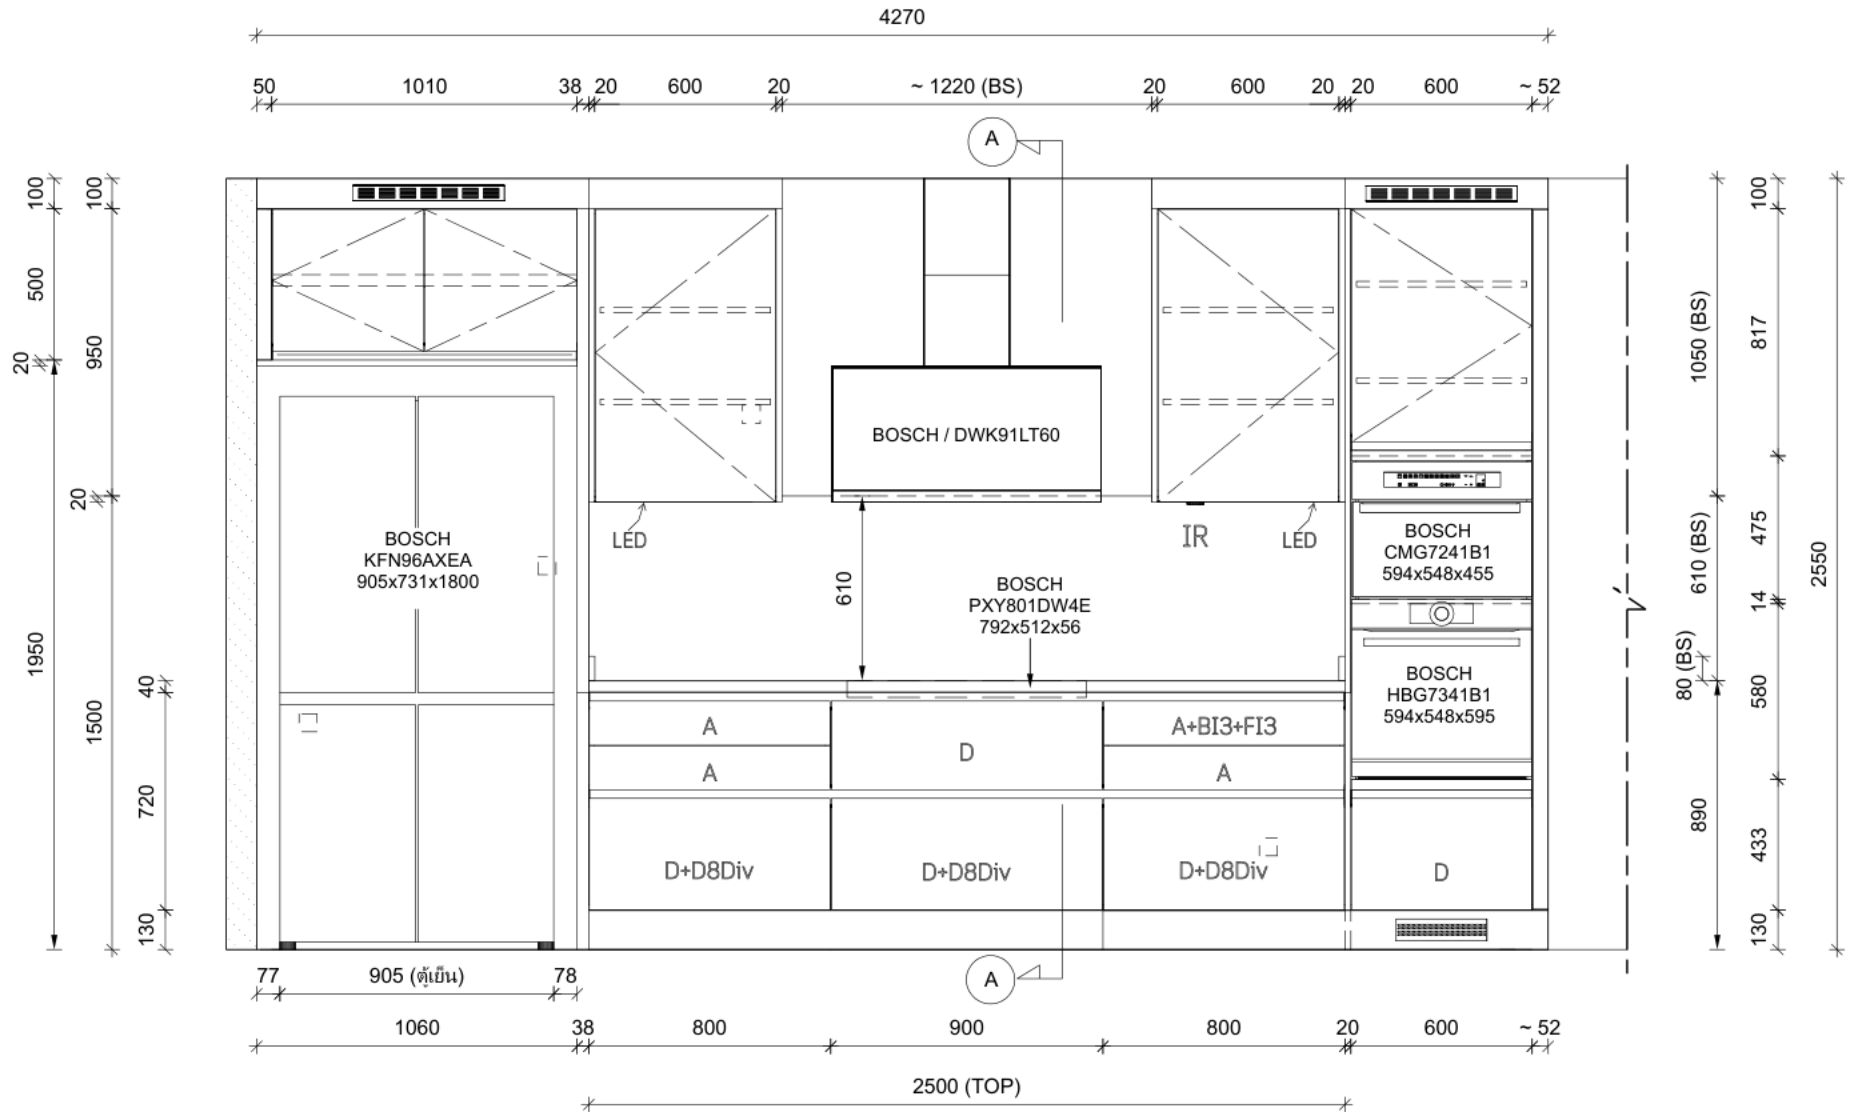

INSIDE : DK Board Laminate DKBB #IAB 8101 | PLEASANT TEAK

OUTSIDE : DK Board Laminate FORMICA FENIX NTM #0748 | BEIGE ARIZONA

FRONTAGE : VI PLUS Laminate FORMICA FENIX NTM #0748 | BEIGE ARIZONA

ด้านหลังปิด Laminate PANAPLAST # S-B 28779PM | LATTE

TOP/BACK SPLASH : QUARTZ VADARA | OSTARA DAWN 20 mm.

HANDLE : ALUMINIUM PROFILE-C | ALUMINIUM

HANDLE : ALUMINIUM PROFILE-J | ALUMINIUM

เสริมแข็ง : DKP #1907 | Ivory

Dkbb

157 Praditmanutham Road
Bangkapi Bangkok 10240
TEL:0-2515-1162 FAX:0-2515-1161
WWW.decorchoice.co.th

Client :ARI 789

Address :

Province :

Phone :

Design :KITCHEN (5B)

Series :ELEGANCE PLUS

Drawn by :Jirayu


Email :

View : ELEVATION

Scale : 1:25

Date : 20/2/2569

Page : 2-5

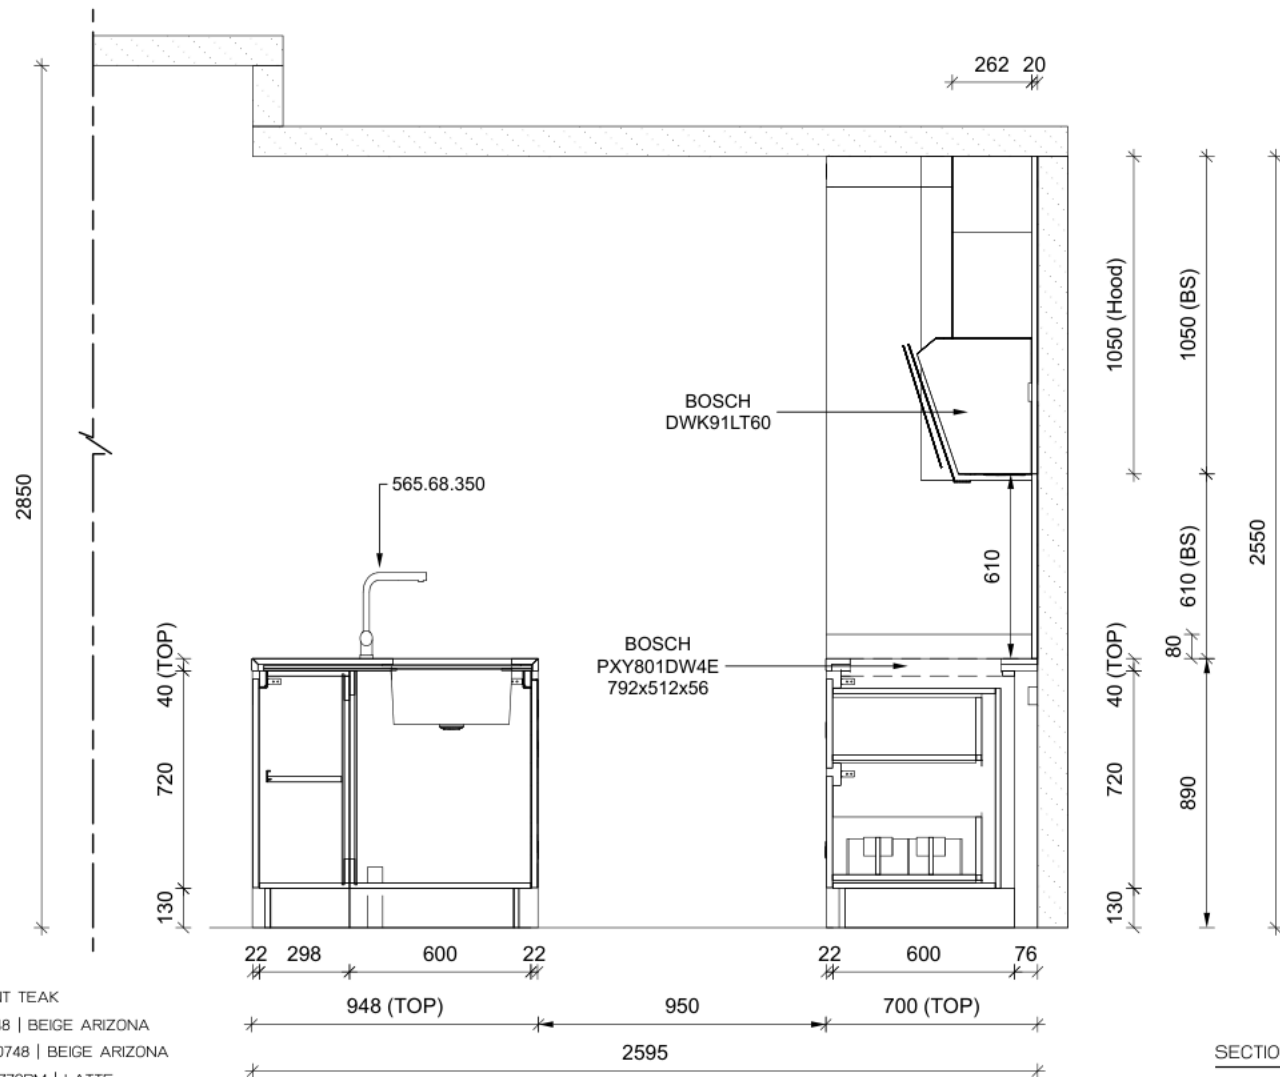


INSIDE : DK Board Laminate DKBB #IAB 8101 | PLEASANT TEAK
 OUTSIDE : DK Board Laminate FORMICA FENIX NTM #0748 | BEIGE ARIZONA
 FRONTAGE : VI PLUS Laminate FORMICA FENIX NTM #0748 | BEIGE ARIZONA
 ด้านหลังปิด Laminate PANAPLAST # S-B 28779PM | LATTE
 TOP/BACK SPLASH : QUARTZ VADARA | OSTARA DAWN 20 mm.
 HANDLE : ALUMINIUM PROFILE-C | ALUMINIUM
 HANDLE : ALUMINIUM PROFILE-J | ALUMINIUM
 เสีร์มแข็ง : DKP #1907 | Ivory


Dkbb

157 Praditmanutham Road
 Bangkapi Bangkok 10240
 TEL:0-2515-1162 FAX:0-2515-1161
 WWW.decorchoice.co.th


Client :ARI 789	Design :KITCHEN (5B)	View : SECTION A
Address :	Series :ELEGANCE PLUS	Scale : 1:25
Province :	Drawn by :Jirayu	Date : 20/2/2569
Phone :	Email :	Page : 3-5

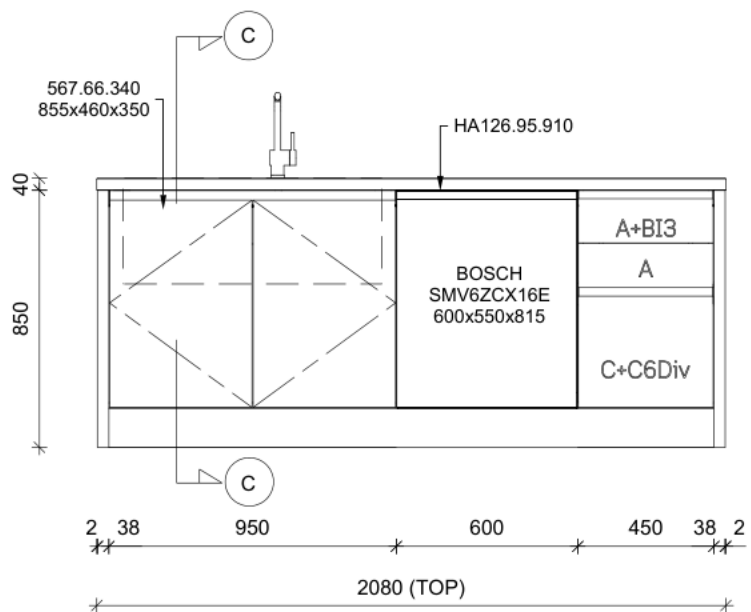

ELEVATION A

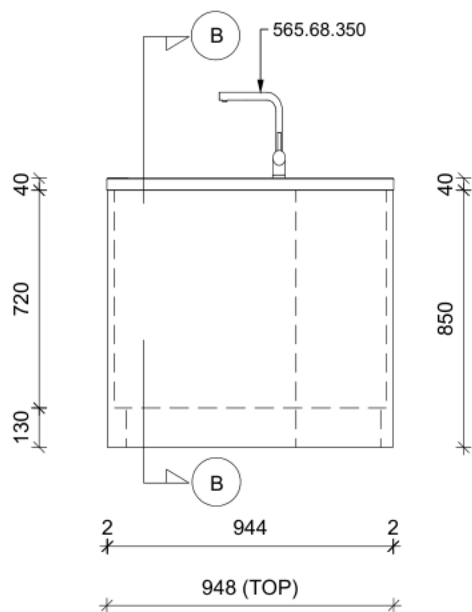

ELEVATION B

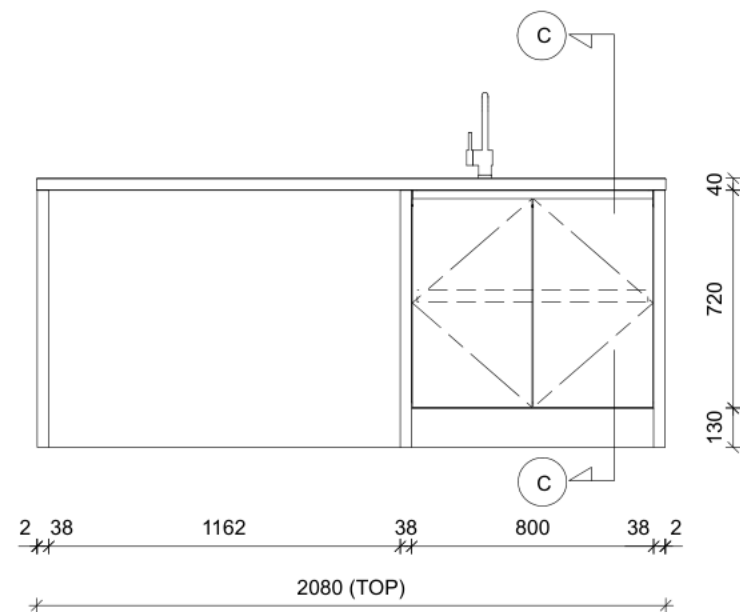

ELEVATION C

INSIDE : DK Board Laminate DKBB #IAB 8101 | PLEASANT TEAK
 OUTSIDE : DK Board Laminate FORMICA FENIX NTM #0748 | BEIGE ARIZONA
 FRONTAGE : VI PLUS Laminate FORMICA FENIX NTM #0748 | BEIGE ARIZONA
 ด้านหลังปิด Laminate PANAPLAST # S-B 28779PM | LATTE
 TOP/BACK SPLASH : QUARTZ VADARA | OSTARA DAWN 20 mm.
 HANDLE : ALUMINIUM PROFILE-C | ALUMINIUM
 HANDLE : ALUMINIUM PROFILE-J | ALUMINIUM
 HANDLE : HAFELE #126.95.910
 เสร็จผนัง : DKP #1907 | Ivory

Dkbb

157 Praditmanutham Road
 Bangkapi Bangkok 10240
 TEL:0-2515-1162 FAX:0-2515-1161
 WWW.decorchoice.co.th

Client :ARI 789

Address :

Province :

Phone :

Design : KITCHEN 5B (ISLAND)

Series :ELEGANCE PLUS

Drawn by :Jirayu


Email :

View : ELEVATION A,B,C


Scale : 1:25

Date : 20/2/2569


Page : 4-5

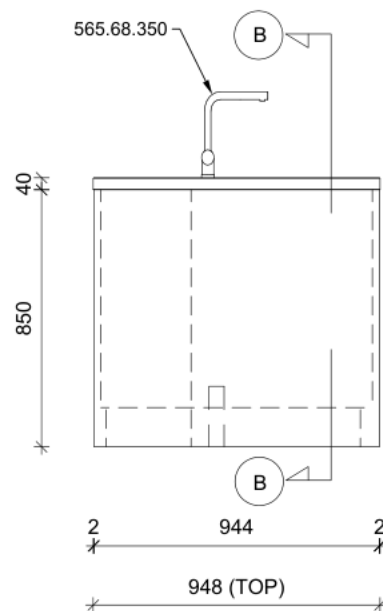

ELEVATION D

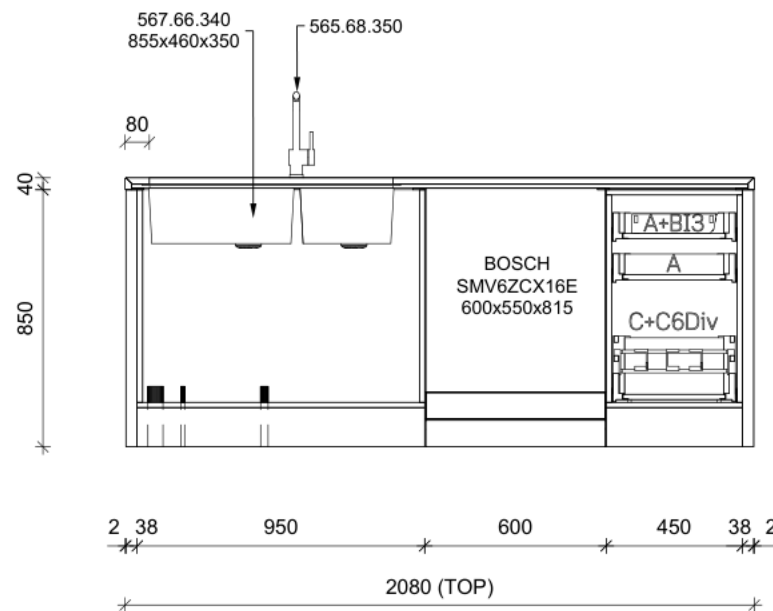

SECTION B

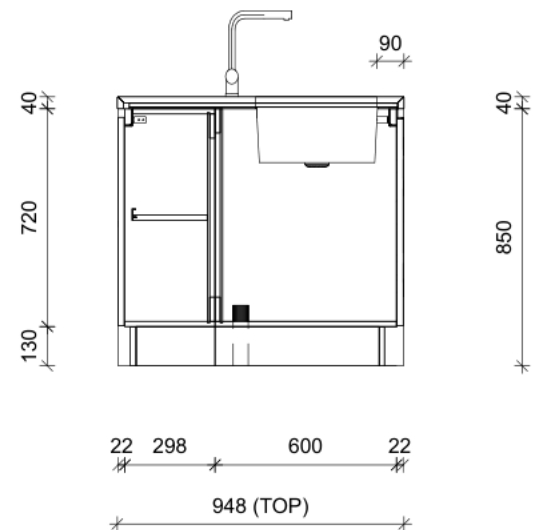

SECTION C

INSIDE : DK Board Laminate DKBB #IAB 8101 | PLEASANT TEAK
 OUTSIDE : DK Board Laminate FORMICA FENIX NTM #0748 | BEIGE ARIZONA
 FRONTAGE : VI PLUS Laminate FORMICA FENIX NTM #0748 | BEIGE ARIZONA
 ด้านหลังปิด Laminate PANAPLAST # S-B 28779PM | LATTE
 TOP/BACK SPLASH : QUARTZ VADARA | OSTARA DAWN 20 mm.
 HANDLE : ALUMINIUM PROFILE-C | ALUMINIUM
 HANDLE : ALUMINIUM PROFILE-J | ALUMINIUM
 HANDLE : HAFELE #126.95.910
 เสร็จเมจ : DKP #1907 | Ivory

Dkbb

157 Praditmanutham Road
 Bangkapi Bangkok 10240
 TEL:0-2515-1162 FAX:0-2515-1161
 WWW.decorchoice.co.th

Client :ARI 789	Design : KITCHEN 5B (ISLAND)	View : ELEVATION D ,SECTION B,C
Address :	Series :ELEGANCE PLUS	Scale : 1:25
Province :	Drawn by :Jirayu	Date : 20/2/2569
Phone :	Email :	Page : 5-5