










INSIDE : DK Board Laminate DKBB #IAB 8101 | PLEASANT TEAK
 OUT SIDE : DK Board Laminate FORMICA FENIX NTM #0748 | BEIGE ARIZONA
 FRONTAGE : VI PLUS Laminate FORMICA FENIX NTM #0748 | BEIGE ARIZONA
 ด้านหลังปิด Laminate PANAPLAST # S-B 28779PM | LATTE
 TOP/BACK SPLASH : QUARTZ VADARA #V743 | OSTARA DAWN 20 mm.
 HANDLE : ALUMINIUM PROFILE-C | ALUMINIUM
 HANDLE : ALUMINIUM PROFILE-J | ALUMINIUM
 HANDLE : HAFELE # 125.95.910
 HANDLE : HAFELE #126.95.920
 เสร็จเรียบร้อย : Ivory

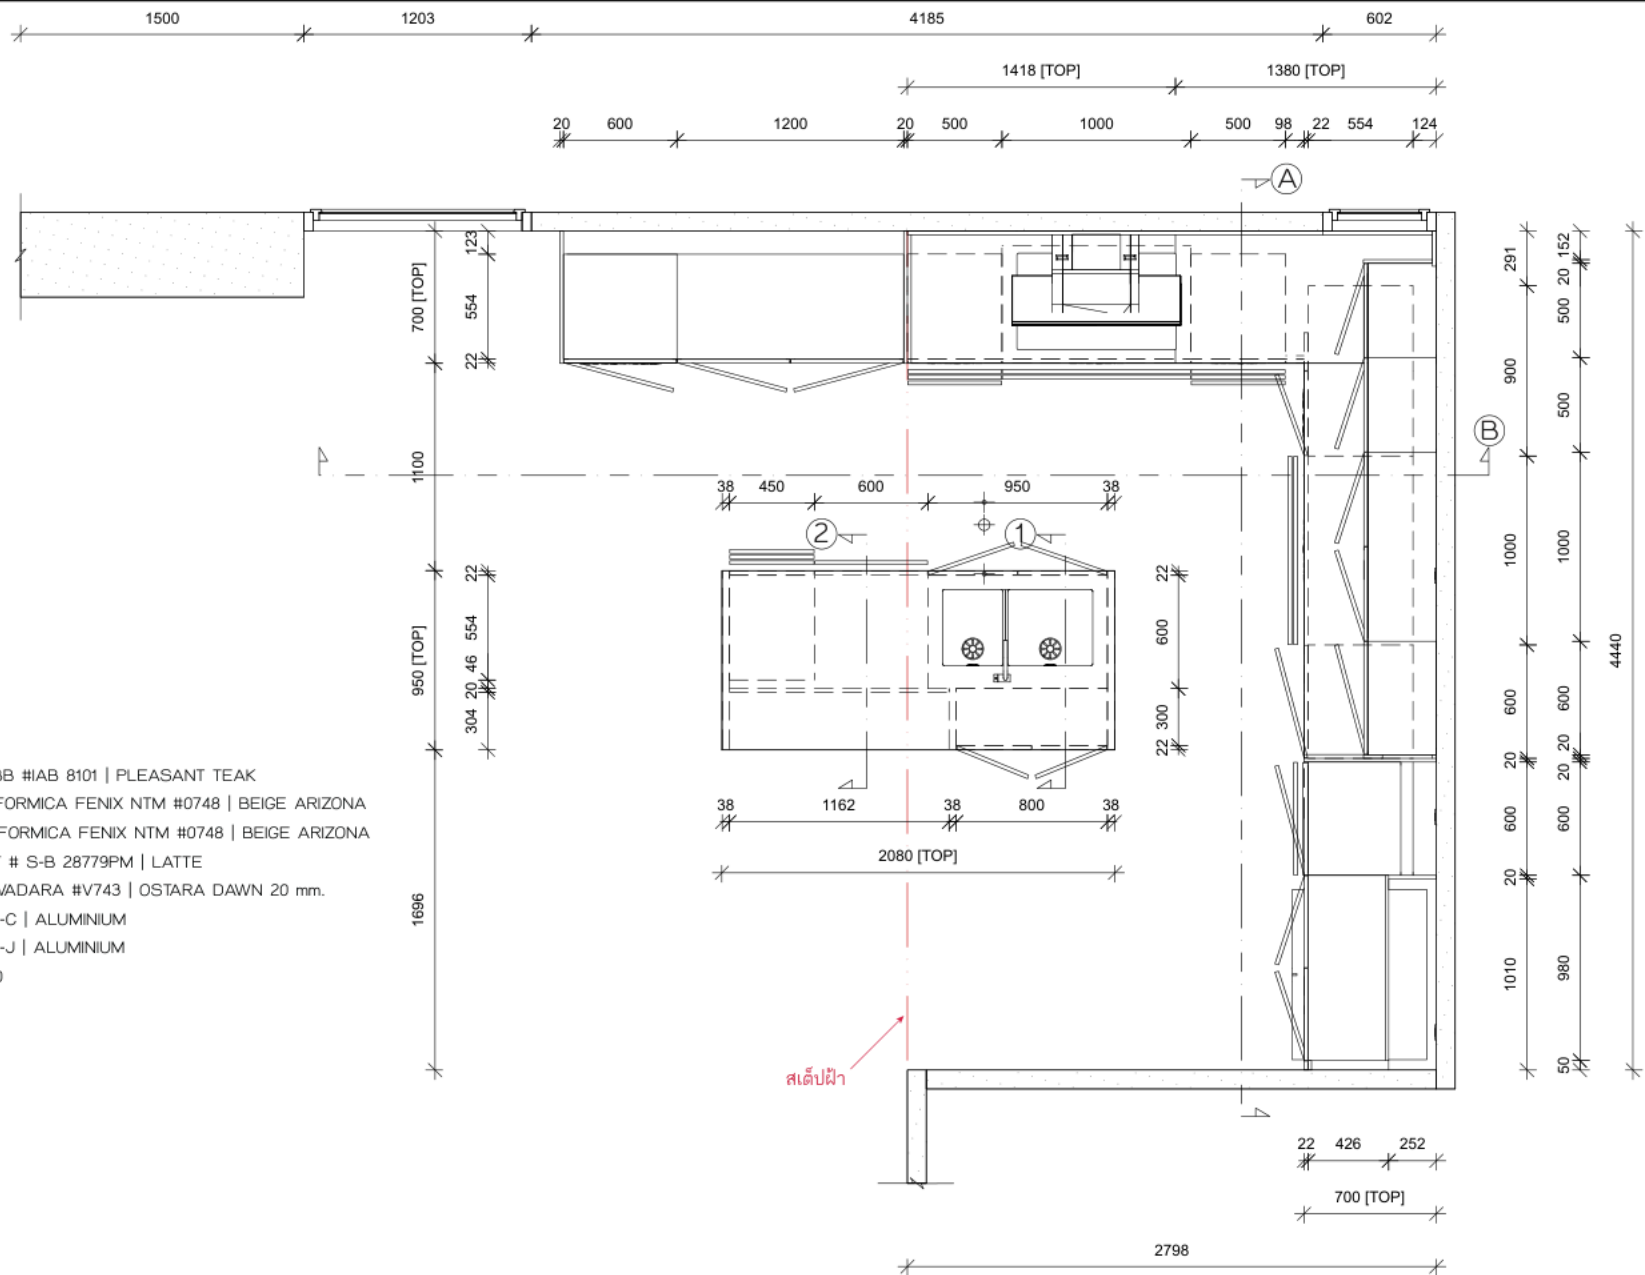

Dkbb

157 Praditmanutham Road
 Bangkapi Bangkok 10240
 TEL: 0-2515-1162 FAX: 0-2515-1161
 WWW.decorchoice.co.th

Client : ARI 789

Address :

Province :-

Phone :

Design : Kitchen 6A

Series : Elegance Plus

Drawn by : บริษัท สุนทรจามร


Email :

View : Plan

Scale : 1:40

Date : 10/4/2569

Page : 01

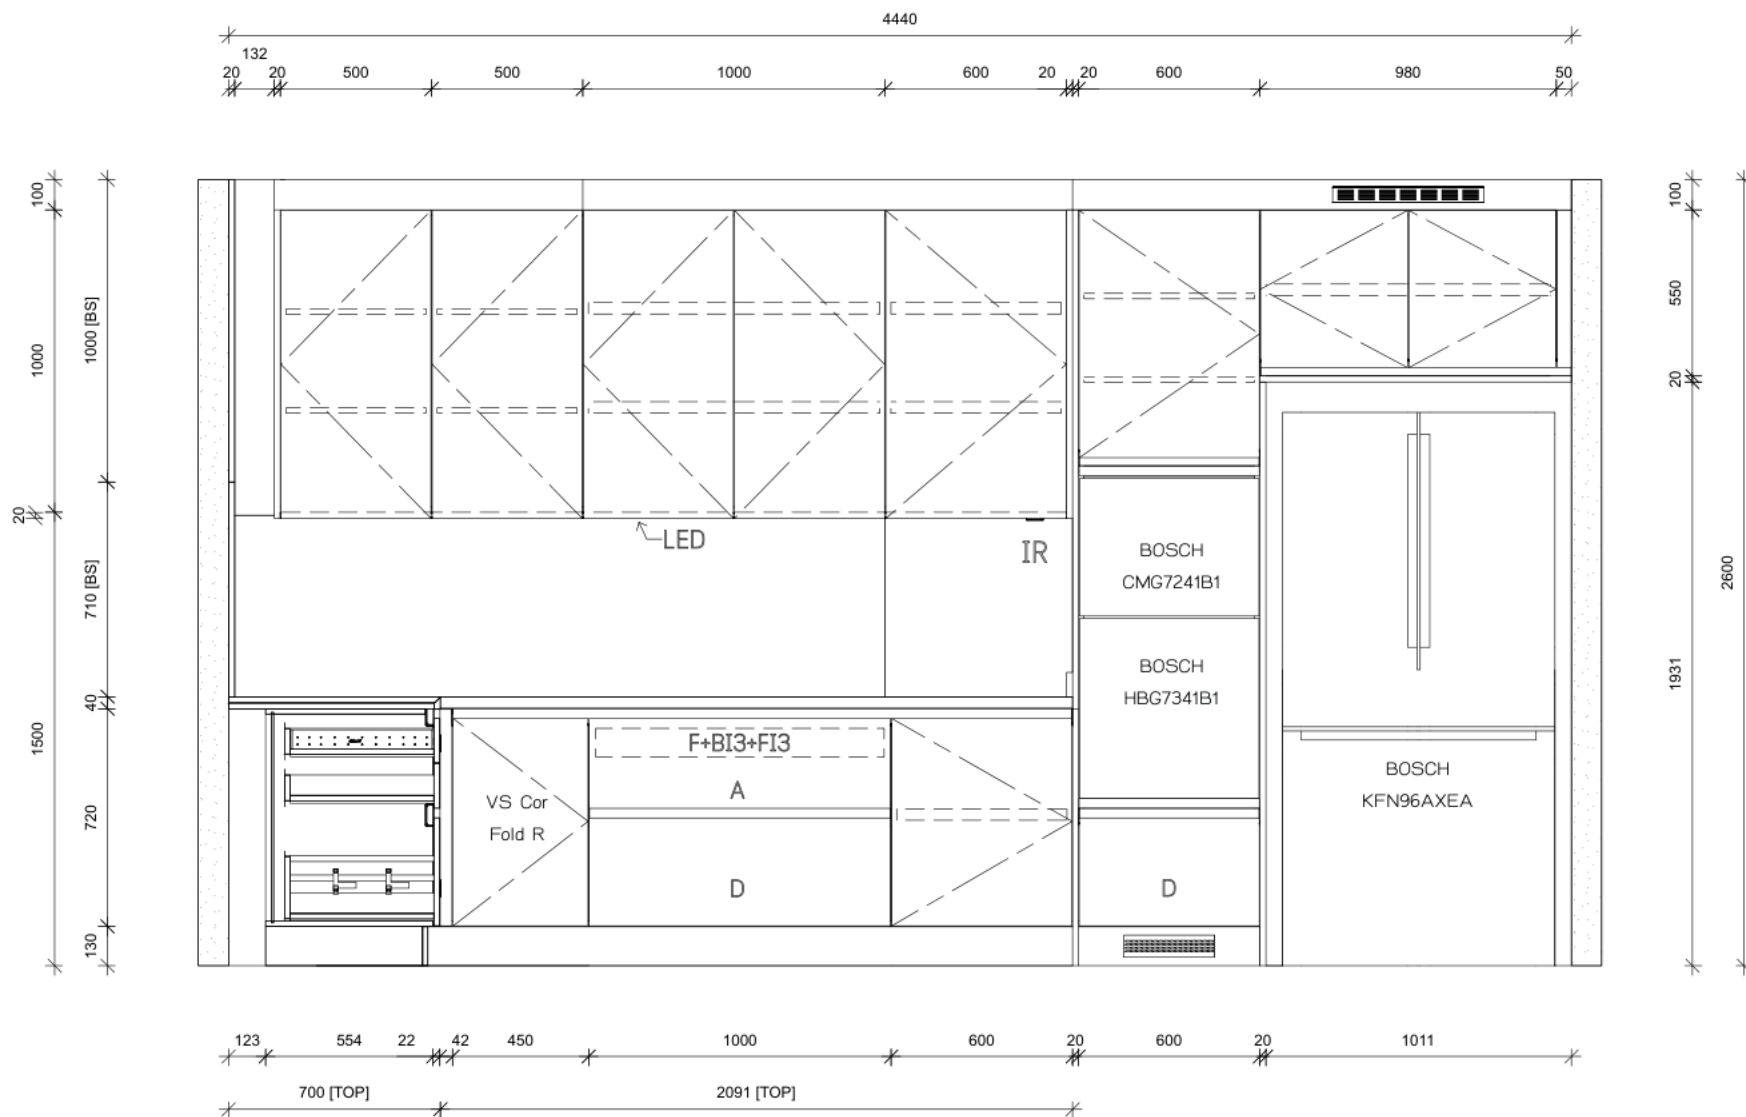

Dkbb

157 Praditmanutham Road
Bangkapi Bangkok 10240
TEL: 0-2515-1162 FAX: 0-2515-1161
WWW.decorchoice.co.th

Client : ARI 789

Address :

Province :-

Phone :

Design : Kitchen 6A

Series : Elegance Plus

Drawn by : บริษัท สุนทรจามร


Email :

View : Elevation A

Scale : 1:25

Date : 10/4/2569

Page : 02

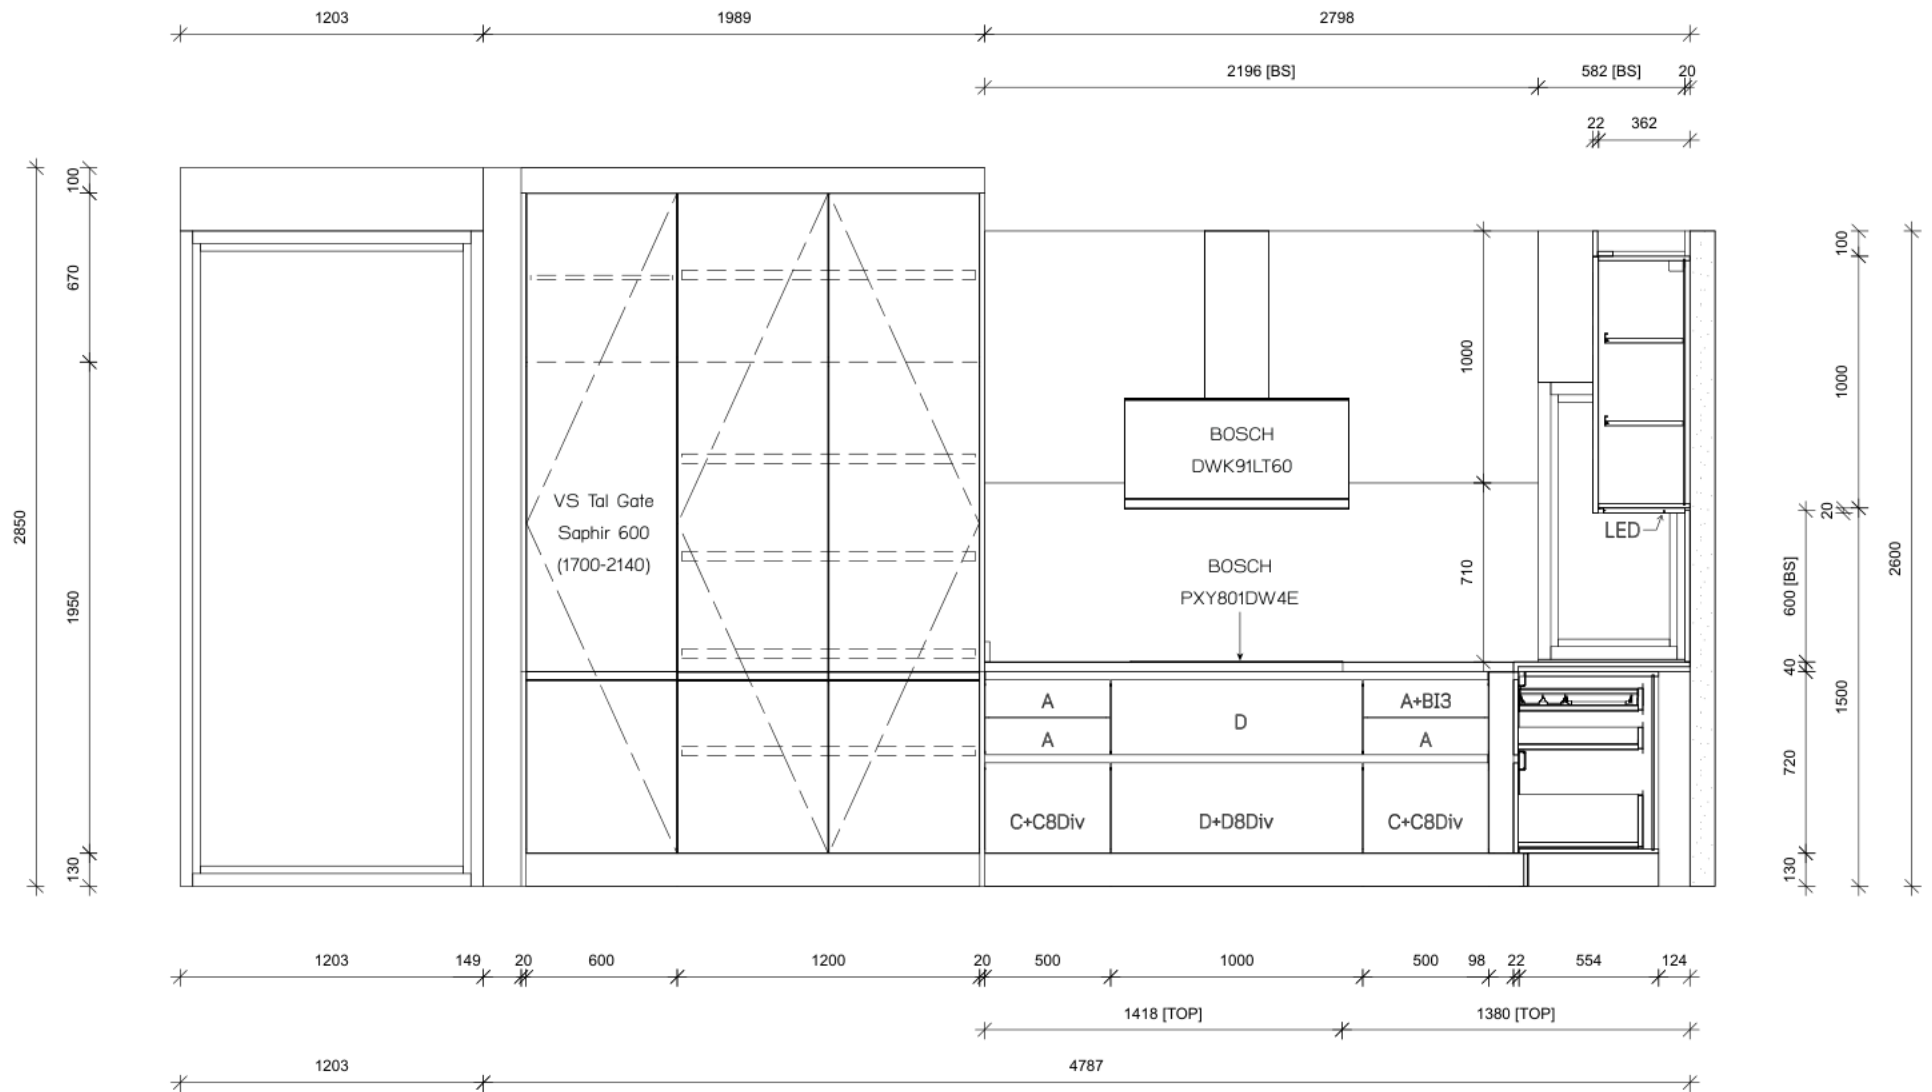

Dkbb

157 Praditmanutham Road
Bangkapi Bangkok 10240
TEL:0-2515-1162 FAX:0-2515-1161
WWW.decorchoice.co.th

Client : ARI 789

Address :

Province :-

Phone :

Design : Kitchen 6A

Series : Elegance Plus

Drawn by : บริษัท สุนทรจามร

Email :

View : Elevation B

Scale : 1:25

Date : 10/4/2569

Page : 03

INSIDE : DK Board Laminate DKBB #IAB 8101 | PLEASANT TEAK

OUT SIDE : DK Board Laminate FORMICA FENIX NTM #0748 | BEIGE ARIZONA

FRONTAGE : VI PLUS Laminate FORMICA FENIX NTM #0748 | BEIGE ARIZONA

ด้านหลังปิด Laminate PANAPLAST # S-B 28779PM | LATTE

TOP/BACK SPLASH : QUARTZ VADARA #V743 | OSTARA DAWN 20 mm.

HANDLE : ALUMINIUM PROFILE-C | ALUMINIUM

HANDLE : ALUMINIUM PROFILE-J | ALUMINIUM


HANDLE : HAFELE # 125.95.910

HANDLE : HAFELE #126.95.920



เสริมแข็ง : Ivory



SECTION 1

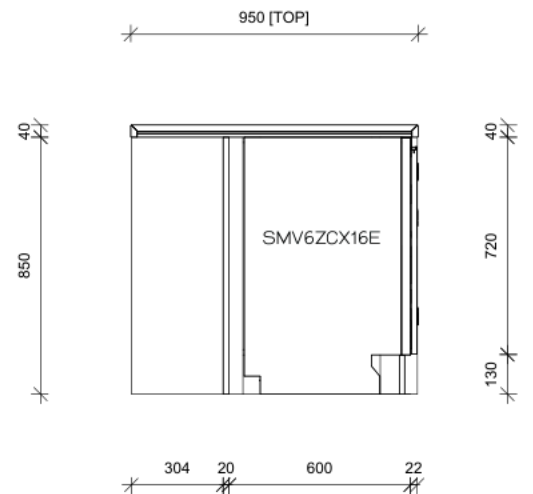

SECTION 2

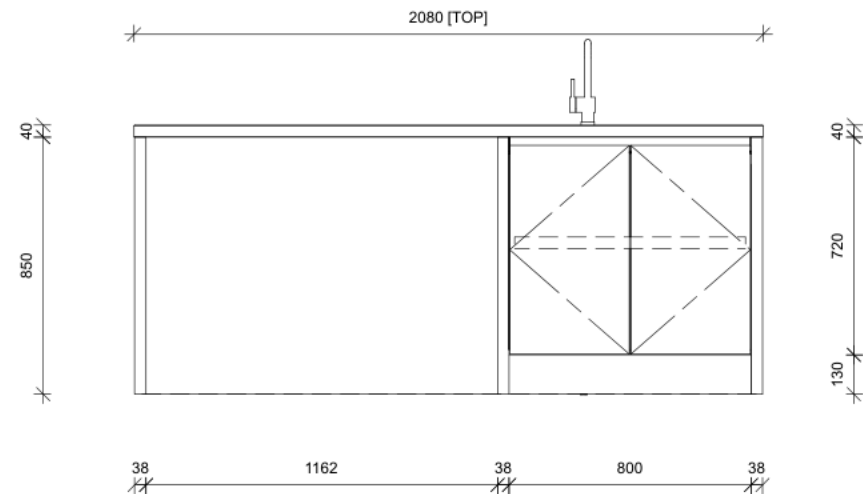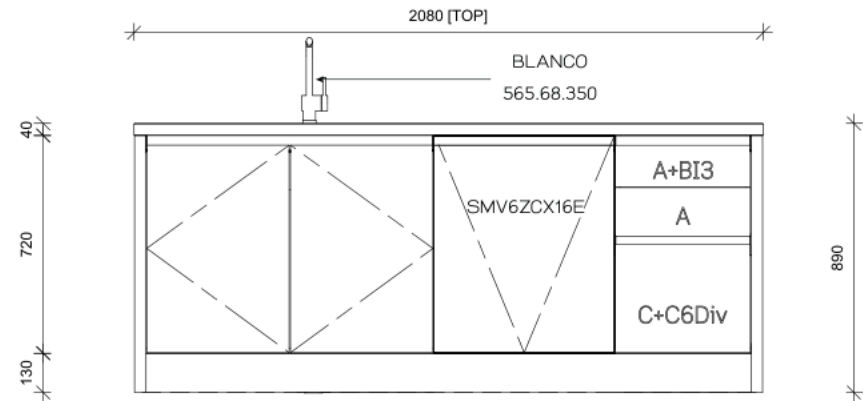

Dkbb

157 Praditmanutham Road
Bangkapi Bangkok 10240
TEL:0-2515-1162 FAX:0-2515-1161
WWW.decorchoice.co.th

Client : ARI 789

Address :

Province :-

Phone :

Design : Kitchen 6A

Series : Elegance Plus

Drawn by : บริษัท สุนทรจามร

Email :

View : Island

Scale : 1:25

Date : 10/4/2569

Page : 04