









INSIDE : DK Board Laminate DKBB #IAB 8101 | PLEASANT TEAK

OUT SIDE : DK Board Laminate FORMICA FENIX NTM #0748 | BEIGE ARIZONA

FRONTAGE : VI PLUS Laminate FORMICA FENIX NTM #0748 | BEIGE ARIZONA

ด้านหลังปิด Laminate PANAPLAST # S-B 28779PM | LATTE

TOP/BACK SPLASH : QUARTZ VADARA #V743 | OSTARA DAWN 20 mm.


HANDLE : ALUMINIUM PROFILE-C | ALUMINIUM

HANDLE : ALUMINIUM PROFILE-J | ALUMINIUM

HANDLE : HAFELE # 125.95.910

HANDLE : HAFELE #126.95.920

เสริมแข็ง : Ivory

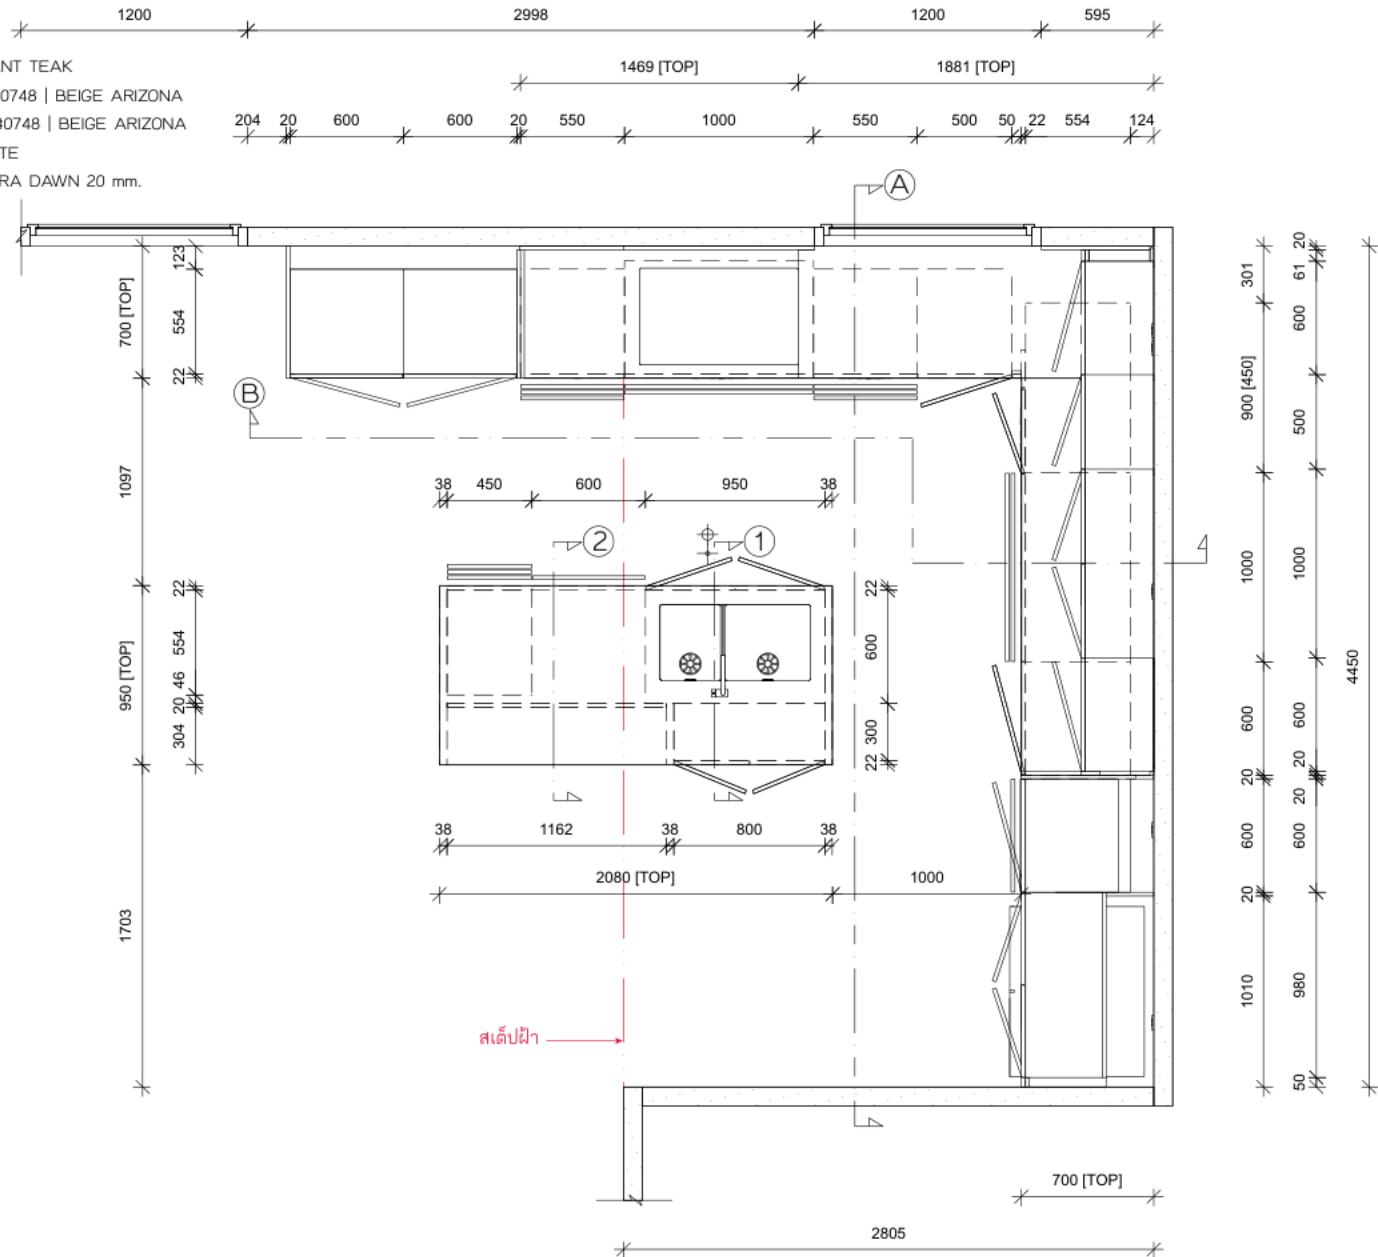

Dkbb

157 Praditmanutham Road
Bangkapi Bangkok 10240
TEL: 0-2515-1162 FAX: 0-2515-1161
WWW.decorchoice.co.th

Client : ARI 789

Address :-

Province :-

Phone :

Design : Kitchen 7A

Series : Elegance Plus

Drawn by : บริษัท สุนทรจามร


Email :

View : Plan

Scale : 1:30

Date : 25/4/2569

Page : 01

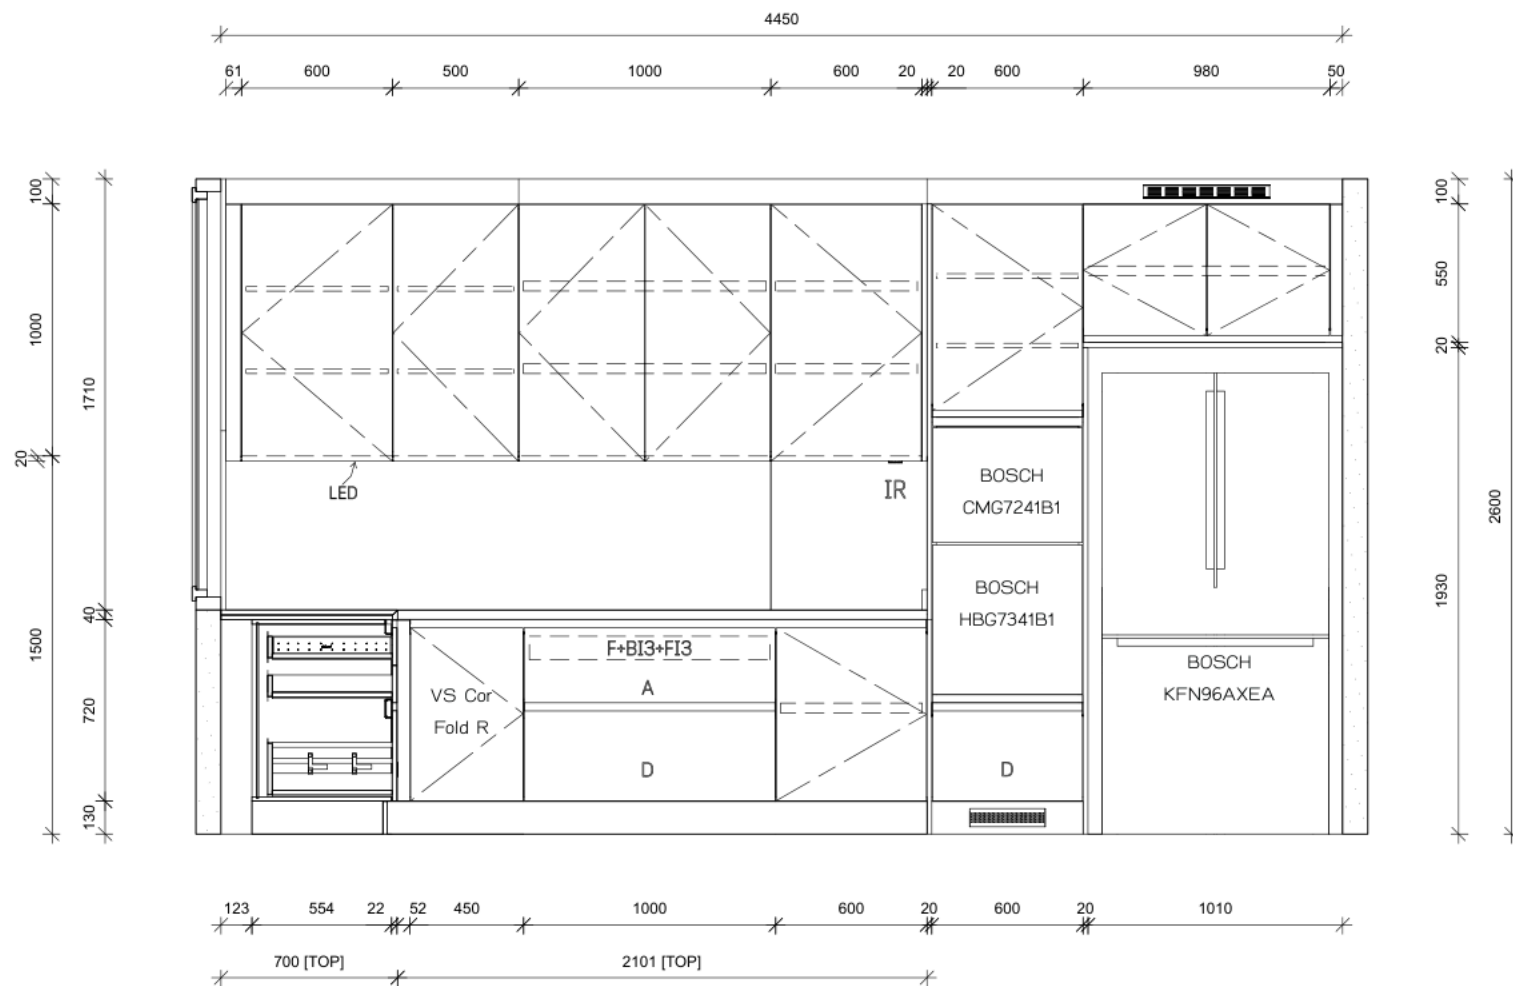

Dkbb

157 Praditmanutham Road
Bangkapi Bangkok 10240
TEL:0-2515-1162 FAX:0-2515-1161
WWW.decorchoice.co.th

Client : ARI 789

Address :

Province :-

Phone :

Design : Kitchen 7A

Series : Elegance Plus

Drawn by : บริษัท สุนทรจามร


Email :

View : Elevation A

Scale : 1:25

Date : 25/4/2569

Page : 02

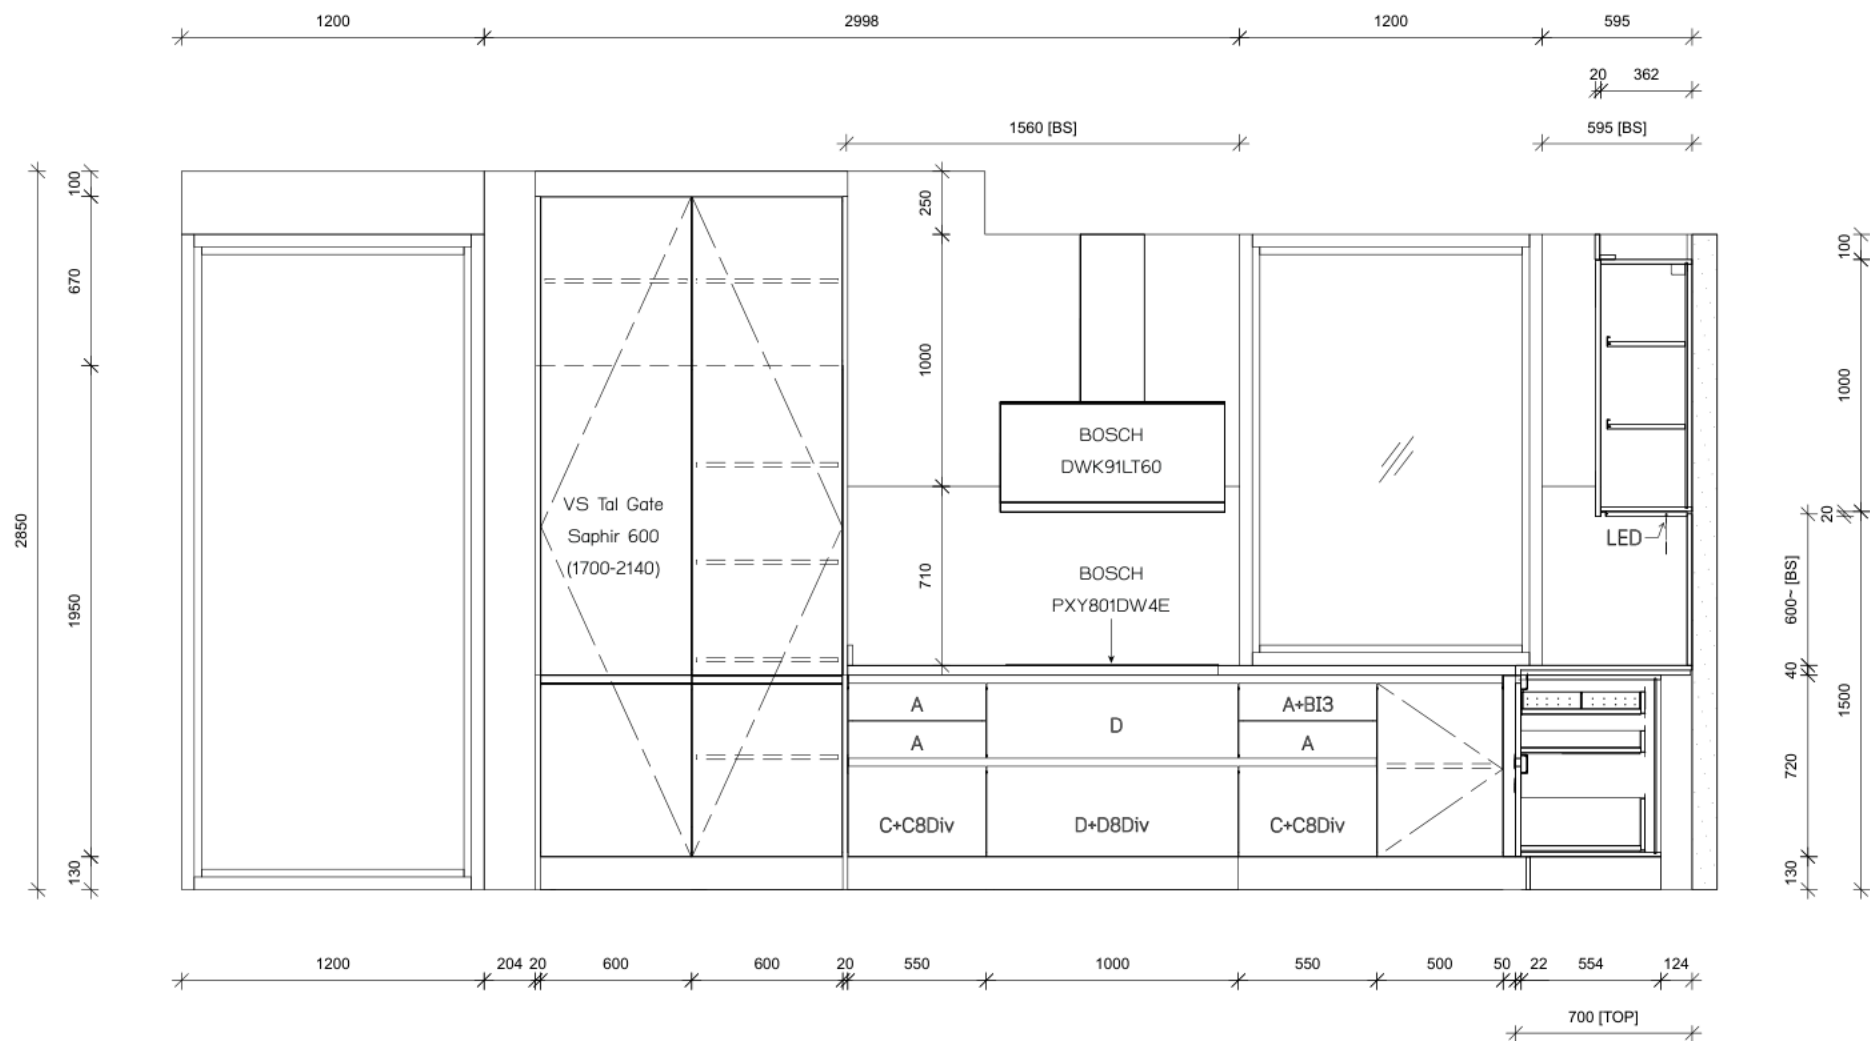

Dkbb

157 Praditmanutham Road
Bangkapi Bangkok 10240
TEL: 0-2515-1162 FAX: 0-2515-1161
WWW.decorchoice.co.th

Client : ARI 789

Address :

Province :-

Phone :

Design : Kitchen 7A

Series : Elegance Plus

Drawn by : บริษัท สุนทรจามร


Email :

View : Elevation B

Scale : 1:25

Date : 25/4/2569

Page : 03

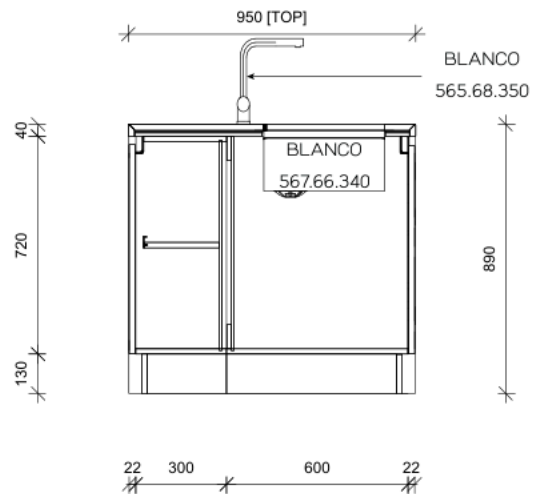

SECTION 1

INSIDE : DK Board Laminate DKBB #IAB 8101 | PLEASANT TEAK

OUT SIDE : DK Board Laminate FORMICA FENIX NTM #0748 | BEIGE ARIZONA

FRONTAGE : VI PLUS Laminate FORMICA FENIX NTM #0748 | BEIGE ARIZONA

ด้านหลังปิด Laminate PANAPLAST # S-B 28779PM | LATTE

TOP/BACK SPLASH : QUARTZ VADARA #V743 | OSTARA DAWN 20 mm.


HANDLE : ALUMINIUM PROFILE-C | ALUMINIUM

HANDLE : ALUMINIUM PROFILE-J | ALUMINIUM



HANDLE : HAFELE # 125.95.910

HANDLE : HAFELE #126.95.920

เสริมแข็ง : Ivory

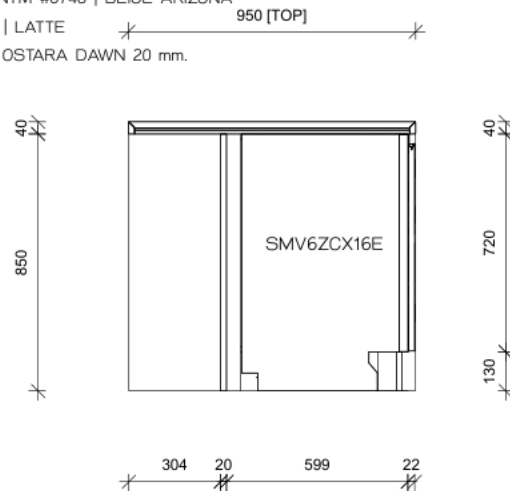

SECTION 2

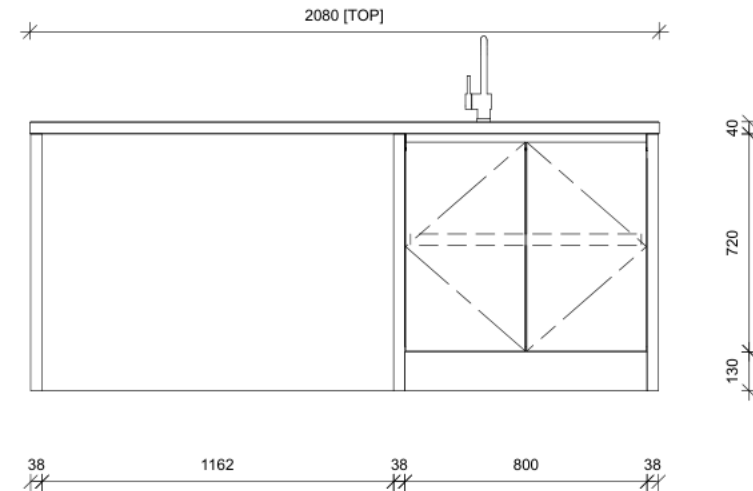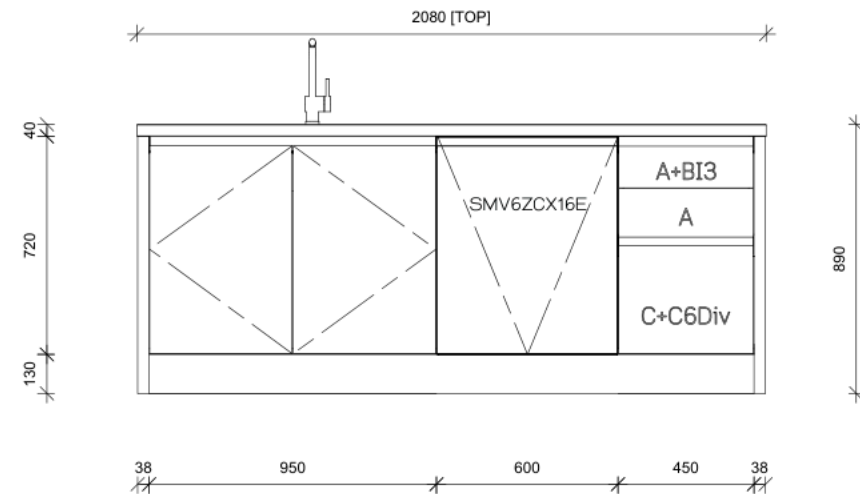

Dkbb

157 Praditmanutham Road
Bangkapi Bangkok 10240
TEL:0-2515-1162 FAX:0-2515-1161
WWW.decorchoice.co.th

Client : ARI 789

Address :

Province :-

Phone :

Design : Kitchen 7A

Series : Elegance Plus

Drawn by : บริษัท สุนทรจามร

Email :

View : Island

Scale : 1:25

Date : 25/4/2569

Page : 04