


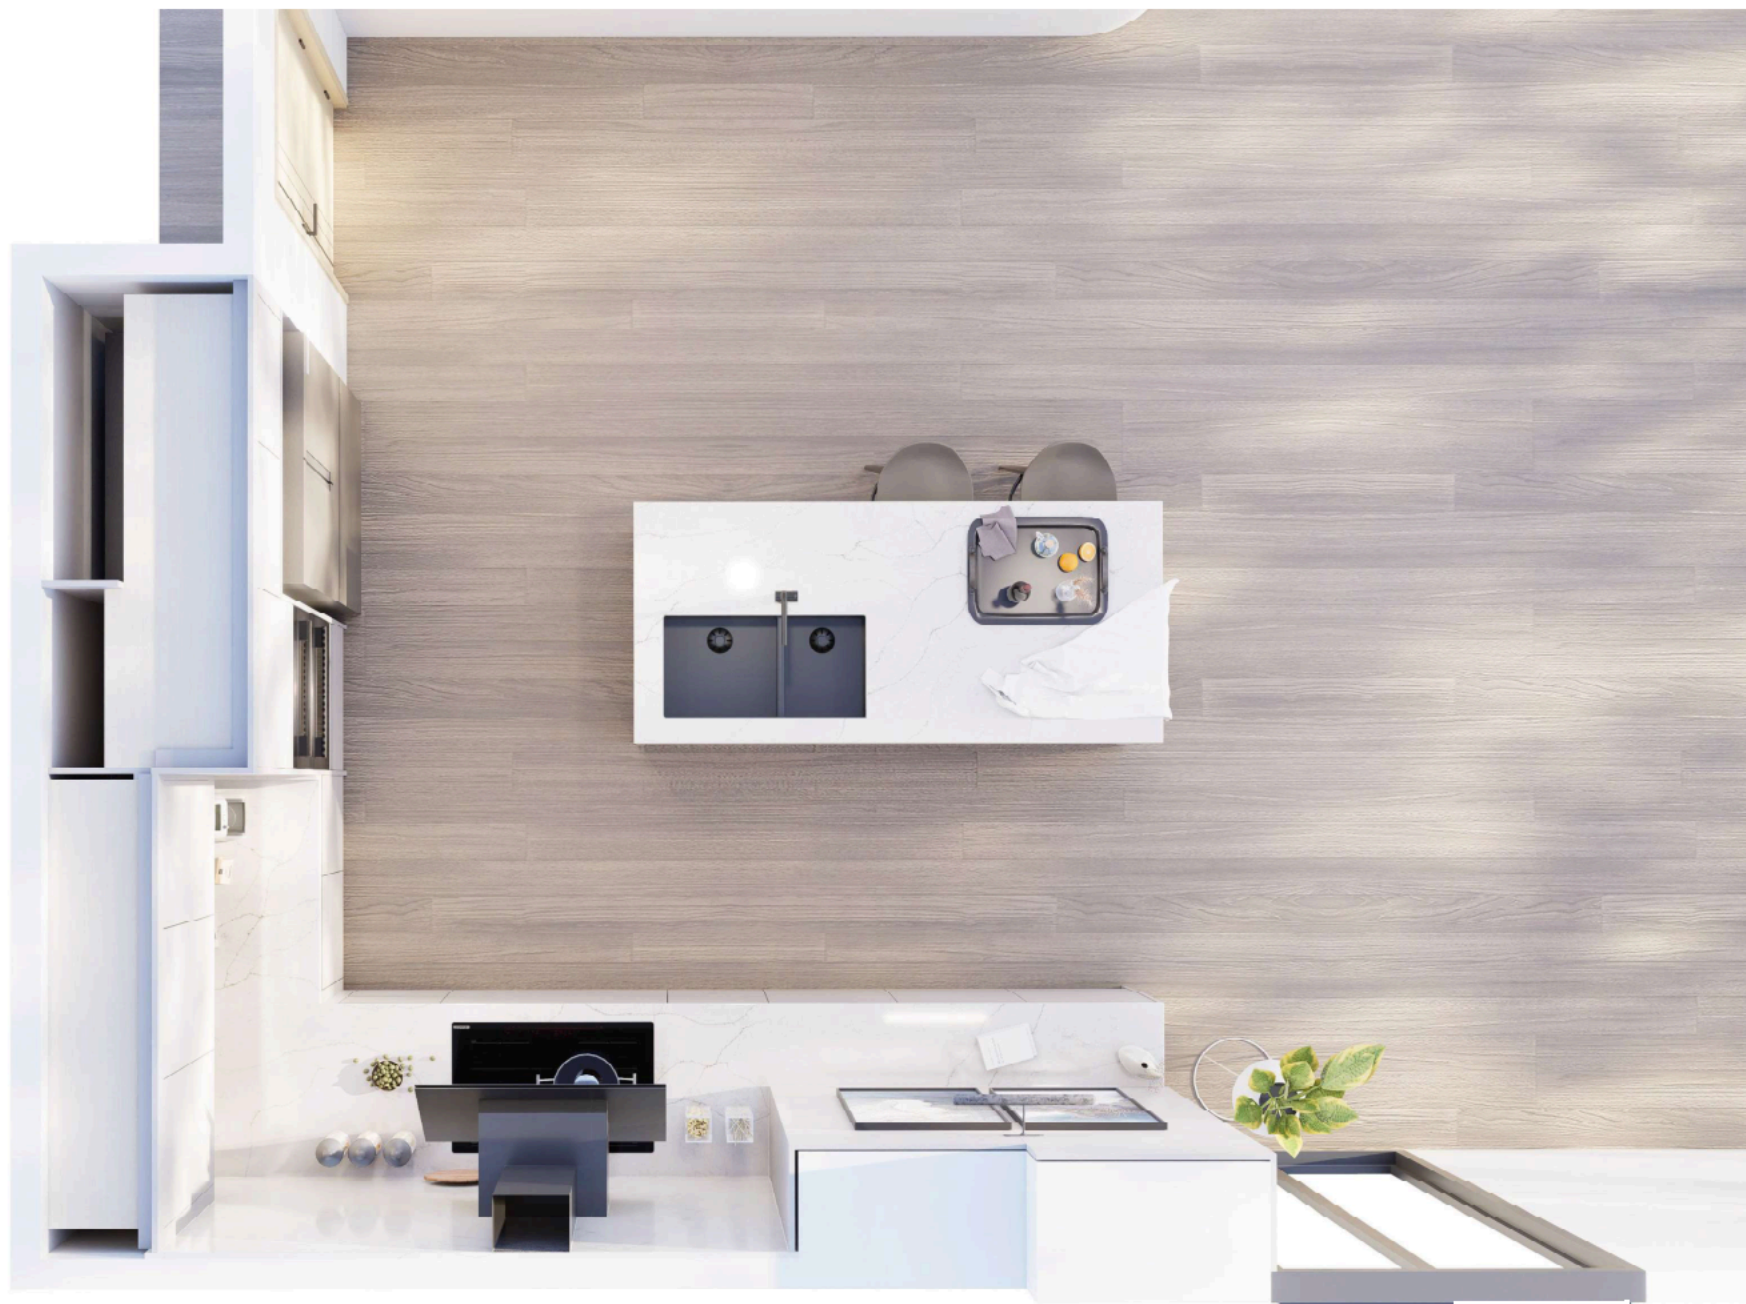







INSIDE : DK Board Laminate DKBB #IAB 8101 | PLEASANT TEAK
 OUTSIDE : DK Board Laminate FORMICA FENIX NTM #0748 | BEIGE ARIZONA
 FRONTAGE : VI PLUS Laminate FORMICA FENIX NTM #0748 | BEIGE ARIZONA
 ด้านหลังปิด Laminate PANAPLAST # S-B 28779PM | LATTE
 TOP/BACK SPLASH : QUARTZ VADARA #V743 | OSTARA DAWN 20 mm.
 HANDLE : ALUMINIUM PROFILE-C | ALUMINIUM
 HANDLE : ALUMINIUM PROFILE-J | ALUMINIUM
 HANDLE : HAFELE # 125.95.910
 เสีร์มแข็ง : Ivory

Dkbb

157 Praditmanutham Road
 Bangkapi Bangkok 10240
 TEL:0-2515-1162 FAX:0-2515-1161
 WWW.decorchoice.co.th

Client : ARI 789

Address :

Province :-

Phone :

Design : Kitchen 7B

Series : Elegance Plus

Drawn by : บริษัท สุนทรจามร


Email :

View : Plan


Scale : 1:30

Date : 20/3/2569

Page : 01

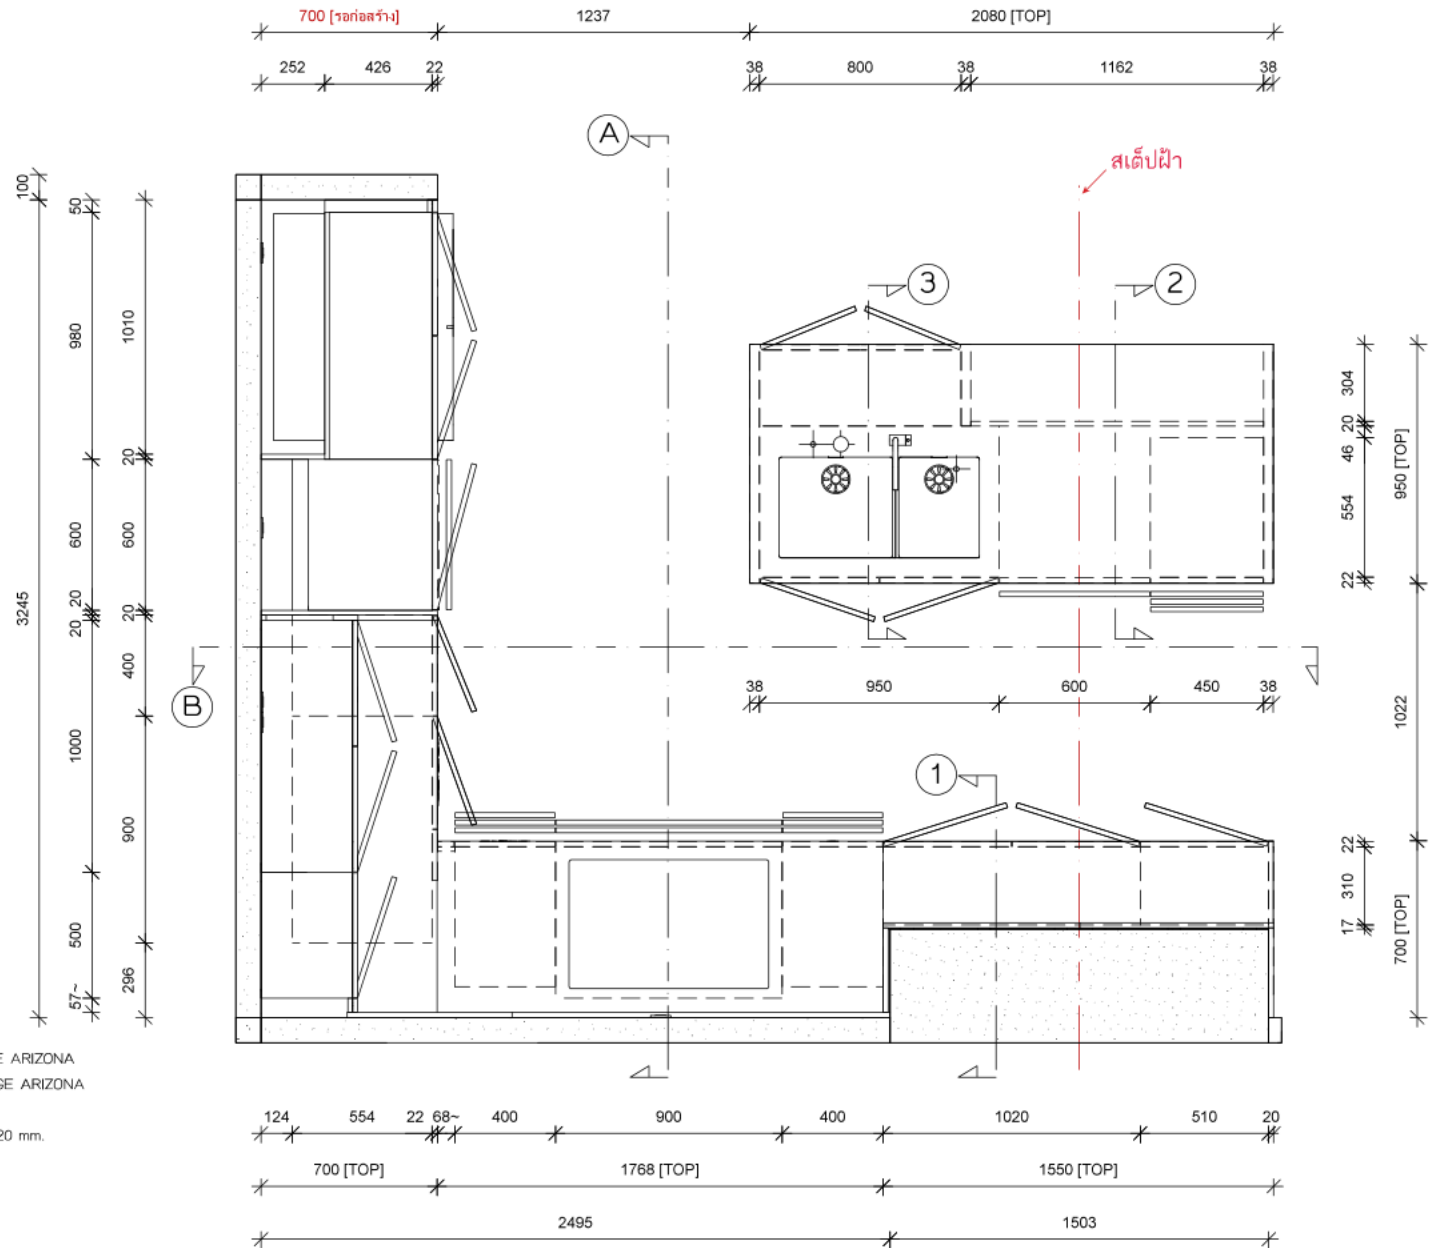



INSIDE : DK Board Laminate DKBB #IAB 8101 | PLEASANT TEAK
 OUTSIDE : DK Board Laminate FORMICA FENIX NTM #0748 | BEIGE ARIZONA
 FRONTAGE : VI PLUS Laminate FORMICA FENIX NTM #0748 | BEIGE ARIZONA
 ด้านหลังปิด Laminate PANAPLAST # S-B 28779PM | LATTE
 TOP/BACK SPLASH : QUARTZ VADARA #V743 | OSTARA DAWN 20 mm.
 HANDLE : ALUMINIUM PROFILE-C | ALUMINIUM
 HANDLE : ALUMINIUM PROFILE-J | ALUMINIUM
 HANDLE : HAFELE # 125.95.910
 เสีร์มีแข็ง : Ivory

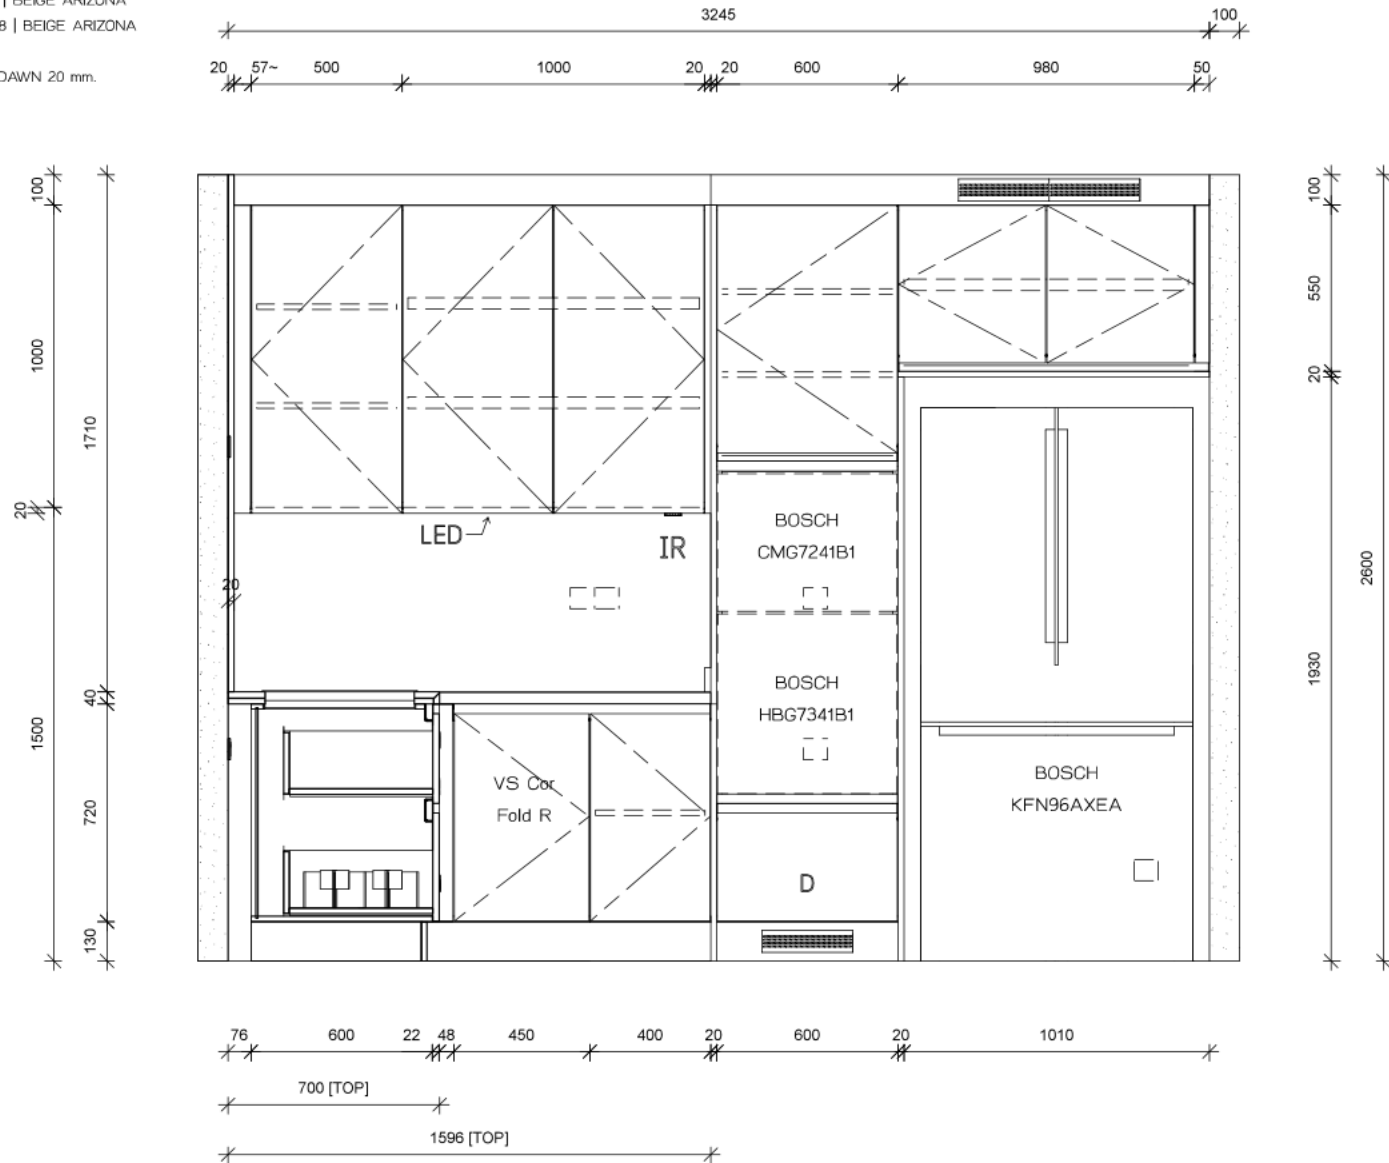

Dkbb

157 Praditmanutham Road
 Bangkapi Bangkok 10240
 TEL:0-2515-1162 FAX:0-2515-1161
 WWW.decochoice.co.th

Client : ARI 789	Design : Kitchen 7B	View : Elevation A
Address :	Series : Elegance Plus	Scale : 1:25
Province :-	Drawn by : บริษัท สุนทรจามร	Date : 20/3/2569
Phone :	Email :	Page : 02

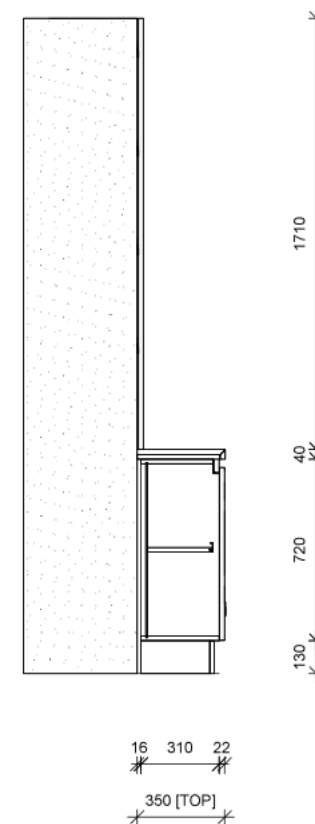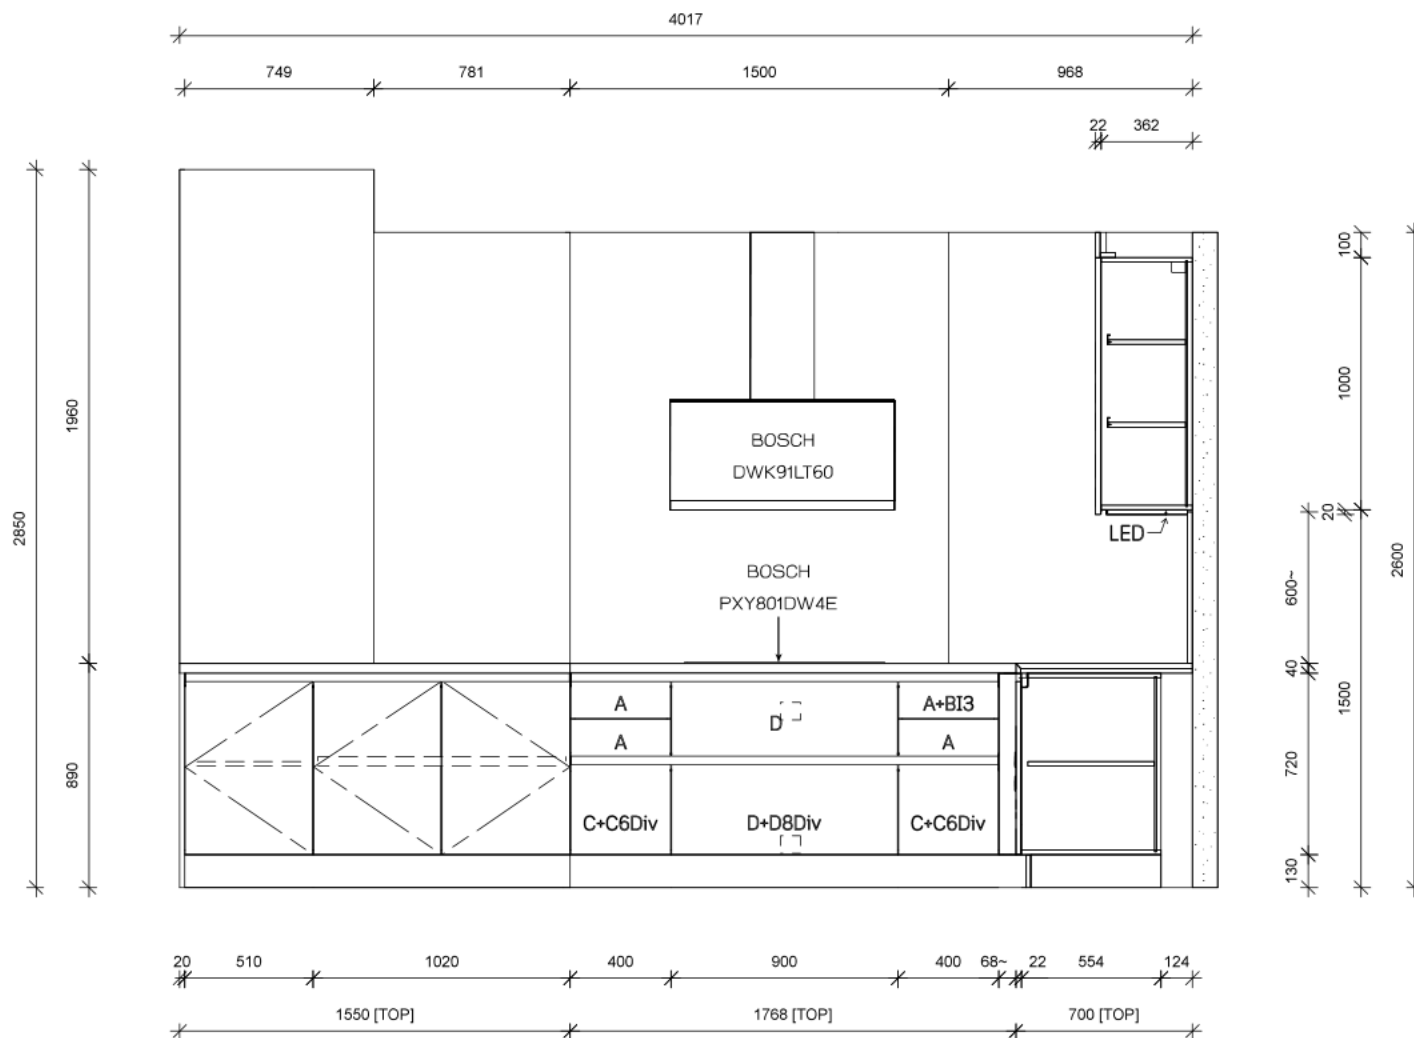

SECTION 1


INSIDE : DK Board Laminate DKBB #IAB 8101 | PLEASANT TEAK
 OUTSIDE : DK Board Laminate FORMICA FENIX NTM #0748 | BEIGE ARIZONA
 FRONTAGE : VI PLUS Laminate FORMICA FENIX NTM #0748 | BEIGE ARIZONA
 ด้านหลังปิด Laminate PANAPLAST # S-B 28779PM | LATTE
 TOP/BACK SPLASH : QUARTZ VADARA #V743 | OSTARA DAWN 20 mm.
 HANDLE : ALUMINIUM PROFILE-C | ALUMINIUM
 HANDLE : ALUMINIUM PROFILE-J | ALUMINIUM
 HANDLE : HAFELE # 125.95.910
 เสีร์มแข็ง : Ivory

Dkbb


157 Praditmanutham Road
 Bangkapi Bangkok 10240
 TEL:0-2515-1162 FAX:0-2515-1161
 WWW.decorchoice.co.th

Client : ARI 789	Design : Kitchen 7B	View : Elevation B , Section 1
Address :	Series : Elegance Plus	Scale : 1:30
Province :-	Drawn by : บริษัท สุนทรจามร	Date : 20/3/2569
Phone :	Email :	Page : 03



INSIDE : DK Board Laminate DKBB #IAB 8101 | PLEASANT TEAK
 OUTSIDE : DK Board Laminate FORMICA FENIX NTM #0748 | BEIGE ARIZONA
 FRONTAGE : VI PLUS Laminate FORMICA FENIX NTM #0748 | BEIGE ARIZONA
 ด้านหลังปิด Laminate PANAPLAST # S-B 28779PM | LATTE
 TOP/BACK SPLASH : QUARTZ VADARA #V743 | OSTARA DAWN 20 mm.
 HANDLE : ALUMINIUM PROFILE-C | ALUMINIUM
 HANDLE : ALUMINIUM PROFILE-J | ALUMINIUM
 HANDLE : HAFELE # 125.95.910
 เสีรมันชิ่ง : Ivory

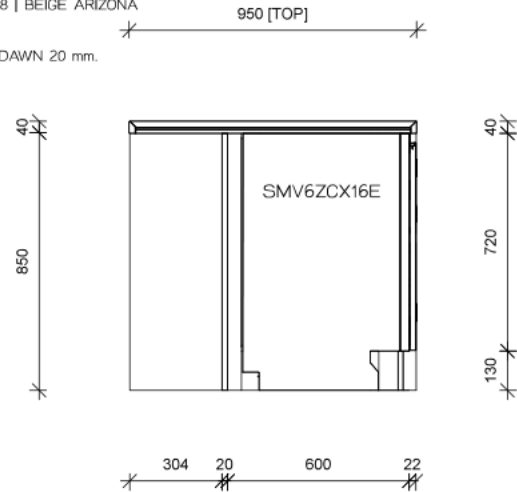

SECTION 2

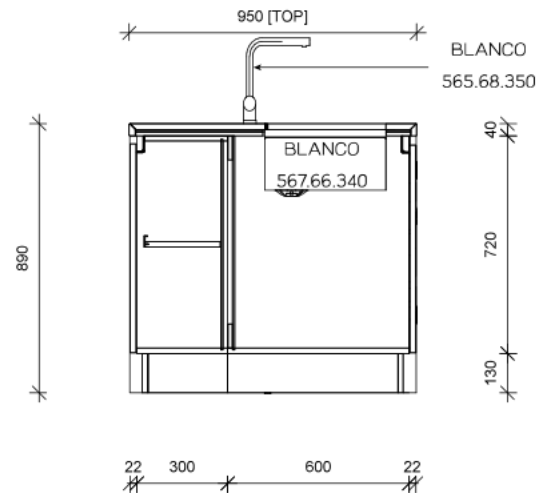

SECTION 3

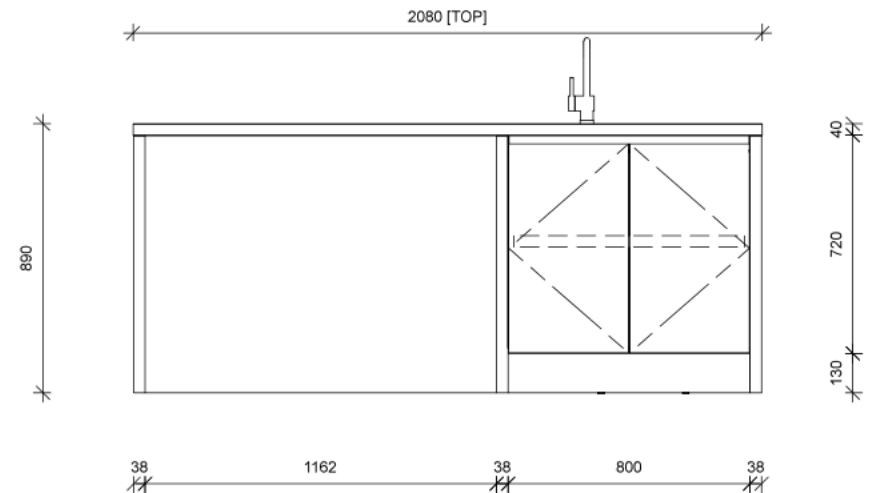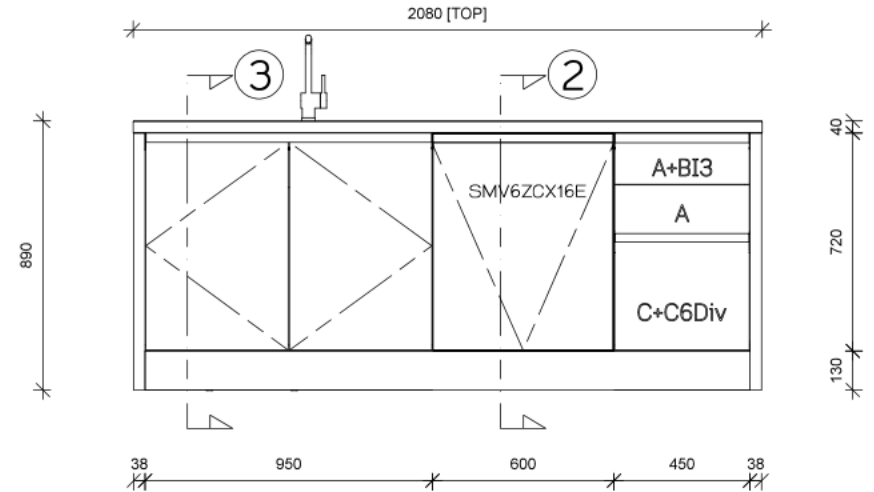

Dkbb

157 Praditmanutham Road
 Bangkapi Bangkok 10240
 TEL:0-2515-1162 FAX:0-2515-1161
 WWW.decorchoice.co.th

Client : ARI 789	Design : Kitchen 7B	View : Island
Address :	Series : Elegance Plus	Scale : 1:25
Province :-	Drawn by : บริษัท สุนทราจามร	Date : 20/3/2569
Phone :	Email :	Page : 04