












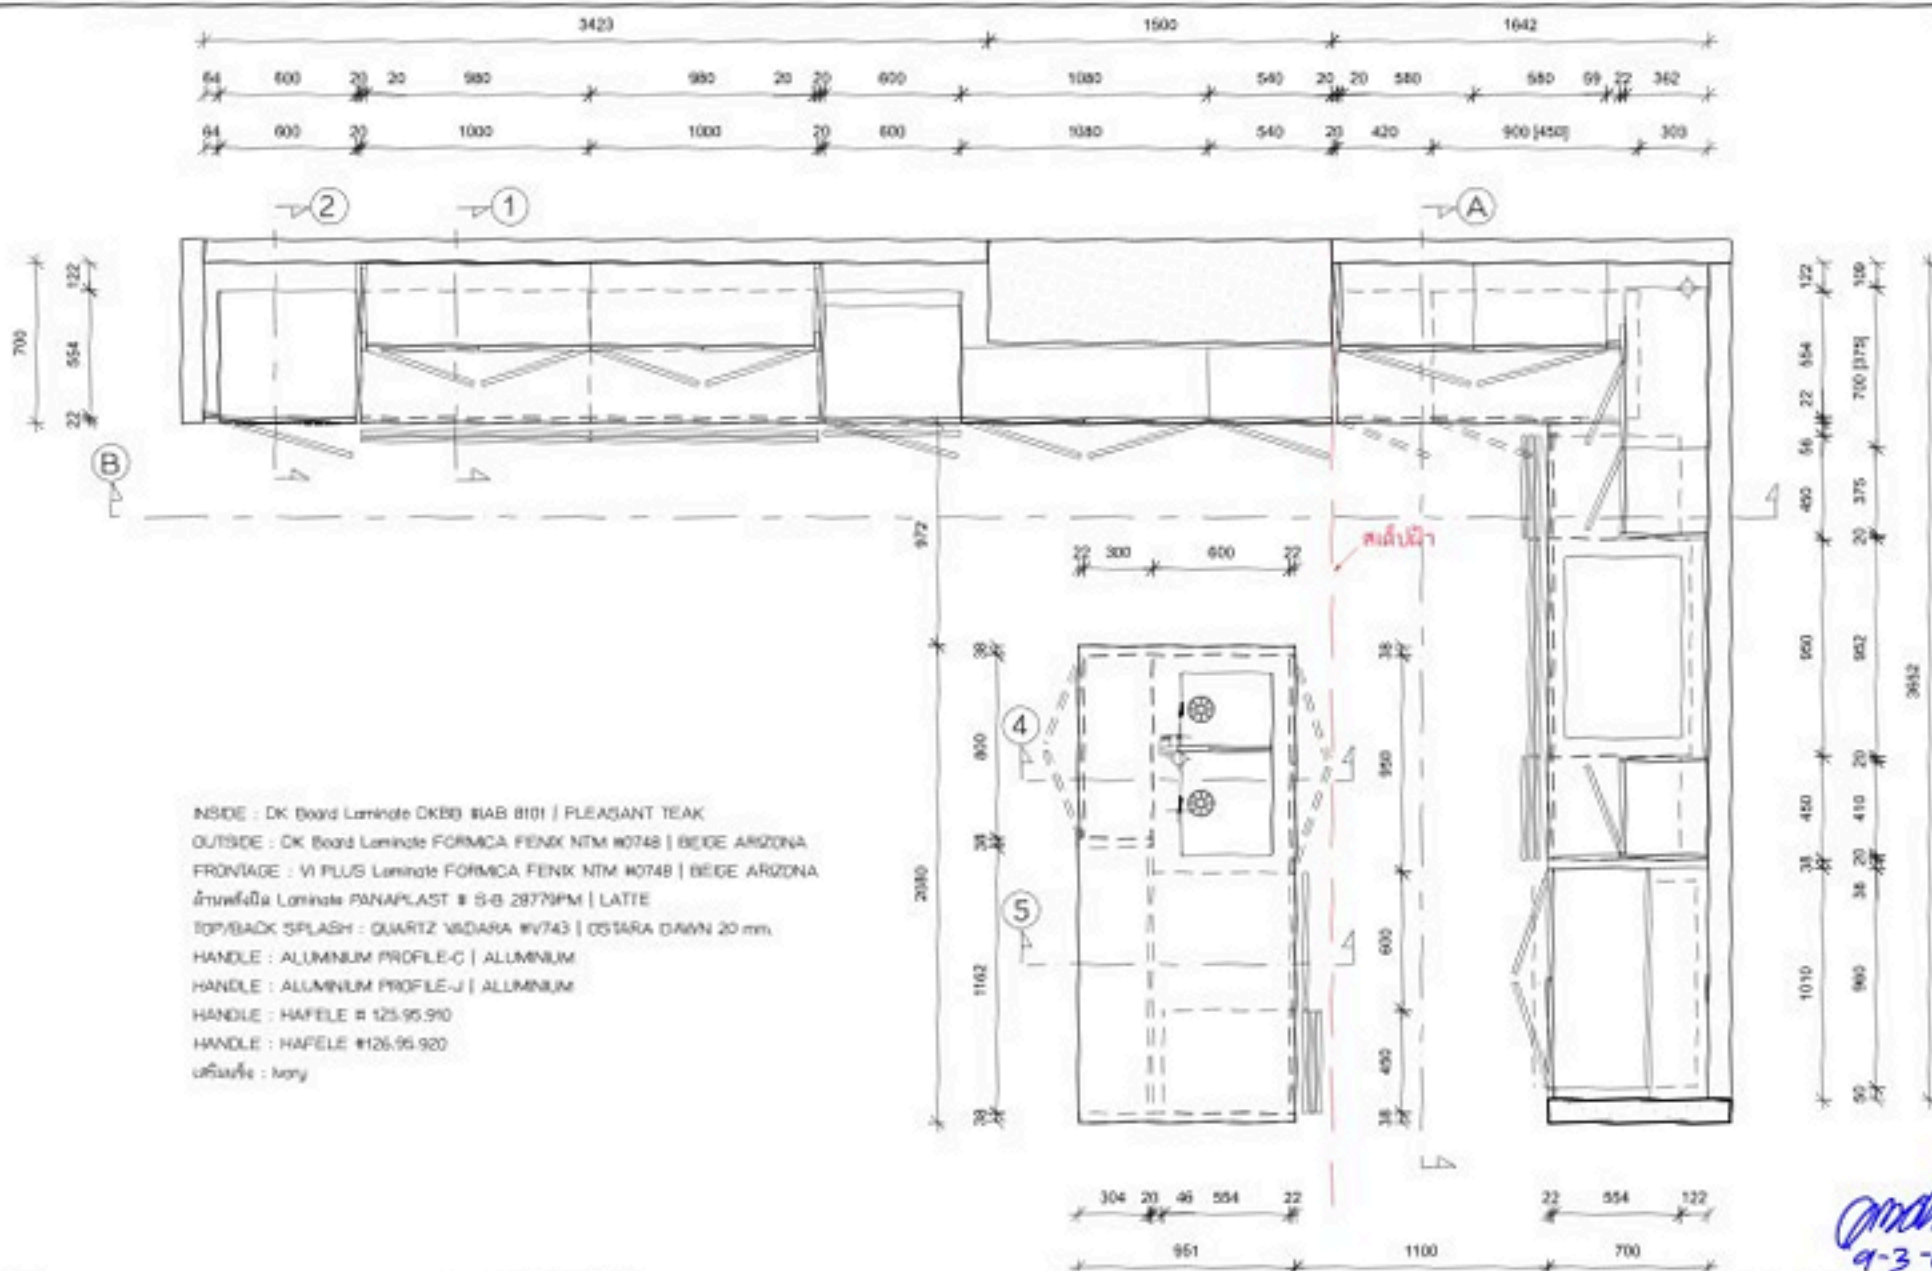

Dkbb

157 Praditmanutham Road
 Bangkok Bangkok 10240
 TEL 0-2615-1162 FAX 0-2515-1161
 09096 dkkorachok@dkb.co.th

Client : Ari 789

Address :

Province :-

Phone :

Design : Kitchen 3A

Series : Elegance Plus

Drawn by : บริษัท ดเคเคเคเคเคเค


Email :

View : Plan

Scale : 1:33

Date : 28/2/2569

Page : 01

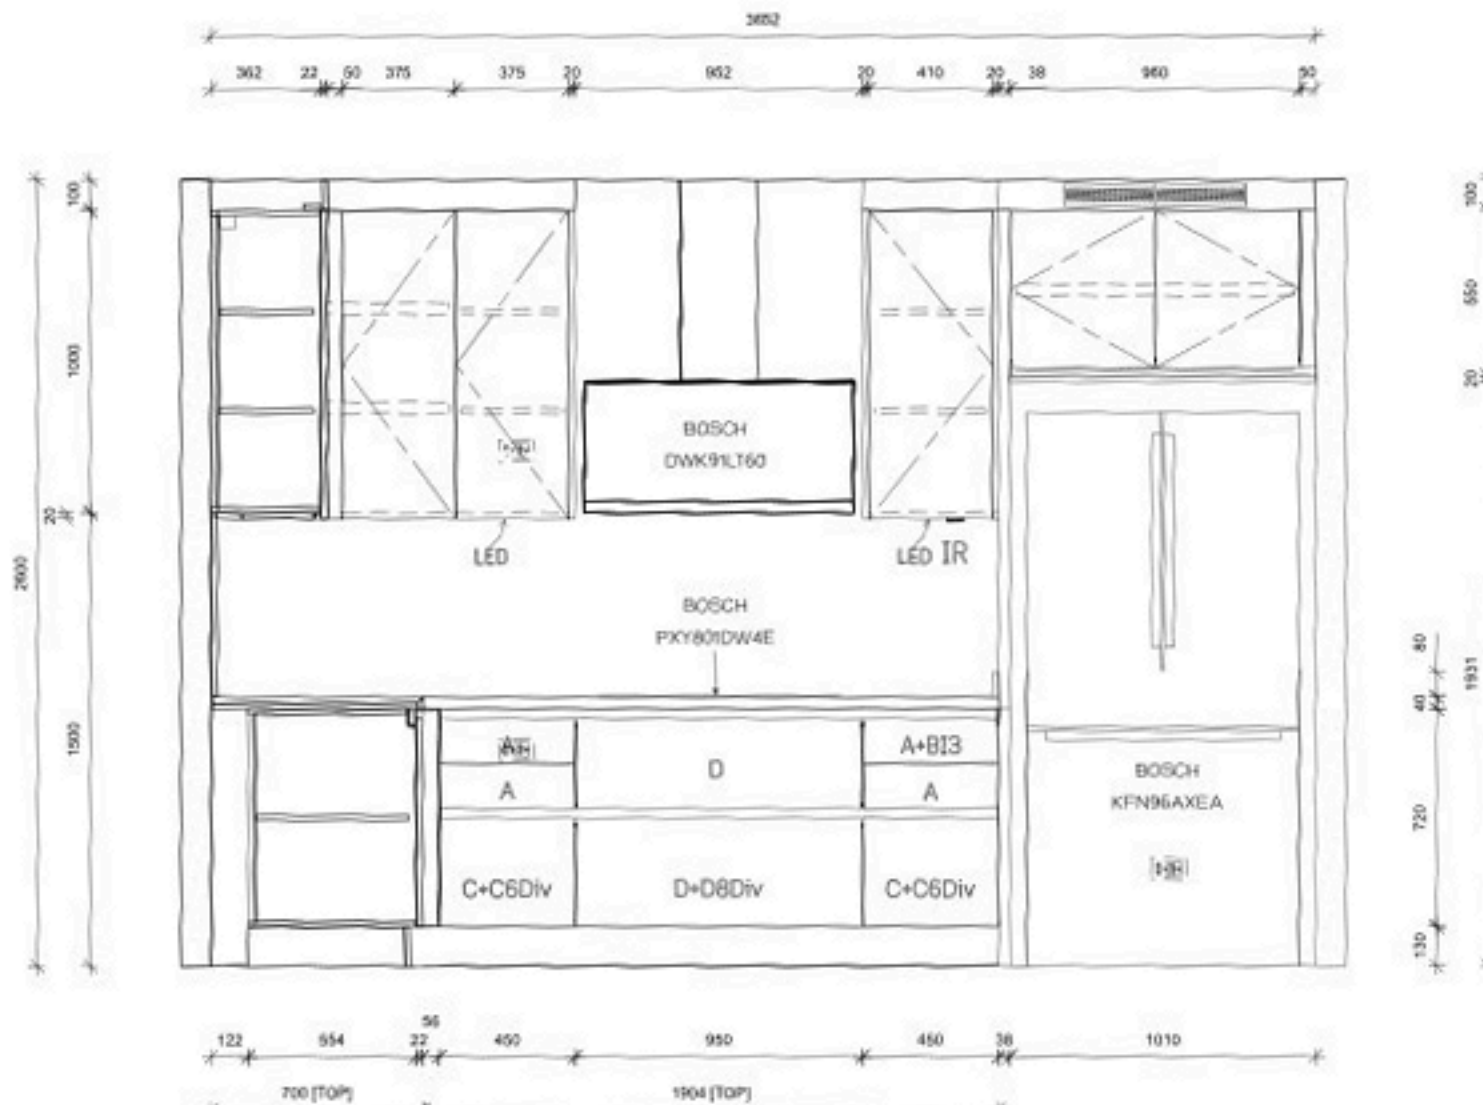

INSIDE : OK Board Laminat DKB #IAB 8101 | PLEASANT TEAK

OUTSIDE : OK Board Laminat FORMICA FENIX NTM #0748 | BEIGE ARIZONA

FRONTAGE : V PLUS Laminat FORMICA FENIX NTM #0748 | BEIGE ARIZONA

ตัวเคลือบ Laminat PANAPLAST # S-B 28779PM | LATTE

TOP/BACK SPLASH : QUARTZ WADARA #V743 | OSTARA DAWN 20 mm.

HANDLE : ALUMINUM PROFILE-C | ALUMINUM

HANDLE : ALUMINUM PROFILE-J | ALUMINUM

HANDLE : HAFELE # 125.95.910

HANDLE : HAFELE #126.95.920

ไม้เคลือบ : Ivory

Dkbb

157 Praditmanutham Road
Bangkapi Bangkok 10240

TEL 0-2515-1182 FAX 0-2515-1181
WWW.dkbscholar.co.th

Client : ARI 789

Address :

Province :-

Phone :

Design : Kitchen 3A

Series : Elegance Plus

Drawn by : วิศวกร สถาปนิก

Email :


View : Elevation A

Scale : 1:25

Date : 28/2/2569

Page : 02

Handwritten signature and date:
9-3-69

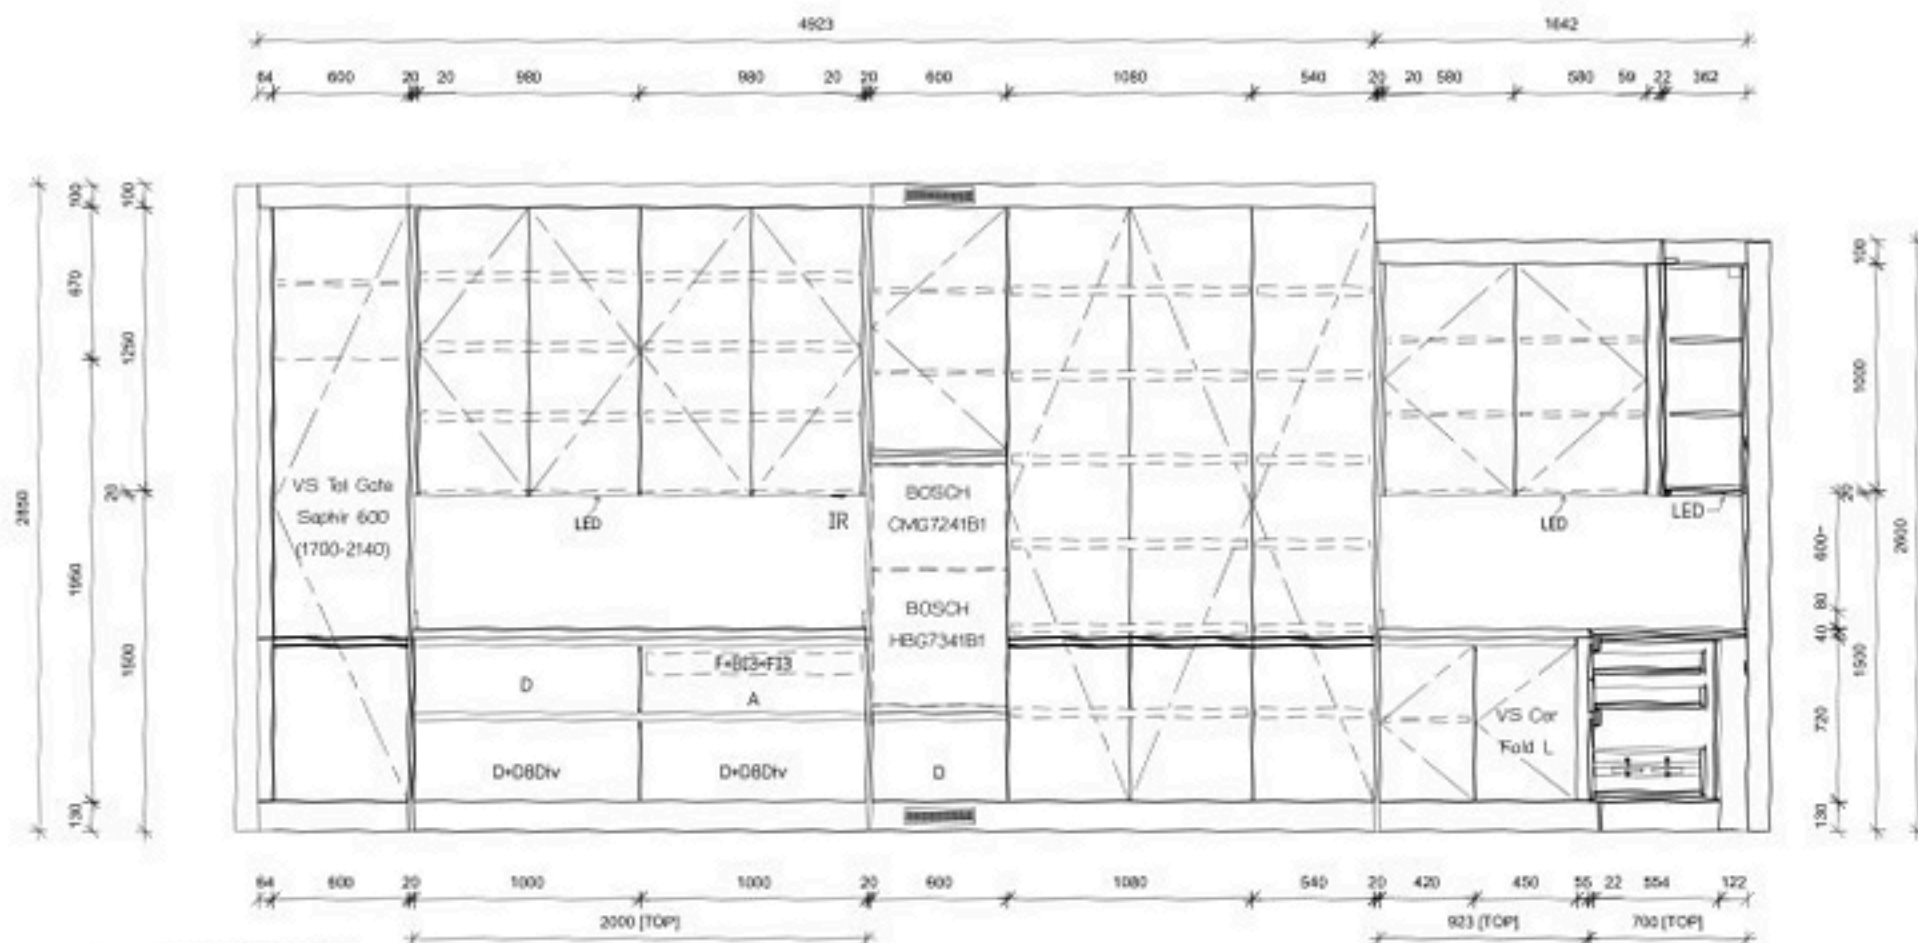

INSIDE : DK Board Laminat DKB #WB 8101 | PLEASANT TEAK
 OUTSIDE : DK Board Laminat FORMICA FENIX NTM #0748 | BEIGE ARIZONA
 FRONTAGE : VI PLUS Laminat FORMICA FENIX NTM #0748 | BEIGE ARIZONA
 Dinding Laminat PANAPLAST # S-B 28779PM | LATTE
 TOP/BACK SPLASH : QUARTZ WADARA #V743 | OSTARA DAWN 20 mm
 HANDLE : ALUMINUM PROFILE-C | ALUMINUM
 HANDLE : ALUMINUM PROFILE-J | ALUMINUM
 HANDLE : HAFELE # 125.95.910
 HANDLE : HAFELE #125.95.920
 Material : kayu

amh
 9-3-69

Dkbb

157 Praditmanutham Road
 Bangkok Bangkok 10240
 TEL 0-2515-1182 FAX 0-2515-1181
 WWW.dkbb.co.th

Client : Ari 789

Address :

Province :-

Phone :

Design : Kitchen 3A

Series : Elegance Plus

Drawn by : บริษัท ดเคบี จำกัด


Email :

View : Elevation B


Scale : 1:33.33

Date : 28/2/2569

Page : 03

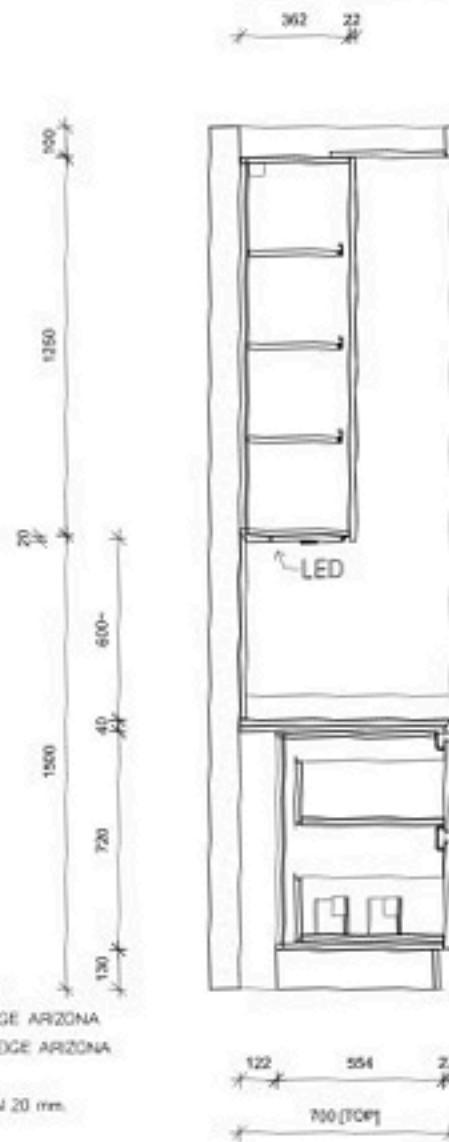

SECTION 1

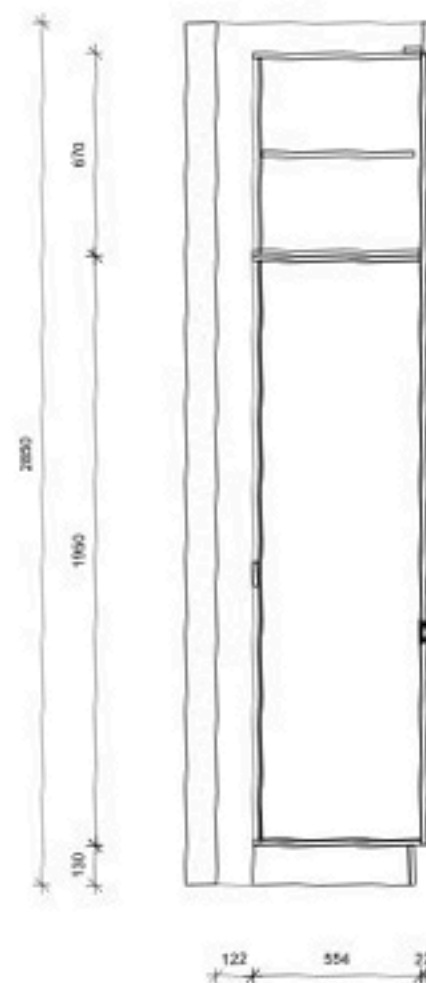

SECTION 2

INSIDE : DK Board Laminale DKB WAB 8101 | PLEASANT TEAK
 OUTSIDE : DK Board Laminale FORMICA FENIX NTM #0748 | BEGE ARIZONA
 FRONTAGE : VI PLUS Laminale FORMICA FENIX NTM #0748 | BEGE ARIZONA
 ฉากด้านหลัง Laminale PANAPLAST # S-B 28779PM | LATTE
 TOP/BACK SPLASH : QUARTZ WADARA #V743 | OSTARA DAWN 20 mm.
 HANDLE : ALUMINUM PROFILE-C | ALUMINUM
 HANDLE : ALUMINUM PROFILE-J | ALUMINUM
 HANDLE : HAFELE # 125.95.910
 HANDLE : HAFELE # 126.95.920
 วัสดุอื่น : Ivory

Handwritten signature and date
 27-3-69

Dkbb

157 Praditmanutham Road
 Bangkapi Bangkok 10240
 TEL 0-2515-1162 FAX 0-2515-1161
 09096 deconchoke.co.th

Client : Ari 789	Design : Kitchen 3A	View : Section 1,2
Address :	Series : Elegance Plus	Scale : 1:25
Province :-	Drawn by : บริษัท ดีเคบีไทย	Date : 28/2/2569
Phone :	Email :	Page : 04

INSIDE : DK Board Laminat DKB #IAB 8101 | PLEASANT TEAK

OUTSIDE : DK Board Laminat FORMICA FENIX NTM #0748 | BEIGE ARIZONA

FRONTAGE : VI PLUS Laminat FORMICA FENIX NTM #0748 | BEIGE ARIZONA

ชั้นวางจาน Laminat PANAPLAST # S-B 28779PM | LATTE

TOP/BACK SPLASH : QUARTZ VADARA #V743 | OSTARA DAWN 20 mm

HANDLE : ALUMINUM PROFILE-C | ALUMINUM

HANDLE : ALUMINUM PROFILE-J | ALUMINUM

HANDLE : HAFELE # 125.95.910

HANDLE : HAFELE #126.95.920

เก้าอี้บาร์ | Ivory




22 400 300 22

SECTION 4




20 602 20 304

SECTION 5

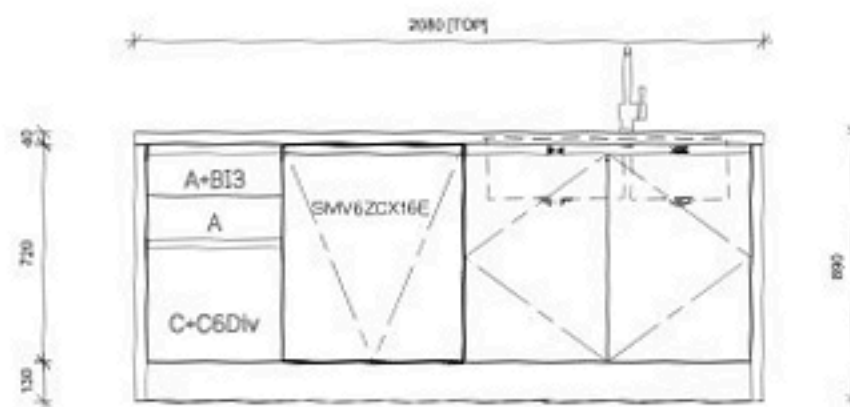

40 450 600 900 40

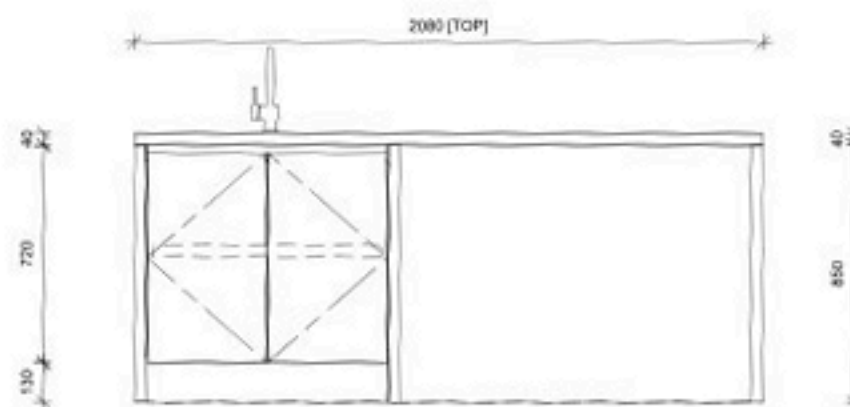

38 800 38 1162 38

Qmoh
9-3-69

Dkbb

157 Praditmanutham Road
Bangkok Bangkok 10240
TEL: 0-2615-1162 FAX: 0-2615-1161
WWW.DKBKITCHEN.CO.TH

Client : Ari 789

Address :

Province :-

Phone :

Design : Kitchen 3A

Series : Elegance Plus

Drawn by : บริษัท ดีเคบีเค

Email :

View : Island

Scale : 1:25

Date : 28/2/2569

Page : 05



โบสถ์เฟอร์นิเจอร์ บริษัท อารี 789 ดีเวลลอปเม้นท์ จำกัด
เลขที่ 10/1 ซอยพหลโยธิน 5 ถนนพหลโยธิน แขวงพญาไท เขตพญาไท
กรุงเทพมหานคร 10400 โทร : 044-110218
เลขประจำตัวผู้เสียภาษีอากร 0105565012642 (สำนักงานใหญ่)

9 มีนาคม 2569

3A Floor 3-KITCHEN รุ่น ELEGANCE PLUS (กันปลวกกันน้ำรับประกัน 10 ปี)

1 KITCHEN ตัว L		1,048,731.00
1.1 KITCHEN ตัว L ขนาด 0.70 X 10.217 X 2.85 ม.	744,346.00	
1.2 TOP และผนังกันเปื้อน หิน QUARTZ VADARA # V743 (OSTARA DAWN)	92,750.00	
1.3 อุปกรณ์ภายในตู้	211,635.00	
2 ISLAND		205,607.00
2.1 ISLAND ขนาด 1.00 X 2.08 X 0.89 ม.	150,227.00	
2.2 TOP หิน QUARTZ VADARA # V743 (OSTARA DAWN)	22,880.00	
2.3 อุปกรณ์ภายในตู้	32,500.00	
	รวม	1,254,338.00
	ส่วนลด 15%	-188,151.00
	ยอดรวม หลังหักส่วนลด	1,066,187.00
3 ไฟ LED		7,240.00
4 ค่าติดตั้งอุปกรณ์ครัว (ในกรณีลูกค้าซื้ออุปกรณ์ครัวเอง)		5,800.00
	รวมเงิน Ex. Vat	1,079,227.00
	VAT 7%	75,545.89
	ยอดสุทธิ	1,154,772.89

หมายเหตุ - ก่อนเซ็นสั่งซื้อสินค้า กรุณาตรวจสอบแบบและรายละเอียดต่างๆ ให้ครบถ้วน
เนื่องจากการสั่งผลิตเฉพาะงาน
- ไฟแสงสว่าง, สีของไฟ LED, ตำแหน่งปลั๊กใช้งาน, กุญแจล็อคต่างๆ ไม่สามารถเพิ่มภายหลังได้
กรุณาตรวจสอบก่อนว่ามีครบตามต้องการหรือไม่
- หลังจากสั่งซื้อสินค้าแล้ว ทางบริษัทฯ ขอสงวนสิทธิ์ในการแก้ไขใดๆทั้งสิ้น

บริษัท เดคคอร์ต ชอยส์ จำกัด

157 ซ.โยธินพัฒนา ถ.ประดิษฐ์มนูธรรม แขวงคลองจั่น เขตบางกะปิ กรุงเทพฯ 10240

Tel : 0 2515 1162 Fax : 0 2515 1161 Call Center : 08-1954-5550

E-mail : decorchoice@gmail.com www.decorchoice.co.th