


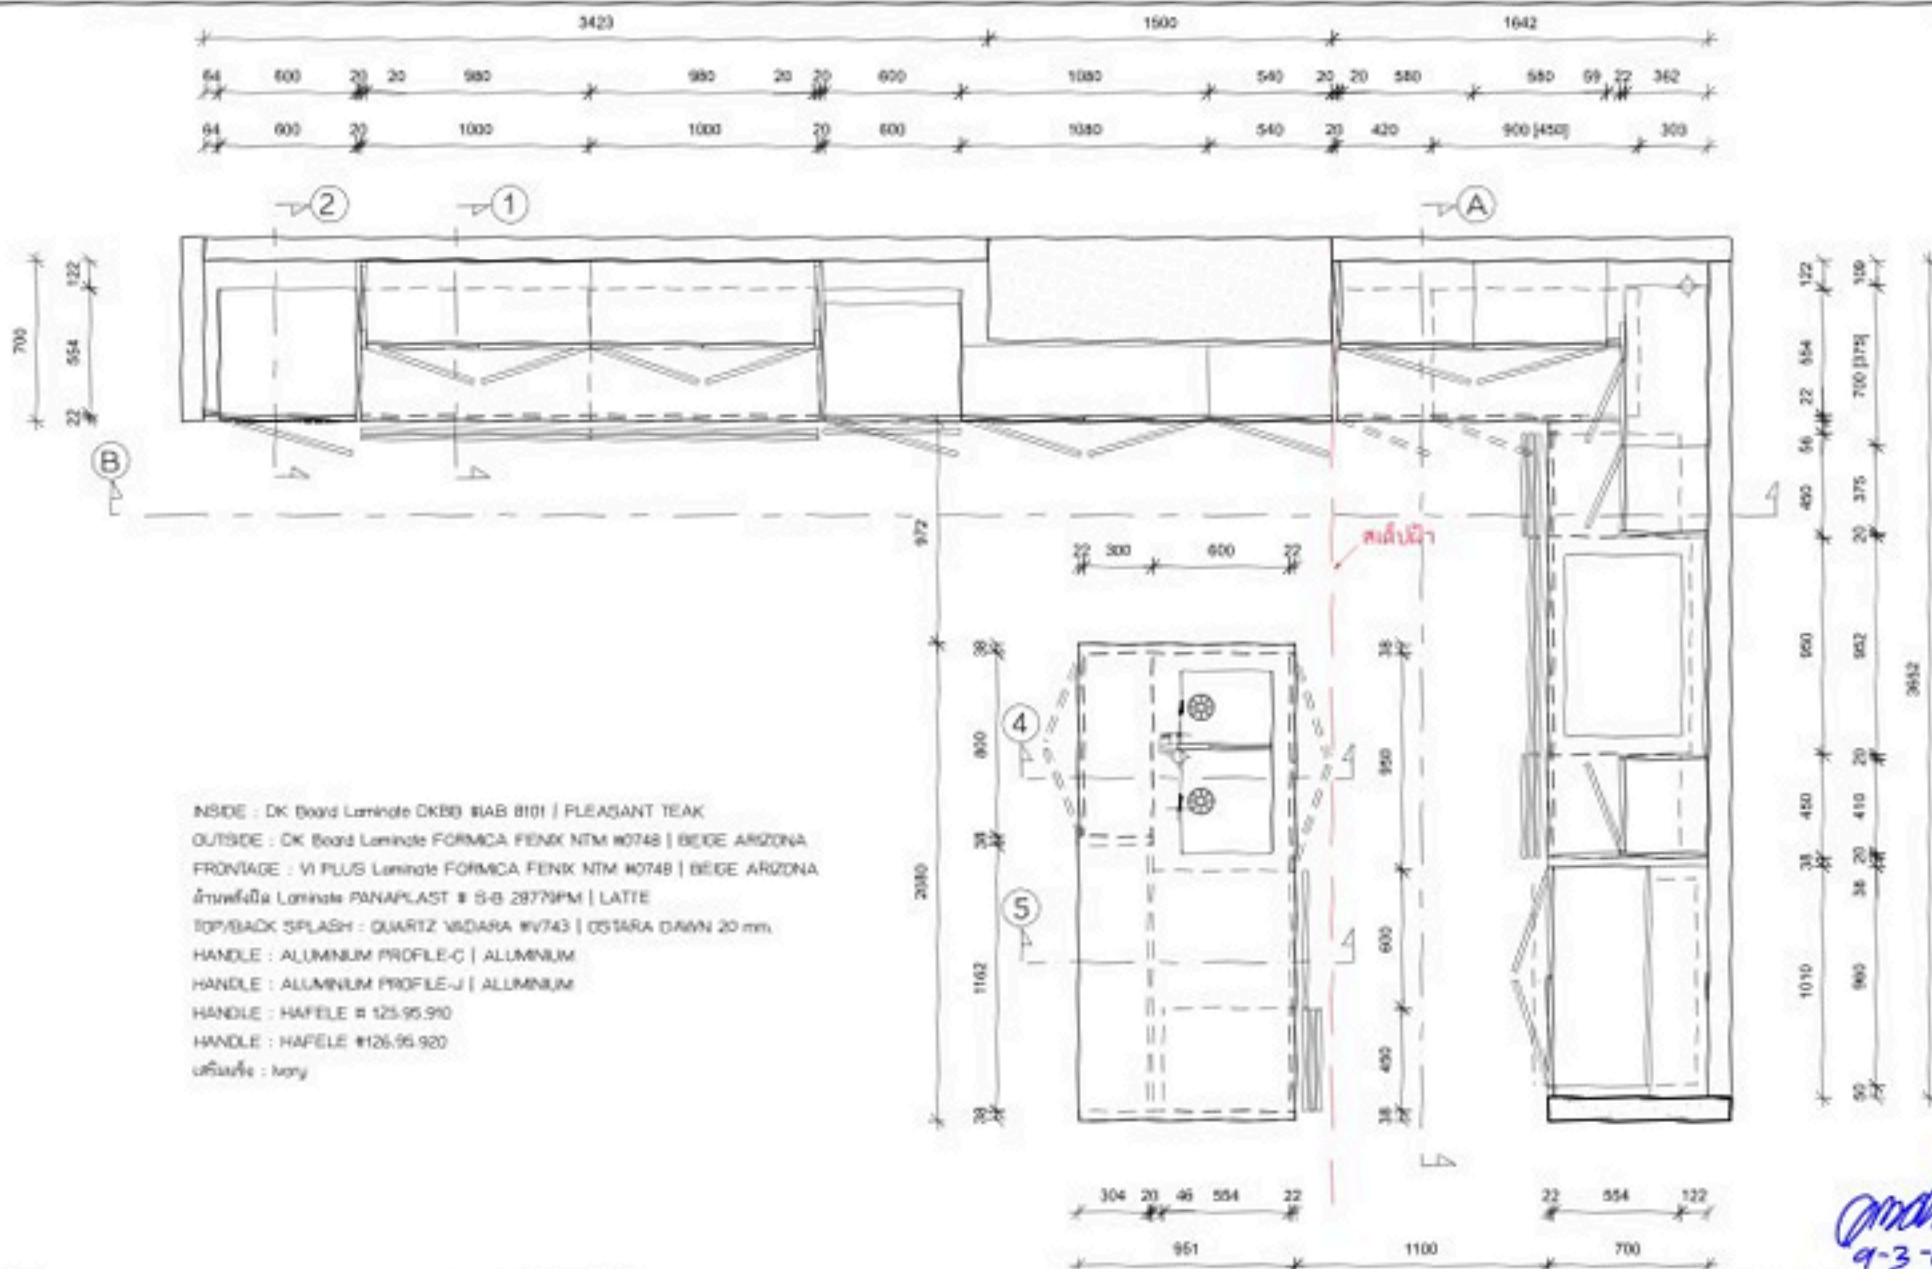

Dkbb

157 Praditmanutham Road
 Bangkok Bangkok 10240
 TEL 0-2515-1162 FAX 0-2515-1161
 09096 dkkorachok@dkb.co.th

Client : Ari 789

Address :

Province :-

Phone :

Design : Kitchen 3A

Series : Elegance Plus

Drawn by : บริษัท ดเคเคเคเคเค


Email :

View : Plan

Scale : 1:33

Date : 28/2/2569

Page : 01

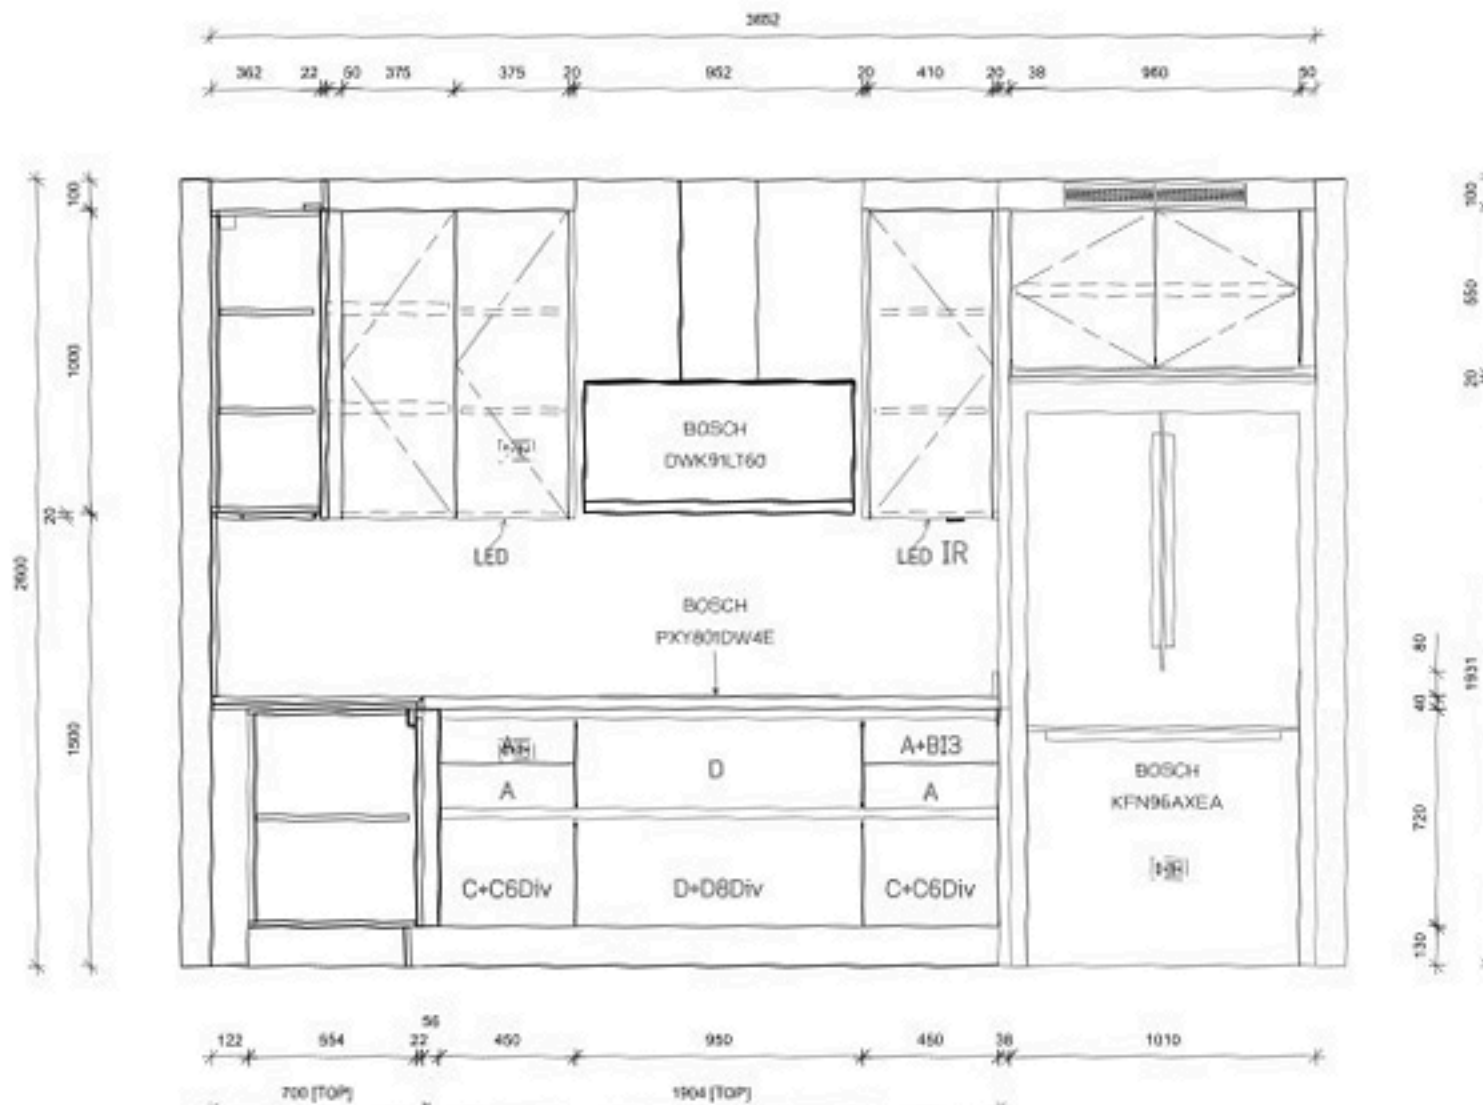

INSIDE : OK Board Laminat DKB #IAB 8101 | PLEASANT TEAK

OUTSIDE : OK Board Laminat FORMICA FENIX NTM #0748 | BEIGE ARIZONA

FRONTAGE : V PLUS Laminat FORMICA FENIX NTM #0748 | BEIGE ARIZONA

แผ่นพื้น Laminat PANAPLAST # S-B 28779PM | LATTE

TOP/BACK SPLASH : QUARTZ WADARA #V743 | OSTARA DAWN 20 mm.

HANDLE : ALUMINUM PROFILE-C | ALUMINUM

HANDLE : ALUMINUM PROFILE-J | ALUMINUM

HANDLE : HAFELE # 125.95.910

HANDLE : HAFELE #126.95.920

ไม้เท้า : Ivory

Dkbb

157 Praditmanutham Road
Bangkapi Bangkok 10240

TEL 0-2515-1182 FAX 0-2515-1181
WWW.dkbschedule.co.th

Client : ARI 789

Address :

Province :-

Phone :

Design : Kitchen 3A

Series : Elegance Plus

Drawn by : บริษัท ธรรมะธรรม

Email :


View : Elevation A

Scale : 1:25

Date : 28/2/2569

Page : 02

Handwritten signature and date:
9-3-69

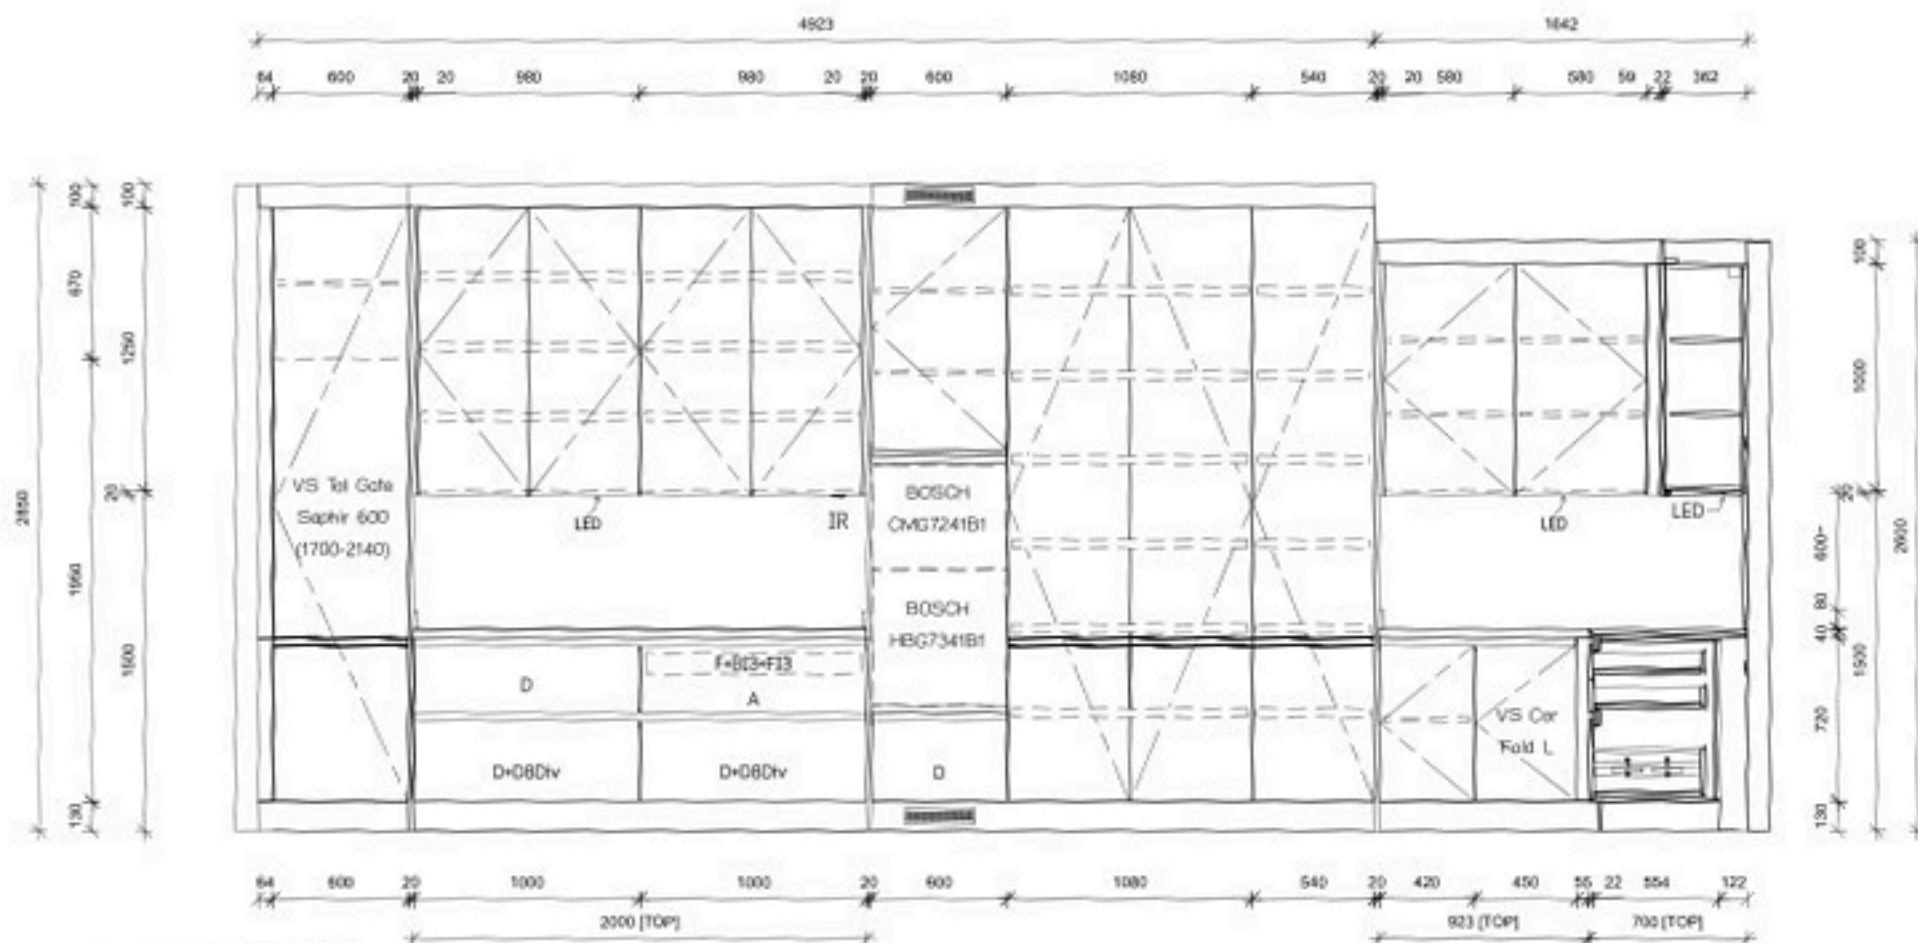

INSIDE : DK Board Laminat DKB #WB 8101 | PLEASANT TEAK
 OUTSIDE : DK Board Laminat FORMICA FENIX NTM #0748 | BEIGE ARIZONA
 FRONTAGE : VI PLUS Laminat FORMICA FENIX NTM #0748 | BEIGE ARIZONA
 Dinding Laminat PANAPLAST # S-B 28779PM | LATTE
 TOP/BACK SPLASH : QUARTZ WADARA #V743 | OSTARA DAWN 20 mm
 HANDLE : ALUMINUM PROFILE-C | ALUMINUM
 HANDLE : ALUMINUM PROFILE-J | ALUMINUM
 HANDLE : HAFELE # 125.95.910
 HANDLE : HAFELE #125.95.920
 Material : kayu

amh
 9-3-69

Dkbb

157 Praditmanutham Road
 Bangkok Bangkok 10240
 TEL 0-2515-1182 FAX 0-2515-1181
 WWW.dkbb.co.th

Client : Ari 789

Address :

Province :-

Phone :

Design : Kitchen 3A

Series : Elegance Plus

Drawn by : บริษัท ดีเคบี


Email :

View : Elevation B


Scale : 1:33.33

Date : 28/2/2569

Page : 03

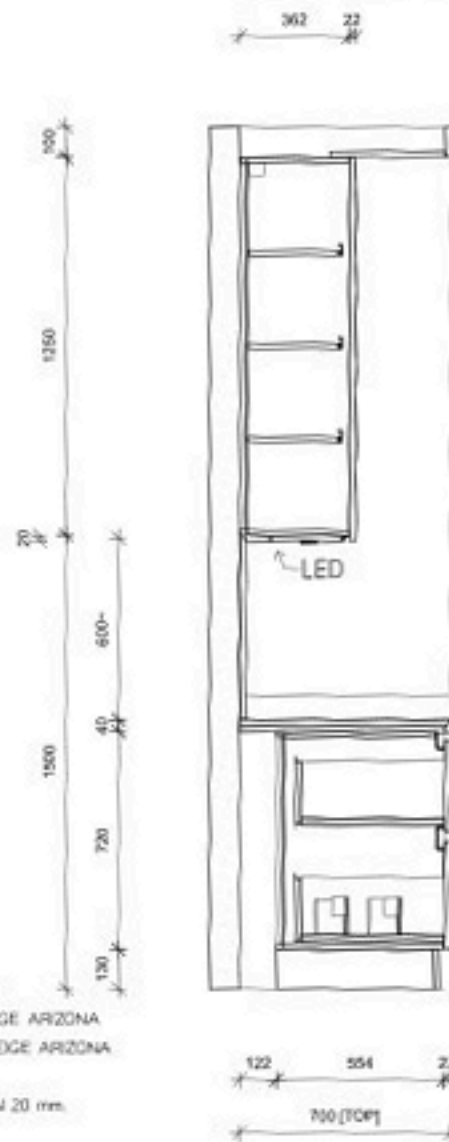

SECTION 1

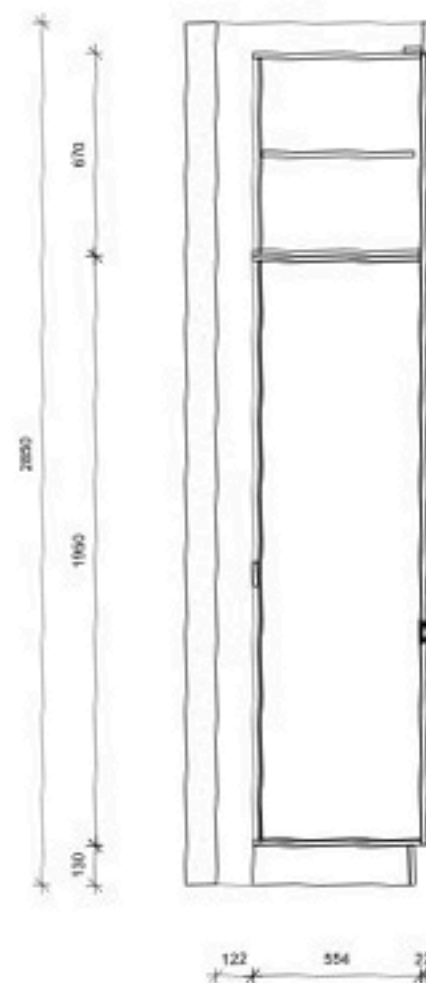

SECTION 2

INSIDE : DK Board Laminale DKB WAB 8101 | PLEASANT TEAK
 OUTSIDE : DK Board Laminale FORMICA FENIX NTM #0748 | BEGE ARIZONA
 FRONTAGE : VI PLUS Laminale FORMICA FENIX NTM #0748 | BEGE ARIZONA
 ฉากด้านหลัง Laminale PANAPLAST # S-B 28779PM | LATTE
 TOP/BACK SPLASH : QUARTZ WADARA #V743 | OSTARA DAWN 20 mm.
 HANDLE : ALUMINUM PROFILE-C | ALUMINUM
 HANDLE : ALUMINUM PROFILE-J | ALUMINUM
 HANDLE : HAFELE # 125.95.910
 HANDLE : HAFELE # 126.95.920
 วัสดุผิว : Ivory

Handwritten signature and date
 27-3-69

Dkbb

157 Praditmanutham Road
 Bangkok Bangkok 10240
 TEL 0-2515-1162 FAX 0-2515-1161
 09096 deconchoke.co.th

Client : Ari 789	Design : Kitchen 3A	View : Section 1,2
Address :	Series : Elegance Plus	Scale : 1:25
Province :-	Drawn by : บริษัท ดีเคบีไทย	Date : 28/2/2569
Phone :	Email :	Page : 04

INSIDE : DK Board Laminat DKB #IAB 8101 | PLEASANT TEAK

OUTSIDE : DK Board Laminat FORMICA FENIX NTM #0748 | BEIGE ARIZONA

FRONTAGE : VI PLUS Laminat FORMICA FENIX NTM #0748 | BEIGE ARIZONA

ชั้นวาง Laminat PANAPLAST # S-B 28779PM | LATTE

TOP/BACK SPLASH : QUARTZ VADARA #V743 | OSTARA DAWN 20 mm

HANDLE : ALUMINUM PROFILE-C | ALUMINUM

HANDLE : ALUMINUM PROFILE-J | ALUMINUM

HANDLE : HAFELE # 125.95.910

HANDLE : HAFELE #126.95.920



เครื่องครัว : hang



SECTION 4



SECTION 5

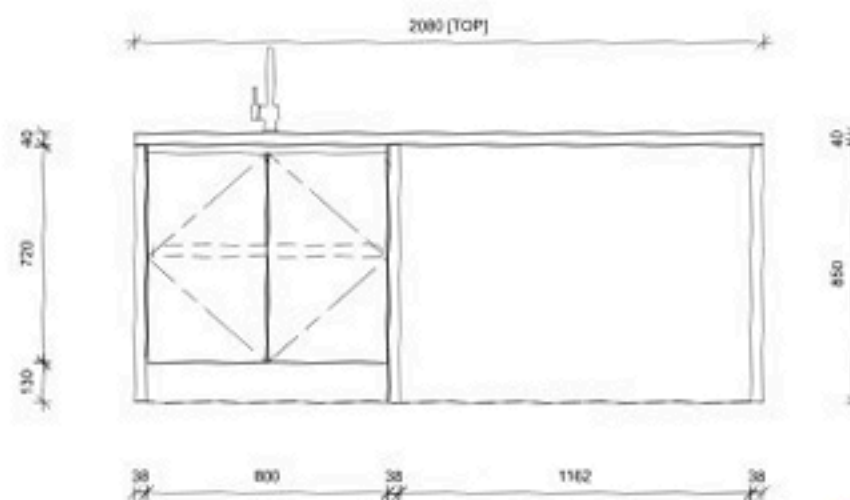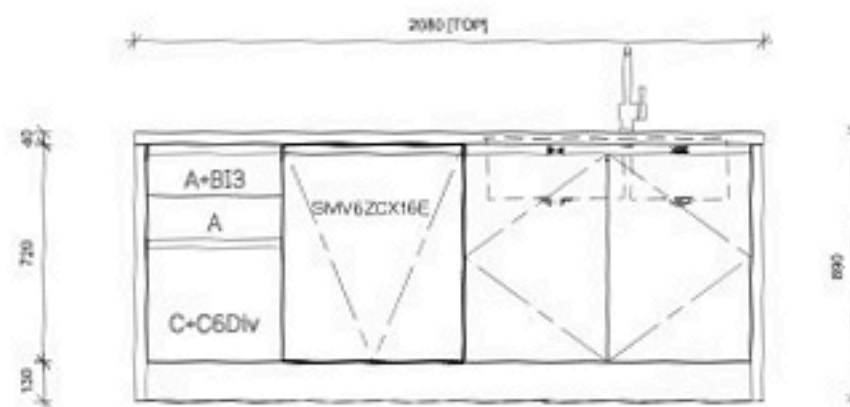

Qmoh
9-3-69

Dkbb

157 Praditmanutham Road
Bangkapi Bangkok 10240
TEL: 0-2615-1162 FAX: 0-2515-1161
WWW.DKBB.CO.TH

Client : Ari 789

Address :

Province :-

Phone :

Design : Kitchen 3A

Series : Elegance Plus

Drawn by : บริษัท ดีเคบีเอ

Email :

View : Island

Scale : 1:25

Date : 28/2/2569

Page : 05