


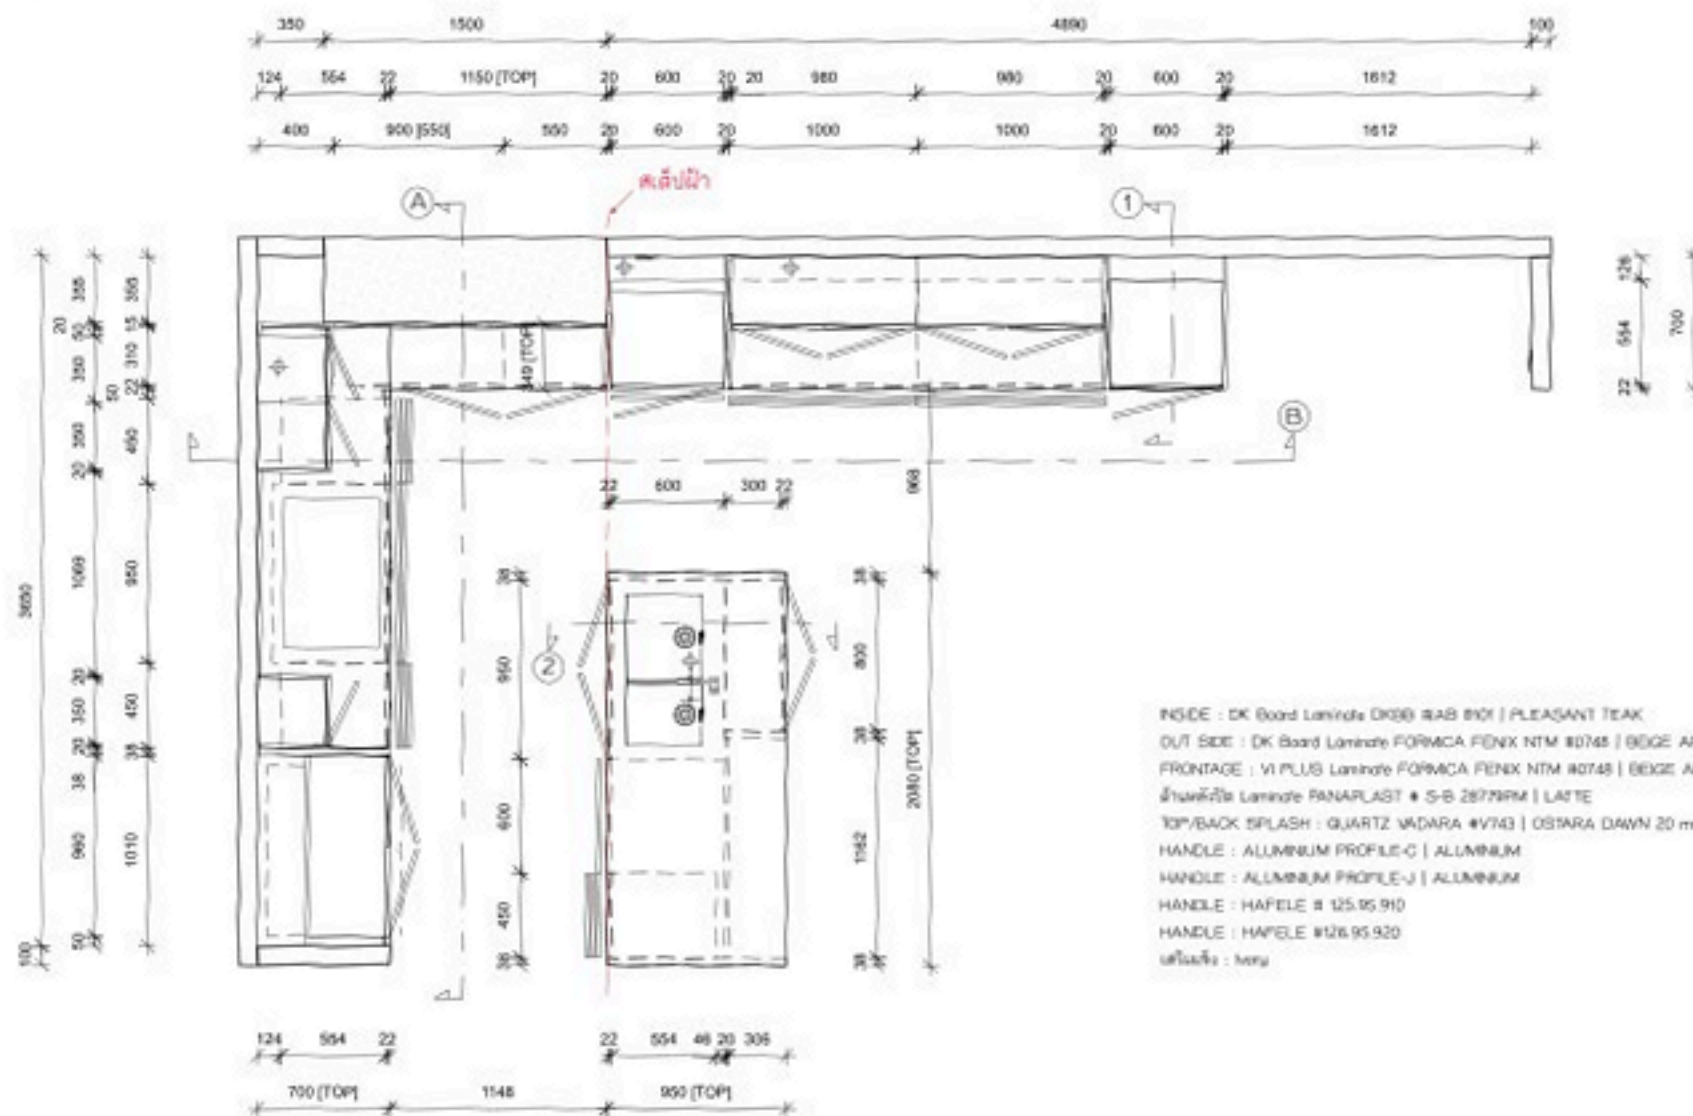

amdt
18-2-69

Dkbb

157 Praditmanutham Road
Bangkok Bangkok 10240
TEL: 0-2615-1162 FAX: 0-2515-1161
090961 dekarachon.co.th

Client : Ari 789

Address :

Province :-

Phone :

Design : Kitchen 3B

Series : Elegance Plus

Drawn by : วิศวกร สถาปนิก

Email :

View : Plan

Scale : 1:40

Date : 14/2/2569

Page : 01



SECTION 1

INSIDE : DK Board Laminate DKBB #48 8101 | PLEASANT TEAK
 OUT SIDE : DK Board Laminate FORMICA FENIX NTM #0748 | BEIGE ARIZONA
 FRONTAGE : W PLUS Laminate FORMICA FENIX NTM #0748 | BEIGE ARIZONA
 ฉนวนกันความร้อน Laminate PANAPLAST II S-B 28779PM | LATTE
 TOP/BACK SPLASH : QUARTZ VADARA #V743 | OSLARA DRAW 20 mm.

HANDLE : ALUMINUM PROFILE-C | ALUMINUM
 HANDLE : ALUMINUM PROFILE-J | ALUMINUM
 HANDLE : HAFELE H 125.95.910
 HANDLE : HAFELE H126.95.920
 วัสดุเคลือบ : Ivory

Amich
 18-2-69

Dkbb

157 Praditmanutham Road
 Bangkok Bangkok 10240
 TEL: 0-2515-1182 FAX: 0-2515-1181
 WWW.DKBKCHOCHE.CO.TH

Client : Ari 789

Address :

Province :-

Phone :

Design : Kitchen 3B

Series : Elegance Plus

Drawn by : บริษัท ดเคบีเค จำกัด


Email :

View : Elevation A , Section 1

Scale : 1:30

Date : 14/2/2569

Page : 02

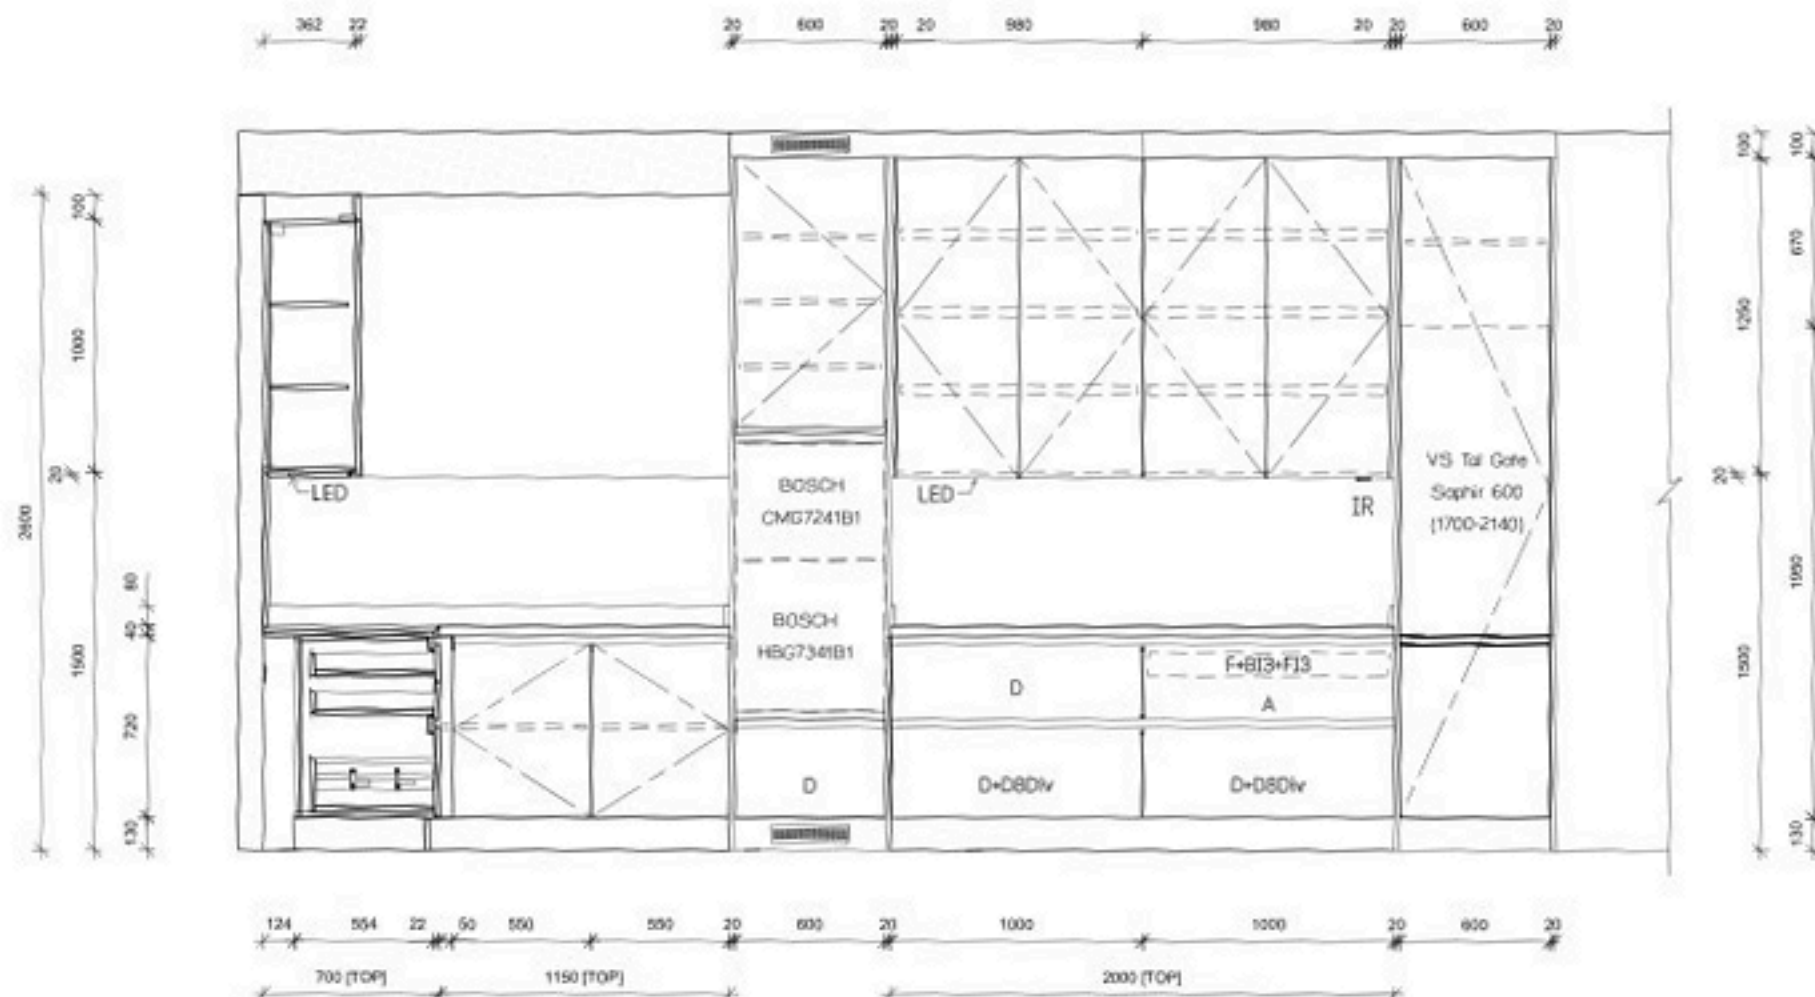

INSIDE : DK Board Laminate OK99 RAB 8101 | PLEASANT TEAK
 OUT SIDE : DK Board Laminate FORMICA PENIX NTM #0748 | EDGE ARIZONA
 FRONTAGE : VI PLUS Laminate FORMICA PENIX NTM #0748 | EDGE ARIZONA
 Handle/Dia Laminate HANAPLAST # S-B 28779PM | LATTE
 TOP/BACK SPLASH : QUARTZ WDARA #V743 | OSTARA DAWN 20 mm

HANDLE : ALUMINUM PROFILE-C | ALUMINUM
 HANDLE : ALUMINUM PROFILE-J | ALUMINUM
 HANDLE : HAFELE # 125.95.910
 HANDLE : HAFELE # 126.95.920
 HANAPLAST : Ivory

Handwritten signature
 18-2-69

Dkbb

157 Praditmanutham Road
 Bangkok Bangkok 10240
 TEL: 0-2515-1182 FAX: 0-2515-1181
 E-MAIL: dkbs@dkbb.co.th

Client : ARI 789

Address :

Province :-

Phone :

Design : Kitchen 3B

Series : Elegance Plus

Drawn by : น.วิรัตน์ อภินันท์



Email :

View : Elevation B

Scale : 1:30

Date : 14/2/2569

Page : 03

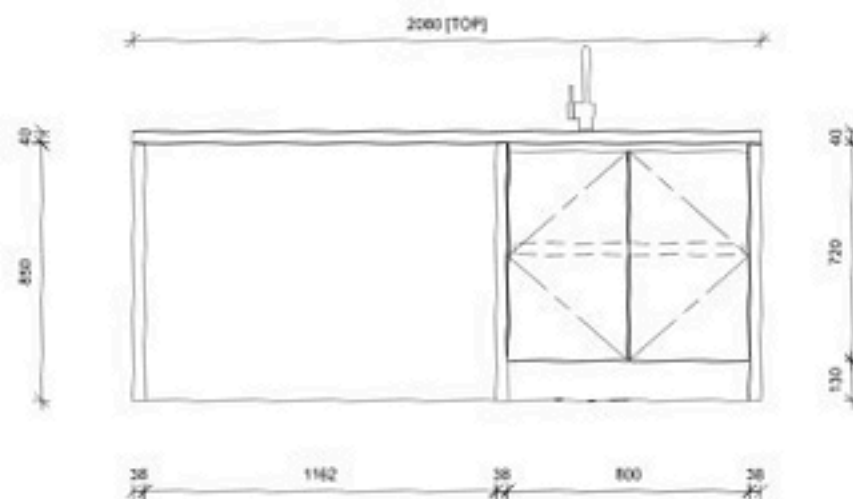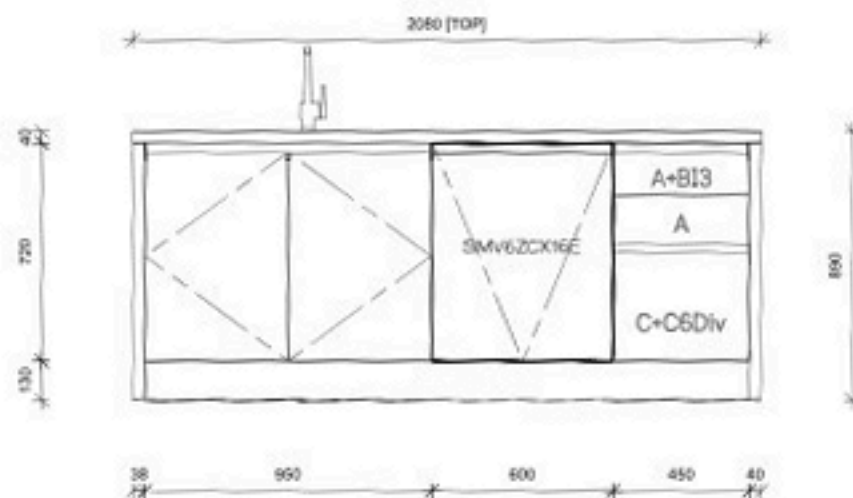

INSIDE : DK Board Laminat DKB #WAB 8101 | PLEASANT TEAK
 OUT SIDE : DK Board Laminat FORMICA FENIX NTM 80748 | EDGE ARIZONA
 FRONTAGE : VI PLUS Laminat FORMICA FENIX NTM 80748 | EDGE ARIZONA
 Island Laminat PANAPLAST # S-B 28779PM | LATTE
 TOP/BACK SPLASH : QUARTZ VADARA #V743 | OSTARA DAWN 20 ml.
 HANDLE : ALUMINUM PROFILE-C | ALUMINUM
 HANDLE : ALUMINUM PROFILE-J | ALUMINUM
 HANDLE : HAFELE # 125.95.910
 HANDLE : HAFELE #126.95.920
 Material : Ivory



SECTION 2

amola
 18-2-69

Dkbb

157 Praditmanutham Road
 Bangkok Bangkok 10240
 TEL 0-2515-1142 FAX 0-2515-1181
 WWW.dkbb.com.th

Client : Ari 789

Address :

Province :-

Phone :

Design : Kitchen 3B

Series : Elegance Plus

Drawn by : บริษัท ดีเคบี

Email :

View : Island

Scale : 1:25

Date : 14/2/2569

Page : 04