












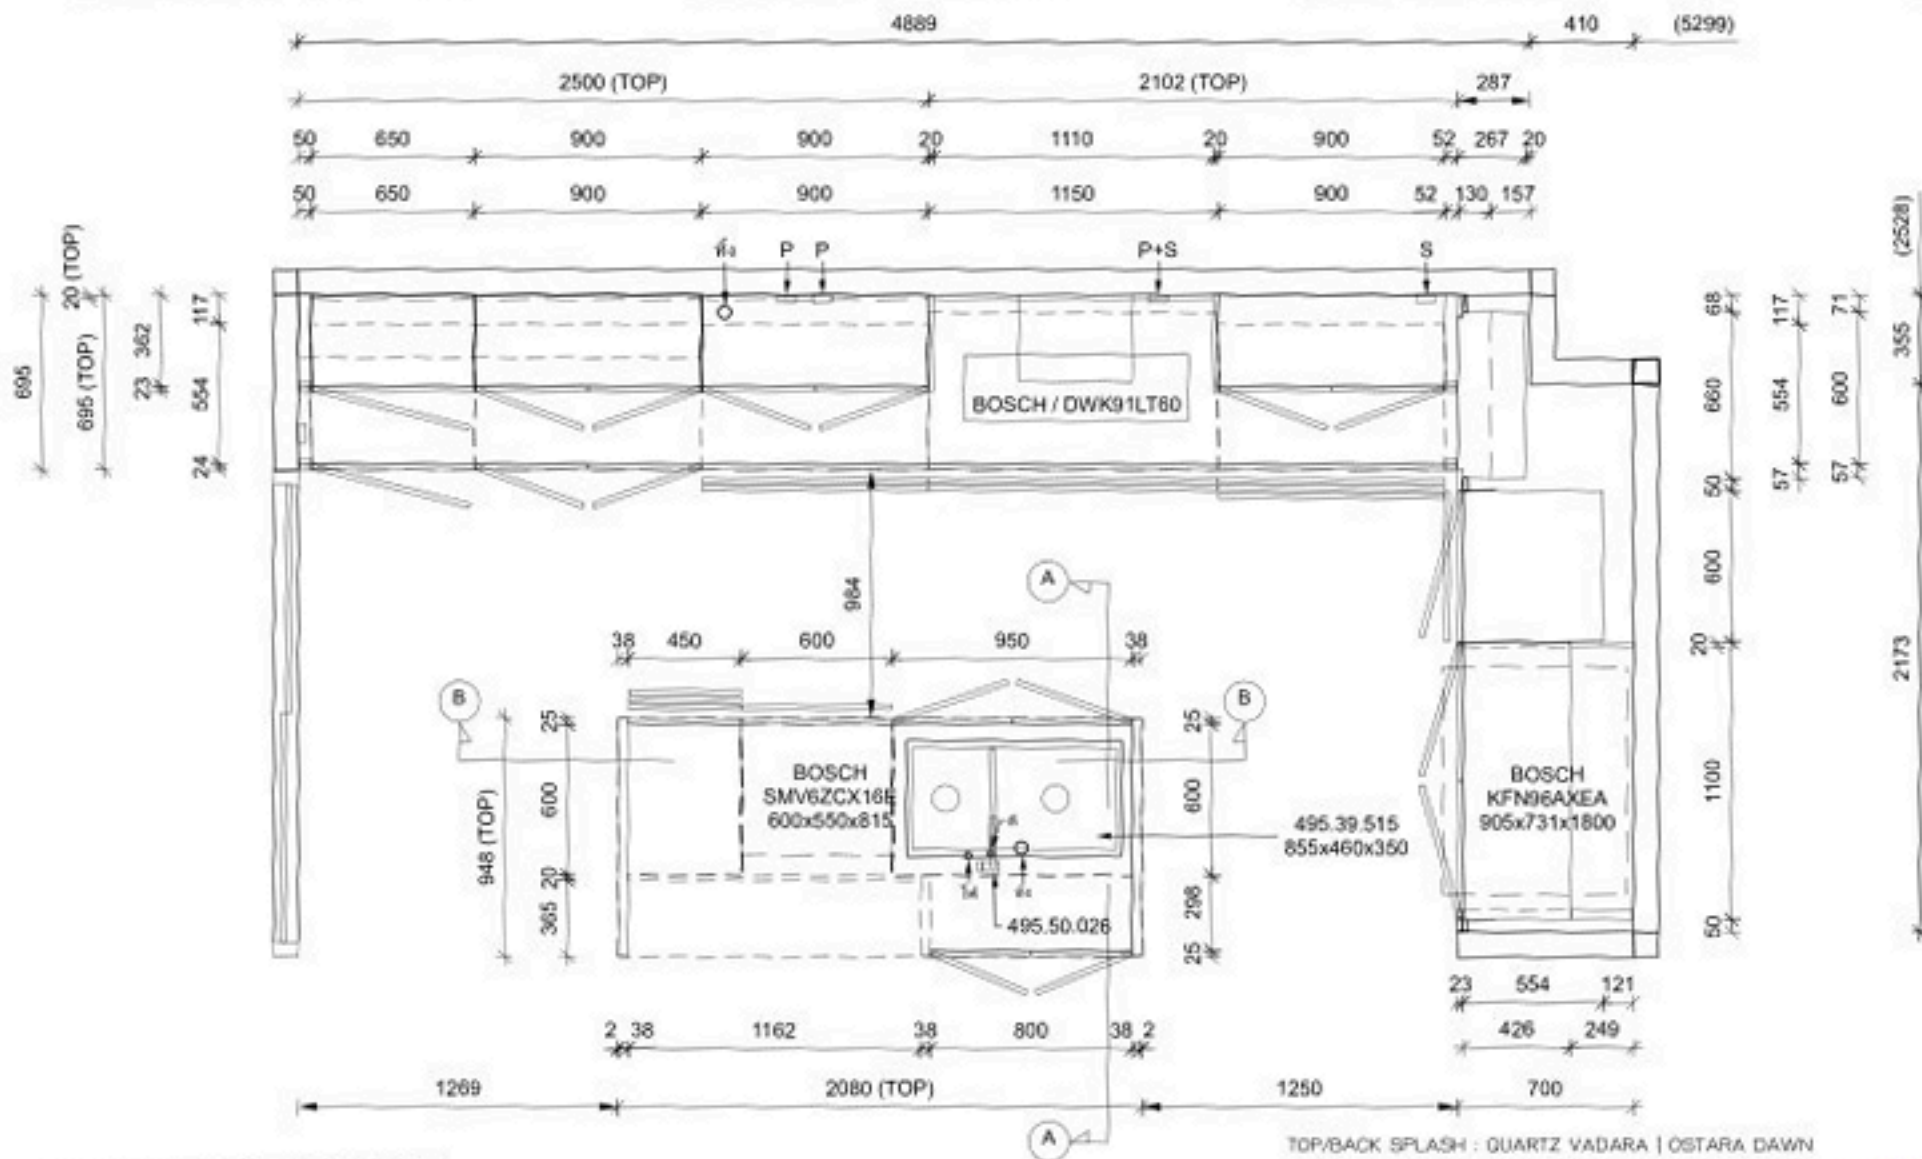

INSIDE : ARBORITE #IAB 8101 | PLEASANT TEAK

OUT SIDE : FORMICA FENIX NTM #0748 | BEIGE ARIZONA

FRONTAGE : FORMICA FENIX NTM #0748 | BEIGE ARIZONA, แผ่นหลังเคาน์เตอร์ PANAPLAST #S-B 28779PM | LATTE

TOP/BACK SPLASH : QUARTZ VADARA | OSTARA DAWN

HANDLE : ALUMINUM PROFILE-C | ALUMINUM

HANDLE : ALUMINUM PROFILE-J | ALUMINUM

เคาน์เตอร์ : DKP #1907 | Ivory

Handwritten signature
22-12-68

Dkbb

157 Praditmanultham Road
Bangkapi Bangkok 10240

TEL 0-2515-1182 FAX 0-2515-1181
www.dkbb.co.th

Client : ARI 789 PROJECT

Address :

Province :

Phone :

Design : KITCHEN

Series : ELEGANCE PLUS

Drawn by : Jirayu


Email :

View : PLAN

Scale : 1:30

Date : 22/12/2568

Page : 1-5

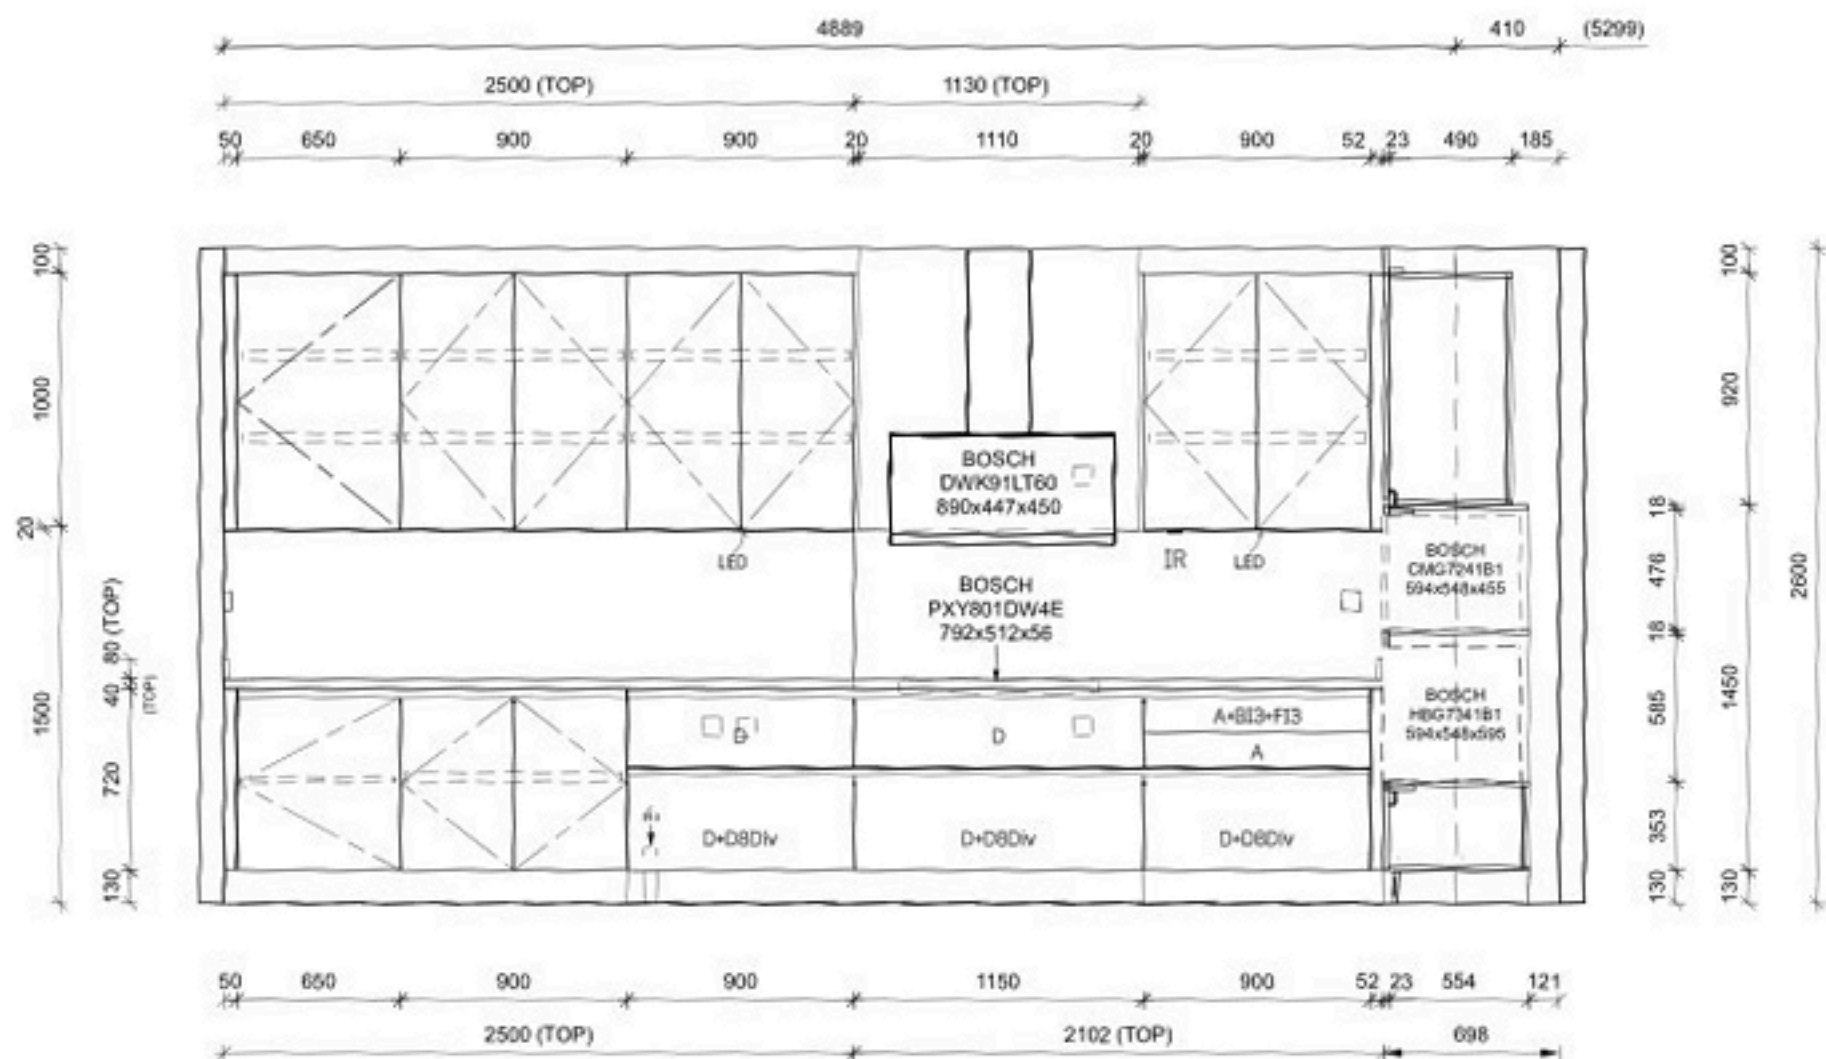

INSIDE : ARBORITE IIIAB 8101 | PLEASANT TEAK

OUT SIDE : FORMICA FENIX NTM #0748 | BEIGE ARIZONA

FRONTAGE : FORMICA FENIX NTM #0748 | BEIGE ARIZONA, ส่วนหลังปิดทึบ PANAPLAST #S-B 28779PM | LATTE

TOP/BACK SPLASH : QUARTZ VADARA | OSTARA DAWN

HANDLE : ALUMINIUM PROFILE-C | ALUMINIUM

HANDLE : ALUMINIUM PROFILE-J | ALUMINIUM

เคาน์เตอร์ : DKP #1907 | Ivory

Handwritten signature
22-12-68

Dkbb

157 Praditmanultham Road
Bangkapi Bangkok 10240

TEL 0-2515-1162 FAX 0-2515-1161
www.dkbbthailand.co.th

Client :ARI 789 PROJECT

Address :

Province :

Phone :

Design :KITCHEN

Series :ELEGANCE PLUS

Drawn by :Jirayu


Email :

View : ELEVATION A

Scale : 1:30

Date : 22/12/2568

Page : 2-5

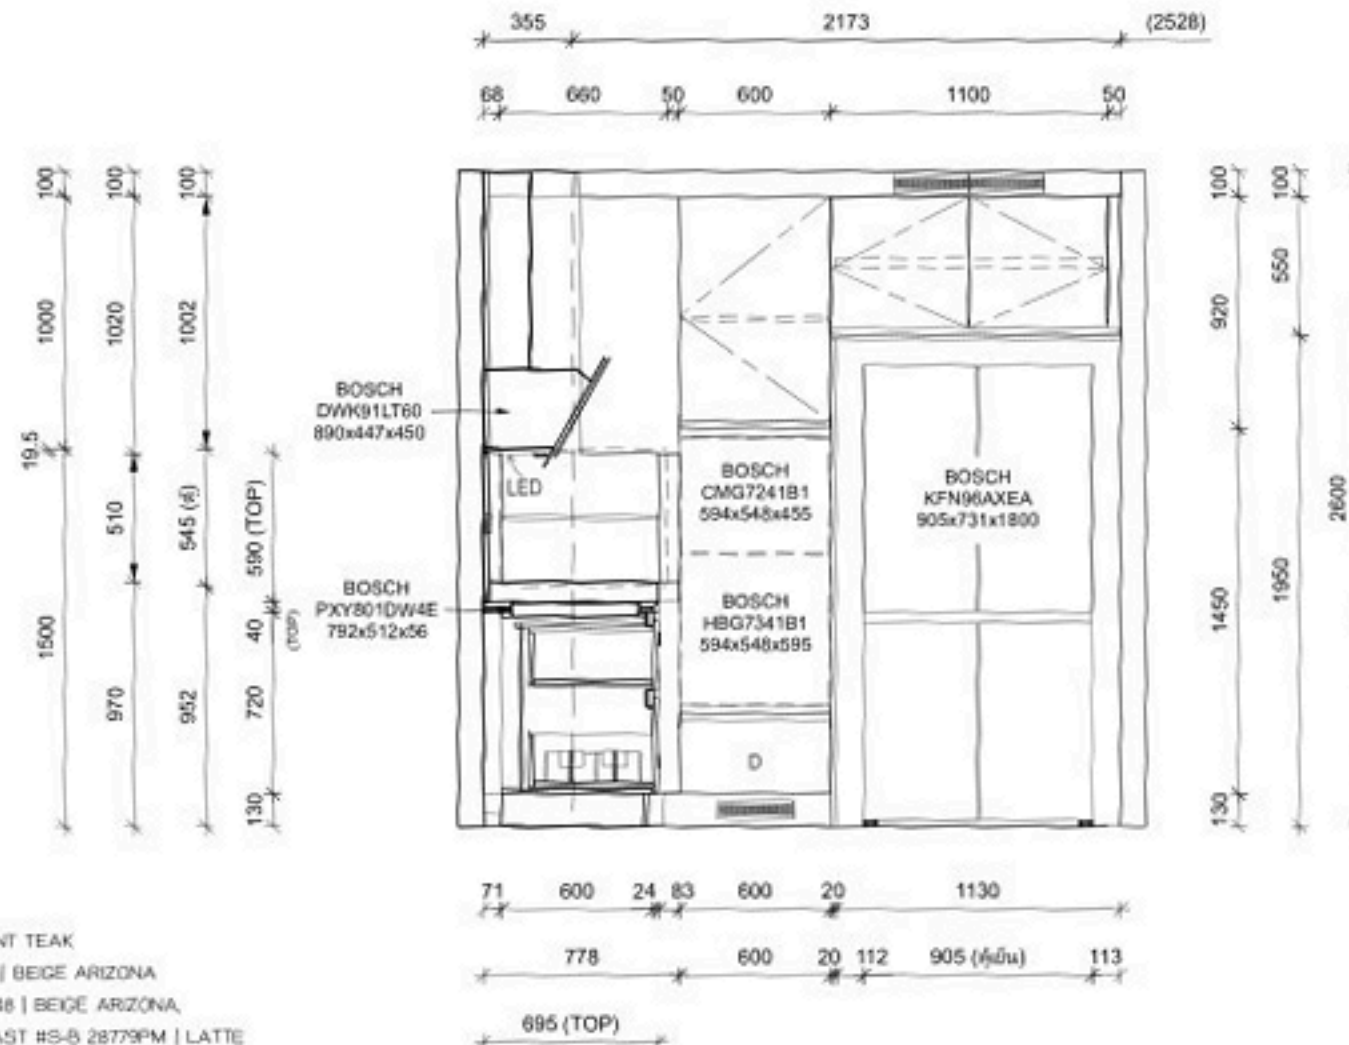

INSIDE : ARBORITE #IAB 8101 | PLEASANT TEAK
 OUT SIDE : FORMICA FENIX NTM #0748 | BEIGE ARIZONA
 FRONTAGE : FORMICA FENIX NTM #0748 | BEIGE ARIZONA
 ฝาหลังตู้บนตู้ PANAPLAST HS-B 28779PM | LATTE
 TOP/BACK SPLASH : QUARTZ VADARA | OSTARA DAWN
 HANDLE : ALUMINUM PROFILE-C | ALUMINUM
 HANDLE : ALUMINUM PROFILE-J | ALUMINUM
 เครื่องใช้ : DKP #1907 | Ivory

22-12-68

Dkbb

157 Praditmanulham Road
 Bangkok Bangkok 10240
 TEL: 0-2515-1182 FAX: 0-2515-1181
 WWW.dkbb.co.th

Client :ARI 789 PROJECT

Address :

Province :

Phone :

Design :KITCHEN

Series :ELEGANCE PLUS

Drawn by :Jirayu




Email :

View : ELEVATION B

Scale : 1:30

Date : 22/12/2568

Page : 3-5

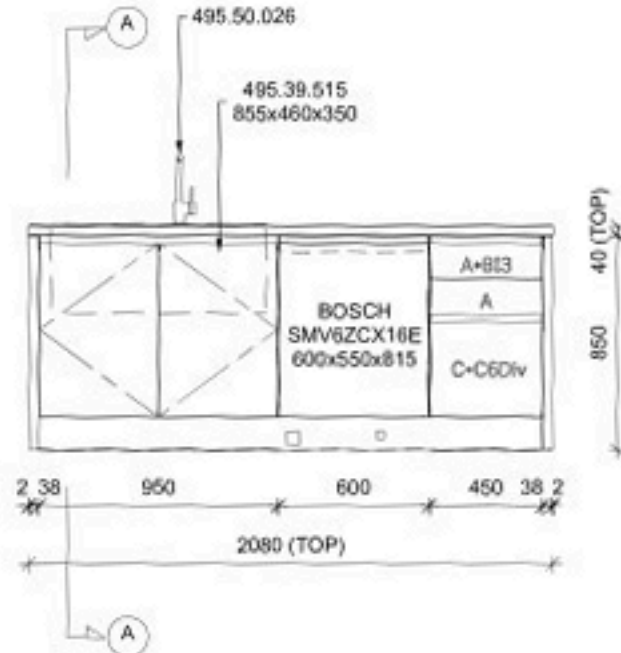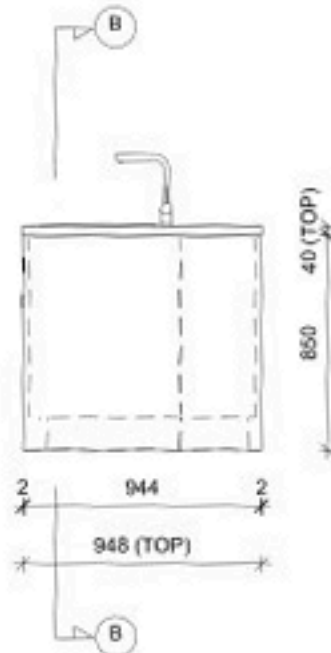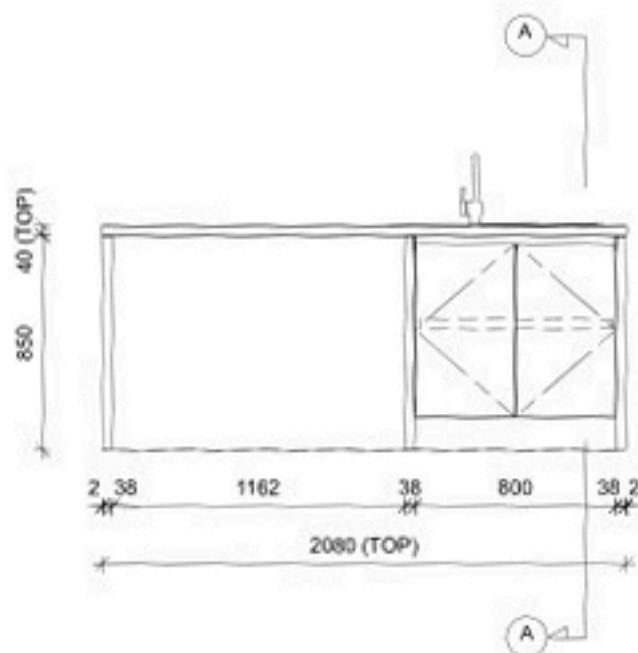

INSIDE : ARBORITE #IAB 8101 | PLEASANT TEAK
 OUT SIDE : FORMICA FENIX NTM #0748 | BEIGE ARIZONA
 FRONTAGE : FORMICA FENIX NTM #0748 | BEIGE ARIZONA
 ด้านหลังติดแผ่น PANAPLAST #S-B 28779PM | LATTE
 TOP/BACK SPLASH : QUARTZ VADARA | OSTARA DAWN
 HANDLE : ALUMINUM PROFILE-C | ALUMINUM
 HANDLE : ALUMINUM PROFILE-J | ALUMINUM
 เฟอร์นิเจอร์ : DKP #1907 | Ivory

Amah
 22-12-68

Dkbb

157 Praditmanutham Road
 Bangkok Bangkok 10240
 TEL 0-2515-1152 FAX 0-2515-1151
 WWW.dkbbthailand.co.th

Client :ARI 789 PROJECT

Address :

Province :

Phone :

Design :KITCHEN (ISLAND)

Series :ELEGANCE PLUS

Drawn by :Jirayu


Email :

View : ELEVATION A,B ,C

Scale : 1:30

Date : 22/12/2568

Page : 4-5

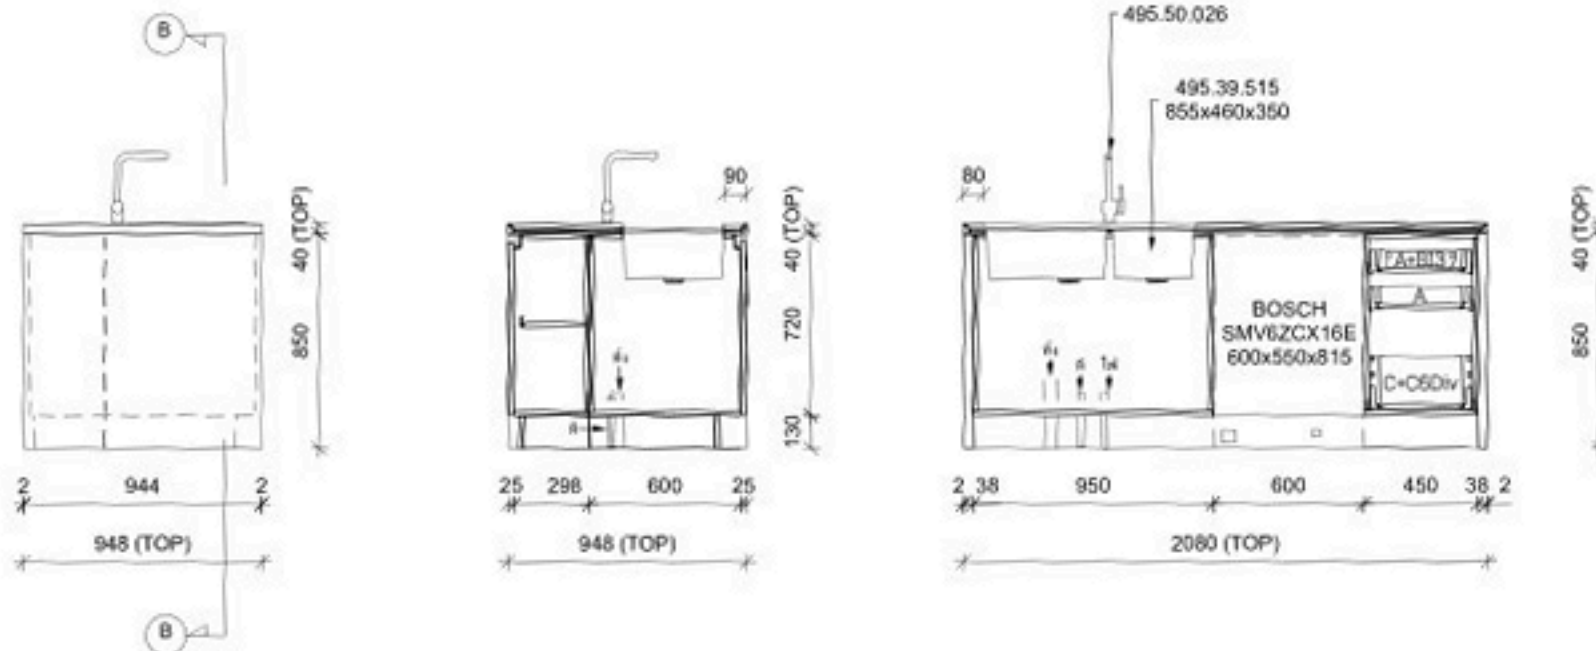

INSIDE : ARBORTE #IAB 8101 | PLEASANT TEAK
 OUT SIDE : FORMICA FENIX NTM #0748 | BEIGE ARIZONA
 FRONTAGE : FORMICA FENIX NTM #0748 | BEIGE ARIZONA
 ฝาหลัง/ลิ้นชักภายใน PANAPLAST #S-B 28779PM | LATTE
 TOP/BACK SPLASH : QUARTZ VADARA | OSTARA DAWN
 HANDLE : ALUMINUM PROFILE-C | ALUMINUM
 HANDLE : ALUMINUM PROFILE-J | ALUMINUM
 เฟอร์นิเจอร์ : DKP #1907 | Ivory

22-12-58

Dkbb

157 Praditmanulham Road
 Bangkok Bangkok 10240
 TEL: 0-2515-1182 FAX: 0-2515-1181
 WWW.dkbb.co.th

Client :ARI 789 PROJECT

Address :

Province :

Phone :

Design :KITCHEN (ISLAND)

Series :ELEGANCE PLUS

Drawn by :Jirayu

Email :

View : ELEVATION D ,SECTION A ,B

Scale : 1:30

Date : 22/12/2568

Page : 5-5



โบสถ์เฟอร์นิเจอร์ บริษัท อารี789 ดีเวลลอปเม้นท์ จำกัด
เลขที่ 10/1 ซอยพหลโยธิน 5 ถนนพหลโยธิน แขวงพญาไท เขตพญาไท
กรุงเทพมหานคร 10400 โทร : 044-110218
เลขประจำตัวผู้เสียภาษีอากร 0105565012642 (สำนักงานใหญ่)

22 ธันวาคม 2568

รายการเพิ่มลดใน KITCHEN และ ISLAND

1	เพิ่ม : ตู้บน รุ่น ELEGANCE PLUS (กันปลวกกันน้ำรับประกัน 10 ปี) ขนาด 0.385 X 1.58 X 1.00 ม.	63,200.00
2	เพิ่ม : อุปกรณ์ภายในตู้ใน KITCHEN	29,280.00
3	เพิ่ม : อุปกรณ์ภายในตู้ใน ISLAND	2,100.00
4	หักคืน : ชั้นวางของ ขนาด 0.25 X 1.58 ม. จำนวน 2 ชั้น	-11,000.00
5	หักคืน : หิน QUARTZ VADARA # V743 (OSTARA DAWN) ด้านหลังชั้นวางของ	-14,843.00
รวม		68,737.00
ส่วนลด 15%		-10,311.00
ยอดรวม หลังหักส่วนลด		58,426.00
6	หักคืน : ไฟ LED ได้ชั้นวางของ	-1,580.00
รวมเงิน Ex. Vat		56,846.00
VAT 7%		3,979.22
ยอดสุทธิ		60,825.22

- หมายเหตุ - ก่อนเซ็นสั่งซื้อสินค้า กรุณาตรวจสอบแบบและรายละเอียดต่างๆ ให้ครบถ้วน
เนื่องจากการสั่งผลิตเฉพาะงาน
- ไฟแสงสว่าง, สีของไฟ LED, ตำแหน่งปลั๊กใช้งาน, กุญแจล็อคต่างๆ ไม่สามารถเพิ่มภายหลังได้
กรุณาตรวจสอบก่อนว่ามีครบตามต้องการหรือไม่
- หลังจากสั่งซื้อสินค้าแล้ว ทางบริษัทฯ ขอสงวนสิทธิ์ในการแก้ไขใดๆทั้งสิ้น

บริษัท เดคคอร์ส ชอยส์ จำกัด

157 ซ.โยธินพัฒนา ถ.ประดิษฐ์มนูธรรม แขวงคลองจั่น เขตบางกะปิ กรุงเทพฯ 10240

Tel : 0 2515 1162 Fax : 0 2515 1161 Call Center : 08-1954-5550

E-mail : decorchoice@gmail.com www.decorchoice.co.th