


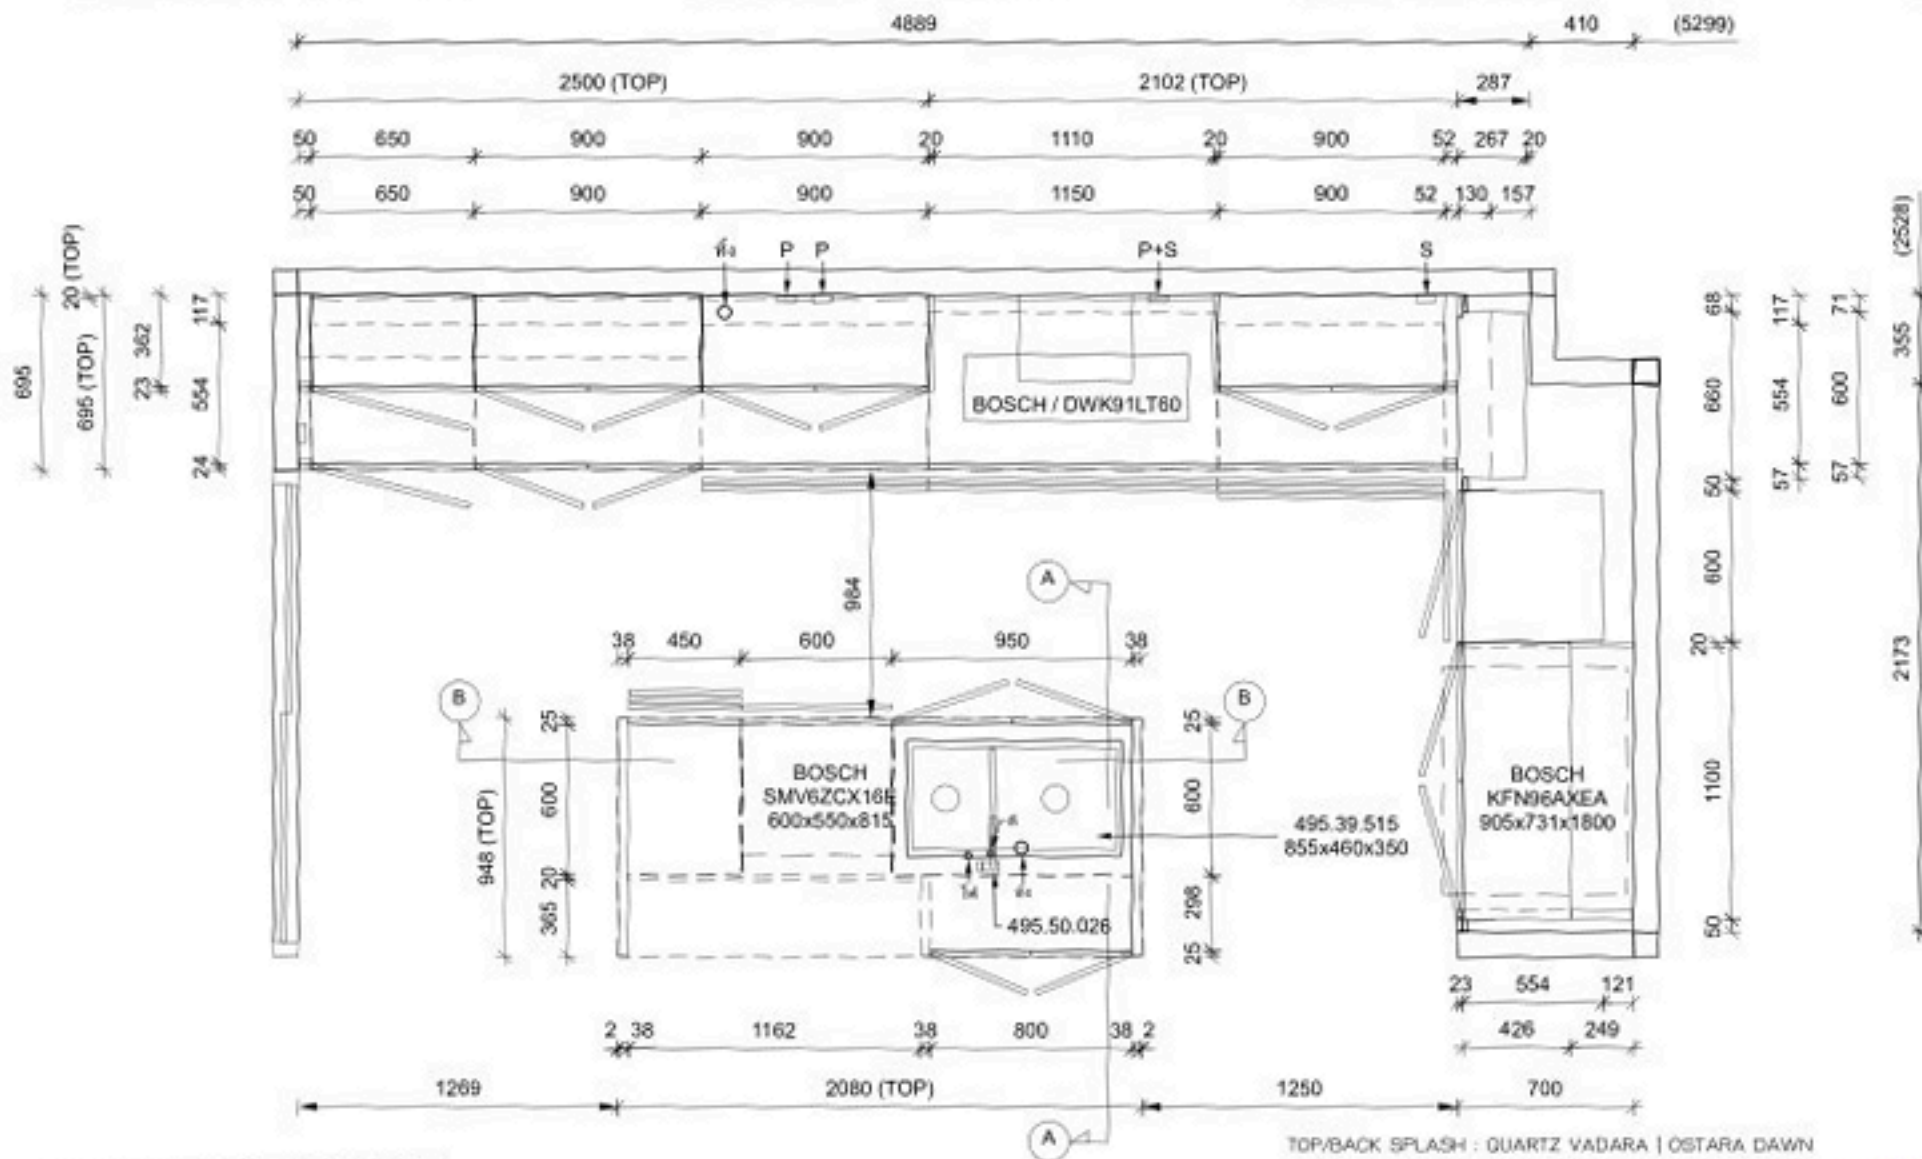

INSIDE : ARBORITE #IAB 8101 | PLEASANT TEAK

OUT SIDE : FORMICA FENIX NTM #0748 | BEIGE ARIZONA

FRONTAGE : FORMICA FENIX NTM #0748 | BEIGE ARIZONA, แผ่นหลังเคาน์เตอร์ PANAPLAST #S-B 28779PM | LATTE

TOP/BACK SPLASH : QUARTZ VADARA | OSTARA DAWN

HANDLE : ALUMINUM PROFILE-C | ALUMINUM

HANDLE : ALUMINUM PROFILE-J | ALUMINUM

เคาน์เตอร์ : DKP #1907 | Ivory

Handwritten signature
22-12-68

Dkbb

157 Praditmanultham Road
Bangkapi Bangkok 10240

TEL 0-2515-1182 FAX 0-2515-1181
www.dkbb.co.th

Client : ARI 789 PROJECT

Address :

Province :

Phone :

Design : KITCHEN

Series : ELEGANCE PLUS

Drawn by : Jirayu


Email :

View : PLAN

Scale : 1:30

Date : 22/12/2568

Page : 1-5

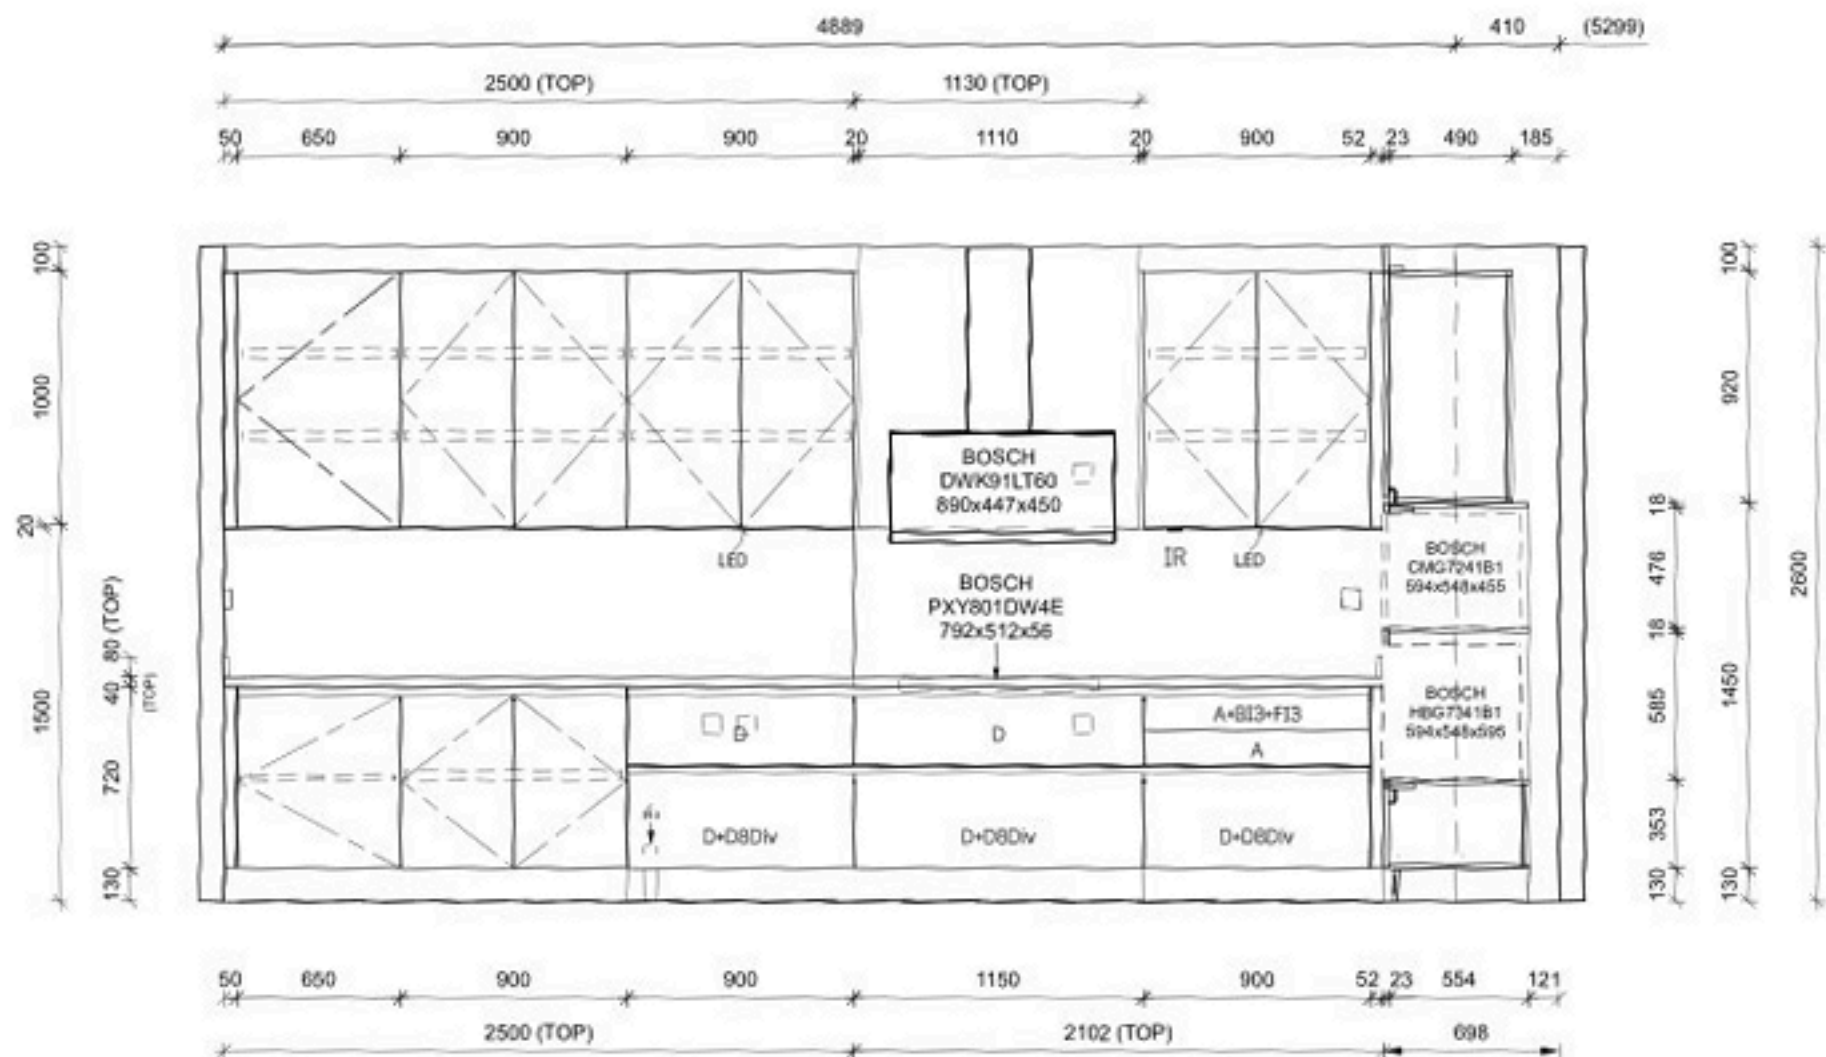

INSIDE : ARBORITE IIIAB 8101 | PLEASANT TEAK

OUT SIDE : FORMICA FENIX NTM #0748 | BEIGE ARIZONA

FRONTAGE : FORMICA FENIX NTM #0748 | BEIGE ARIZONA, ส่วนหลังปิดทึบ PANAPLAST #S-B 28779PM | LATTE

TOP/BACK SPLASH : QUARTZ VADARA | OSTARA DAWN

HANDLE : ALUMINIUM PROFILE-C | ALUMINIUM

HANDLE : ALUMINIUM PROFILE-J | ALUMINIUM

เคาน์เตอร์ : DKP #1907 | Ivory

Handwritten signature
22-12-68

Dkbb

157 Praditmanutham Road
Bangkok Bangkok 10240

TEL 0-2515-1152 FAX 0-2515-1151
www.dkbb.co.th

Client :ARI 789 PROJECT

Address :

Province :

Phone :

Design :KITCHEN

Series :ELEGANCE PLUS

Drawn by :Jirayu


Email :

View : ELEVATION A

Scale : 1:30

Date : 22/12/2568

Page : 2-5

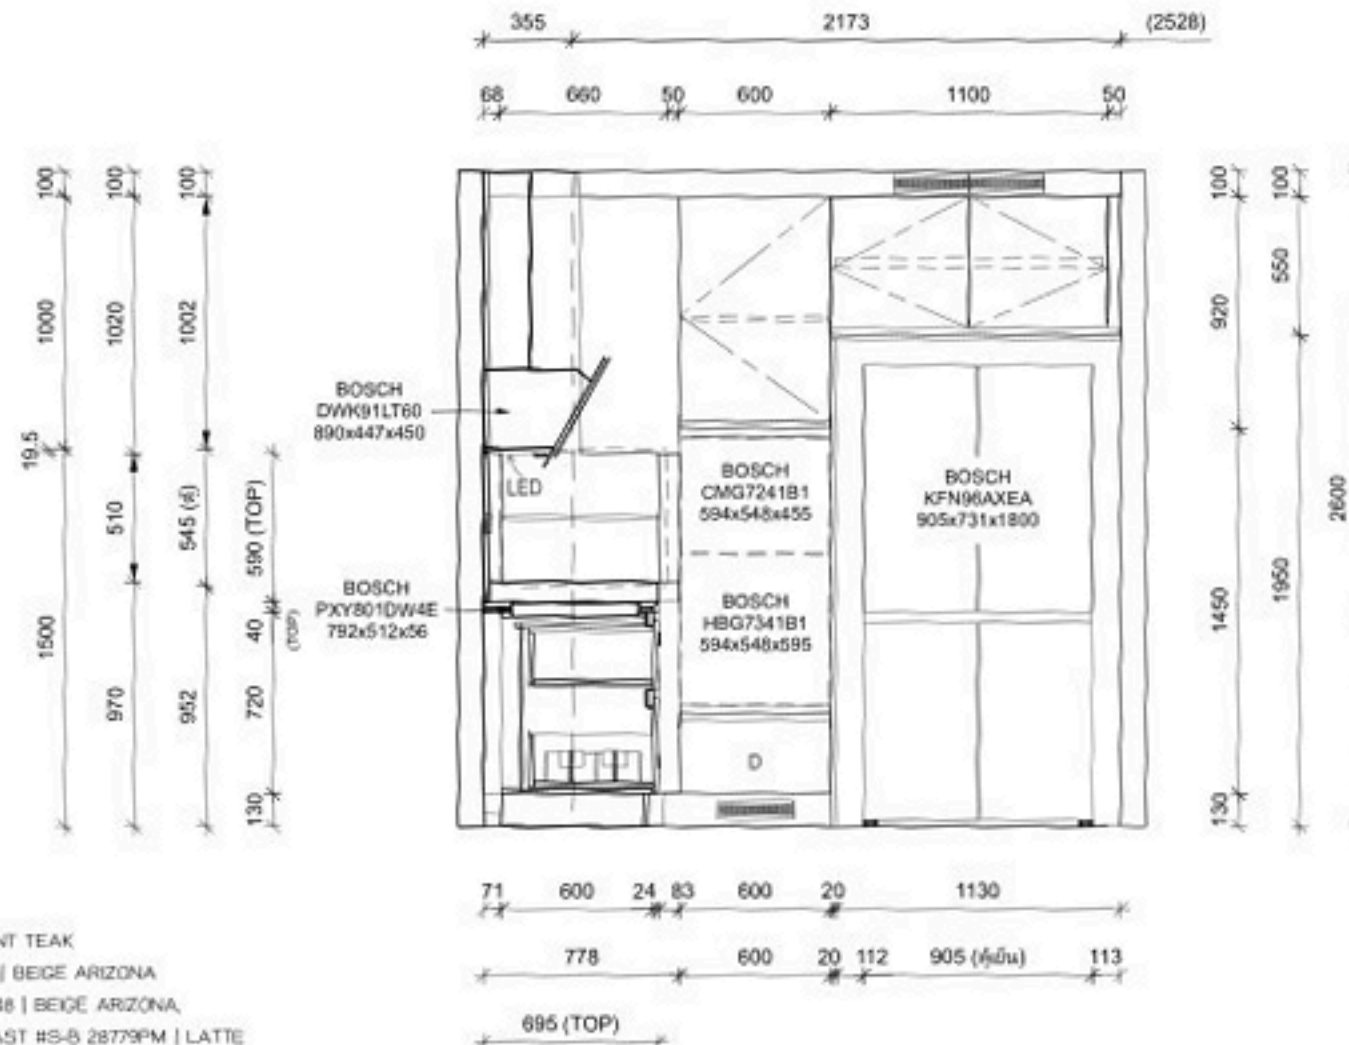

INSIDE : ARBORITE #IAB 8101 | PLEASANT TEAK
 OUT SIDE : FORMICA FENIX NTM #0748 | BEIGE ARIZONA
 FRONTAGE : FORMICA FENIX NTM #0748 | BEIGE ARIZONA
 ฝาตู้หลังตู้ภายใน PANAPLAST HS-B 28779PM | LATTE
 TOP/BACK SPLASH : QUARTZ VADARA | OSTARA DAWN
 HANDLE : ALUMINUM PROFILE-C | ALUMINUM
 HANDLE : ALUMINUM PROFILE-J | ALUMINUM
 กระจกใส : DKP #1907 | Ivory

amoh
 22-12-68

Dkbb

157 Praditmanulham Road
 Bangkapi Bangkok 10240
 TEL: 0-2515-1182 FAX: 0-2515-1181
 WWW.dkbb.co.th

Client :ARI 789 PROJECT

Address :

Province :

Phone :

Design :KITCHEN

Series :ELEGANCE PLUS

Drawn by :Jirayu




Email :

View : ELEVATION B

Scale : 1:30

Date : 22/12/2568

Page : 3-5

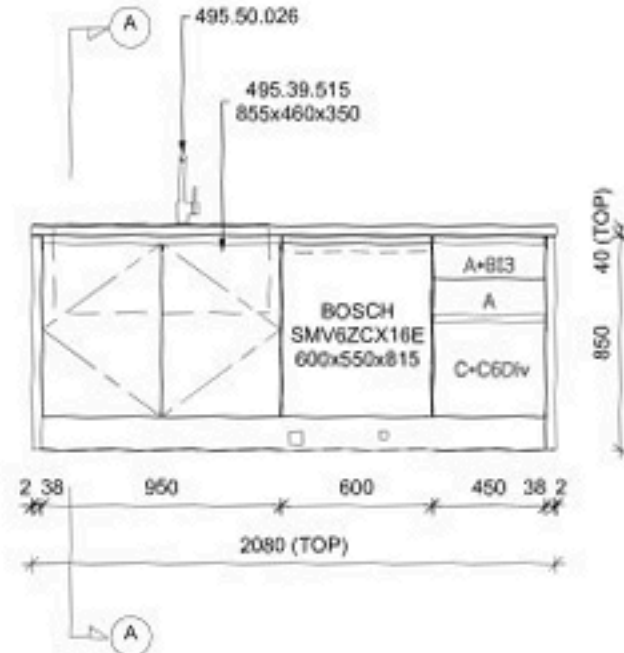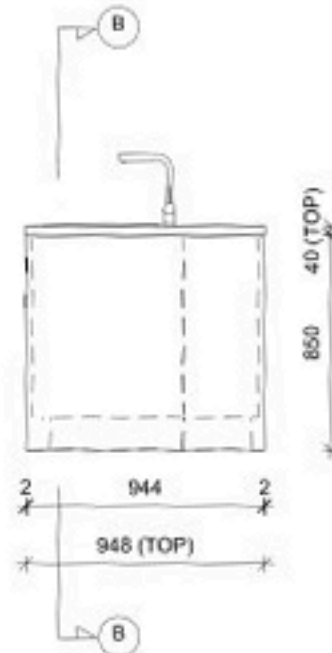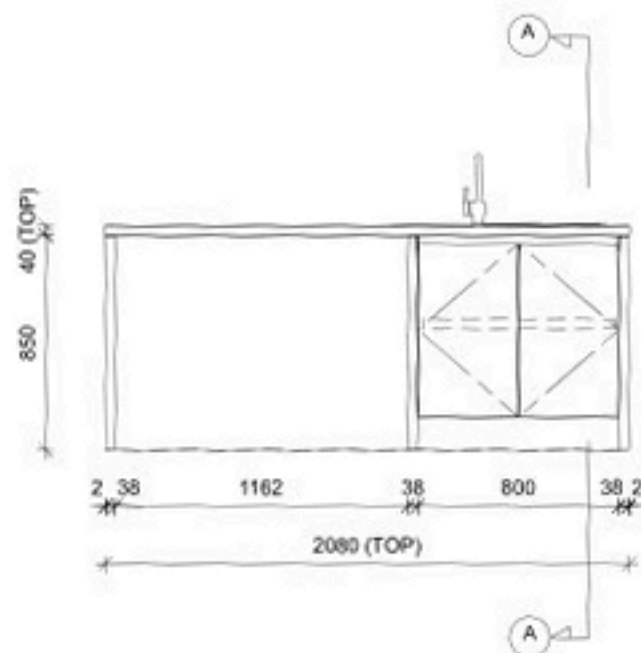

INSIDE : ARBORITE #IAB 8101 | PLEASANT TEAK
 OUT SIDE : FORMICA FENIX NTM #0748 | BEIGE ARIZONA
 FRONTAGE : FORMICA FENIX NTM #0748 | BEIGE ARIZONA
 ด้านหลังติดแผ่น PANAPLAST #S-B 28779PM | LATTE
 TOP/BACK SPLASH : QUARTZ VADARA | OSTARA DAWN
 HANDLE : ALUMINUM PROFILE-C | ALUMINUM
 HANDLE : ALUMINUM PROFILE-J | ALUMINUM
 เฟอร์นิเจอร์ : DKP #1907 | Ivory

Amat
 22-12-68

Dkbb

157 Praditmanutham Road
 Bangkok Bangkok 10240
 TEL 0-2515-1162 FAX 0-2515-1161
 WWW.dkbbthailand.co.th

Client :ARI 789 PROJECT

Address :

Province :

Phone :

Design :KITCHEN (ISLAND)

Series :ELEGANCE PLUS

Drawn by :Jirayu




Email :

View : ELEVATION A,B ,C

Scale : 1:30

Date : 22/12/2568

Page : 4-5

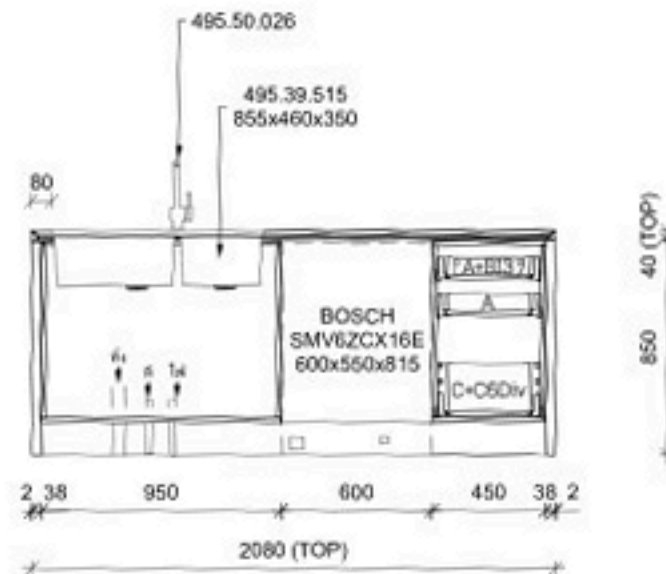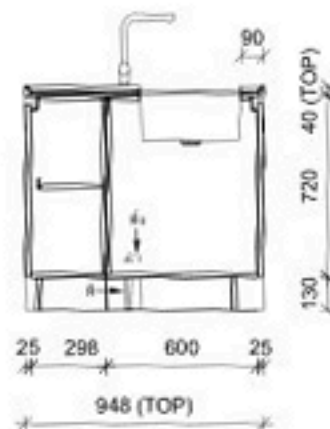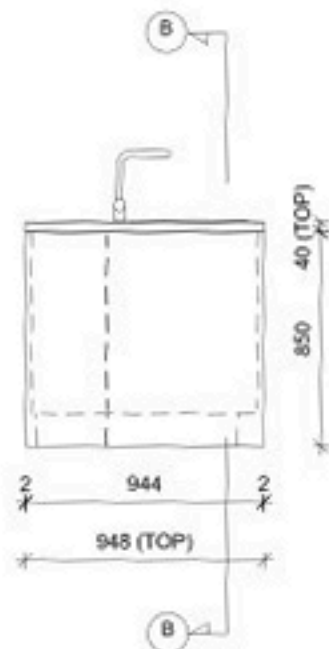

INSIDE : ARBORTE #IAB 8101 | PLEASANT TEAK
 OUT SIDE : FORMICA FENIX NTM #0748 | BEIGE ARIZONA
 FRONTAGE : FORMICA FENIX NTM #0748 | BEIGE ARIZONA
 ฝาหลัง/ลิ้นชัก/ตู้ PANAPLAST #S-B 28779PM | LATTE
 TOP/BACK SPLASH : QUARTZ VADARA | OSTARA DAWN
 HANDLE : ALUMINUM PROFILE-C | ALUMINUM
 HANDLE : ALUMINUM PROFILE-J | ALUMINUM
 เฟอร์นิเจอร์ : DKP #1907 | Ivory

amh
 22-12-58

Dkbb

157 Praditmanulham Road
 Bangkok Bangkok 10240
 TEL: 0-2515-1182 FAX: 0-2515-1181
 WWW.dkbb.co.th

Client :ARI 789 PROJECT

Address :

Province :

Phone :

Design :KITCHEN (ISLAND)

Series :ELEGANCE PLUS

Drawn by :Jirayu

Email :

View : ELEVATION D ,SECTION A ,B

Scale : 1:30

Date : 22/12/2568

Page : 5-5